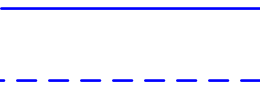


DANH MỤC BẢN VẼ	
MÃ BẢN VẼ	TÊN BẢN VẼ / DRAWING NAME
IT-01	DRAWING LIST
IT-02	LEGEND AND SYMBOL LIST
CY-MEA-DIAGRAM	NETWORK DIAGRAM_CY & MEA
MLM-DIAGRAM	NETWORK DIAGRAM_MLM
IT-LIFT	LIFT
DC-4BF	RACK LAYOUT DATA CENTER – 4BF
ELV-B1F	RACK LAYOUT ENGINEERING NETWORK ELV – B1F
IDF-M.B3F	RACK LAYOUT IDF-M.B3F
IDF-M.B1F	RACK LAYOUT ENGINEERING NETWORK ELV – B1F
IDF-M.1F	RACK LAYOUT IDF-M.1F
IDF-AV.2F & M.2F	RACK LAYOUT IDF-AV.2F & IDF-M.2F
IDF A.2F	RACK LAYOUT IDF-A.2F (MLM)
IDF-M.3F	RACK LAYOUT IDF-M.3F
IDF-AV.3AF & M.3AF	RACK LAYOUT IDF-AV.3AF & IDF-M.3AF
IDF-M.4F	RACK LAYOUT IDF-M.4F
IDF-M.4AF	RACK LAYOUT IDF-M.4AF
IDF-M.4BF	RACK LAYOUT IDF-M.4BF
IDF-M.5F	RACK LAYOUT IDF-M.5F
IDF-M.7F	RACK LAYOUT IDF-M.7F
IDF-M.9F	RACK LAYOUT IDF-M.9F
IDF-M.11F	RACK LAYOUT IDF-M.11F
IDF-M.13F	RACK LAYOUT IDF-M.13F
IDF-M.15F	RACK LAYOUT IDF-M.15F
IDF-M.18F	RACK LAYOUT IDF-M.18F
IDF-M.21F	RACK LAYOUT IDF-M.21F
IDF-M.23F	RACK LAYOUT IDF-M.23F
IDF-A.24AF	RACK LAYOUT IDF-A.24AF (MLM)
IDF-A.26F	RACK LAYOUT IDF-A.26F (MLM)
IDF-A.29F	RACK LAYOUT IDF-A.29F (MLM)
IDF-A.32F	RACK LAYOUT IDF-A.32F (MLM)
IDF-A.35F	RACK LAYOUT IDF-A.35F (MLM)
IDF-A.38F	RACK LAYOUT IDF-A.38F (MLM)
IDF-MEA BLOCK	RACK LAYOUT – MEA BLOCK 25~38 th FLOOR (~5 IDF RACK)
IDF-M.39F	RACK LAYOUT IDF-M.39F

DỰ ÁN:	
TỔ HỢP KHÁCH SẠN, CĂN HỘ DỊCH VỤ MARRIOTT VÀ NHÀ Ở ĐỂ BÁN	
ĐỊA ĐIỂM XÂY DỰNG: 58 BẠCH ĐẰNG, P. HẢI CHÂU 1, Q. HẢI CHÂU, TP. ĐÀ NẴNG	
CHỦ ĐẦU TƯ:	
CÔNG TY CỔ PHẦN ĐỊA ỐC FOODINCO	
ĐỊA CHỈ: 58 BẠCH ĐẰNG, P. HẢI CHÂU 1, Q. HẢI CHÂU, TP. ĐÀ NẴNG	
BAN QUẢN LÝ DỰ ÁN:	
TƯ VẤN GIÁM SÁT:	
CN CÔNG TY TNHH APAVE CHÂU Á - THÁI BÌNH DƯƠNG TẠI ĐÀ NẴNG	
NGUYỄN ĐĂNG HÙNG	
ĐƠN VỊ NHÀ THẦU CHÍNH:	
CÔNG TY CỔ PHẦN ALPHANAM E&C	
NHÀ THẦU THI CÔNG:	
 CÔNG TY TNHH VIỄN THÔNG SÁNG TẠO THUẬN PHONG (INNOTEL)	
55/31 TRẦN ĐÌNH XU, P. CẦU KHO, Q. 1, HCM Tel: (84 28) 3 862 1119 Fax: (84 28) 3 863 0366	
CHỈ HUY TRƯỞNG:	
NGUYỄN ĐỨC TIẾN	
NGƯỜI KIỂM TRA:	
NGƯỜI LẬP:	
TÊN BẢN VẼ:	
DRAWING LIST	
NGÀY HT:	01/09/2022
CHỈNH SỬA:	01
MÃ BẢN VẼ:	IT-01
HỒ SƠ THAM CHIẾU:	220726 ELV - CAP NHAT CCTV THEO Y KIEN MI GS&S

DANH MỤC KÝ HIỆU VÀ CHÚ THÍCH	
KÝ HIỆU / HÌNH ẢNH	TÊN / MÔ TẢ
	10G (MM fiber)
	DAC 40G (for Stacking)
	DAC 10G (for Stacking)
	CORE SWITCH
	ACCESS SWITCH
	WIRELESS CONTROLLER

DỰ ÁN:

TỔ HỢP KHÁCH SẠN, CĂN HỘ DỊCH VỤ MARRIOTT VÀ NHÀ Ở ĐỂ BÁN

ĐỊA ĐIỂM XÂY DỰNG:

58 BẠCH ĐẰNG, P. HẢI CHÂU 1, Q. HẢI CHÂU, TP. ĐÀ NẴNG

CHỦ ĐẦU TƯ:

CÔNG TY CỔ PHẦN ĐỊA ỐC FOODINCO

ĐỊA CHỈ:

58 BẠCH ĐẰNG, P. HẢI CHÂU 1, Q. HẢI CHÂU, TP. ĐÀ NẴNG

BAN QUẢN LÝ DỰ ÁN:

TƯ VẤN GIÁM SÁT:

CN CÔNG TY TNHH APAVE CHÂU Á - THÁI BÌNH DƯƠNG TẠI ĐÀ NẴNG

NGUYỄN ĐĂNG HÙNG

ĐƠN VỊ NHÀ THẦU CHÍNH:

CÔNG TY CỔ PHẦN ALPHANAM E&C

NHÀ THẦU THI CÔNG:



CÔNG TY TNHH VIỄN THÔNG SÁNG TẠO THUẬN PHONG (INNOTEL)

55/31 TRẦN ĐÌNH XU, P. CẦU KHO, Q. 1, HCM
Tel: (84 28) 3 862 1119 || Fax: (84 28) 3 863 0366

CHỈ HUY TRƯỞNG:

NGUYỄN ĐỨC TIẾN

NGƯỜI KIỂM TRA:

NGƯỜI LẬP:

TÊN BẢN VẼ:

LEGEND AND SYMBOL LIST

NGÀY HT:

01/09/2022

CHỈNH SỬA:


01

MÃ BẢN VẼ:


IT-02

HỒ SƠ THAM CHIẾU:


220726 ELV - CAP NHAT CCTV THEO Y KIEN MI GS&S

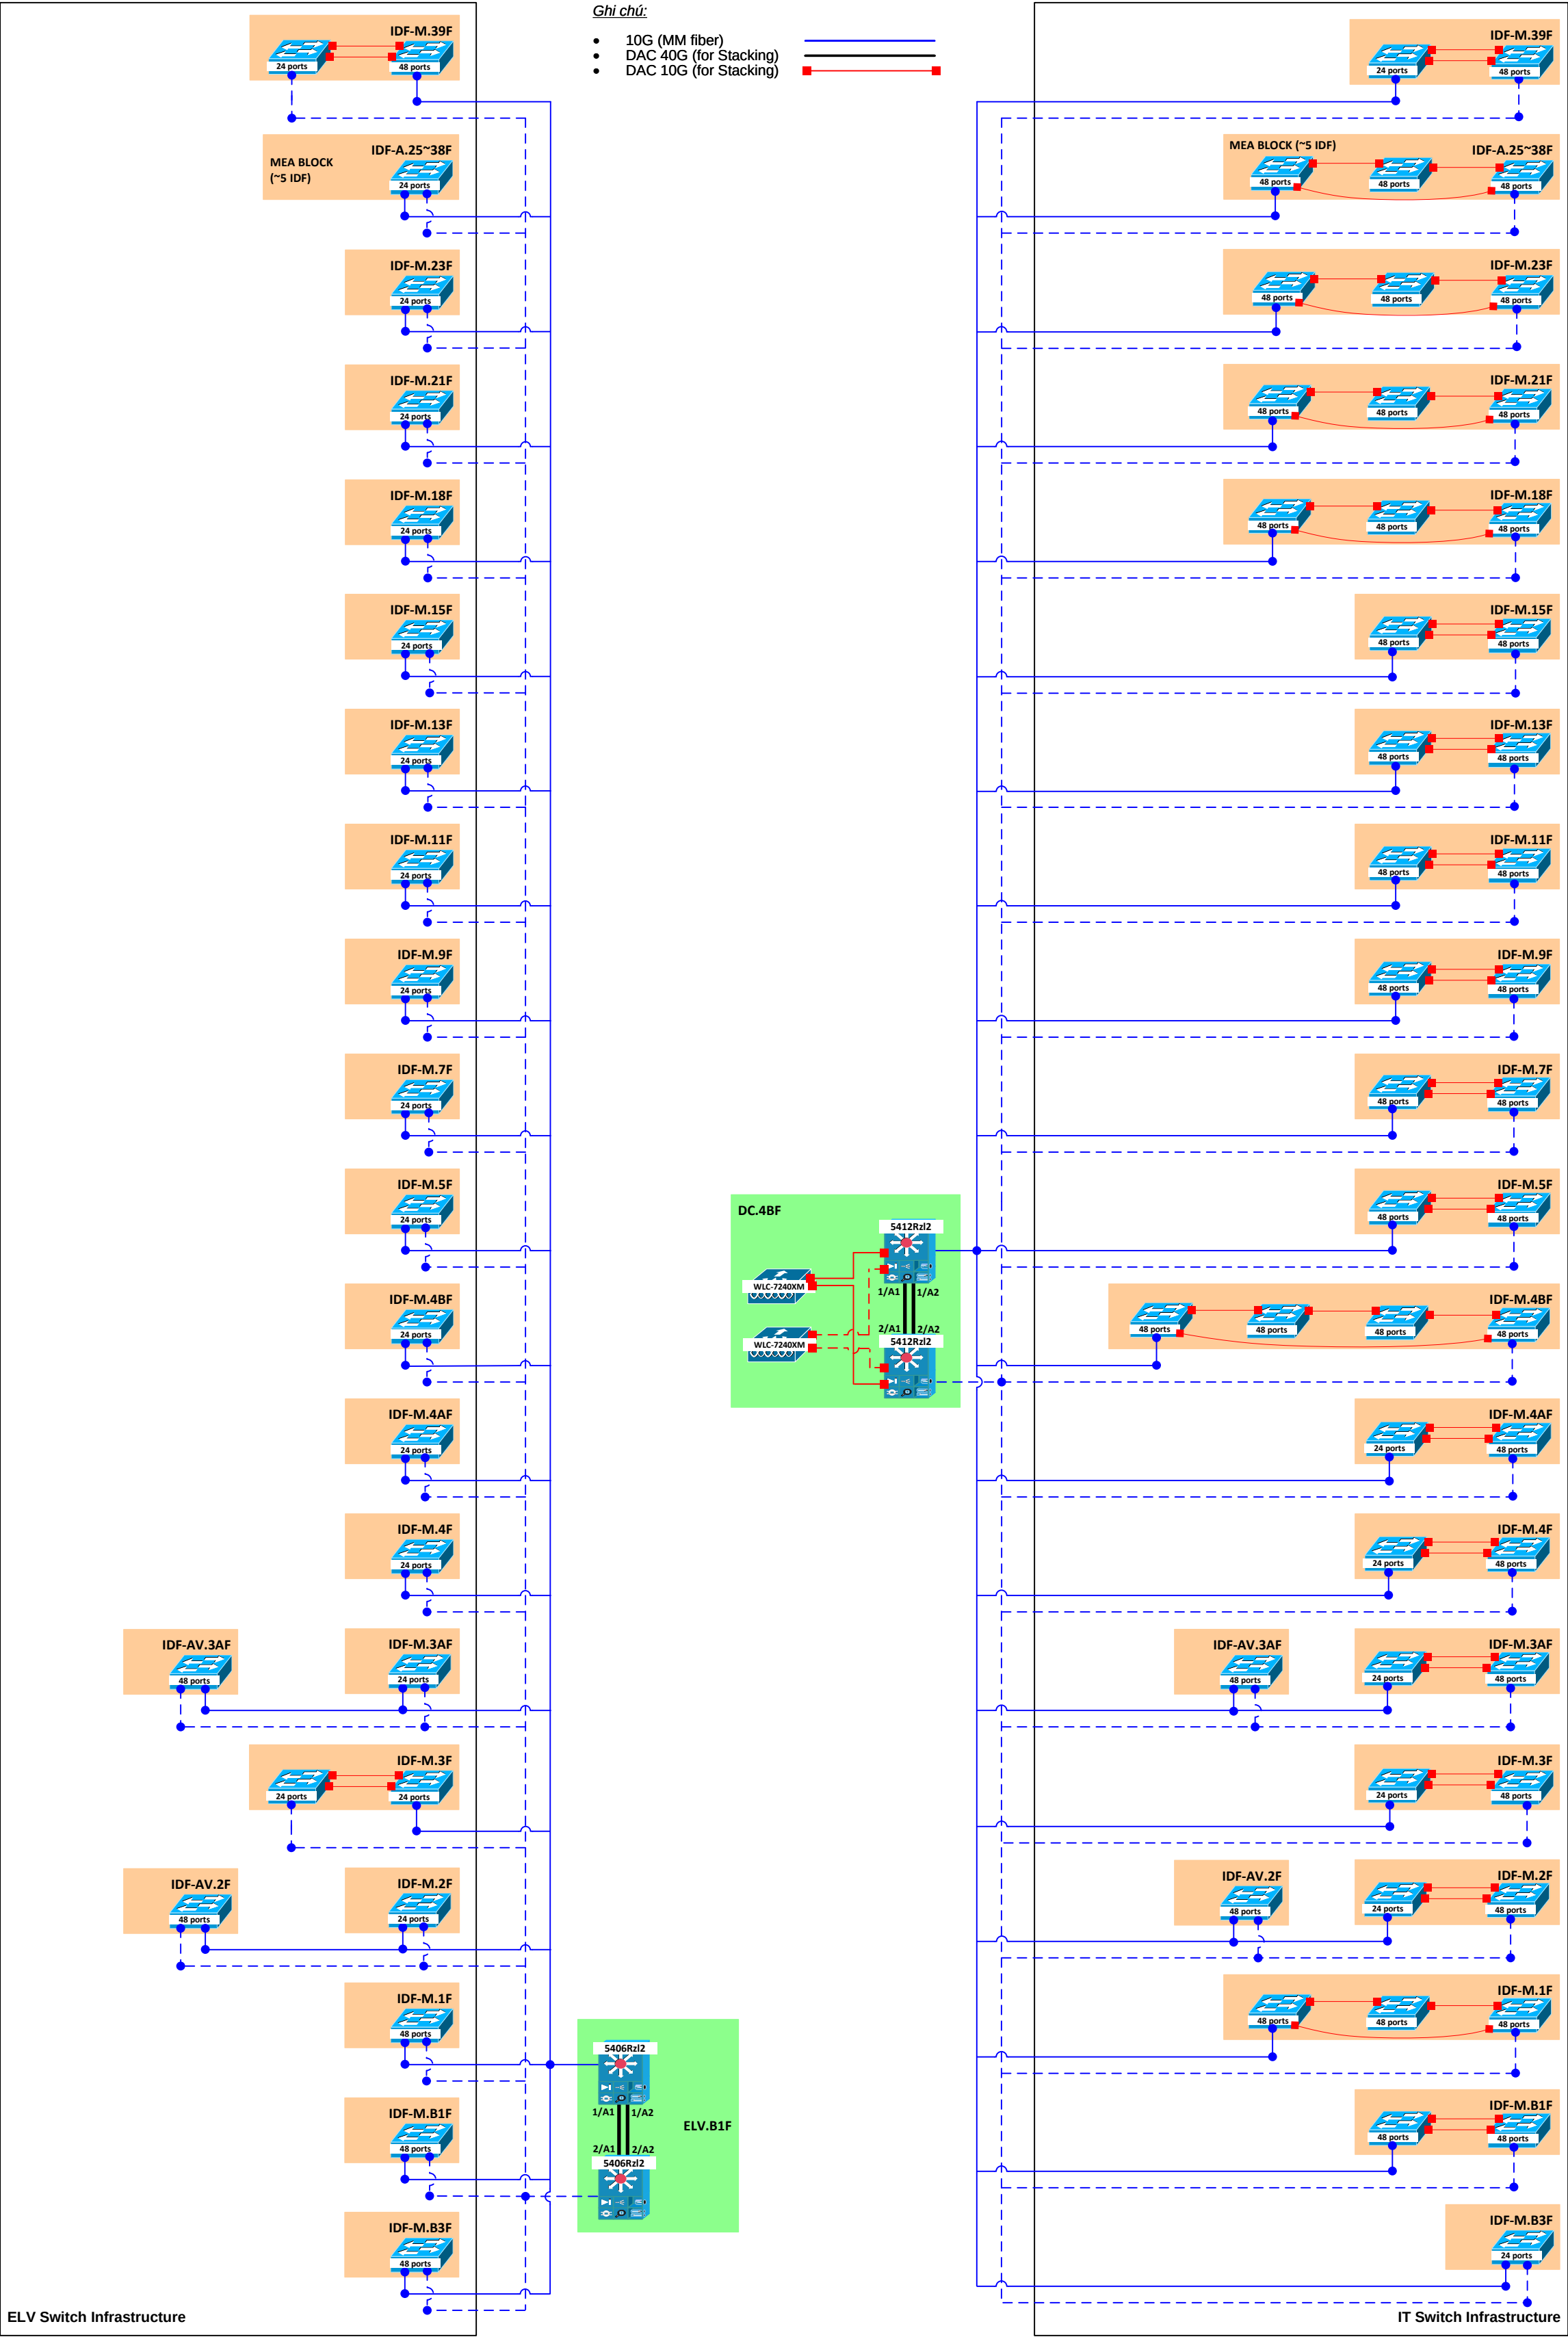


DỰ ÁN:		TỔ HỢP KHÁCH SẠN, CĂN HỘ DỊCH VỤ MARRIOTT VÀ NHÀ Ở ĐỂ BÁN	
ĐỊA ĐIỂM XÂY DỰNG:		58 BẠCH ĐẰNG, P. HẢI CHÂU 1, Q. HẢI CHÂU, TP. ĐÀ NẴNG	
CHỦ ĐẦU TƯ:		CÔNG TY CỔ PHẦN ĐỊA ỐC FOODINCO	
ĐỊA CHỈ:		58 BẠCH ĐẰNG, P. HẢI CHÂU 1, Q. HẢI CHÂU, TP. ĐÀ NẴNG	
BAN QUẢN LÝ DỰ ÁN:			
TƯ VẤN GIÁM SÁT:		CN CÔNG TY TNHH APAVE CHÂU Á - THÁI BÌNH DƯƠNG TẠI ĐÀ NẴNG	
		NGUYỄN ĐĂNG HÙNG	
ĐƠN VỊ NHÀ THẦU CHÍNH:		CÔNG TY CỔ PHẦN ALPHANAM E&C	
NHÀ THẦU THI CÔNG:		 CÔNG TY TNHH VIỄN THÔNG SÁNG TẠO THUẬN PHONG (INNOTEL) 55/31 TRẦN ĐÌNH XU, P. CẦU KHO, Q. 1, HCM Tel: (84 28) 3 862 1119 Fax: (84 28) 3 863 0366	
CHỈ HUY TRƯỞNG:			
NGUYỄN ĐỨC TIẾN			
NGƯỜI KIỂM TRA:			
NGƯỜI LẬP:			
TÊN BẢN VẼ:		NETWORK DIAGRAM_CY & MEA	
NGÀY HT:		01/09/2022	
CHỈNH SỬA:		01	
MÃ BẢN VẼ:		CY-MEA-DIAGRAM	
HỒ SƠ THAM CHIẾU:		220726 ELV - CAP NHAT CCTV THEO Y KIEN MI GS&S	

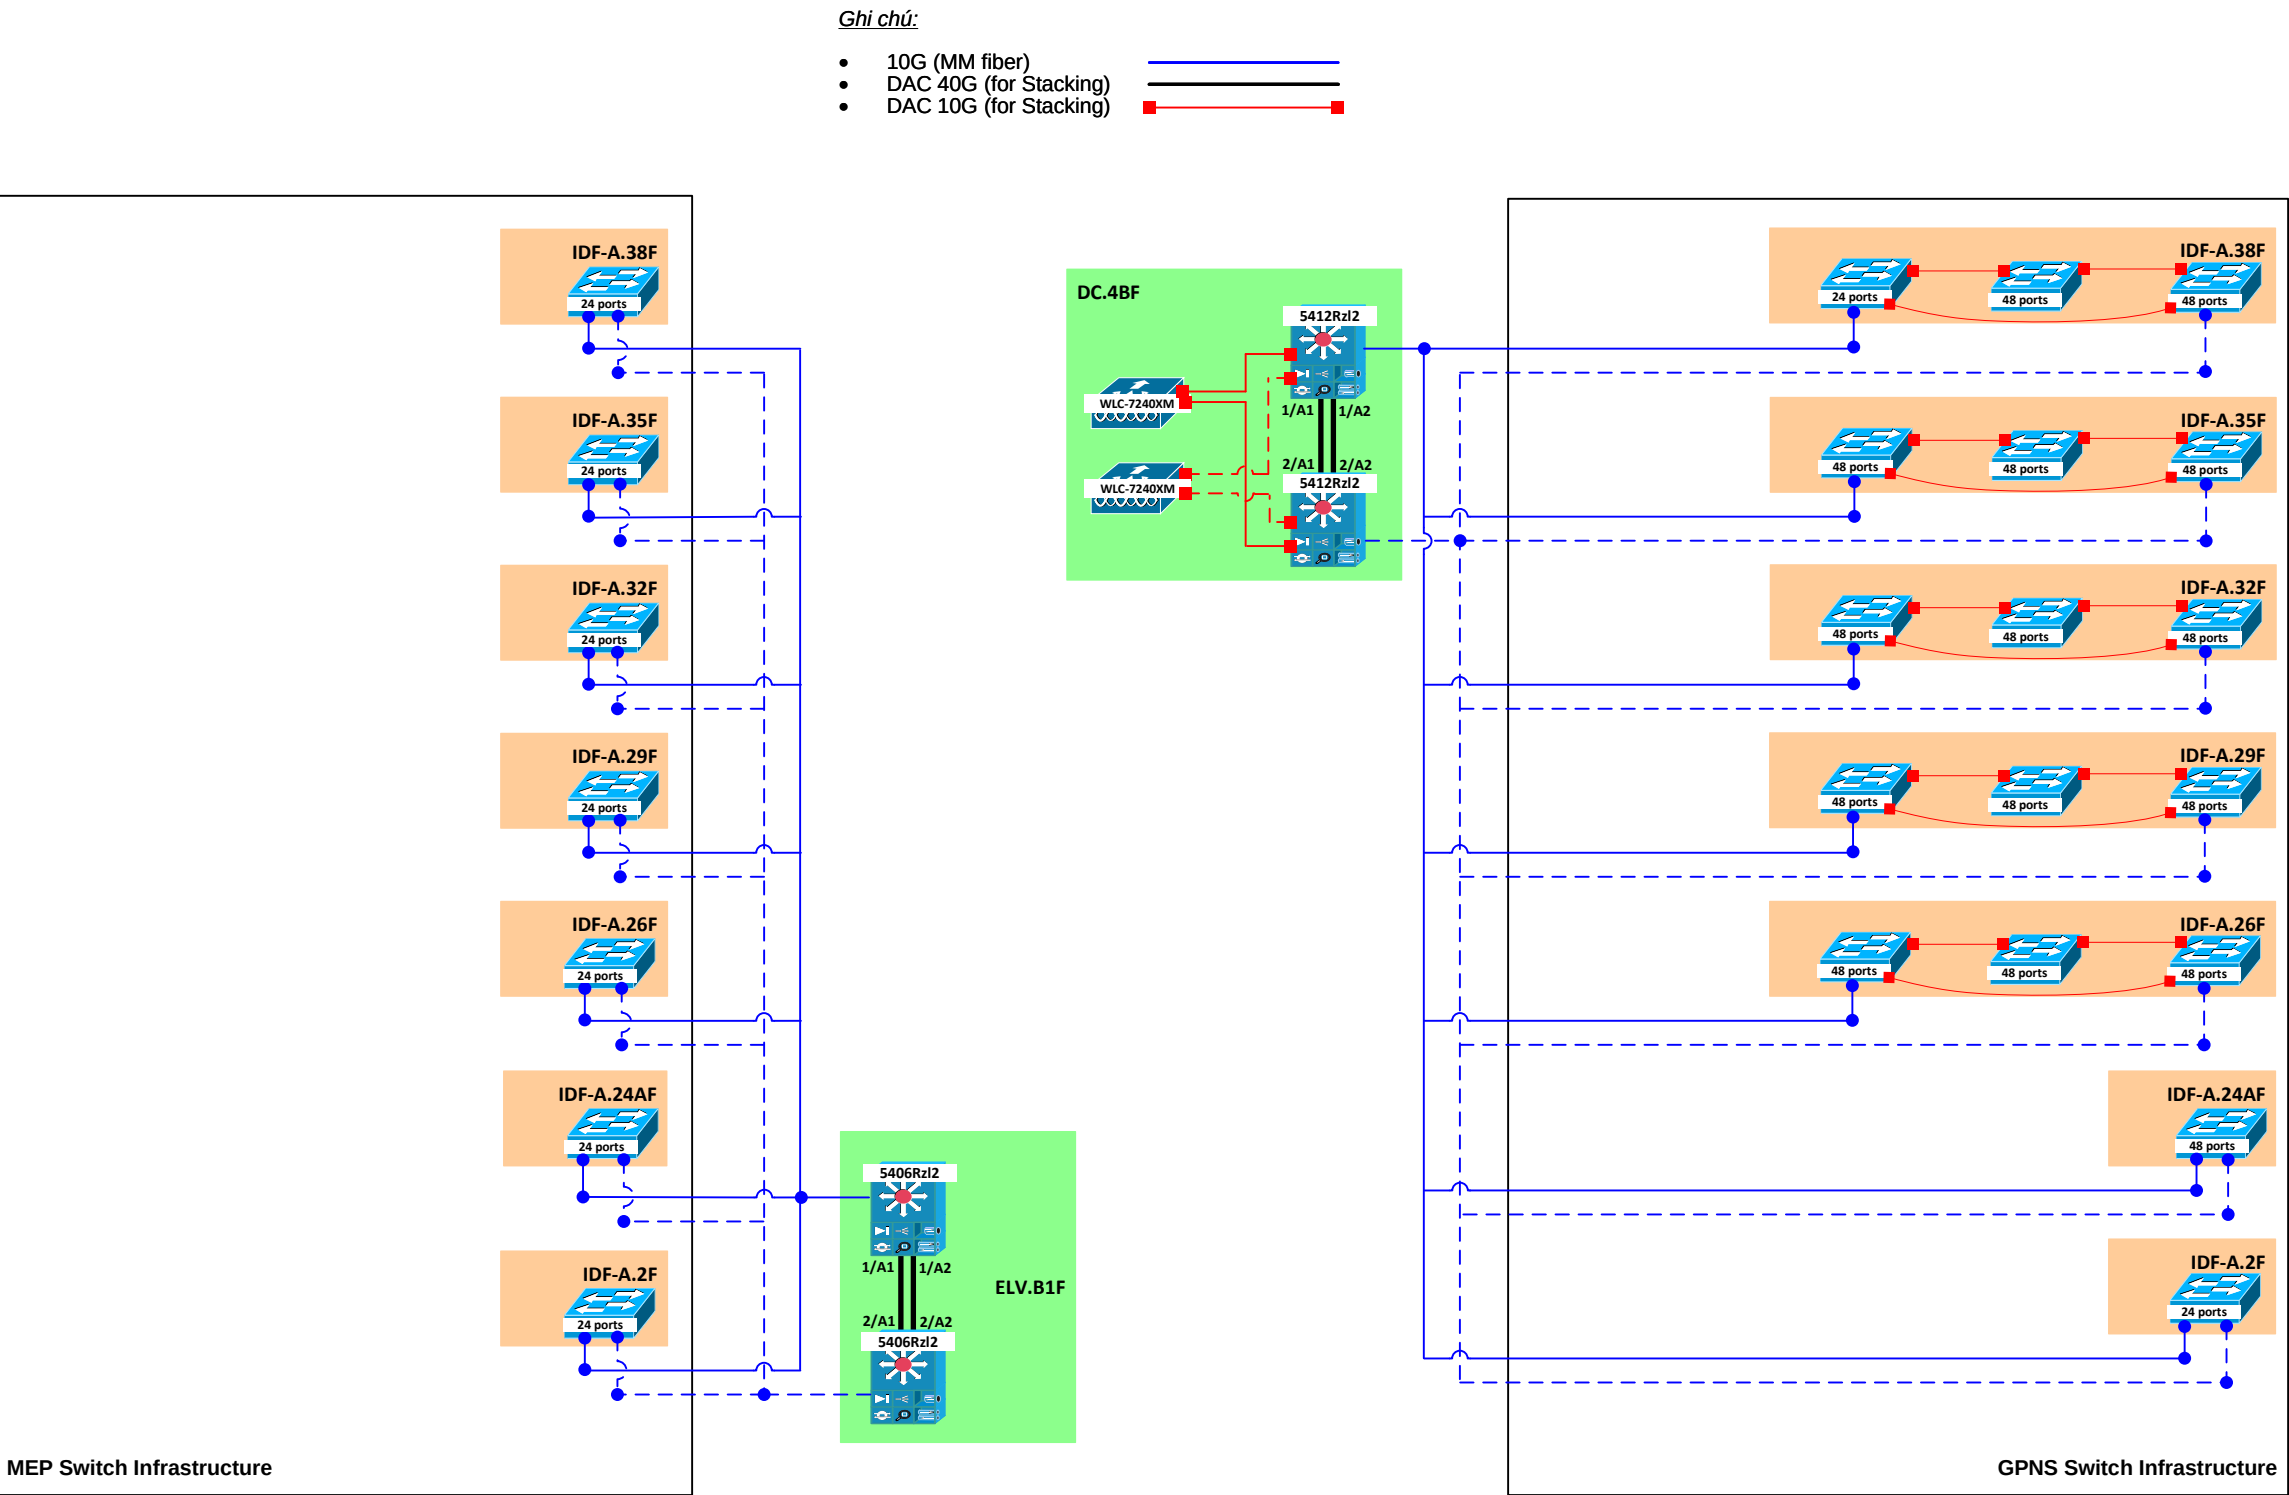


DỰ ÁN: TỔ HỢP KHÁCH SẠN, CĂN HỘ DỊCH VỤ MARRIOTT VÀ NHÀ Ở ĐỂ BÁN ĐỊA ĐIỂM XÂY DỰNG: 58 BẠCH ĐẰNG, P. HẢI CHÂU 1, Q. HẢI CHÂU, TP. ĐÀ NẴNG	
CHỦ ĐẦU TƯ: CÔNG TY CỔ PHẦN ĐỊA ỐC FOODINCO ĐỊA CHỈ: 58 BẠCH ĐẰNG, P. HẢI CHÂU 1, Q. HẢI CHÂU, TP. ĐÀ NẴNG	
BAN QUẢN LÝ DỰ ÁN:	
TƯ VẤN GIÁM SÁT: CN CÔNG TY TNHH APAVE CHÂU Á - THÁI BÌNH DƯƠNG TẠI ĐÀ NẴNG NGUYỄN ĐĂNG HÙNG	
ĐƠN VỊ NHÀ THẦU CHÍNH: CÔNG TY CỔ PHẦN ALPHANAM E&C	
NHÀ THẦU THI CÔNG:  CÔNG TY TNHH VIỄN THÔNG SÁNG TẠO THUẬN PHONG (INNOTEL) 55/31 TRẦN ĐÌNH XU, P. CẦU KHO, Q. 1, HCM Tel: (84 28) 3 862 1119 Fax: (84 28) 3 863 0366	
CHỈ HUY TRƯỞNG:	
NGƯỜI KIỂM TRA:	
NGƯỜI LẬP:	
TÊN BẢN VẼ: NETWORK DIAGRAM_MLM	
NGÀY HT:	01/09/2022
CHỈNH SỬA:	01
MÃ BẢN VẼ:	MLM-DIAGRAM
HỒ SƠ THAM CHIẾU:	220726 ELV - CAP NHAT CCTV THEO Y KIEN MI GS&S

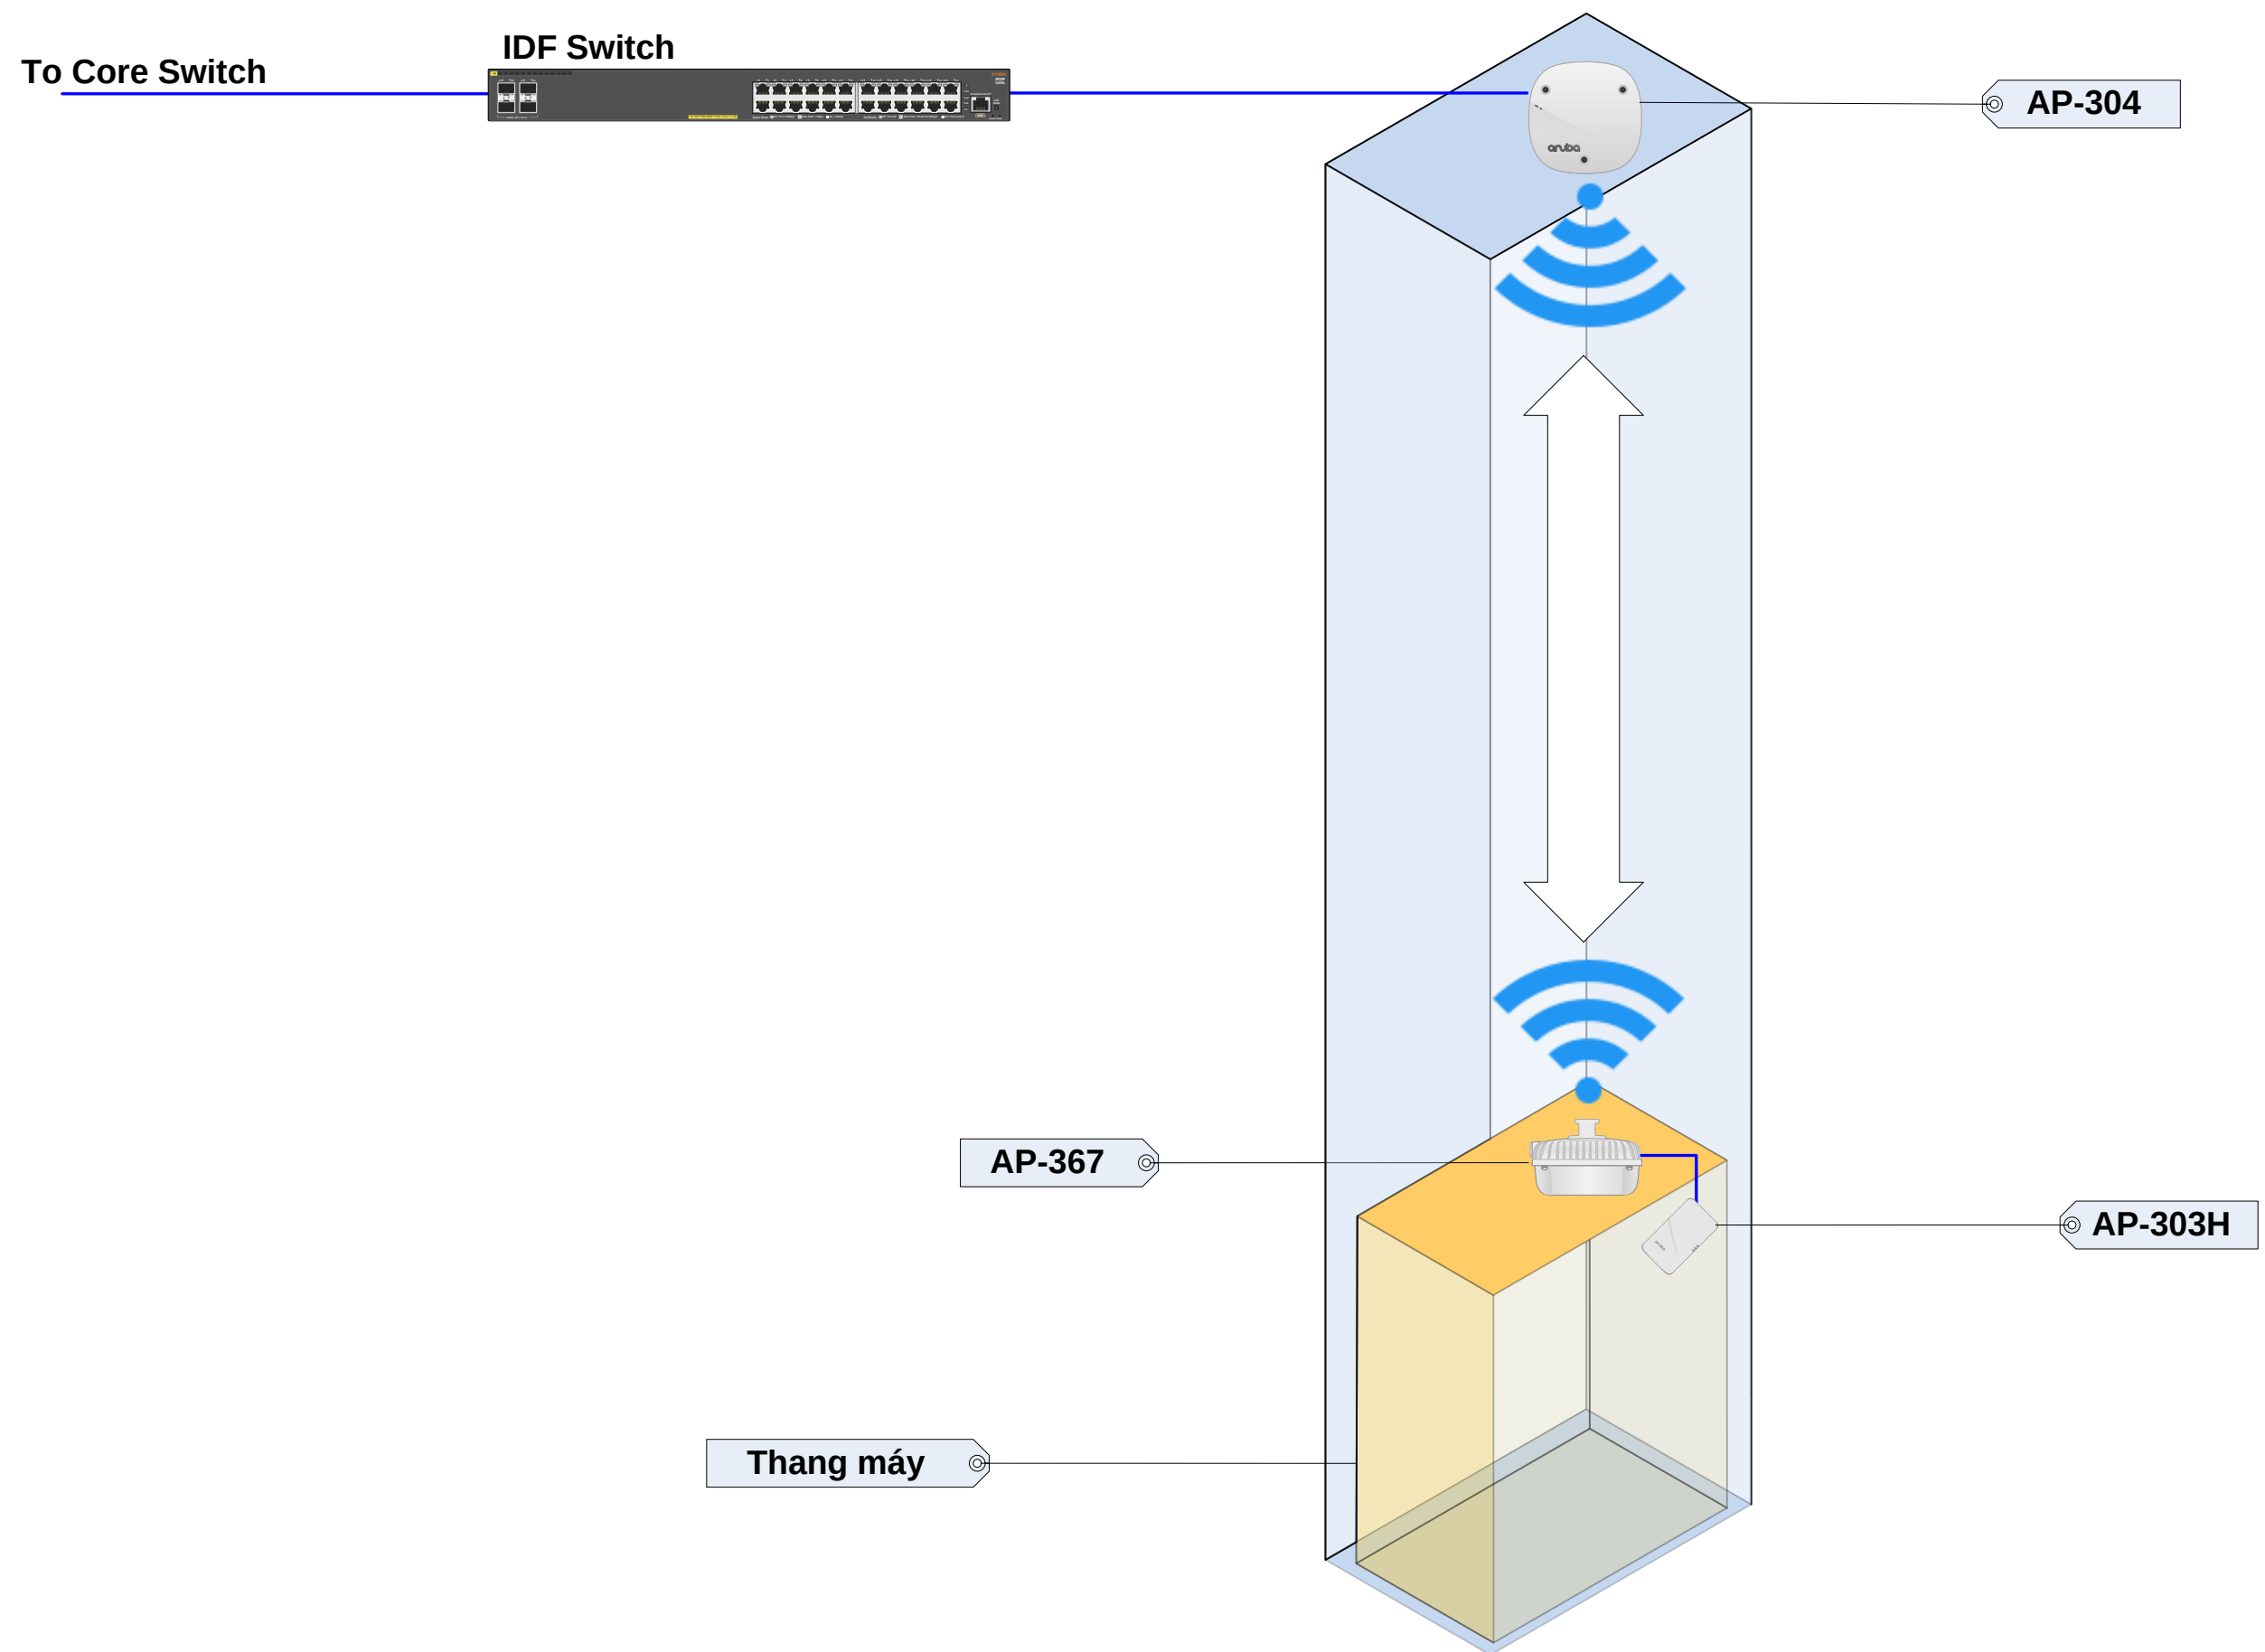


DỰ ÁN: TỔ HỢP KHÁCH SẠN, CĂN HỘ DỊCH VỤ MARRIOTT VÀ NHÀ Ở ĐỂ BÁN	
ĐỊA ĐIỂM XÂY DỰNG: 58 BẠCH ĐẰNG, P. HẢI CHÂU 1, Q. HẢI CHÂU, TP. ĐÀ NẴNG	
CHỦ ĐẦU TƯ: CÔNG TY CỔ PHẦN ĐỊA ỐC FOODINCO	
ĐỊA CHỈ: 58 BẠCH ĐẰNG, P. HẢI CHÂU 1, Q. HẢI CHÂU, TP. ĐÀ NẴNG	
BAN QUẢN LÝ DỰ ÁN:	
TƯ VẤN GIÁM SÁT: CN CÔNG TY TNHH APAVE CHÂU Á - THÁI BÌNH DƯƠNG TẠI ĐÀ NẴNG	
NGUYỄN ĐĂNG HÙNG	
ĐƠN VỊ NHÀ THẦU CHÍNH: CÔNG TY CỔ PHẦN ALPHANAM E&C	
NHÀ THẦU THI CÔNG:  CÔNG TY TNHH VIỄN THÔNG SÁNG TẠO THUẬN PHONG (INNOTEL) 55/31 TRẦN ĐÌNH XU, P. CẦU KHO, Q. 1, HCM Tel: (84 28) 3 862 1119 Fax: (84 28) 3 863 0366	
CHỈ HUY TRƯỞNG:	
NGUYỄN ĐỨC TIẾN	
NGƯỜI KIỂM TRA:	
NGƯỜI LẬP:	
TÊN BẢN VẼ: LIFT	
NGÀY HT:	01/09/2022
CHỈNH SỬA:	01
MÃ BẢN VẼ:	IT-LIFT
HỒ SƠ THAM CHIẾU:	220726 ELV - CAP NHAT CCTV THEO Y KIEN MI GS&S

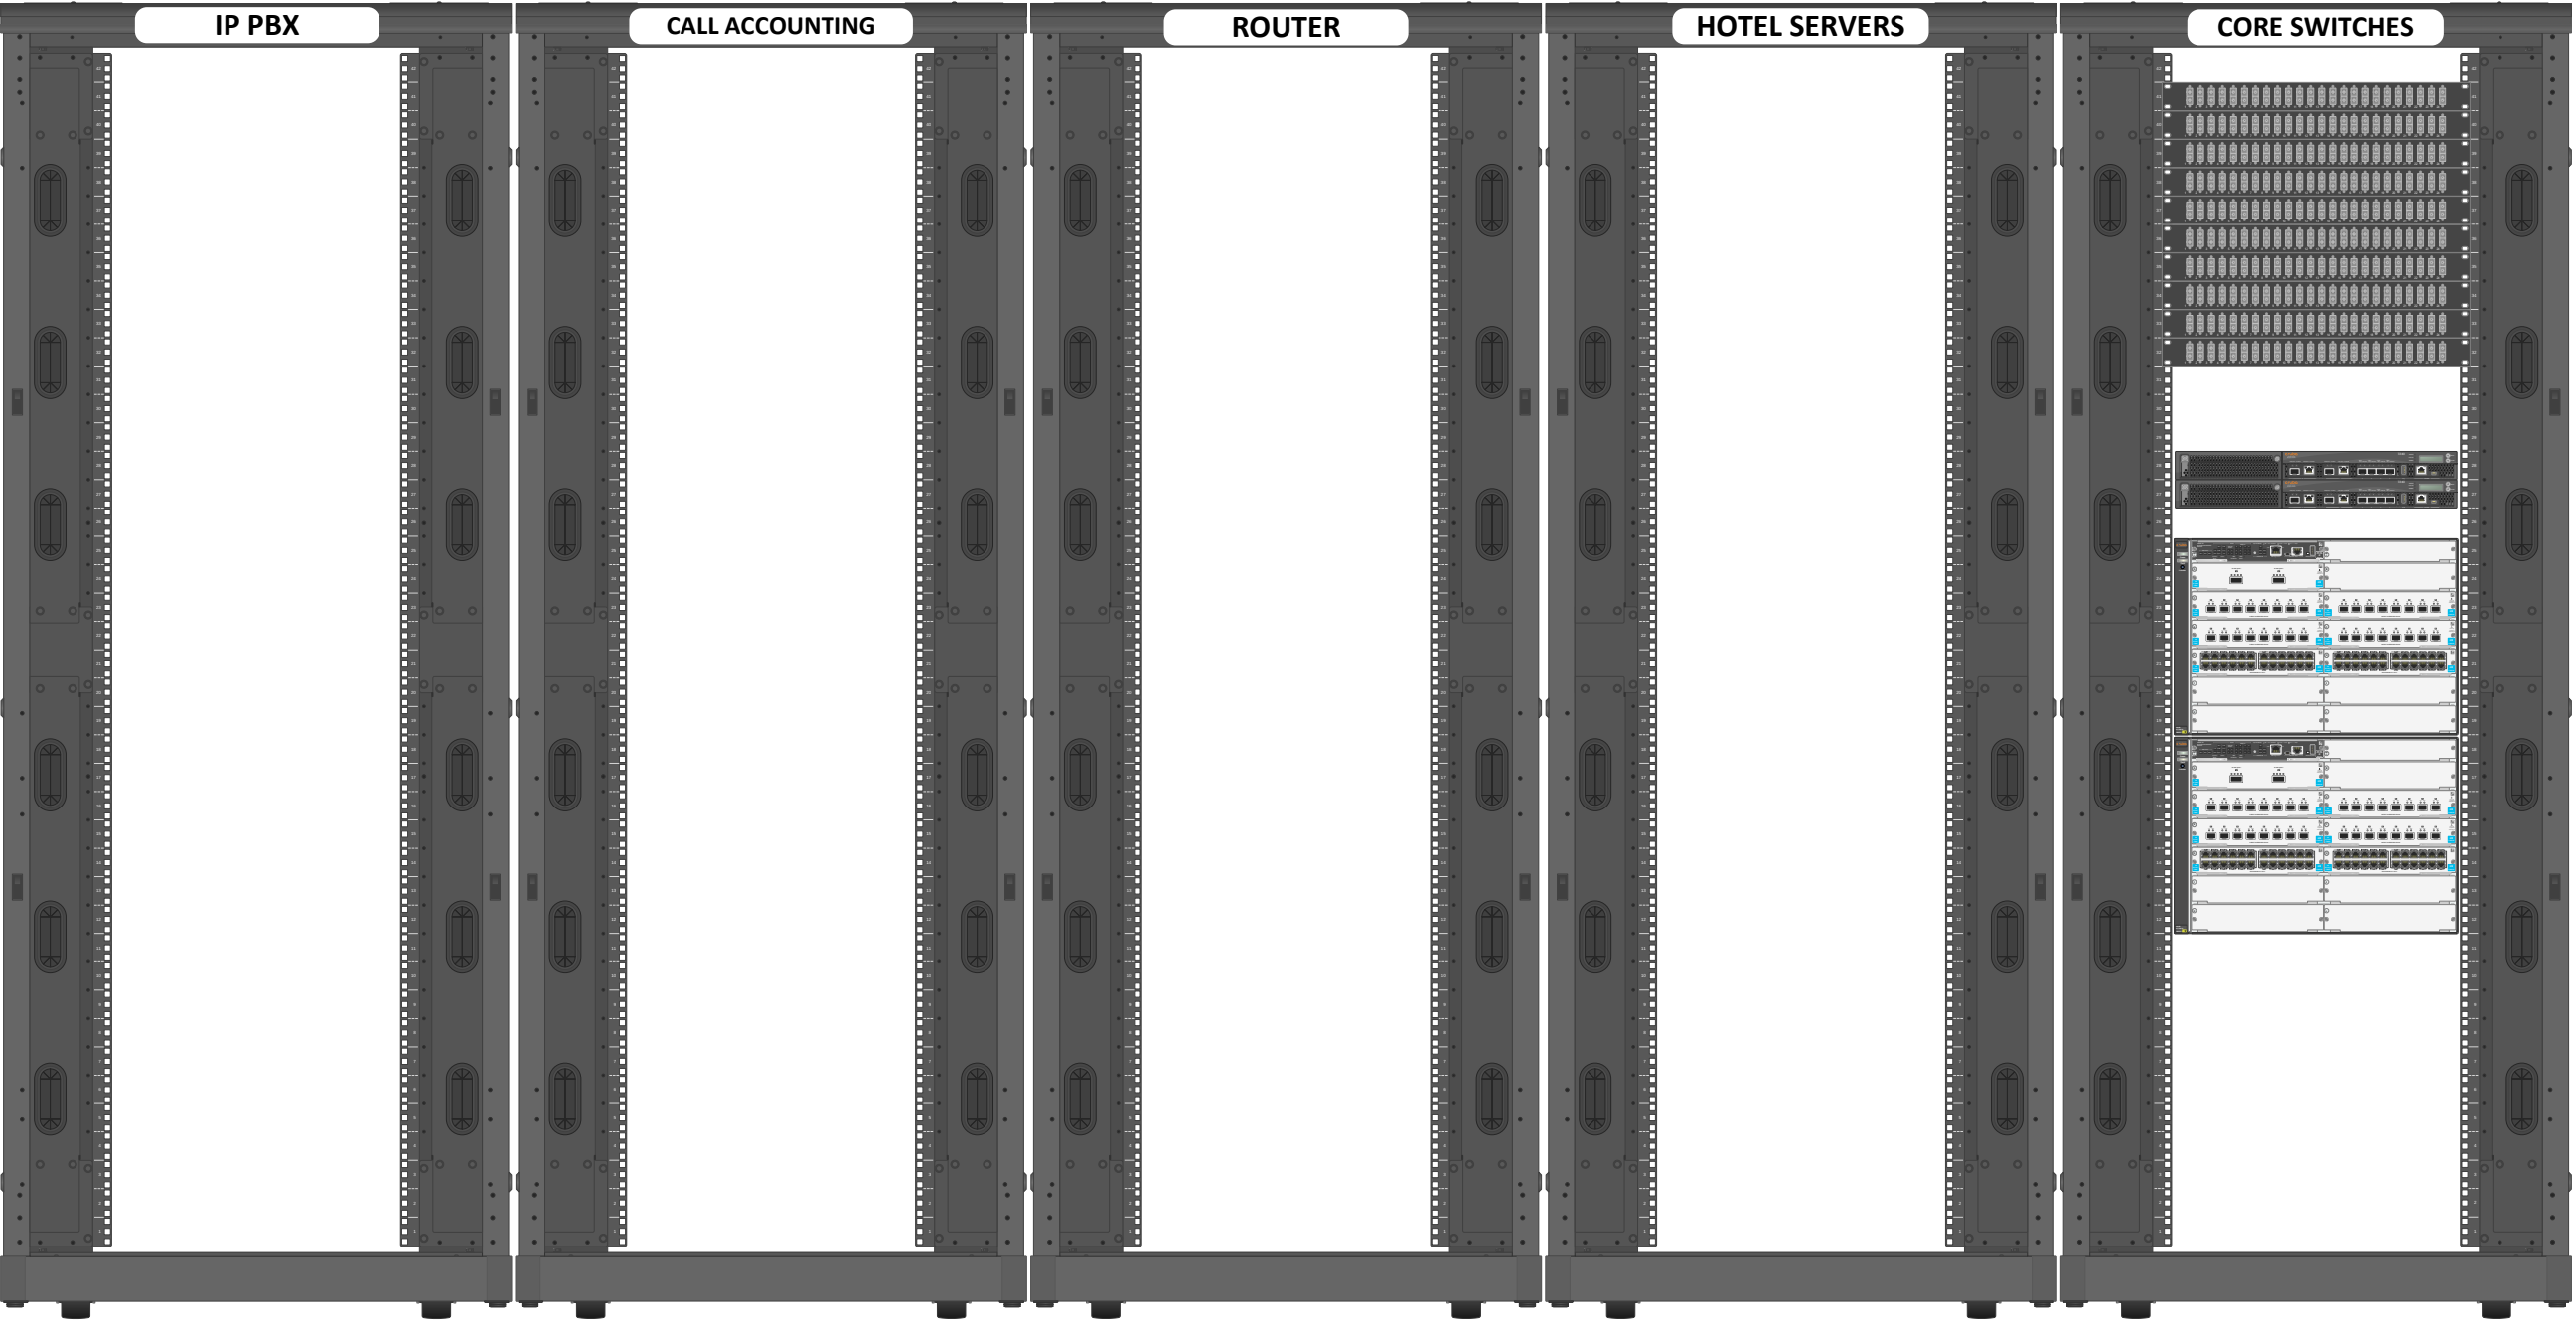


DỰ ÁN: TỔ HỢP KHÁCH SẠN, CĂN HỘ DỊCH VỤ MARRIOTT VÀ NHÀ Ở ĐỂ BÁN ĐỊA ĐIỂM XÂY DỰNG: 58 BẠCH ĐẰNG, P. HẢI CHÂU 1, Q. HẢI CHÂU, TP. ĐÀ NẴNG	
CHỦ ĐẦU TƯ: CÔNG TY CỔ PHẦN ĐỊA ỐC FOODINCO ĐỊA CHỈ: 58 BẠCH ĐẰNG, P. HẢI CHÂU 1, Q. HẢI CHÂU, TP. ĐÀ NẴNG	
BAN QUẢN LÝ DỰ ÁN:	
TƯ VẤN GIÁM SÁT: CN CÔNG TY TNHH APAVE CHÂU Á - THÁI BÌNH DƯƠNG TẠI ĐÀ NẴNG NGUYỄN ĐĂNG HÙNG	
ĐƠN VỊ NHÀ THẦU CHÍNH: CÔNG TY CỔ PHẦN ALPHANAM E&C	
NHÀ THẦU THI CÔNG:  CÔNG TY TNHH VIỄN THÔNG SÁNG TẠO THUẬN PHONG (INNOTEL) 55/31 TRẦN ĐÌNH XU, P. CẦU KHO, Q. 1, HCM Tel: (84 28) 3 862 1119 Fax: (84 28) 3 863 0366	
CHỈ HUY TRƯỞNG:	
NGƯỜI KIỂM TRA:	
NGƯỜI LẬP:	
TÊN BẢN VẼ: RACK LAYOUT DATA CENTER – 4BF	
NGÀY HT:	01/09/2022
CHỈNH SỬA:	01
MÃ BẢN VẼ:	DC-4BF
HỒ SƠ THAM CHIẾU:	220726 ELV - CAP NHAT CCTV THEO Y KIEN MI GS&S

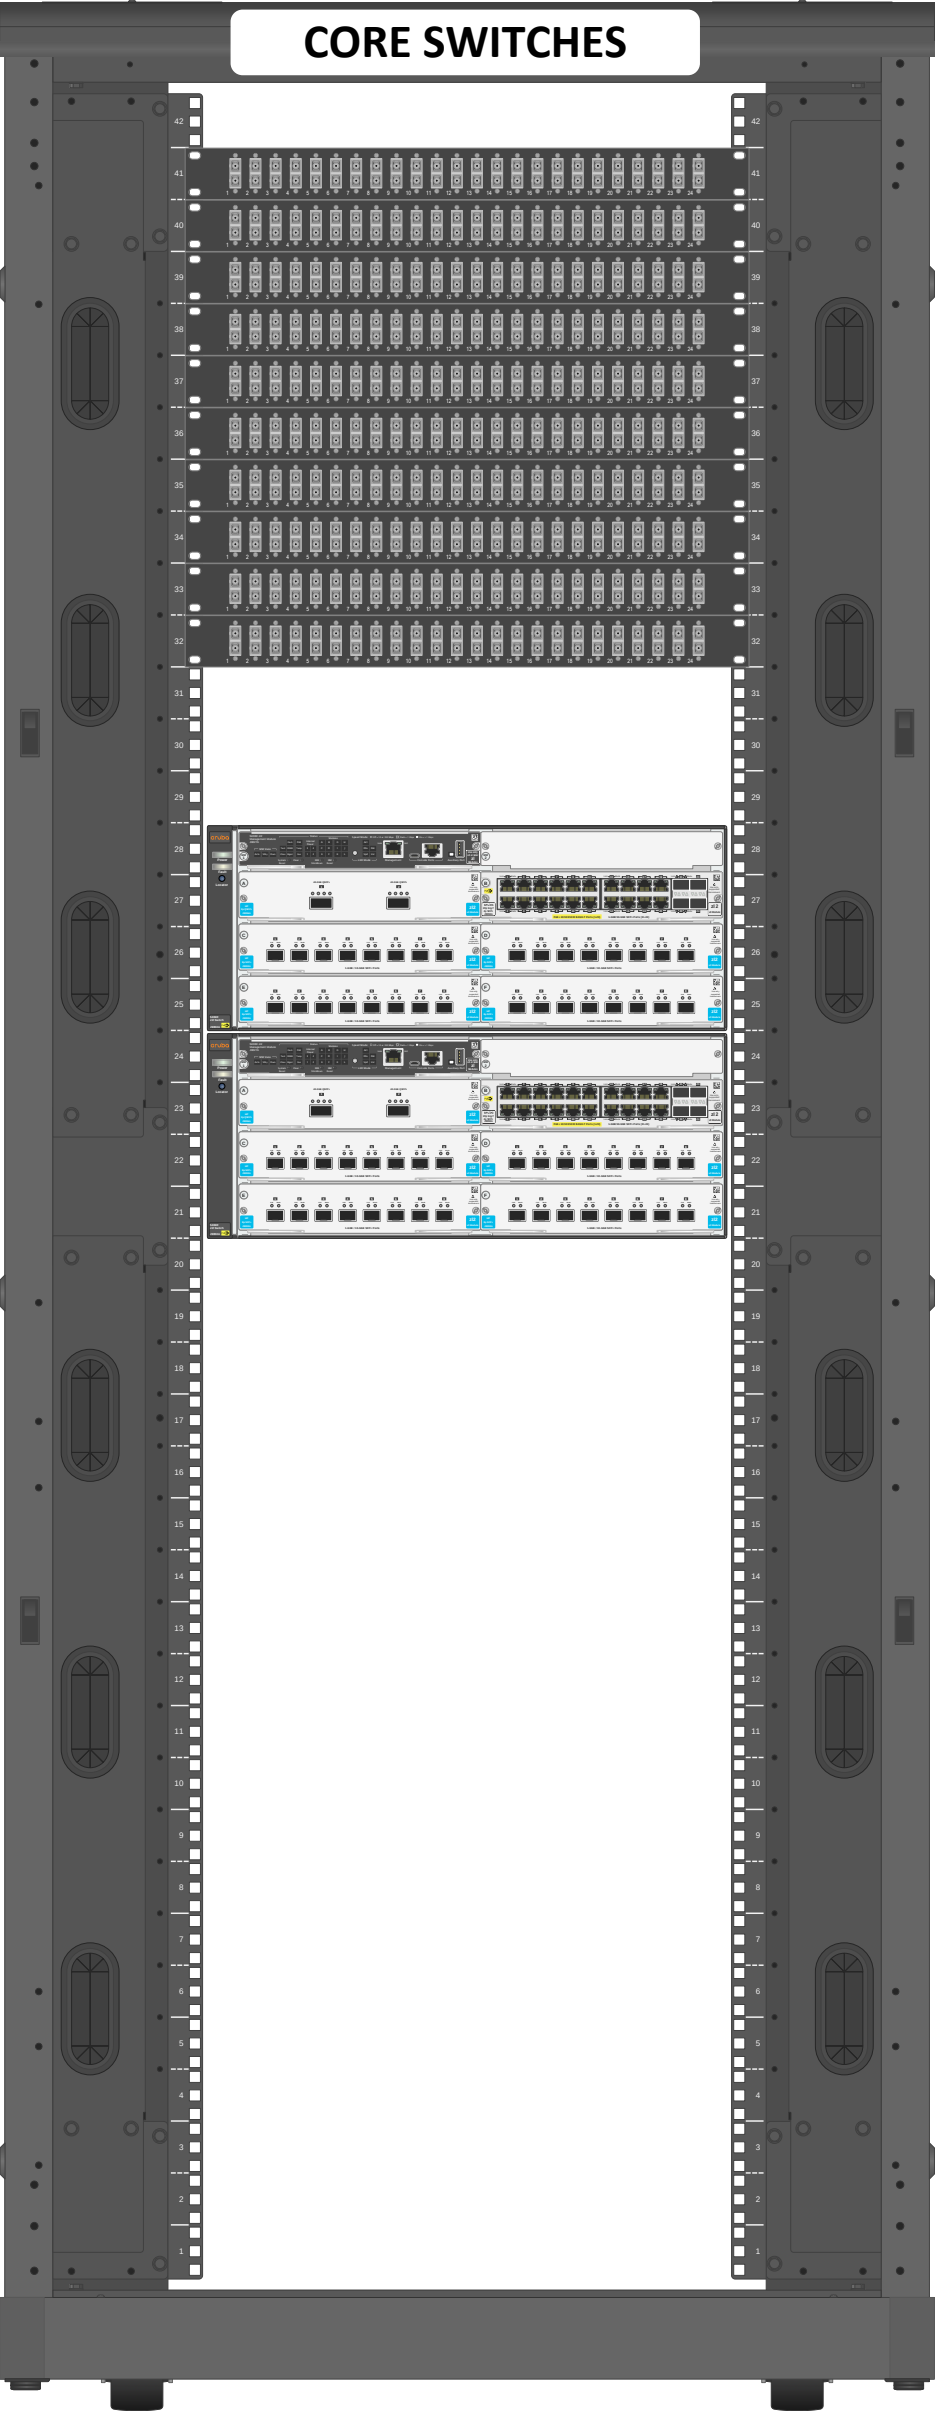


DỰ ÁN: TỔ HỢP KHÁCH SẠN, CĂN HỘ DỊCH VỤ MARRIOTT VÀ NHÀ Ở ĐỂ BÁN ĐỊA ĐIỂM XÂY DỰNG: 58 BẠCH ĐẰNG, P. HẢI CHÂU 1, Q. HẢI CHÂU, TP. ĐÀ NẴNG	
CHỦ ĐẦU TƯ: CÔNG TY CỔ PHẦN ĐỊA ỐC FOODINCO ĐỊA CHỈ: 58 BẠCH ĐẰNG, P. HẢI CHÂU 1, Q. HẢI CHÂU, TP. ĐÀ NẴNG	
BAN QUẢN LÝ DỰ ÁN:	
TƯ VẤN GIÁM SÁT: CN CÔNG TY TNHH APAVE CHÂU Á - THÁI BÌNH DƯƠNG TẠI ĐÀ NẴNG NGUYỄN ĐĂNG HÙNG	
ĐƠN VỊ NHÀ THẦU CHÍNH: CÔNG TY CỔ PHẦN ALPHANAM E&C	
NHÀ THẦU THI CÔNG:  CÔNG TY TNHH VIỄN THÔNG SÁNG TẠO THUẬN PHONG (INNOTEL) 55/31 TRẦN ĐÌNH XU, P. CẦU KHO, Q. 1, HCM Tel: (84 28) 3 862 1119 Fax: (84 28) 3 863 0366	
CHỈ HUY TRƯỞNG:	
NGƯỜI KIỂM TRA:	
NGƯỜI LẬP:	
TÊN BẢN VẼ: RACK LAYOUT ENGINEERING NETWORK ELV – B1F	
NGÀY HT:	01/09/2022
CHỈNH SỬA:	01
MÃ BẢN VẼ:	ELV-B1F
HỒ SƠ THAM CHIẾU:	220726 ELV - CAP NHAT CCTV THEO Y KIEN MI GS&S

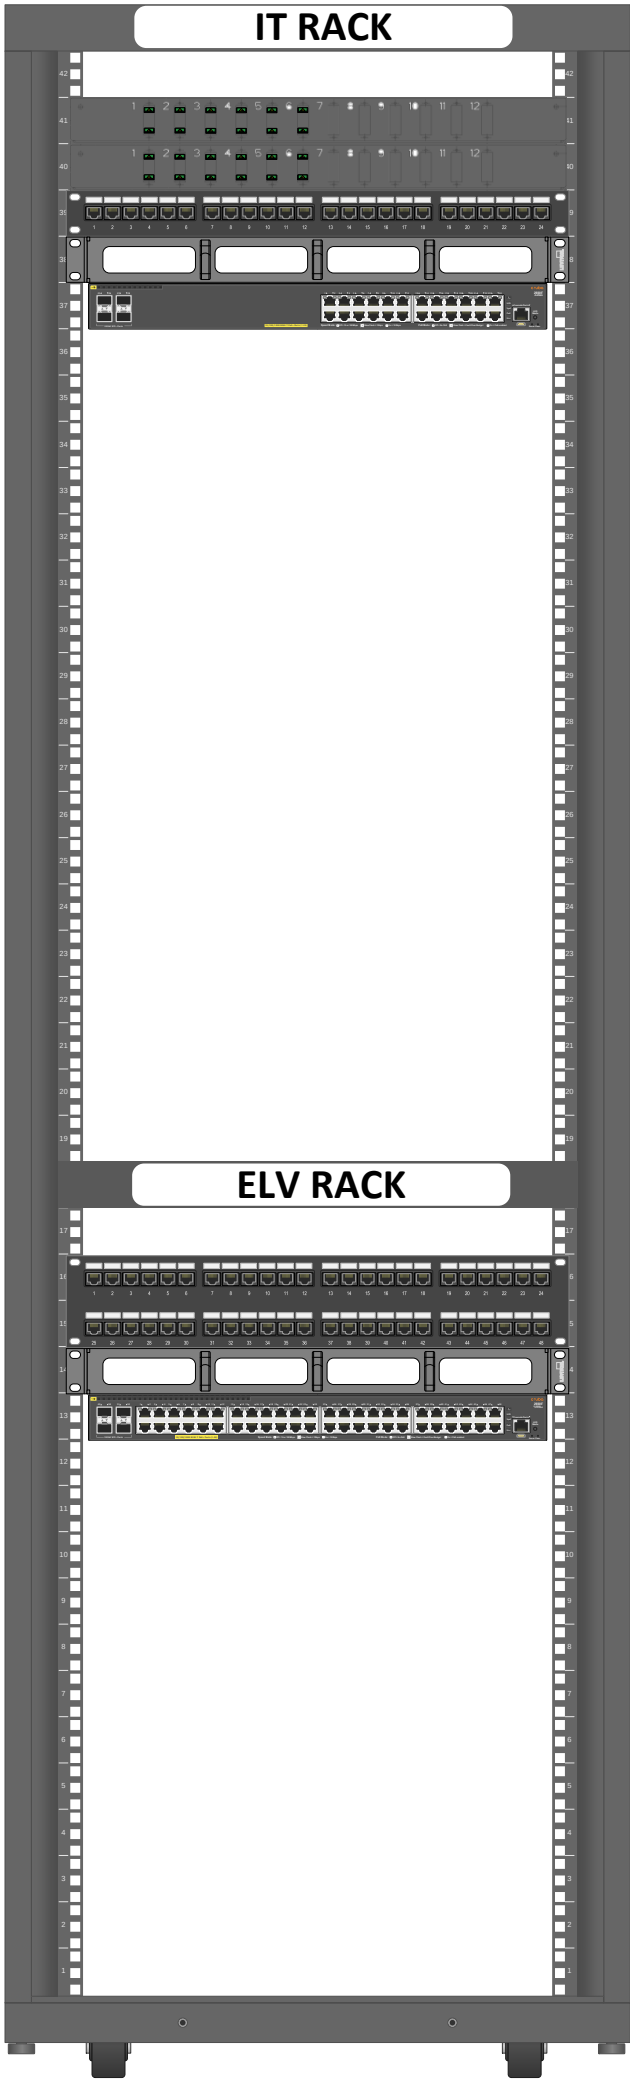



DỰ ÁN: TỔ HỢP KHÁCH SẠN, CĂN HỘ DỊCH VỤ MARRIOTT VÀ NHÀ Ở ĐỂ BÁN ĐỊA ĐIỂM XÂY DỰNG: 58 BẠCH ĐẰNG, P. HẢI CHÂU 1, Q. HẢI CHÂU, TP. ĐÀ NẴNG	
CHỦ ĐẦU TƯ: CÔNG TY CỔ PHẦN ĐỊA ỐC FOODINCO ĐỊA CHỈ: 58 BẠCH ĐẰNG, P. HẢI CHÂU 1, Q. HẢI CHÂU, TP. ĐÀ NẴNG	
BAN QUẢN LÝ DỰ ÁN:	
TƯ VẤN GIÁM SÁT: CN CÔNG TY TNHH APAVE CHÂU Á - THÁI BÌNH DƯƠNG TẠI ĐÀ NẴNG NGUYỄN ĐĂNG HÙNG	
ĐƠN VỊ NHÀ THẦU CHÍNH: CÔNG TY CỔ PHẦN ALPHANAM E&C	
NHÀ THẦU THI CÔNG:  CÔNG TY TNHH VIỄN THÔNG SÁNG TẠO THUẬN PHONG (INNOTEL) 55/31 TRẦN ĐÌNH XU, P. CẦU KHO, Q. 1, HCM Tel: (84 28) 3 862 1119 Fax: (84 28) 3 863 0366	
CHỈ HUY TRƯỞNG: NGUYỄN ĐỨC TIẾN	
NGƯỜI KIỂM TRA:	
NGƯỜI LẬP:	
TÊN BẢN VẼ: RACK LAYOUT IDF-M.B3F	
NGÀY HT:	01/09/2022
CHỈNH SỬA:	01
MÃ BẢN VẼ:	IDF-M.B3F
HỒ SƠ THAM CHIẾU:	220726 ELV - CAP NHAT CCTV THEO Y KIEN MI GS&S

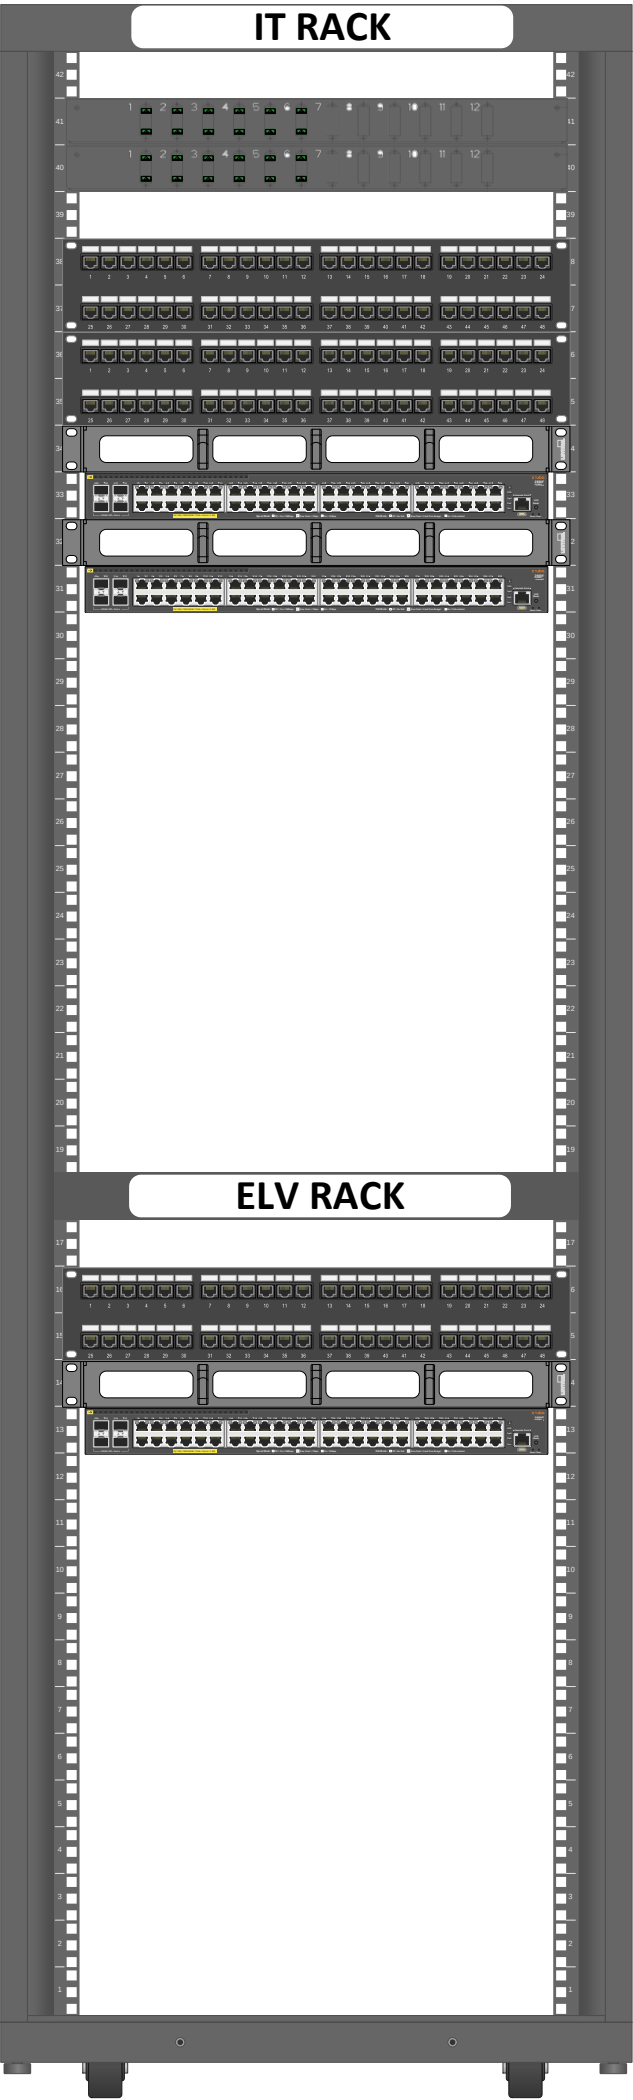


DỰ ÁN: TỔ HỢP KHÁCH SẠN, CĂN HỘ DỊCH VỤ MARRIOTT VÀ NHÀ Ở ĐỂ BÁN ĐỊA ĐIỂM XÂY DỰNG: 58 BẠCH ĐẰNG, P. HẢI CHÂU 1, Q. HẢI CHÂU, TP. ĐÀ NẴNG	
CHỦ ĐẦU TƯ: CÔNG TY CỔ PHẦN ĐỊA ỐC FOODINCO ĐỊA CHỈ: 58 BẠCH ĐẰNG, P. HẢI CHÂU 1, Q. HẢI CHÂU, TP. ĐÀ NẴNG	
BAN QUẢN LÝ DỰ ÁN:	
TƯ VẤN GIÁM SÁT: CN CÔNG TY TNHH APAVE CHÂU Á - THÁI BÌNH DƯƠNG TẠI ĐÀ NẴNG NGUYỄN ĐĂNG HÙNG	
ĐƠN VỊ NHÀ THẦU CHÍNH: CÔNG TY CỔ PHẦN ALPHANAM E&C	
NHÀ THẦU THI CÔNG:  CÔNG TY TNHH VIỄN THÔNG SÁNG TẠO THUẬN PHONG (INNOTEL) 55/31 TRẦN ĐÌNH XU, P. CẦU KHO, Q. 1, HCM Tel: (84 28) 3 862 1119 Fax: (84 28) 3 863 0366	
CHỈ HUY TRƯỞNG:	
NGUYỄN ĐỨC TIẾN	
NGƯỜI KIỂM TRA:	
NGƯỜI LẬP:	
TÊN BẢN VẼ: RACK LAYOUT IDF-M.B1F	
NGÀY HT:	01/09/2022
CHỈNH SỬA:	01
MÃ BẢN VẼ:	IDF-M.B1F
HỒ SƠ THAM CHIẾU:	220726 ELV - CAP NHAT CCTV THEO Y KIEN MI GS&S

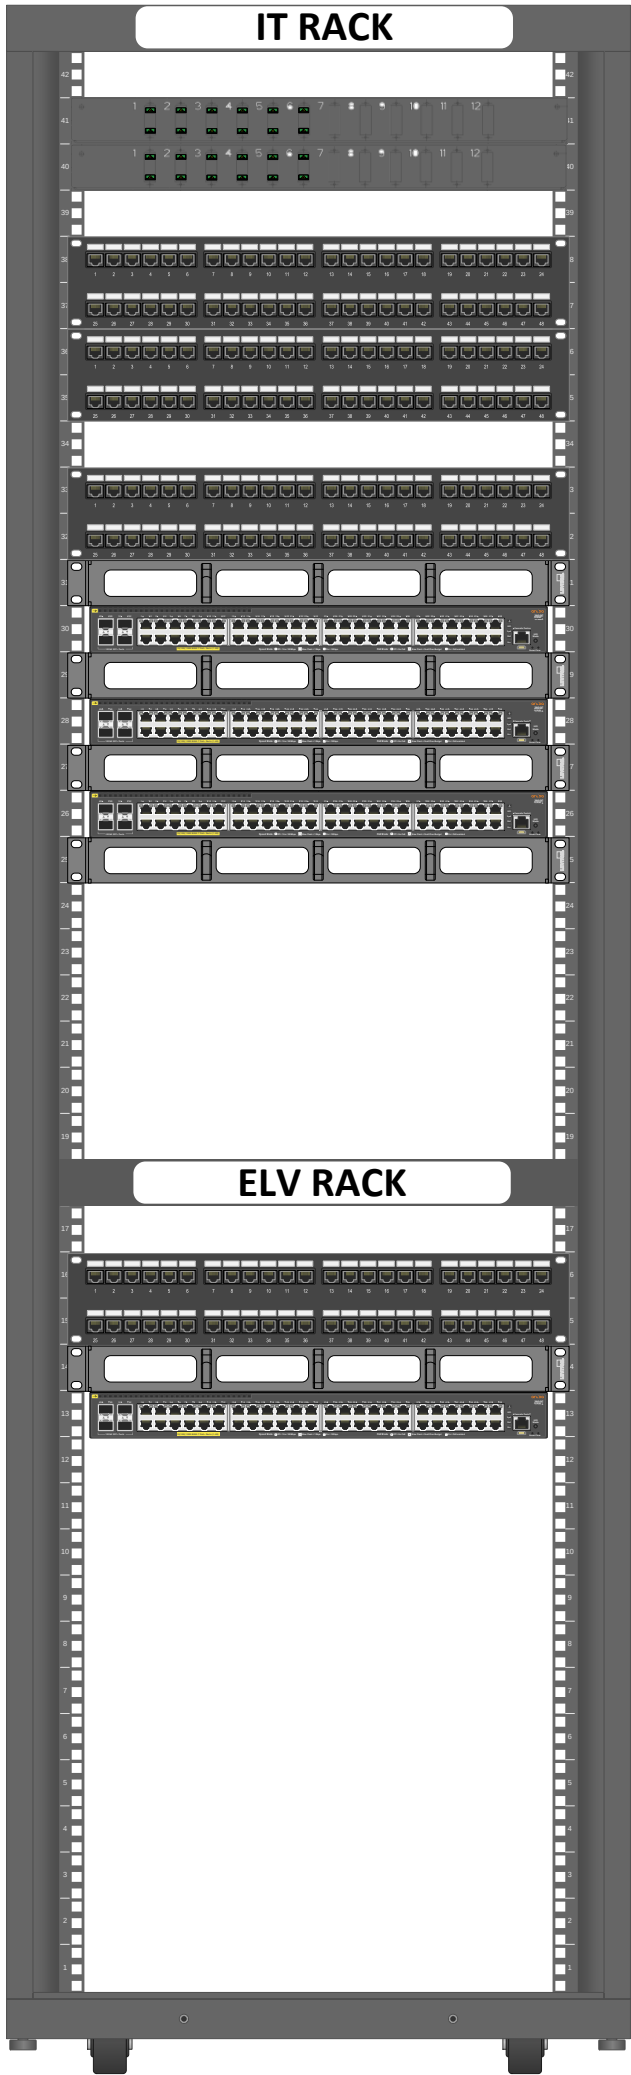


DỰ ÁN: TỔ HỢP KHÁCH SẠN, CĂN HỘ DỊCH VỤ MARRIOTT VÀ NHÀ Ở ĐỂ BÁN ĐỊA ĐIỂM XÂY DỰNG: 58 BẠCH ĐẰNG, P. HẢI CHÂU 1, Q. HẢI CHÂU, TP. ĐÀ NẴNG	
CHỦ ĐẦU TƯ: CÔNG TY CỔ PHẦN ĐỊA ỐC FOODINCO ĐỊA CHỈ: 58 BẠCH ĐẰNG, P. HẢI CHÂU 1, Q. HẢI CHÂU, TP. ĐÀ NẴNG	
BAN QUẢN LÝ DỰ ÁN:	
TƯ VẤN GIÁM SÁT: CN CÔNG TY TNHH APAVE CHÂU Á - THÁI BÌNH DƯƠNG TẠI ĐÀ NẴNG NGUYỄN ĐĂNG HÙNG	
ĐƠN VỊ NHÀ THẦU CHÍNH: CÔNG TY CỔ PHẦN ALPHANAM E&C	
NHÀ THẦU THI CÔNG:  CÔNG TY TNHH VIỄN THÔNG SÁNG TẠO THUẬN PHONG (INNOTEL) 55/31 TRẦN ĐÌNH XU, P. CẦU KHO, Q. 1, HCM Tel: (84 28) 3 862 1119 Fax: (84 28) 3 863 0366	
CHỈ HUY TRƯỞNG:	
NGƯỜI KIỂM TRA:	
NGƯỜI LẬP:	
TÊN BẢN VẼ: RACK LAYOUT IDF-M.1F	
NGÀY HT:	01/09/2022
CHỈNH SỬA:	01
MÃ BẢN VẼ:	IDF-M.1F
HỒ SƠ THAM CHIẾU:	220726 ELV - CAP NHAT CCTV THEO Y KIEN MI GS&S

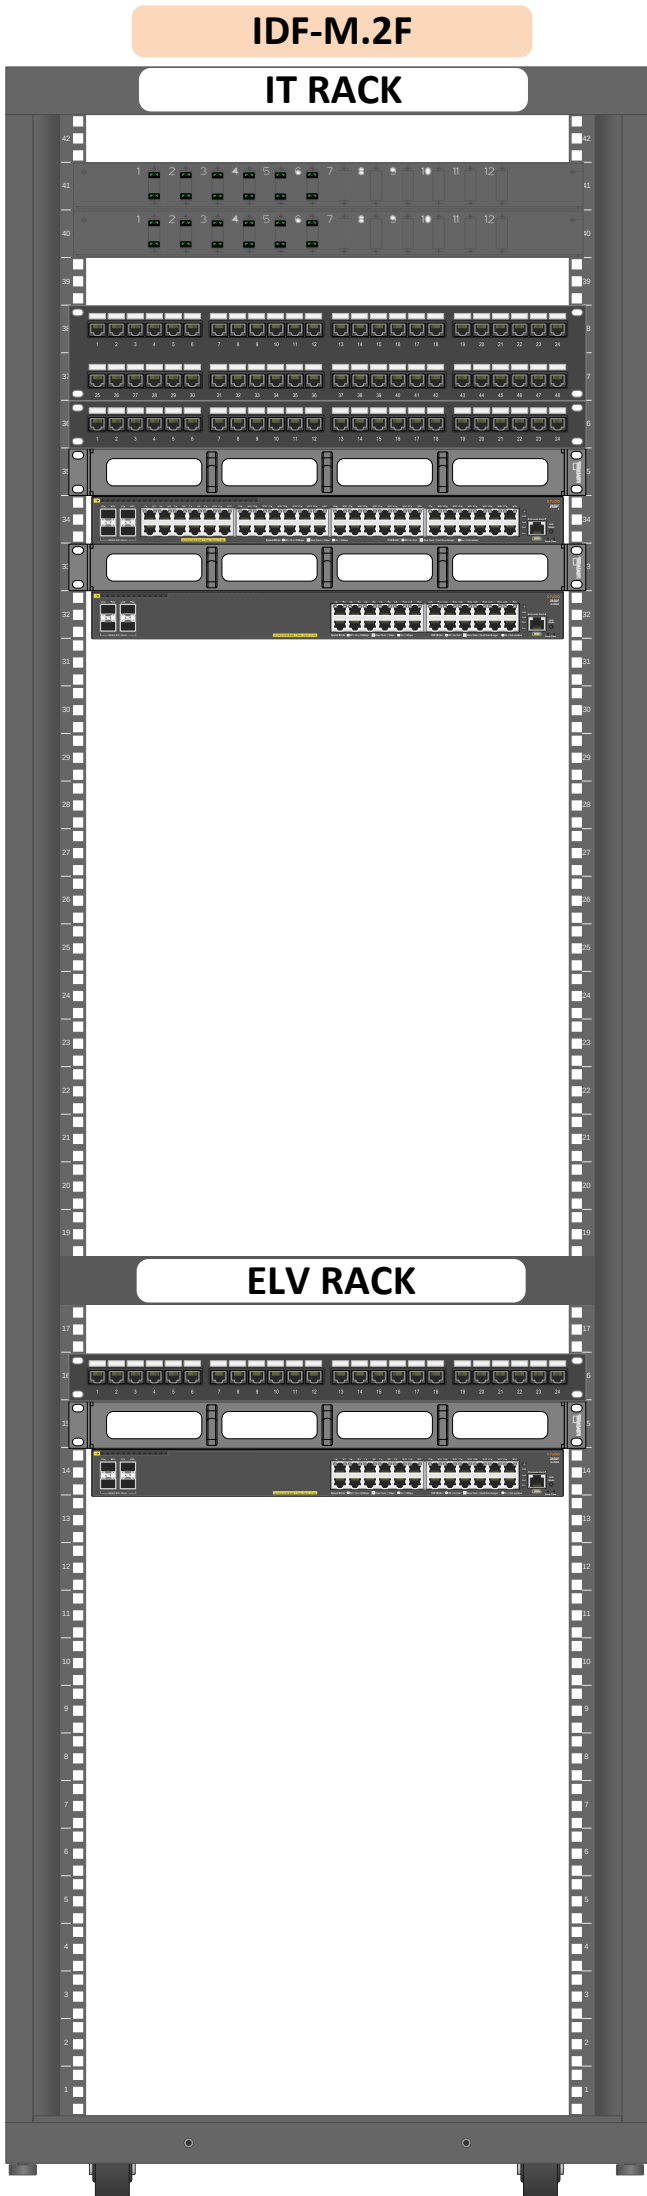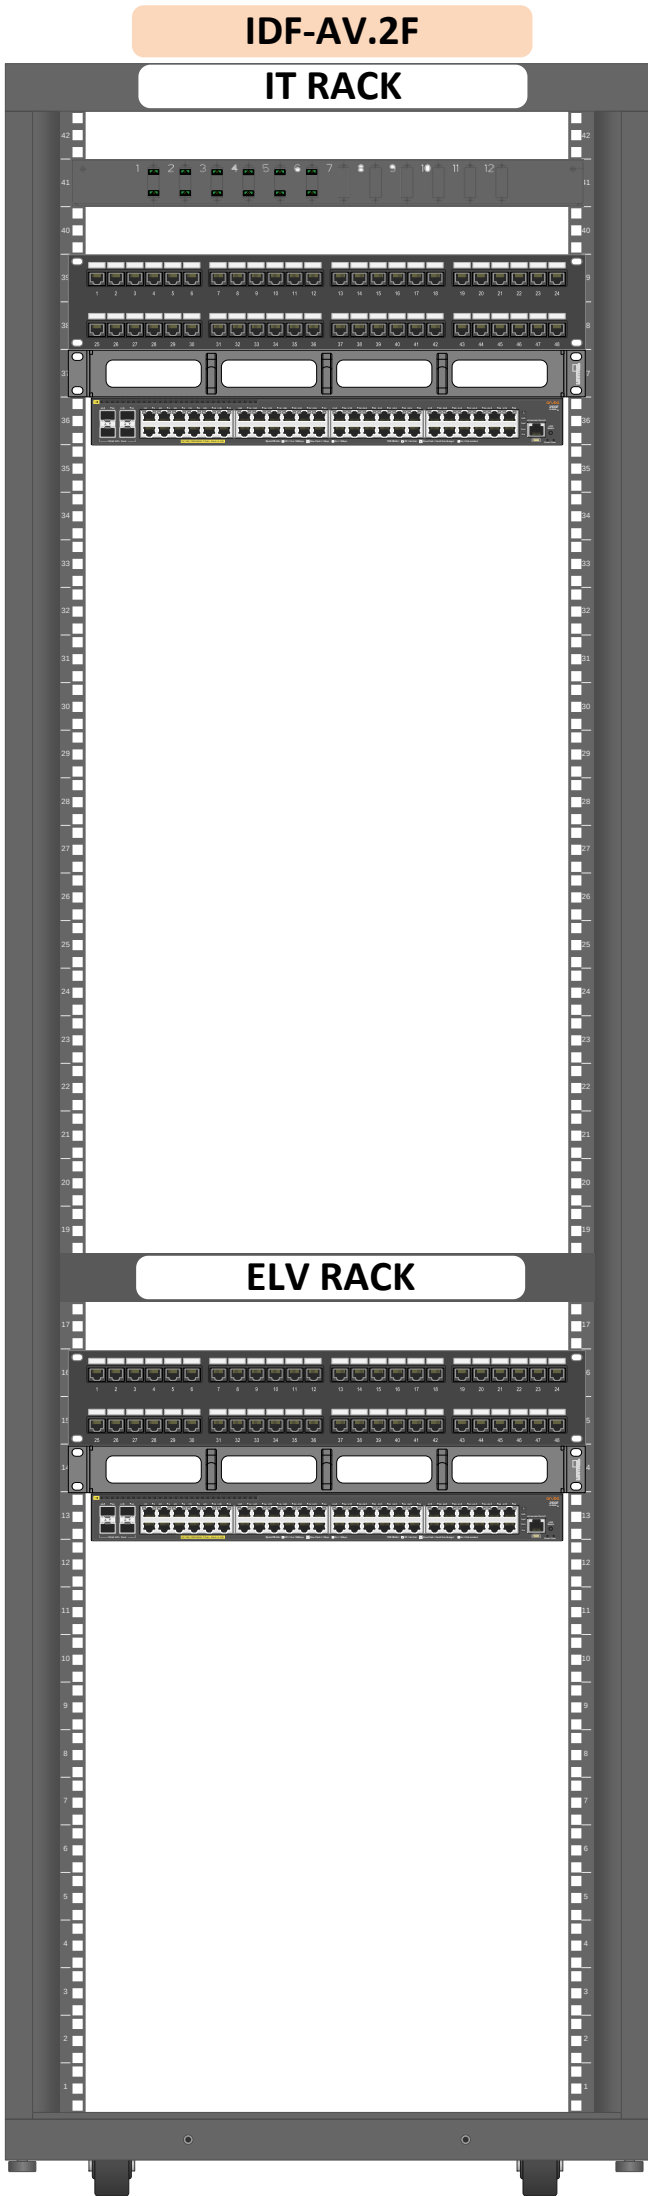



Dự Án: TỔ HỢP KHÁCH SẠN, CĂN HỘ DỊCH VỤ MARRIOTT VÀ NHÀ Ở ĐỂ BÁN Địa Điểm Xây Dựng: 58 Bạch Đằng, P. Hải Châu 1, Q. Hải Châu, TP. Đà Nẵng	
Chủ Đầu Tư: CÔNG TY CỔ PHẦN ĐỊA ỐC FOODINCO Địa Chỉ: 58 Bạch Đằng, P. Hải Châu 1, Q. Hải Châu, TP. Đà Nẵng	
Ban Quản Lý Dự Án:	
Tư Vấn Giám Sát: CN CÔNG TY TNHH APAVE CHÂU Á - THÁI BÌNH DƯƠNG TẠI ĐÀ NẴNG NGUYỄN ĐĂNG HÙNG	
Đơn Vị Nhà Thầu Chính: CÔNG TY CỔ PHẦN ALPHANAM E&C	
Nhà Thầu Thi Công: innotel maximizing your access CÔNG TY TNHH VIỄN THÔNG SÁNG TẠO THUẬN PHONG (INNOTEL) 55/31 TRẦN ĐÌNH XU, P. CẦU KHO, Q. 1, HCM Tel: (84 28) 3 862 1119 Fax: (84 28) 3 863 0366	
Chỉ Huy Trưởng:	
NGUYỄN ĐỨC TIẾN	
Người Kiểm Tra:	
Người Lập:	
Tên Bản Vẽ: RACK LAYOUT IDF-AV.2F & IDF-M.2F	
Ngày HT:	01/09/2022
Chỉnh Sửa:	01
Mã Bản Vẽ:	IDF-AV.2F & M.2F
Hồ Sơ Tham Chiếu:	220726 ELV - CAP NHAT CCTV THEO Y KIẾN MI GS&S

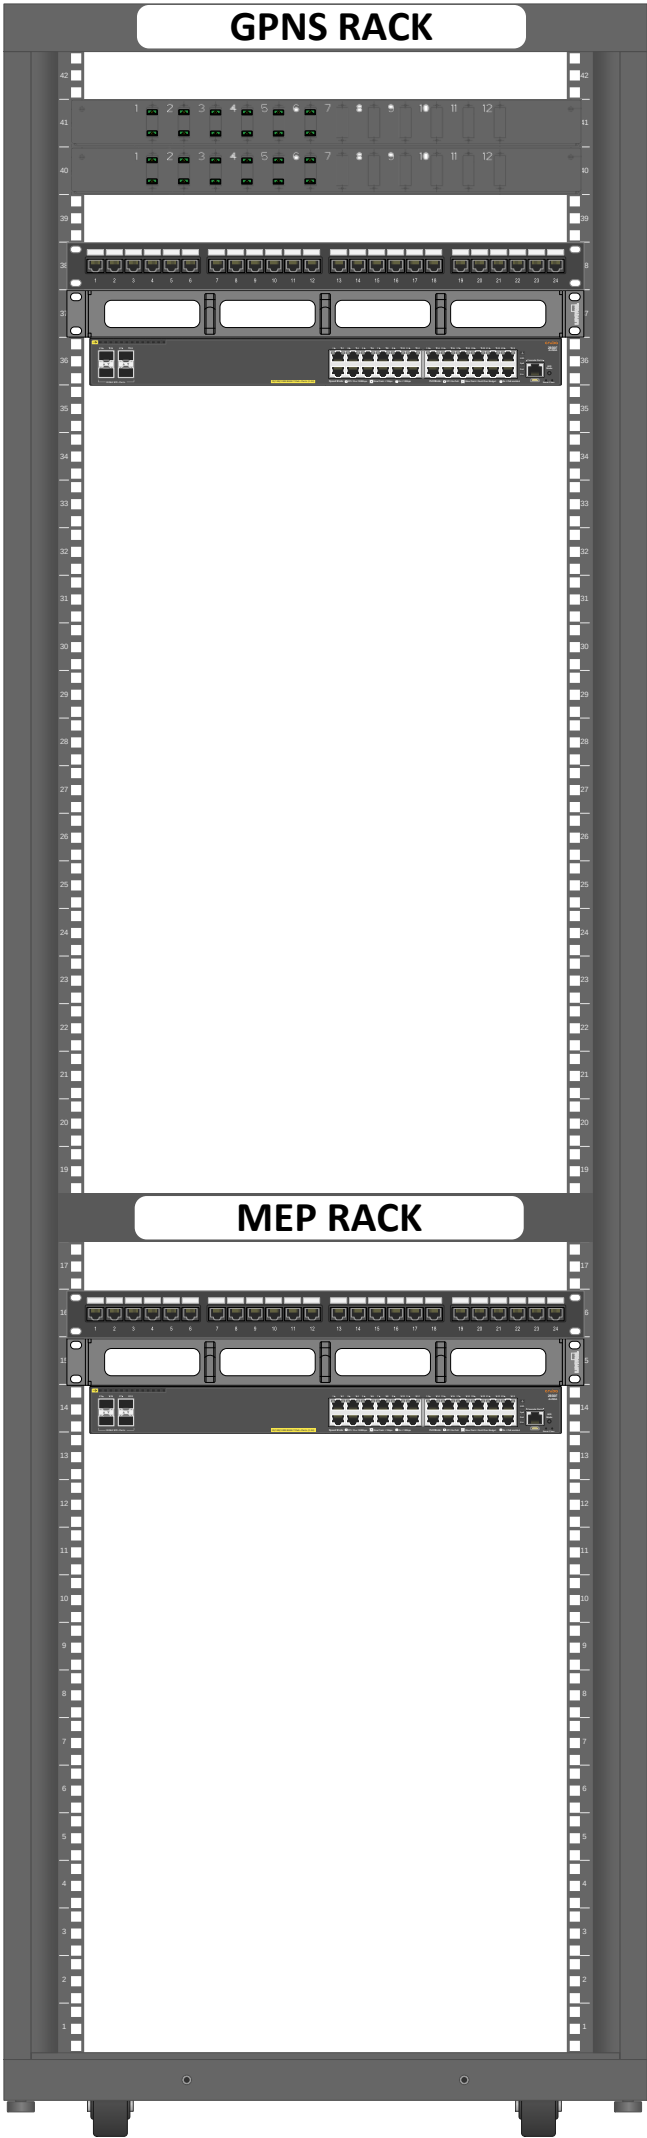


DỰ ÁN: TỔ HỢP KHÁCH SẠN, CĂN HỘ DỊCH VỤ MARRIOTT VÀ NHÀ Ở ĐỂ BÁN ĐỊA ĐIỂM XÂY DỰNG: 58 BẠCH ĐẰNG, P. HẢI CHÂU 1, Q. HẢI CHÂU, TP. ĐÀ NẴNG	
CHỦ ĐẦU TƯ: CÔNG TY CỔ PHẦN ĐỊA ỐC FOODINCO ĐỊA CHỈ: 58 BẠCH ĐẰNG, P. HẢI CHÂU 1, Q. HẢI CHÂU, TP. ĐÀ NẴNG	
BAN QUẢN LÝ DỰ ÁN:	
TƯ VẤN GIÁM SÁT: CN CÔNG TY TNHH APAVE CHÂU Á - THÁI BÌNH DƯƠNG TẠI ĐÀ NẴNG NGUYỄN ĐĂNG HÙNG	
ĐƠN VỊ NHÀ THẦU CHÍNH: CÔNG TY CỔ PHẦN ALPHANAM E&C	
NHÀ THẦU THI CÔNG:  CÔNG TY TNHH VIỄN THÔNG SÁNG TẠO THUẬN PHONG (INNOTEL) 55/31 TRẦN ĐÌNH XU, P. CẦU KHO, Q. 1, HCM Tel: (84 28) 3 862 1119 Fax: (84 28) 3 863 0366	
CHỈ HUY TRƯỞNG:	
NGUYỄN ĐỨC TIẾN	
NGƯỜI KIỂM TRA:	
NGƯỜI LẬP:	
TÊN BẢN VẼ: RACK LAYOUT IDF-A.2F (MLM)	
NGÀY HT:	01/09/2022
CHỈNH SỬA:	01
MÃ BẢN VẼ:	IDF A.2F
HỒ SƠ THAM CHIẾU:	220726 ELV - CAP NHAT CCTV THEO Y KIEN MI GS&S

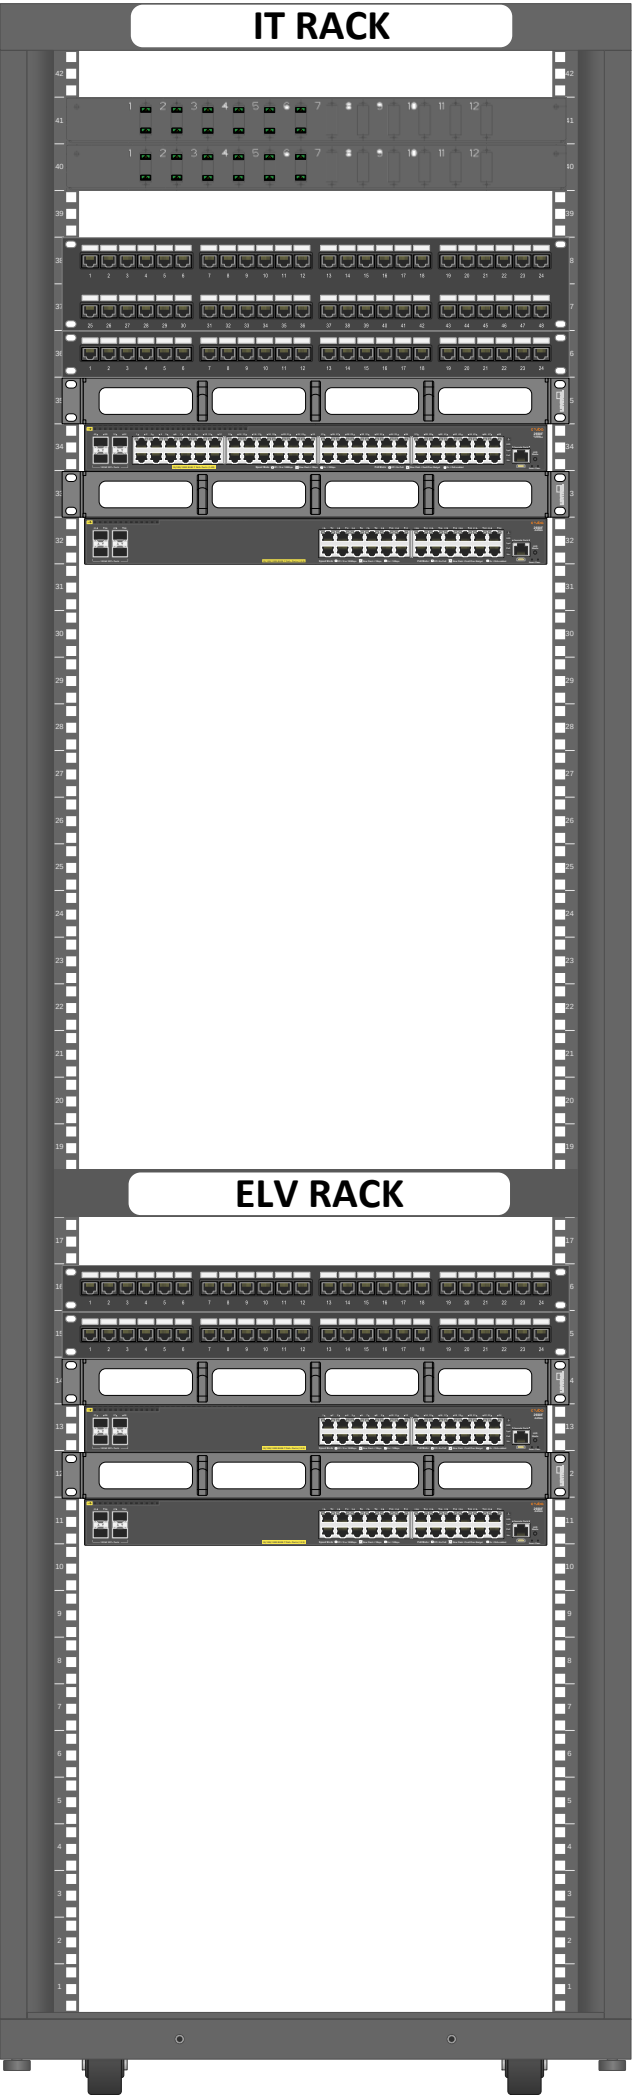


DỰ ÁN: TỔ HỢP KHÁCH SẠN, CĂN HỘ DỊCH VỤ MARRIOTT VÀ NHÀ Ở ĐỂ BÁN ĐỊA ĐIỂM XÂY DỰNG: 58 BẠCH ĐẰNG, P. HẢI CHÂU 1, Q. HẢI CHÂU, TP. ĐÀ NẴNG	
CHỦ ĐẦU TƯ: CÔNG TY CỔ PHẦN ĐỊA ỐC FOODINCO ĐỊA CHỈ: 58 BẠCH ĐẰNG, P. HẢI CHÂU 1, Q. HẢI CHÂU, TP. ĐÀ NẴNG	
BAN QUẢN LÝ DỰ ÁN:	
TƯ VẤN GIÁM SÁT: CN CÔNG TY TNHH APAVE CHÂU Á - THÁI BÌNH DƯƠNG TẠI ĐÀ NẴNG NGUYỄN ĐĂNG HÙNG	
ĐƠN VỊ NHÀ THẦU CHÍNH: CÔNG TY CỔ PHẦN ALPHANAM E&C	
NHÀ THẦU THI CÔNG:  CÔNG TY TNHH VIỄN THÔNG SÁNG TẠO THUẬN PHONG (INNOTEL) 55/31 TRẦN ĐÌNH XU, P. CẦU KHO, Q. 1, HCM Tel: (84 28) 3 862 1119 Fax: (84 28) 3 863 0366	
CHỈ HUY TRƯỞNG:	
NGUYỄN ĐỨC TIẾN	
NGƯỜI KIỂM TRA:	
NGƯỜI LẬP:	
TÊN BẢN VẼ: RACK LAYOUT IDF-M.3F	
NGÀY HT:	01/09/2022
CHỈNH SỬA:	01
MÃ BẢN VẼ:	IDF-M.3F
HỒ SƠ THAM CHIẾU:	220726 ELV - CAP NHAT CCTV THEO Y KIEN MI GS&S

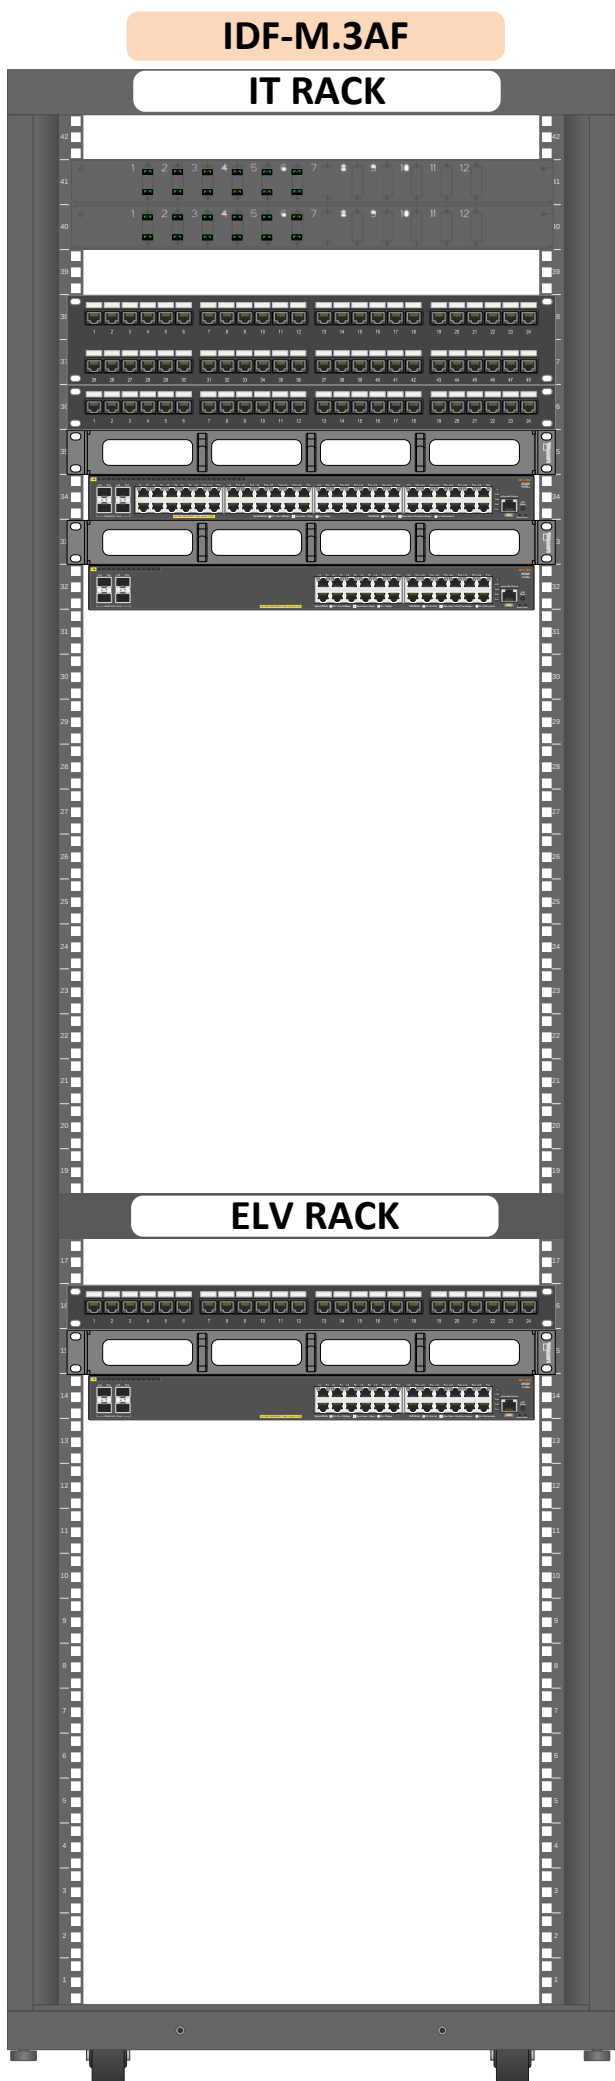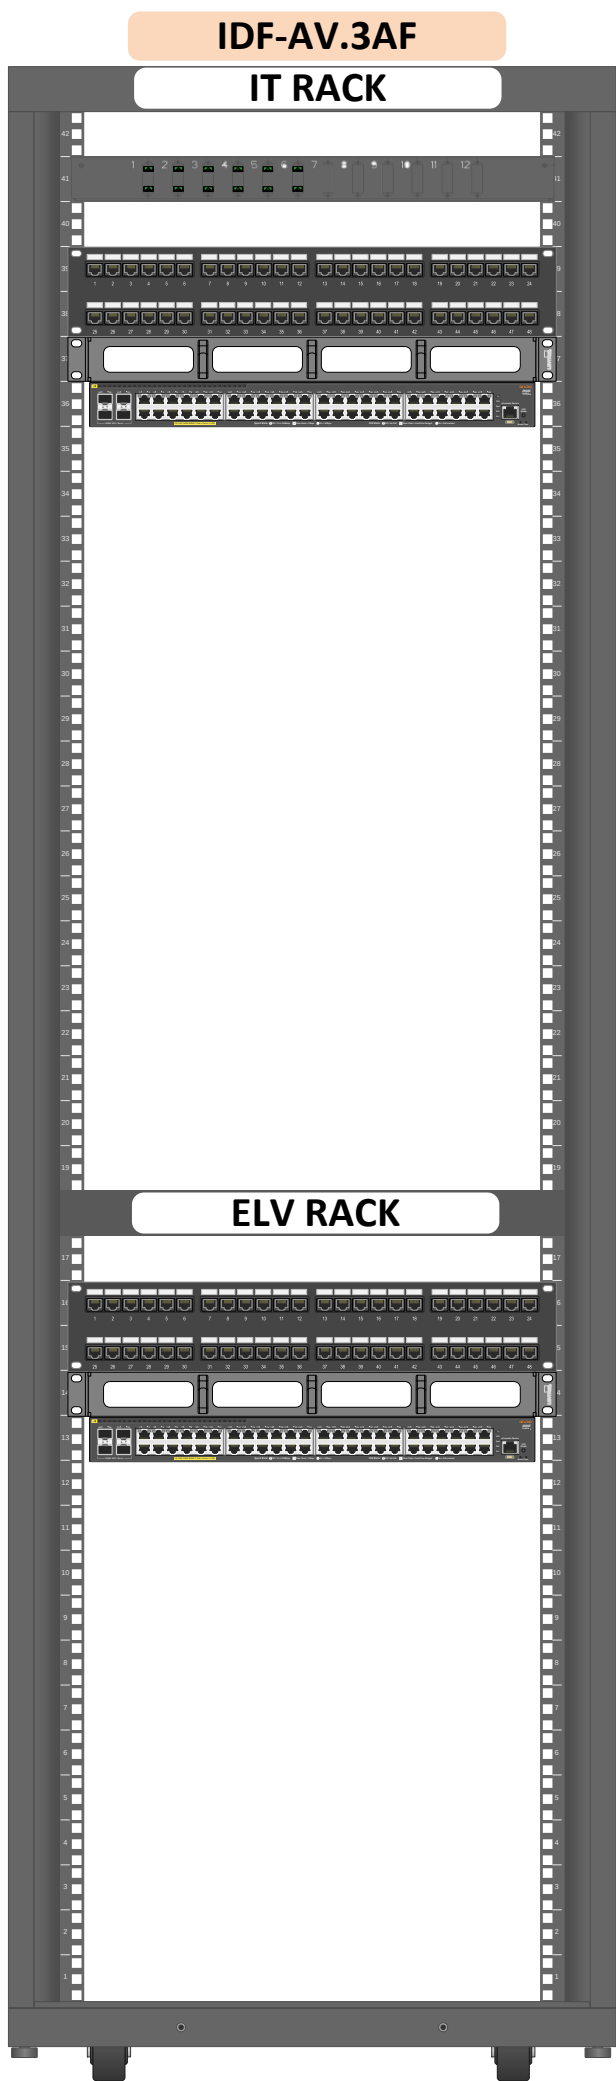


DỰ ÁN: TỔ HỢP KHÁCH SẠN, CĂN HỘ DỊCH VỤ MARRIOTT VÀ NHÀ Ở ĐỂ BÁN ĐỊA ĐIỂM XÂY DỰNG: 58 BẠCH ĐẰNG, P. HẢI CHÂU 1, Q. HẢI CHÂU, TP. ĐÀ NẴNG	
CHỦ ĐẦU TƯ: CÔNG TY CỔ PHẦN ĐỊA ỐC FOODINCO ĐỊA CHỈ: 58 BẠCH ĐẰNG, P. HẢI CHÂU 1, Q. HẢI CHÂU, TP. ĐÀ NẴNG	
BAN QUẢN LÝ DỰ ÁN:	
TƯ VẤN GIÁM SÁT: CN CÔNG TY TNHH APAVE CHÂU Á - THÁI BÌNH DƯƠNG TẠI ĐÀ NẴNG NGUYỄN ĐĂNG HÙNG	
ĐƠN VỊ NHÀ THẦU CHÍNH: CÔNG TY CỔ PHẦN ALPHANAM E&C	
NHÀ THẦU THI CÔNG:  CÔNG TY TNHH VIỄN THÔNG SÁNG TẠO THUẬN PHONG (INNOTEL) 55/31 TRẦN ĐÌNH XU, P. CẦU KHO, Q. 1, HCM Tel: (84 28) 3 862 1119 Fax: (84 28) 3 863 0366	
CHỈ HUY TRƯỞNG:	
NGƯỜI KIỂM TRA:	
NGƯỜI LẬP:	
TÊN BẢN VẼ: RACK LAYOUT IDF-AV.3AF & IDF-M.3AF	
NGÀY HT:	01/09/2022
CHỈNH SỬA:	01
MÃ BẢN VẼ:	IDF-AV.3AF & M.3AF
HỒ SƠ THAM CHIẾU:	220726 ELV - CAP NHAT CCTV THEO Y KIEN MI GS&S

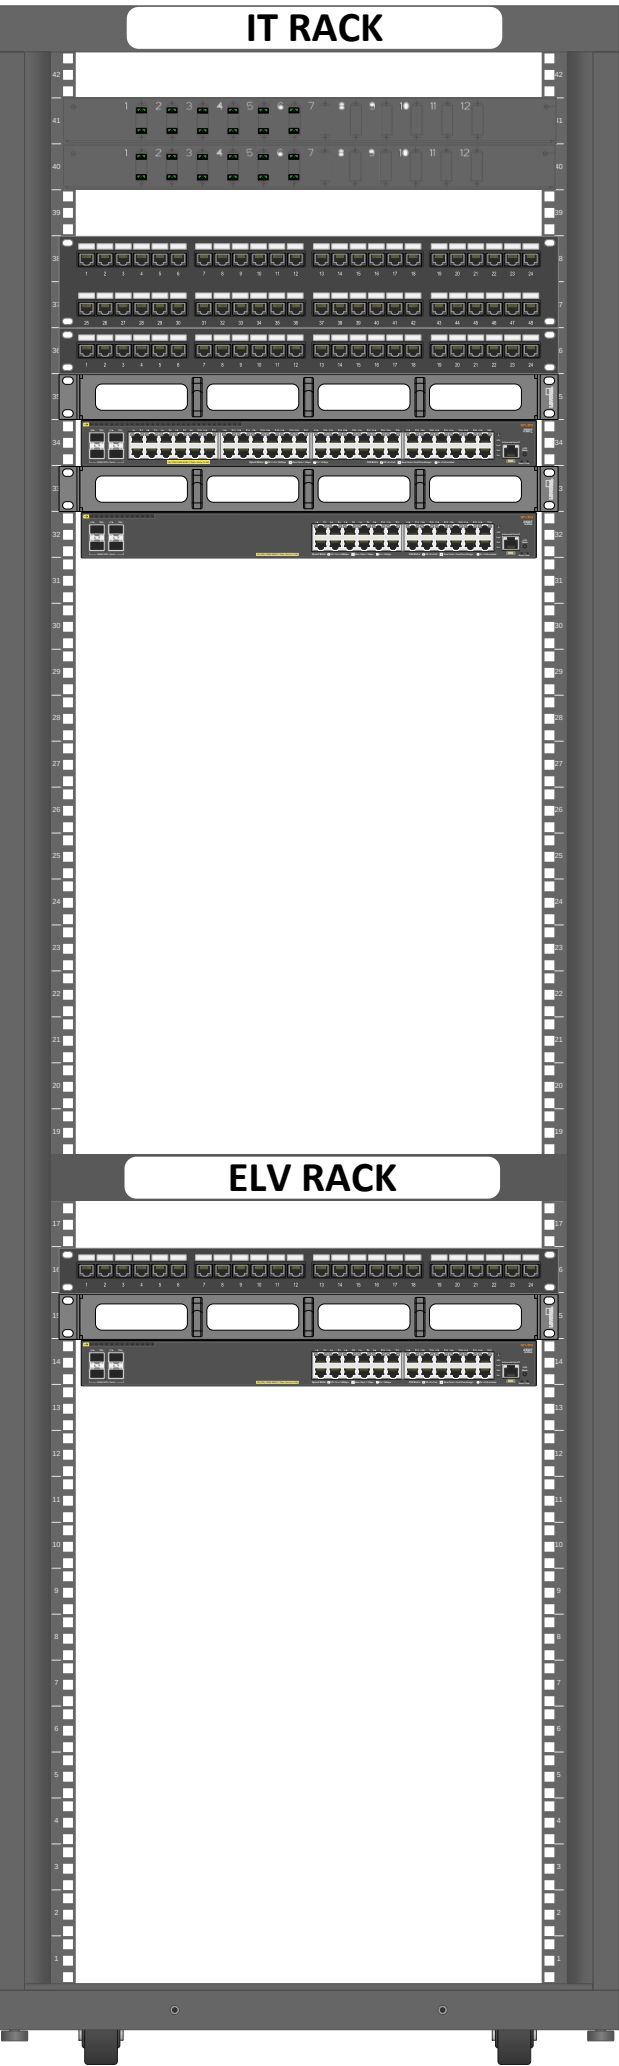


DỰ ÁN: TỔ HỢP KHÁCH SẠN, CĂN HỘ DỊCH VỤ MARRIOTT VÀ NHÀ Ở ĐỂ BÁN ĐỊA ĐIỂM XÂY DỰNG: 58 BẠCH ĐẰNG, P. HẢI CHÂU 1, Q. HẢI CHÂU, TP. ĐÀ NẴNG	
CHỦ ĐẦU TƯ: CÔNG TY CỔ PHẦN ĐỊA ỐC FOODINCO ĐỊA CHỈ: 58 BẠCH ĐẰNG, P. HẢI CHÂU 1, Q. HẢI CHÂU, TP. ĐÀ NẴNG	
BAN QUẢN LÝ DỰ ÁN:	
TƯ VẤN GIÁM SÁT: CN CÔNG TY TNHH APAVE CHÂU Á - THÁI BÌNH DƯƠNG TẠI ĐÀ NẴNG NGUYỄN ĐĂNG HÙNG	
ĐƠN VỊ NHÀ THẦU CHÍNH: CÔNG TY CỔ PHẦN ALPHANAM E&C	
NHÀ THẦU THI CÔNG:  CÔNG TY TNHH VIỄN THÔNG SÁNG TẠO THUẬN PHONG (INNOTEL) 55/31 TRẦN ĐÌNH XU, P. CẦU KHO, Q. 1, HCM Tel: (84 28) 3 862 1119 Fax: (84 28) 3 863 0366	
CHỈ HUY TRƯỞNG:	
NGUYỄN ĐỨC TIẾN	
NGƯỜI KIỂM TRA:	
NGƯỜI LẬP:	
TÊN BẢN VẼ: RACK LAYOUT IDF-M.4F	
NGÀY HT:	01/09/2022
CHỈNH SỬA:	01
MÃ BẢN VẼ:	IDF-M.4F
HỒ SƠ THAM CHIẾU:	220726 ELV - CAP NHAT CCTV THEO Y KIEN MI GS&S

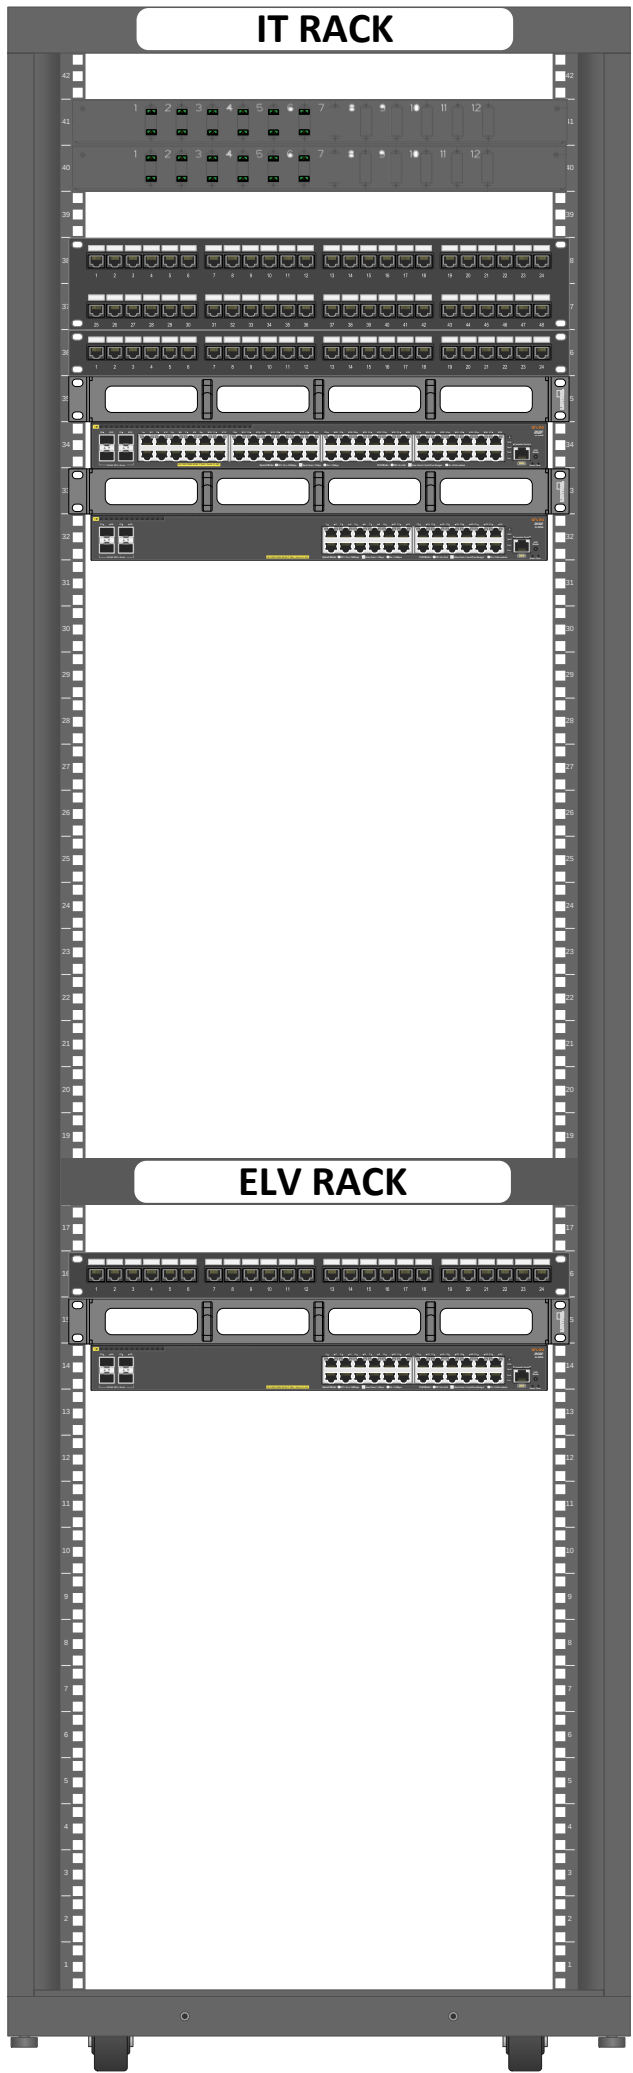


DỰ ÁN: TỔ HỢP KHÁCH SẠN, CĂN HỘ DỊCH VỤ MARRIOTT VÀ NHÀ Ở ĐỂ BÁN ĐỊA ĐIỂM XÂY DỰNG: 58 BẠCH ĐẰNG, P. HẢI CHÂU 1, Q. HẢI CHÂU, TP. ĐÀ NẴNG	
CHỦ ĐẦU TƯ: CÔNG TY CỔ PHẦN ĐỊA ỐC FOODINCO ĐỊA CHỈ: 58 BẠCH ĐẰNG, P. HẢI CHÂU 1, Q. HẢI CHÂU, TP. ĐÀ NẴNG	
BAN QUẢN LÝ DỰ ÁN:	
TƯ VẤN GIÁM SÁT: CN CÔNG TY TNHH APAVE CHÂU Á - THÁI BÌNH DƯƠNG TẠI ĐÀ NẴNG NGUYỄN ĐĂNG HÙNG	
ĐƠN VỊ NHÀ THẦU CHÍNH: CÔNG TY CỔ PHẦN ALPHANAM E&C	
NHÀ THẦU THI CÔNG:  CÔNG TY TNHH VIỄN THÔNG SÁNG TẠO THUẬN PHONG (INNOTEL) 55/31 TRẦN ĐÌNH XU, P. CẦU KHO, Q. 1, HCM Tel: (84 28) 3 862 1119 Fax: (84 28) 3 863 0366	
CHỈ HUY TRƯỞNG:	
NGUYỄN ĐỨC TIẾN	
NGƯỜI KIỂM TRA:	
NGƯỜI LẬP:	
TÊN BẢN VẼ: RACK LAYOUT IDF-M.4AF	
NGÀY HT:	01/09/2022
CHỈNH SỬA:	01
MÃ BẢN VẼ:	IDF-M.4AF
HỒ SƠ THAM CHIẾU:	220726 ELV - CAP NHAT CCTV THEO Y KIEN MI GS&S

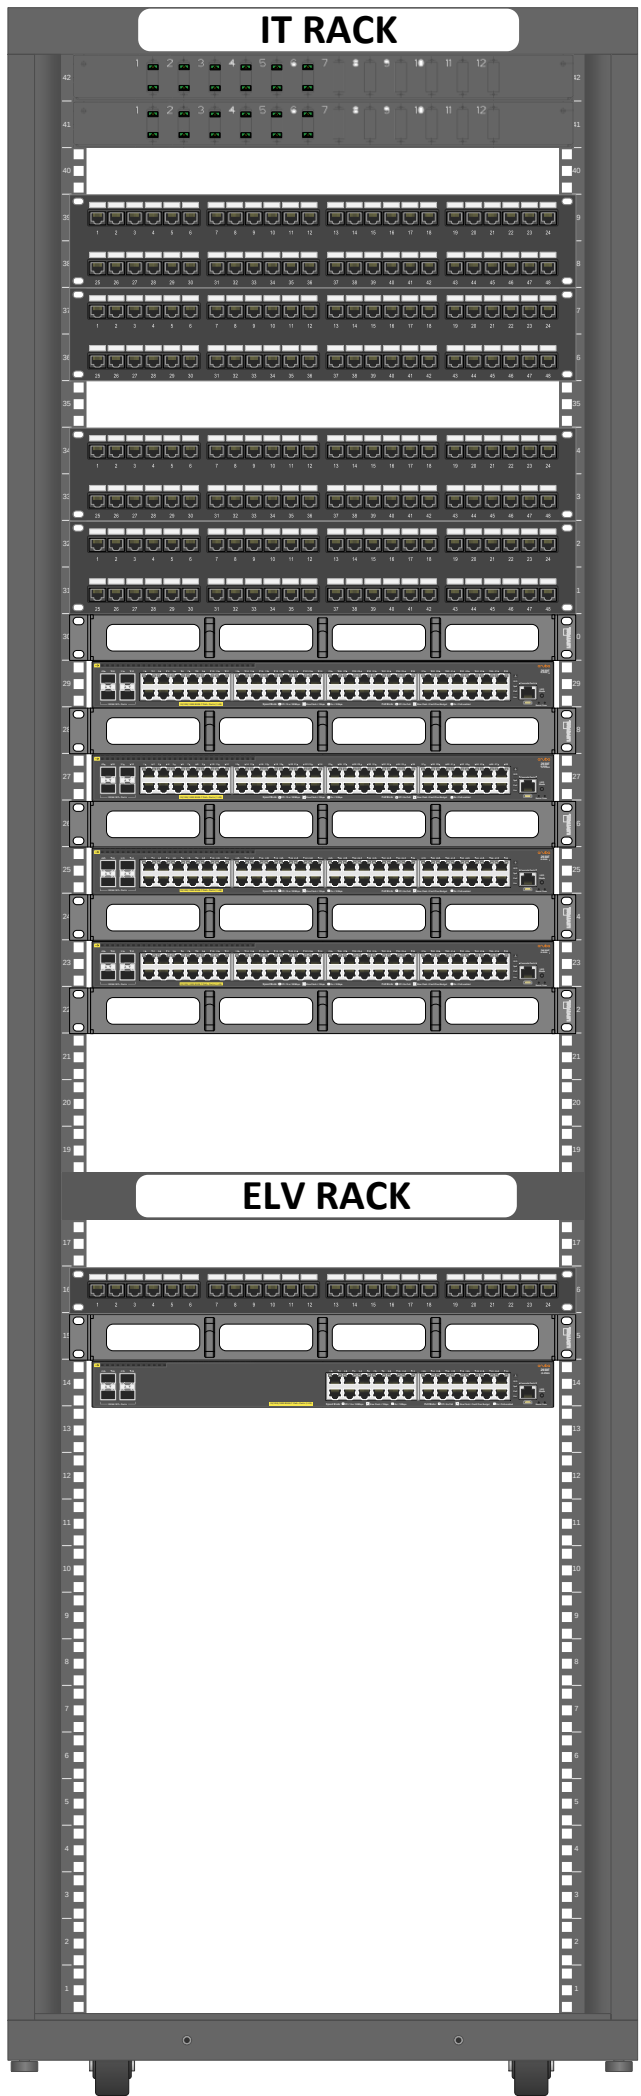


DỰ ÁN: TỔ HỢP KHÁCH SẠN, CĂN HỘ DỊCH VỤ MARRIOTT VÀ NHÀ Ở ĐỂ BÁN ĐỊA ĐIỂM XÂY DỰNG: 58 BẠCH ĐẰNG, P. HẢI CHÂU 1, Q. HẢI CHÂU, TP. ĐÀ NẴNG	
CHỦ ĐẦU TƯ: CÔNG TY CỔ PHẦN ĐỊA ỐC FOODINCO ĐỊA CHỈ: 58 BẠCH ĐẰNG, P. HẢI CHÂU 1, Q. HẢI CHÂU, TP. ĐÀ NẴNG	
BAN QUẢN LÝ DỰ ÁN:	
TƯ VẤN GIÁM SÁT: CN CÔNG TY TNHH APAVE CHÂU Á - THÁI BÌNH DƯƠNG TẠI ĐÀ NẴNG NGUYỄN ĐĂNG HÙNG	
ĐƠN VỊ NHÀ THẦU CHÍNH: CÔNG TY CỔ PHẦN ALPHANAM E&C	
NHÀ THẦU THI CÔNG:  CÔNG TY TNHH VIỄN THÔNG SÁNG TẠO THUẬN PHONG (INNOTEL) 55/31 TRẦN ĐÌNH XU, P. CẦU KHO, Q. 1, HCM Tel: (84 28) 3 862 1119 Fax: (84 28) 3 863 0366	
CHỈ HUY TRƯỞNG:	
NGUYỄN ĐỨC TIẾN	
NGƯỜI KIỂM TRA:	
NGƯỜI LẬP:	
TÊN BẢN VẼ: RACK LAYOUT IDF-M.4BF	
NGÀY HT:	01/09/2022
CHỈNH SỬA:	01
MÃ BẢN VẼ:	IDF-M.4BF
HỒ SƠ THAM CHIẾU:	220726 ELV - CAP NHAT CCTV THEO Y KIEN MI GS&S

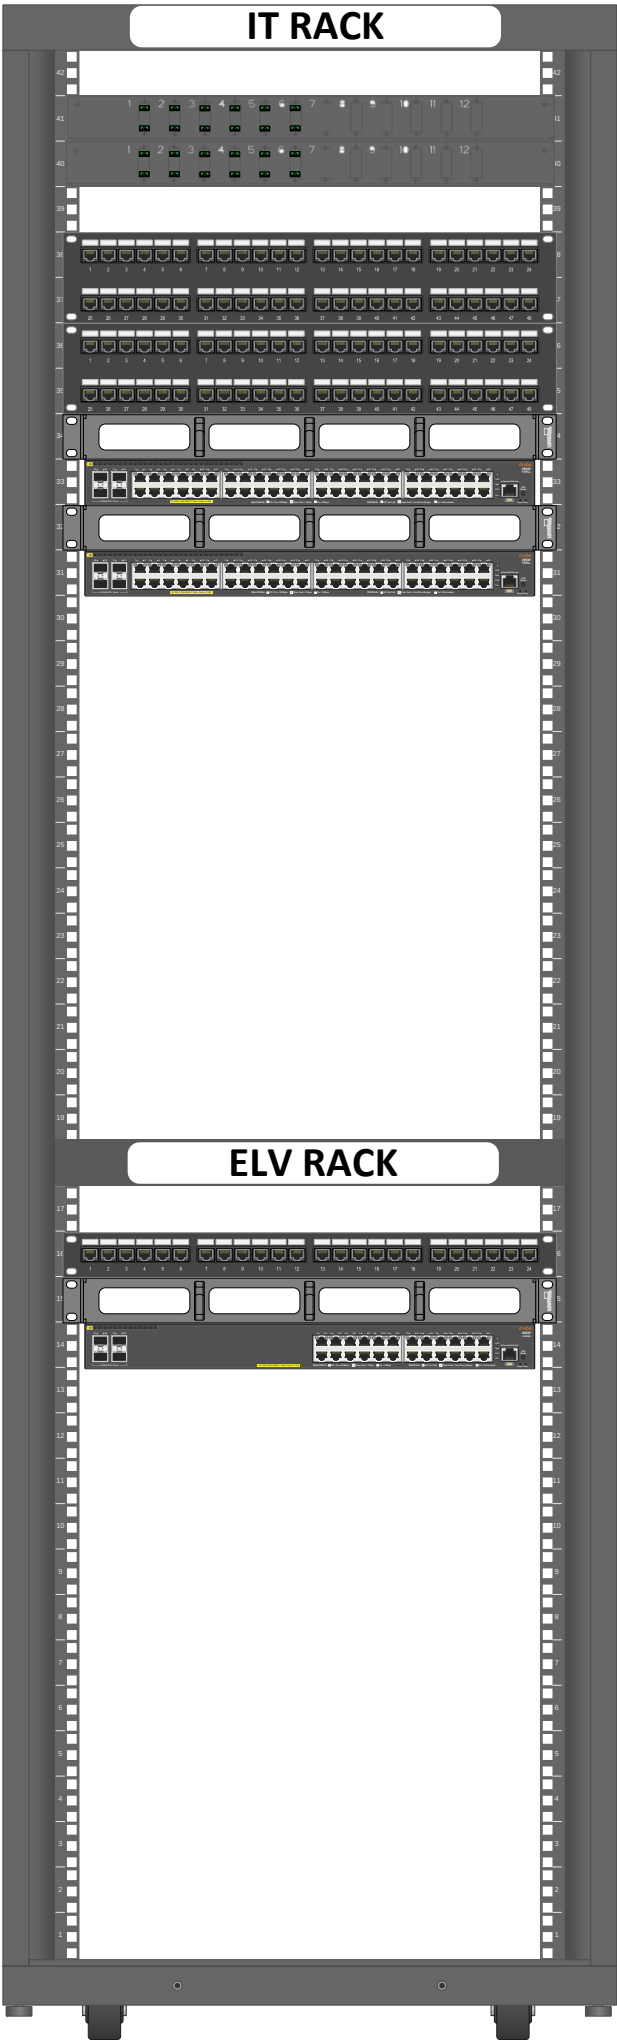


DỰ ÁN: TỔ HỢP KHÁCH SẠN, CĂN HỘ DỊCH VỤ MARRIOTT VÀ NHÀ Ở ĐỂ BÁN ĐỊA ĐIỂM XÂY DỰNG: 58 BẠCH ĐẰNG, P. HẢI CHÂU 1, Q. HẢI CHÂU, TP. ĐÀ NẴNG	
CHỦ ĐẦU TƯ: CÔNG TY CỔ PHẦN ĐỊA ỐC FOODINCO ĐỊA CHỈ: 58 BẠCH ĐẰNG, P. HẢI CHÂU 1, Q. HẢI CHÂU, TP. ĐÀ NẴNG	
BAN QUẢN LÝ DỰ ÁN:	
TƯ VẤN GIÁM SÁT: CN CÔNG TY TNHH APAVE CHÂU Á - THÁI BÌNH DƯƠNG TẠI ĐÀ NẴNG NGUYỄN ĐĂNG HÙNG	
ĐƠN VỊ NHÀ THẦU CHÍNH: CÔNG TY CỔ PHẦN ALPHANAM E&C	
NHÀ THẦU THI CÔNG:  CÔNG TY TNHH VIỄN THÔNG SÁNG TẠO THUẬN PHONG (INNOTEL) 55/31 TRẦN ĐÌNH XU, P. CẦU KHO, Q. 1, HCM Tel: (84 28) 3 862 1119 Fax: (84 28) 3 863 0366	
CHỈ HUY TRƯỞNG:	
NGUYỄN ĐỨC TIẾN	
NGƯỜI KIỂM TRA:	
NGƯỜI LẬP:	
TÊN BẢN VẼ: RACK LAYOUT IDF-M.5F	
NGÀY HT:	01/09/2022
CHỈNH SỬA:	01
MÃ BẢN VẼ:	IDF-M.5F
HỒ SƠ THAM CHIẾU:	220726 ELV - CAP NHAT CCTV THEO Y KIEN MI GS&S

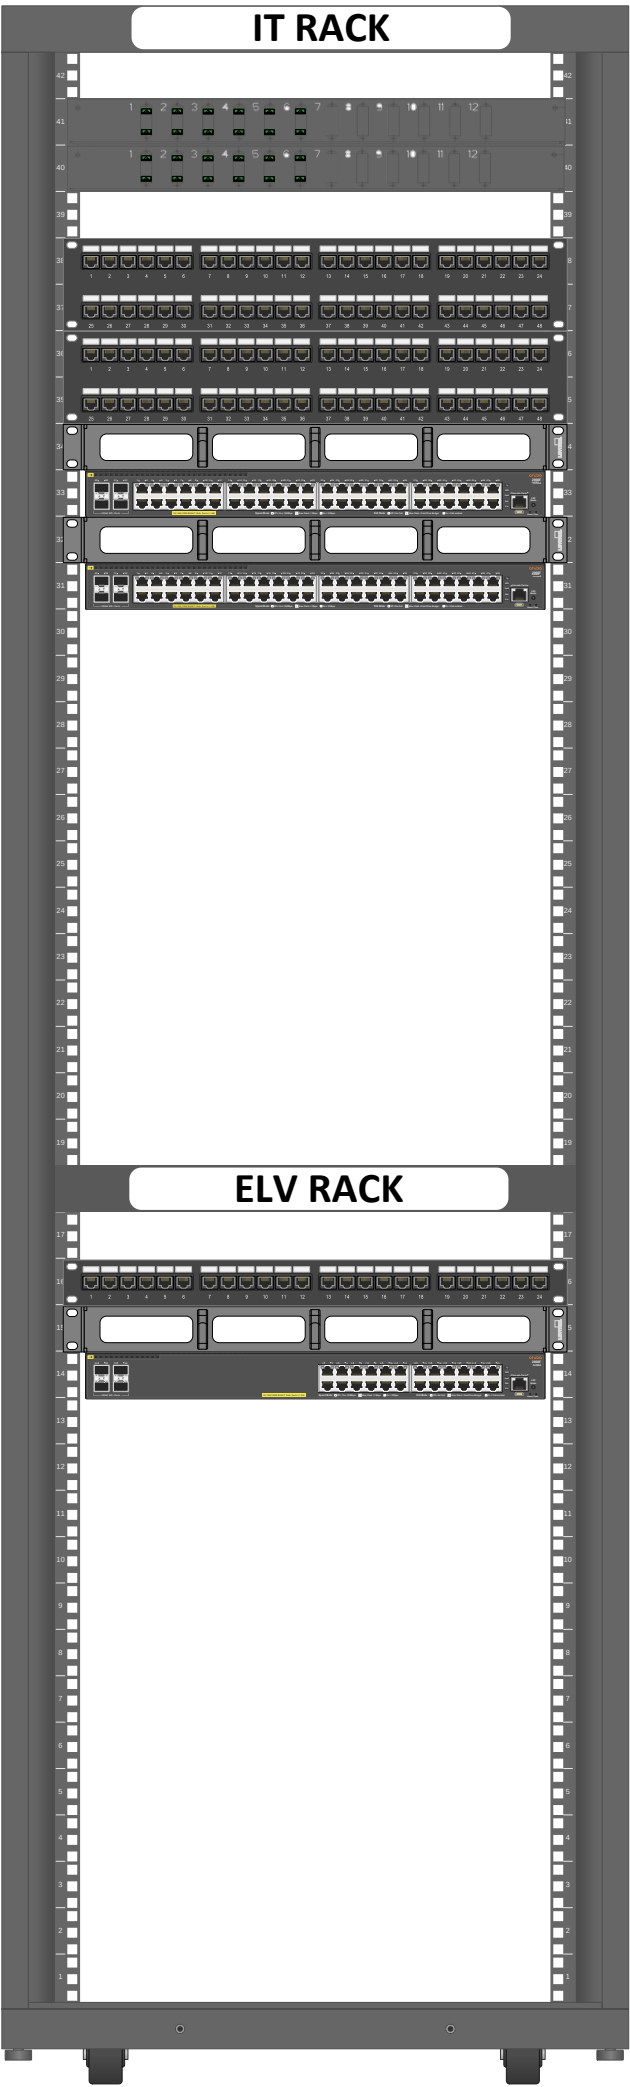


Dự án: TỔ HỢP KHÁCH SẠN, CĂN HỘ DỊCH VỤ MARRIOTT VÀ NHÀ Ở ĐỂ BÁN Địa điểm xây dựng: 58 Bạch Đằng, P. Hải Châu 1, Q. Hải Châu, TP. Đà Nẵng	
Chủ đầu tư: CÔNG TY CỔ PHẦN ĐỊA ỐC FOODINCO Địa chỉ: 58 Bạch Đằng, P. Hải Châu 1, Q. Hải Châu, TP. Đà Nẵng	
Ban quản lý dự án:	
Tư vấn giám sát: CN CÔNG TY TNHH APAVE CHÂU Á - THÁI BÌNH DƯƠNG TẠI ĐÀ NẴNG NGUYỄN ĐĂNG HÙNG	
Đơn vị nhà thầu chính: CÔNG TY CỔ PHẦN ALPHANAM E&C	
Nhà thầu thi công: innotel maximizing your access CÔNG TY TNHH VIỄN THÔNG SÁNG TẠO THUẬN PHONG (INNOTEL) 55/31 TRẦN ĐÌNH XU, P. CẦU KHO, Q. 1, HCM Tel: (84 28) 3 862 1119 Fax: (84 28) 3 863 0366	
Chỉ huy trưởng:	
NGUYỄN ĐỨC TIẾN	
Người kiểm tra:	
Người lập:	
Tên bản vẽ: RACK LAYOUT IDF-M.7F	
Ngày HT:	01/09/2022
Chỉnh sửa:	01
Mã bản vẽ:	IDF-M.7F
Hồ sơ tham chiếu:	220726 ELV - CAP NHAT CCTV THEO Y KIẾN MI GS&S

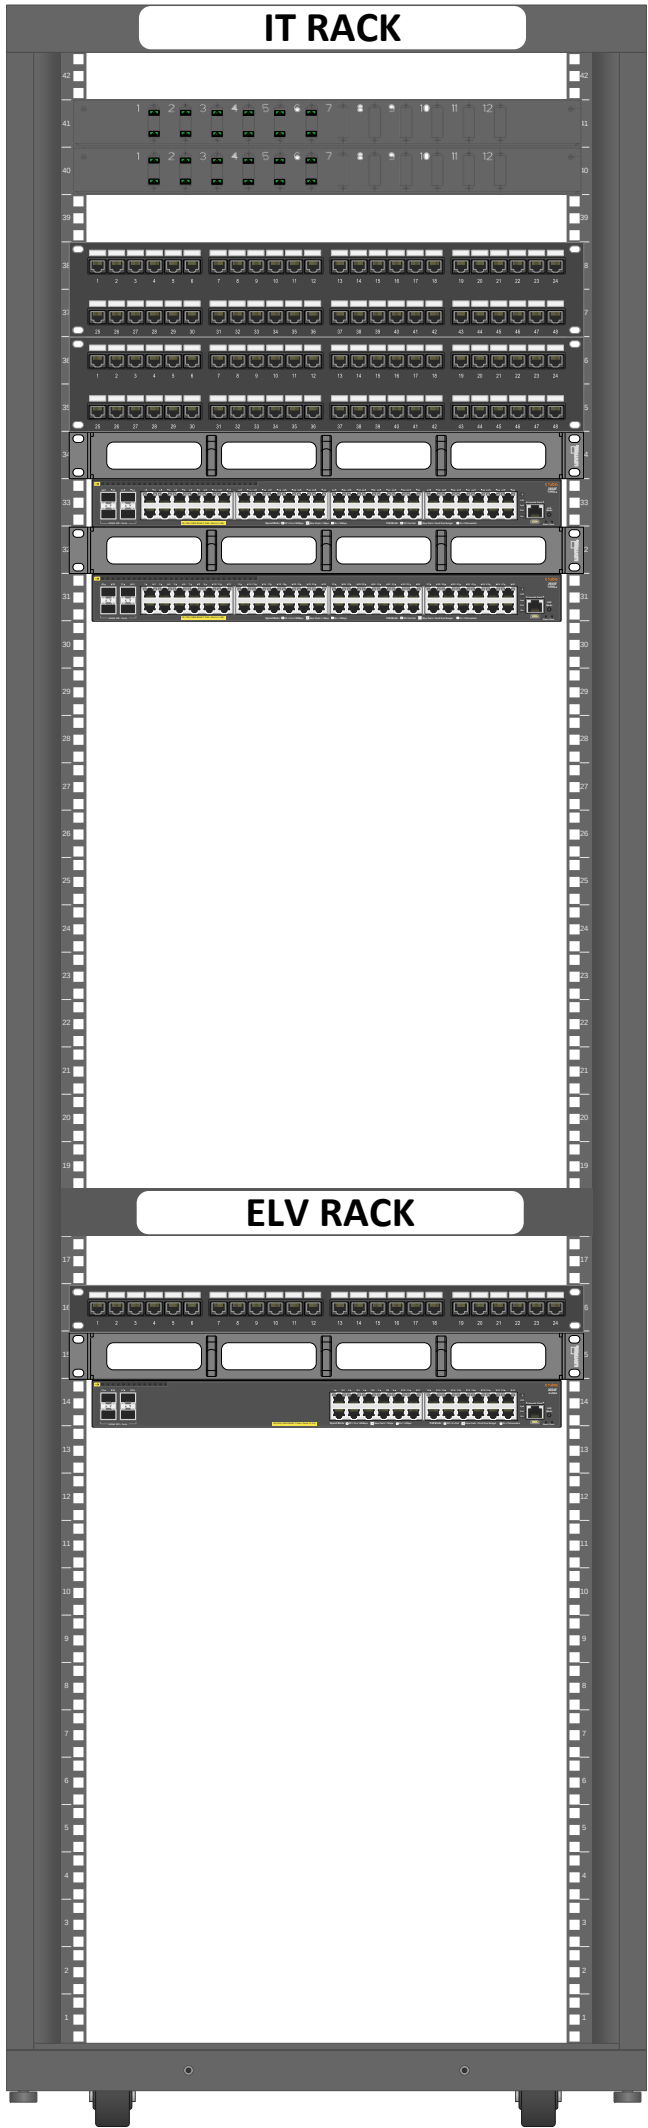


DỰ ÁN: TỔ HỢP KHÁCH SẠN, CĂN HỘ DỊCH VỤ MARRIOTT VÀ NHÀ Ở ĐỂ BÁN ĐỊA ĐIỂM XÂY DỰNG: 58 BẠCH ĐẰNG, P. HẢI CHÂU 1, Q. HẢI CHÂU, TP. ĐÀ NẴNG	
CHỦ ĐẦU TƯ: CÔNG TY CỔ PHẦN ĐỊA ỐC FOODINCO ĐỊA CHỈ: 58 BẠCH ĐẰNG, P. HẢI CHÂU 1, Q. HẢI CHÂU, TP. ĐÀ NẴNG	
BAN QUẢN LÝ DỰ ÁN:	
TƯ VẤN GIÁM SÁT: CN CÔNG TY TNHH APAVE CHÂU Á - THÁI BÌNH DƯƠNG TẠI ĐÀ NẴNG NGUYỄN ĐĂNG HÙNG	
ĐƠN VỊ NHÀ THẦU CHÍNH: CÔNG TY CỔ PHẦN ALPHANAM E&C	
NHÀ THẦU THI CÔNG:  CÔNG TY TNHH VIỄN THÔNG SÁNG TẠO THUẬN PHONG (INNOTEL) 55/31 TRẦN ĐÌNH XU, P. CẦU KHO, Q. 1, HCM Tel: (84 28) 3 862 1119 Fax: (84 28) 3 863 0366	
CHỈ HUY TRƯỞNG:	
NGƯỜI KIỂM TRA:	
NGƯỜI LẬP:	
TÊN BẢN VẼ: RACK LAYOUT IDF-M.9F	
NGÀY HT:	01/09/2022
CHỈNH SỬA:	01
MÃ BẢN VẼ:	IDF-M.9F
HỒ SƠ THAM CHIẾU:	220726 ELV - CAP NHAT CCTV THEO Y KIEN MI GS&S

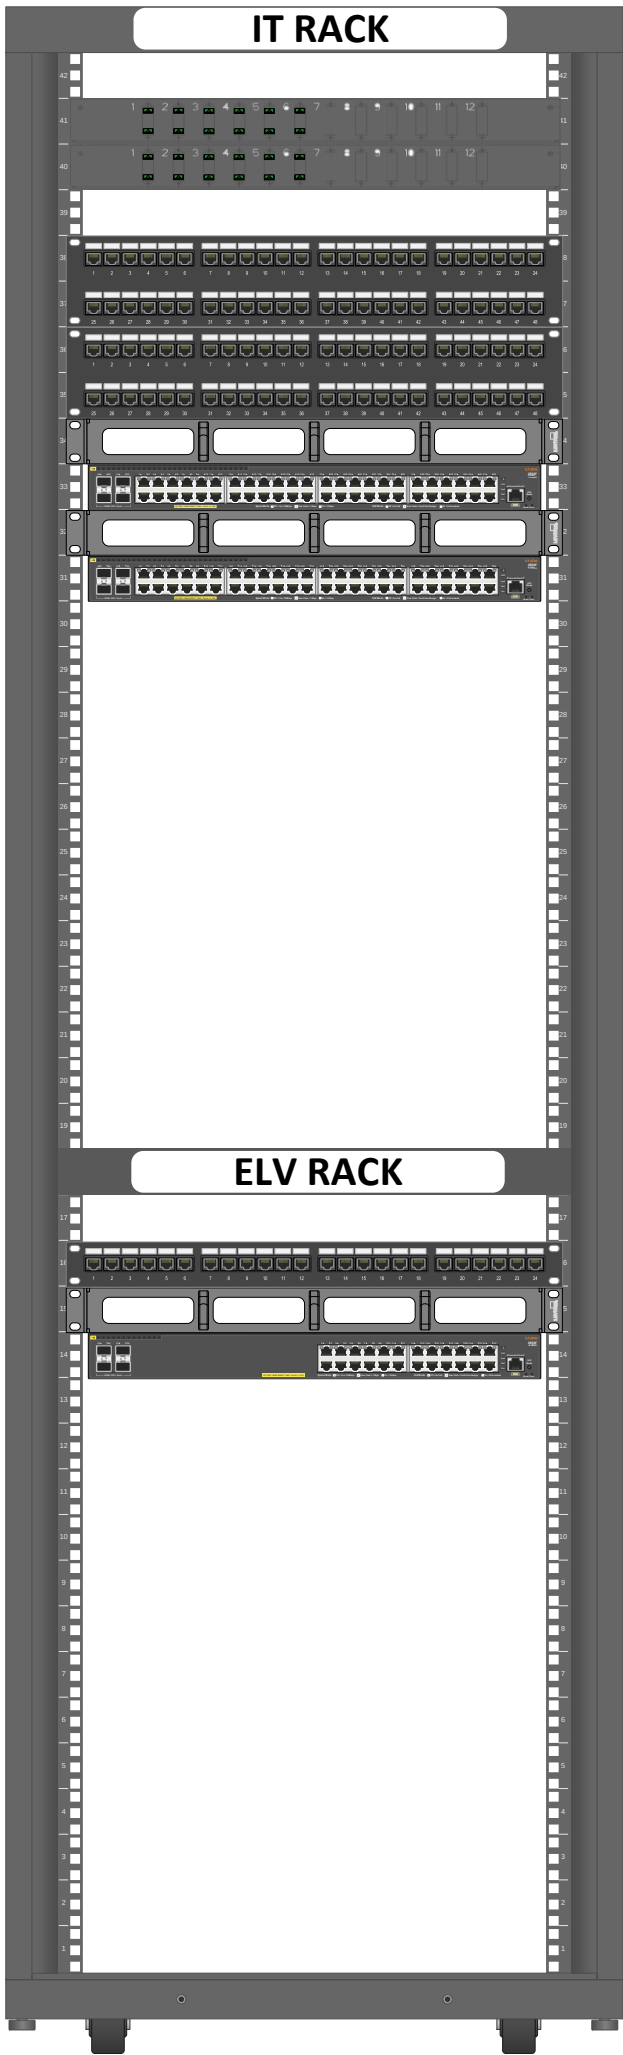


DỰ ÁN: TỔ HỢP KHÁCH SẠN, CĂN HỘ DỊCH VỤ MARRIOTT VÀ NHÀ Ở ĐỂ BÁN ĐỊA ĐIỂM XÂY DỰNG: 58 BẠCH ĐẰNG, P. HẢI CHÂU 1, Q. HẢI CHÂU, TP. ĐÀ NẴNG	
CHỦ ĐẦU TƯ: CÔNG TY CỔ PHẦN ĐỊA ỐC FOODINCO ĐỊA CHỈ: 58 BẠCH ĐẰNG, P. HẢI CHÂU 1, Q. HẢI CHÂU, TP. ĐÀ NẴNG	
BAN QUẢN LÝ DỰ ÁN:	
TƯ VẤN GIÁM SÁT: CN CÔNG TY TNHH APAVE CHÂU Á - THÁI BÌNH DƯƠNG TẠI ĐÀ NẴNG NGUYỄN ĐĂNG HÙNG	
ĐƠN VỊ NHÀ THẦU CHÍNH: CÔNG TY CỔ PHẦN ALPHANAM E&C	
NHÀ THẦU THI CÔNG:  CÔNG TY TNHH VIỄN THÔNG SÁNG TẠO THUẬN PHONG (INNOTEL) 55/31 TRẦN ĐÌNH XU, P. CẦU KHO, Q. 1, HCM Tel: (84 28) 3 862 1119 Fax: (84 28) 3 863 0366	
CHỈ HUY TRƯỞNG:	
NGUYỄN ĐỨC TIẾN	
NGƯỜI KIỂM TRA:	
NGƯỜI LẬP:	
TÊN BẢN VẼ: RACK LAYOUT IDF-M.11F	
NGÀY HT:	01/09/2022
CHỈNH SỬA:	01
MÃ BẢN VẼ:	IDF-M.11F
HỒ SƠ THAM CHIẾU:	220726 ELV - CAP NHAT CCTV THEO Y KIEN MI GS&S

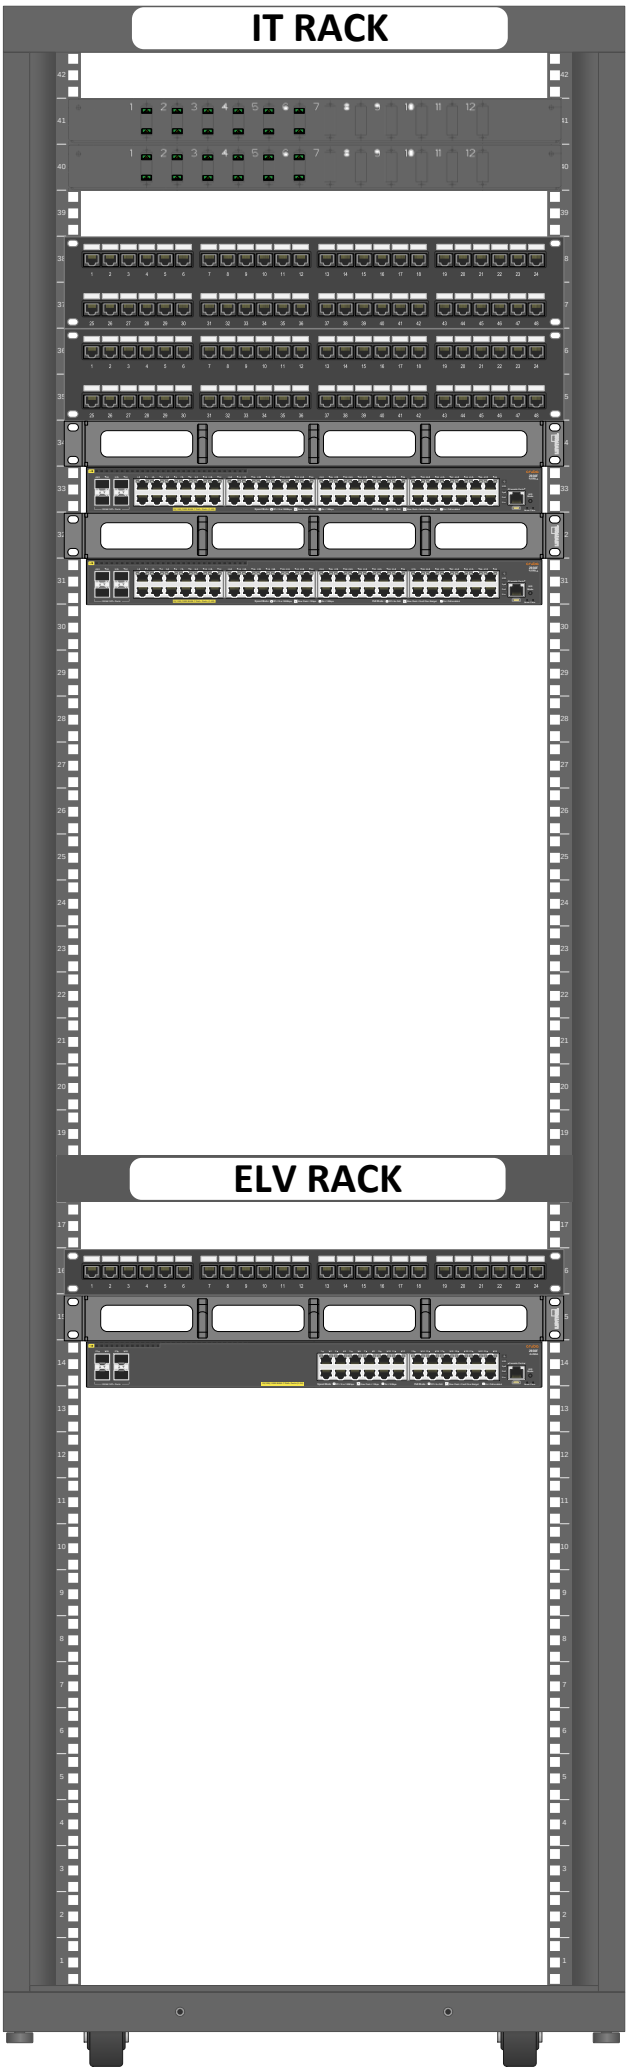


DỰ ÁN: TỔ HỢP KHÁCH SẠN, CĂN HỘ DỊCH VỤ MARRIOTT VÀ NHÀ Ở ĐỂ BÁN ĐỊA ĐIỂM XÂY DỰNG: 58 BẠCH ĐẰNG, P. HẢI CHÂU 1, Q. HẢI CHÂU, TP. ĐÀ NẴNG	
CHỦ ĐẦU TƯ: CÔNG TY CỔ PHẦN ĐỊA ỐC FOODINCO ĐỊA CHỈ: 58 BẠCH ĐẰNG, P. HẢI CHÂU 1, Q. HẢI CHÂU, TP. ĐÀ NẴNG	
BAN QUẢN LÝ DỰ ÁN:	
TƯ VẤN GIÁM SÁT: CN CÔNG TY TNHH APAVE CHÂU Á - THÁI BÌNH DƯƠNG TẠI ĐÀ NẴNG NGUYỄN ĐĂNG HÙNG	
ĐƠN VỊ NHÀ THẦU CHÍNH: CÔNG TY CỔ PHẦN ALPHANAM E&C	
NHÀ THẦU THI CÔNG:  CÔNG TY TNHH VIỄN THÔNG SÁNG TẠO THUẬN PHONG (INNOTEL) 55/31 TRẦN ĐÌNH XU, P. CẦU KHO, Q. 1, HCM Tel: (84 28) 3 862 1119 Fax: (84 28) 3 863 0366	
CHỈ HUY TRƯỞNG:	
NGUYỄN ĐỨC TIẾN	
NGƯỜI KIỂM TRA:	
NGƯỜI LẬP:	
TÊN BẢN VẼ: RACK LAYOUT IDF-M.13F	
NGÀY HT:	01/09/2022
CHỈNH SỬA:	01
MÃ BẢN VẼ:	IDF-M.13F
HỒ SƠ THAM CHIẾU:	220726 ELV - CAP NHAT CCTV THEO Y KIEN MI GS&S

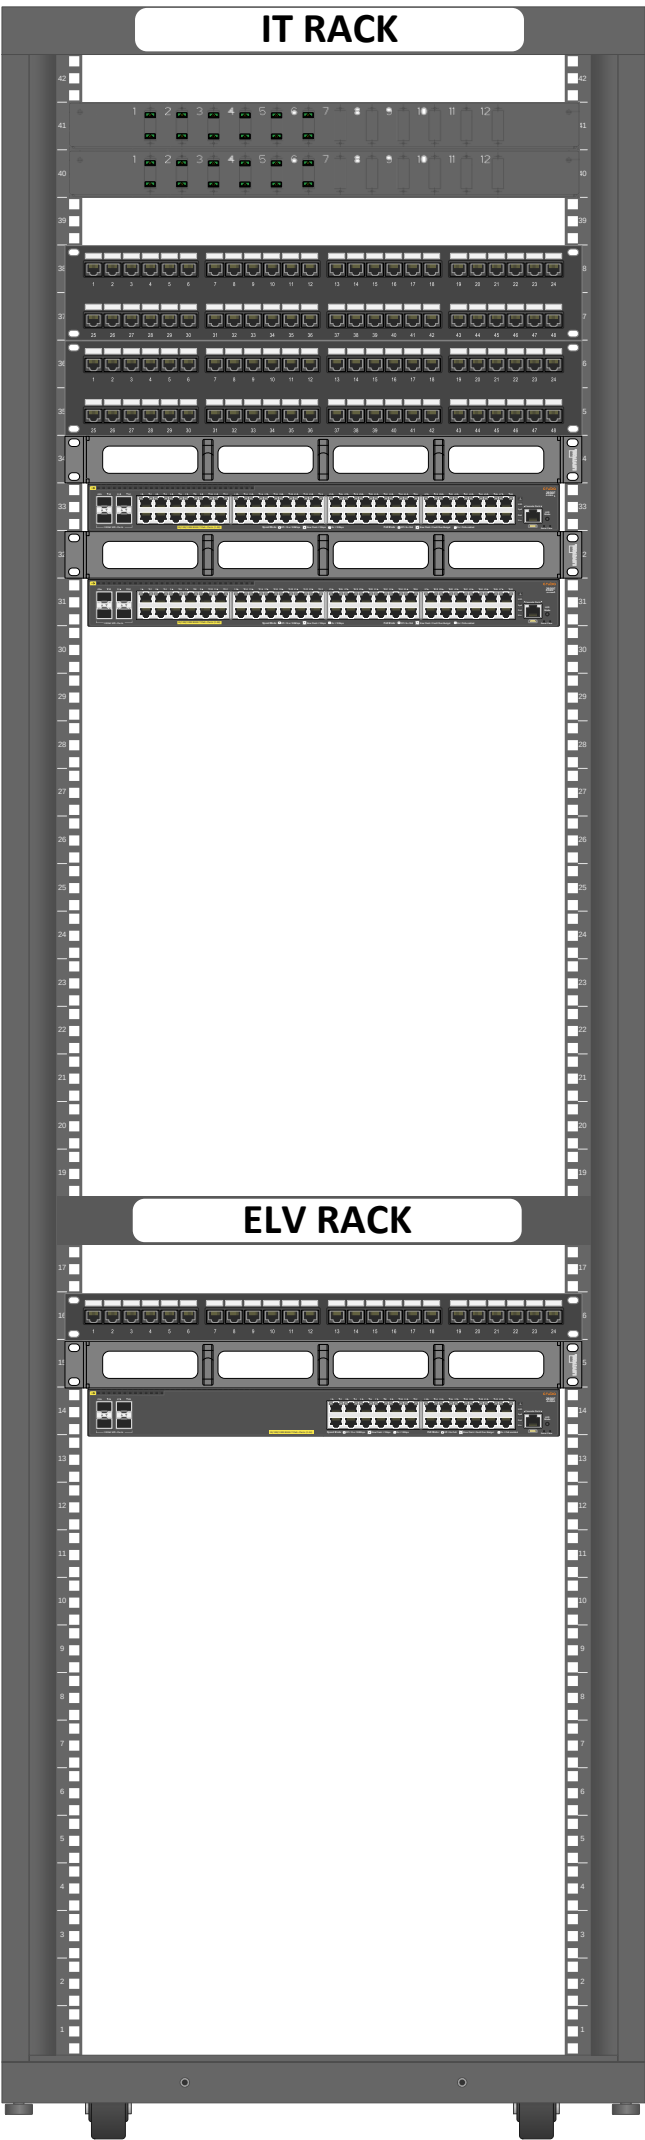


DỰ ÁN: TỔ HỢP KHÁCH SẠN, CĂN HỘ DỊCH VỤ MARRIOTT VÀ NHÀ Ở ĐỂ BÁN ĐỊA ĐIỂM XÂY DỰNG: 58 BẠCH ĐẰNG, P. HẢI CHÂU 1, Q. HẢI CHÂU, TP. ĐÀ NẴNG	
CHỦ ĐẦU TƯ: CÔNG TY CỔ PHẦN ĐỊA ỐC FOODINCO ĐỊA CHỈ: 58 BẠCH ĐẰNG, P. HẢI CHÂU 1, Q. HẢI CHÂU, TP. ĐÀ NẴNG	
BAN QUẢN LÝ DỰ ÁN:	
TƯ VẤN GIÁM SÁT: CN CÔNG TY TNHH APAVE CHÂU Á - THÁI BÌNH DƯƠNG TẠI ĐÀ NẴNG NGUYỄN ĐĂNG HÙNG	
ĐƠN VỊ NHÀ THẦU CHÍNH: CÔNG TY CỔ PHẦN ALPHANAM E&C	
NHÀ THẦU THI CÔNG:  CÔNG TY TNHH VIỄN THÔNG SÁNG TẠO THUẬN PHONG (INNOTEL) 55/31 TRẦN ĐÌNH XU, P. CẦU KHO, Q. 1, HCM Tel: (84 28) 3 862 1119 Fax: (84 28) 3 863 0366	
CHỈ HUY TRƯỞNG:	
NGUYỄN ĐỨC TIẾN	
NGƯỜI KIỂM TRA:	
NGƯỜI LẬP:	
TÊN BẢN VẼ: RACK LAYOUT IDF-M.15F	
NGÀY HT:	01/09/2022
CHỈNH SỬA:	01
MÃ BẢN VẼ:	IDF-M.15F
HỒ SƠ THAM CHIẾU:	220726 ELV - CAP NHAT CCTV THEO Y KIEN MI GS&S

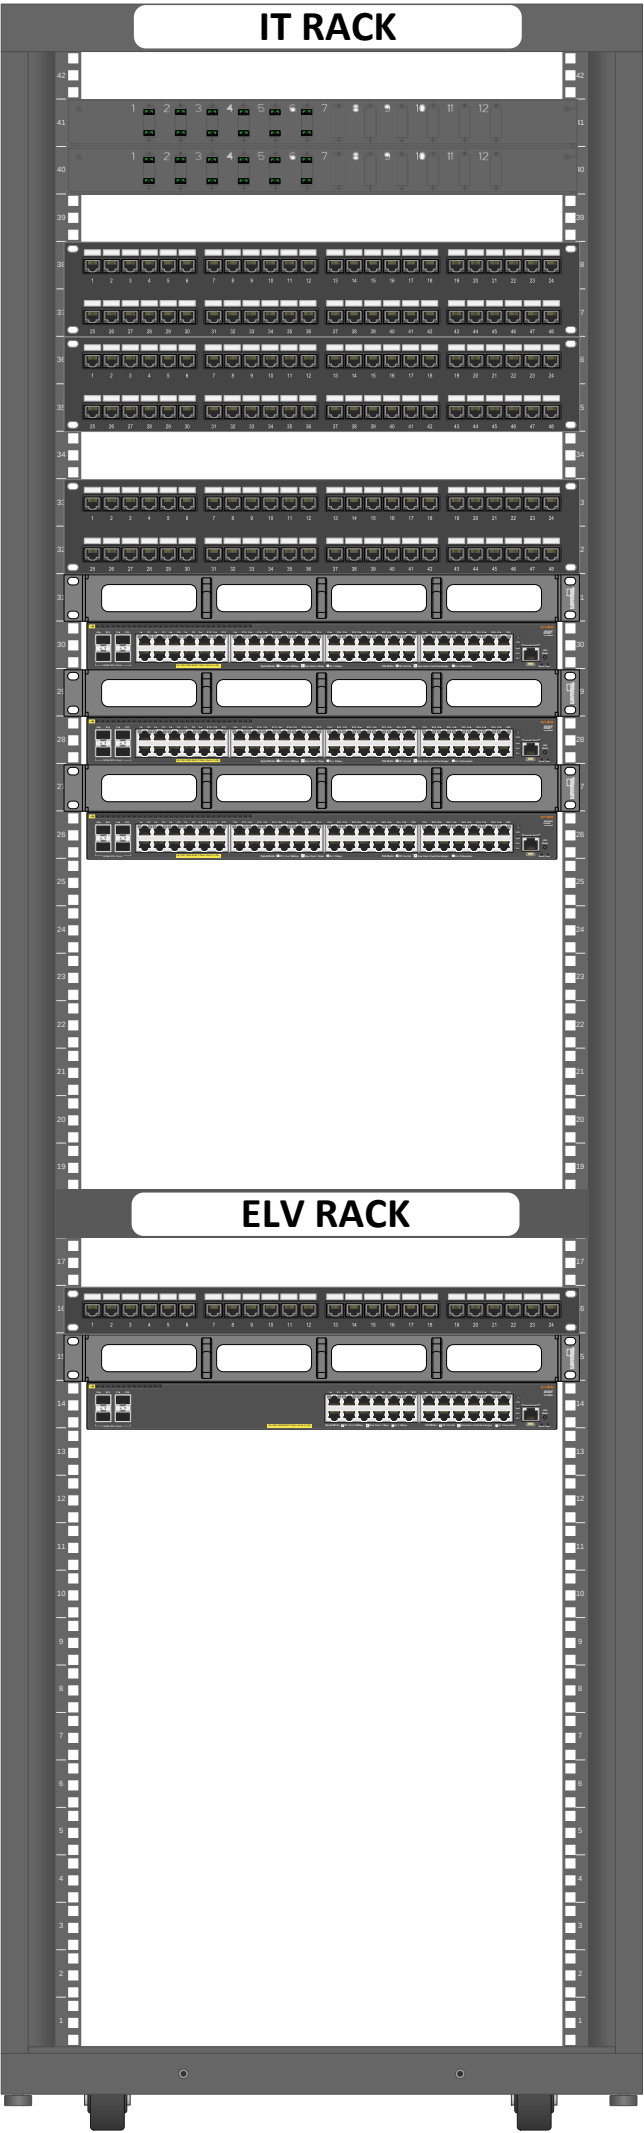


DỰ ÁN: TỔ HỢP KHÁCH SẠN, CĂN HỘ DỊCH VỤ MARRIOTT VÀ NHÀ Ở ĐỂ BÁN ĐỊA ĐIỂM XÂY DỰNG: 58 BẠCH ĐẰNG, P. HẢI CHÂU 1, Q. HẢI CHÂU, TP. ĐÀ NẴNG	
CHỦ ĐẦU TƯ: CÔNG TY CỔ PHẦN ĐỊA ỐC FOODINCO ĐỊA CHỈ: 58 BẠCH ĐẰNG, P. HẢI CHÂU 1, Q. HẢI CHÂU, TP. ĐÀ NẴNG	
BAN QUẢN LÝ DỰ ÁN:	
TƯ VẤN GIÁM SÁT: CN CÔNG TY TNHH APAVE CHÂU Á - THÁI BÌNH DƯƠNG TẠI ĐÀ NẴNG NGUYỄN ĐĂNG HÙNG	
ĐƠN VỊ NHÀ THẦU CHÍNH: CÔNG TY CỔ PHẦN ALPHANAM E&C	
NHÀ THẦU THI CÔNG:  CÔNG TY TNHH VIỄN THÔNG SÁNG TẠO THUẬN PHONG (INNOTEL) 55/31 TRẦN ĐÌNH XU, P. CẦU KHO, Q. 1, HCM Tel: (84 28) 3 862 1119 Fax: (84 28) 3 863 0366	
CHỈ HUY TRƯỞNG:	
NGƯỜI KIỂM TRA:	
NGƯỜI LẬP:	
TÊN BẢN VẼ: RACK LAYOUT IDF-M.18F	
NGÀY HT:	01/09/2022
CHỈNH SỬA:	01
MÃ BẢN VẼ:	IDF-M.18F
HỒ SƠ THAM CHIẾU:	220726 ELV - CAP NHAT CCTV THEO Y KIEN MI GS&S

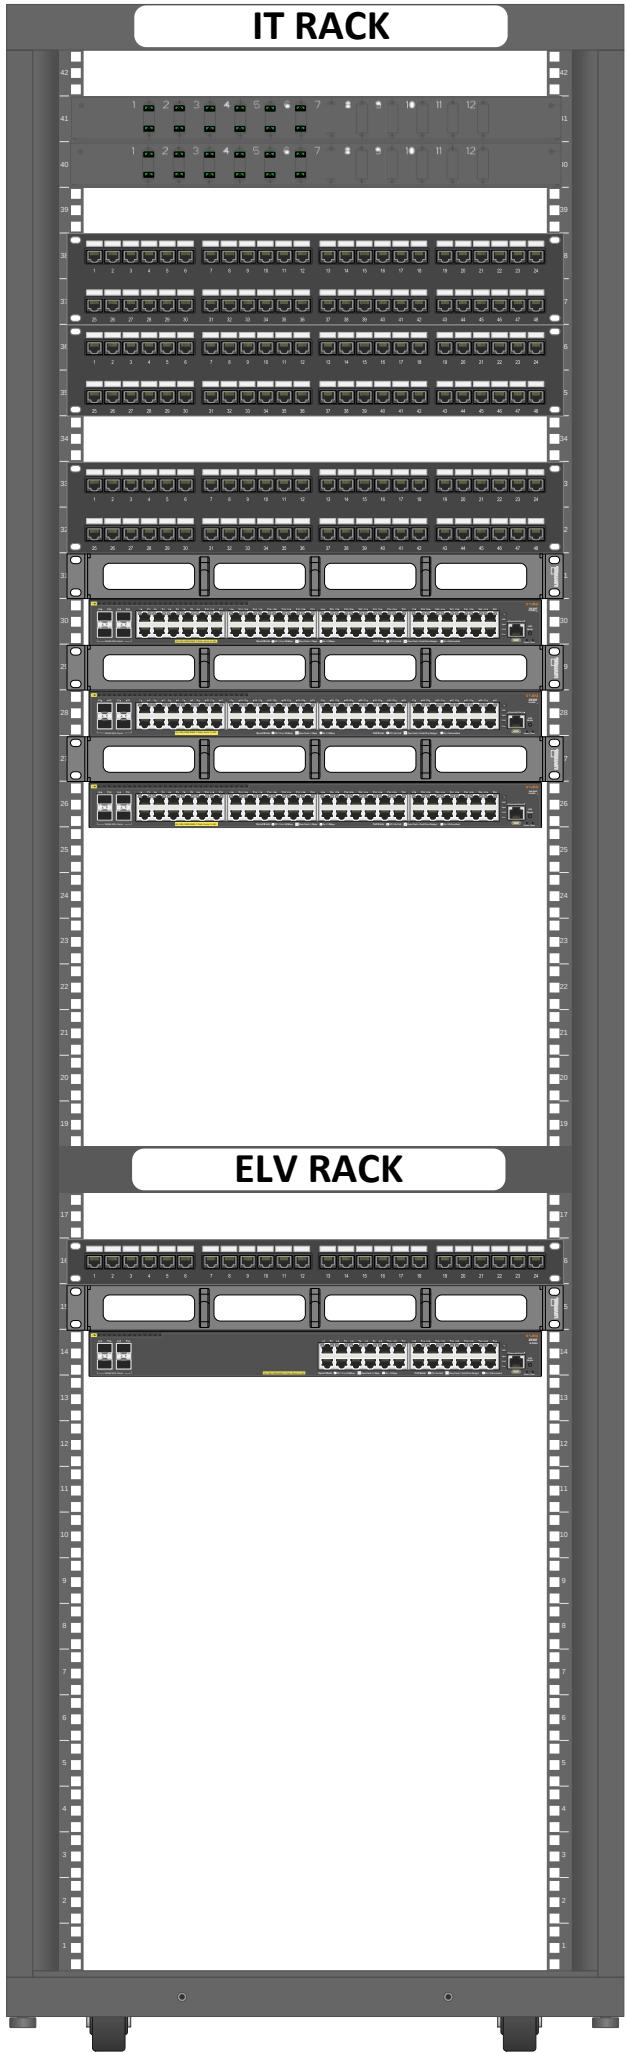


DỰ ÁN: TỔ HỢP KHÁCH SẠN, CĂN HỘ DỊCH VỤ MARRIOTT VÀ NHÀ Ở ĐỂ BÁN ĐỊA ĐIỂM XÂY DỰNG: 58 BẠCH ĐẰNG, P. HẢI CHÂU 1, Q. HẢI CHÂU, TP. ĐÀ NẴNG	
CHỦ ĐẦU TƯ: CÔNG TY CỔ PHẦN ĐỊA ỐC FOODINCO ĐỊA CHỈ: 58 BẠCH ĐẰNG, P. HẢI CHÂU 1, Q. HẢI CHÂU, TP. ĐÀ NẴNG	
BAN QUẢN LÝ DỰ ÁN:	
TƯ VẤN GIÁM SÁT: CN CÔNG TY TNHH APAVE CHÂU Á - THÁI BÌNH DƯƠNG TẠI ĐÀ NẴNG NGUYỄN ĐĂNG HÙNG	
ĐƠN VỊ NHÀ THẦU CHÍNH: CÔNG TY CỔ PHẦN ALPHANAM E&C	
NHÀ THẦU THI CÔNG:  CÔNG TY TNHH VIỄN THÔNG SÁNG TẠO THUẬN PHONG (INNOTEL) 55/31 TRẦN ĐÌNH XU, P. CẦU KHO, Q. 1, HCM Tel: (84 28) 3 862 1119 Fax: (84 28) 3 863 0366	
CHỈ HUY TRƯỞNG:	
NGUYỄN ĐỨC TIẾN	
NGƯỜI KIỂM TRA:	
NGƯỜI LẬP:	
TÊN BẢN VẼ: RACK LAYOUT IDF-M.21F	
NGÀY HT:	01/09/2022
CHỈNH SỬA:	01
MÃ BẢN VẼ:	IDF-M.21F
HỒ SƠ THAM CHIẾU:	220726 ELV - CAP NHAT CCTV THEO Y KIEN MI GS&S

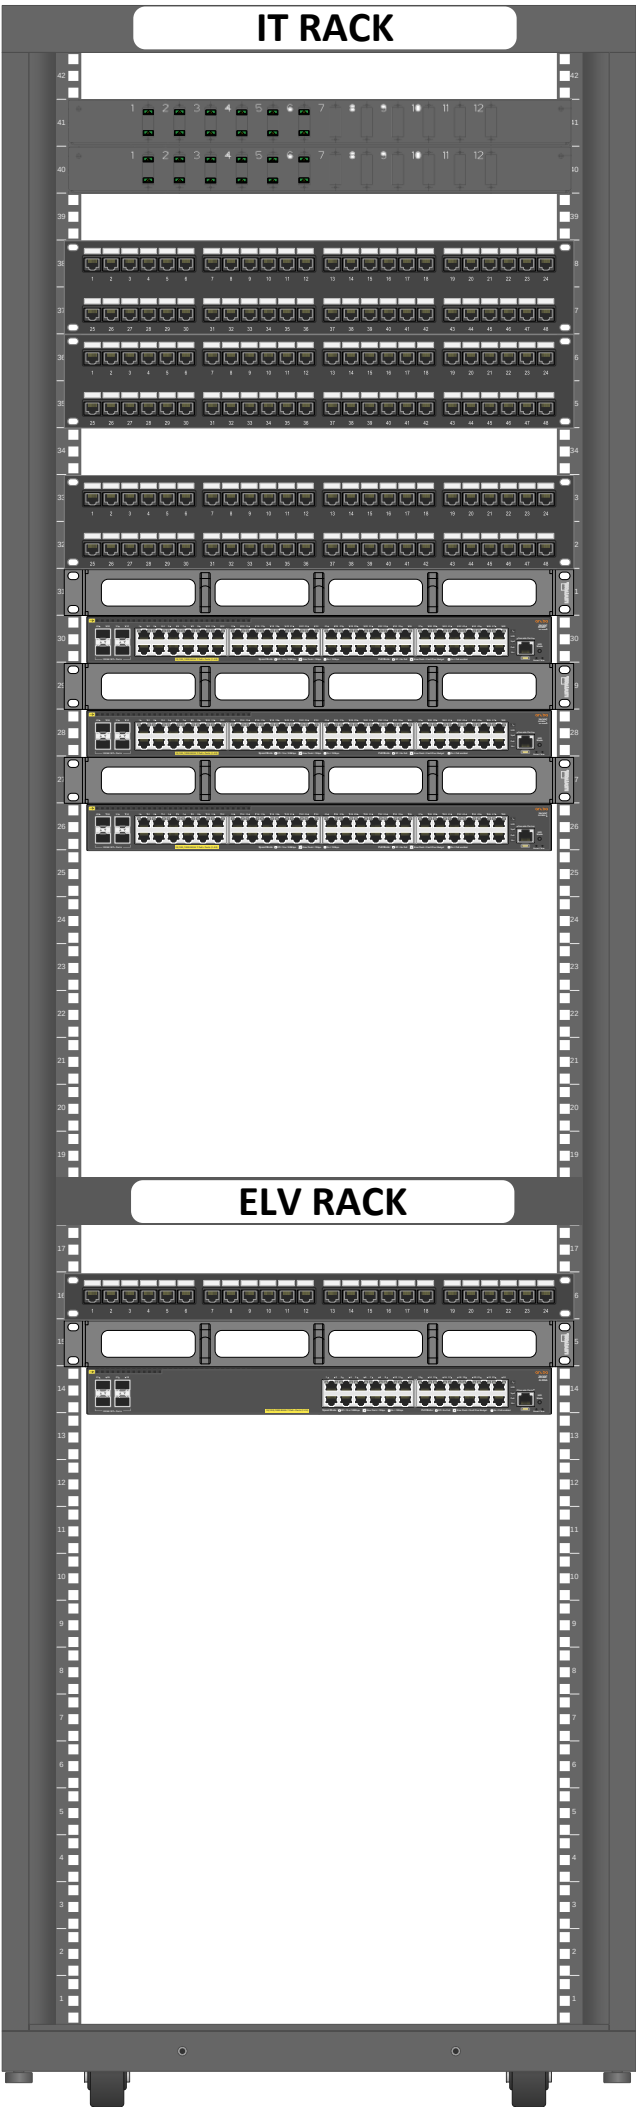


DỰ ÁN: TỔ HỢP KHÁCH SẠN, CĂN HỘ DỊCH VỤ MARRIOTT VÀ NHÀ Ở ĐỂ BÁN ĐỊA ĐIỂM XÂY DỰNG: 58 BẠCH ĐẰNG, P. HẢI CHÂU 1, Q. HẢI CHÂU, TP. ĐÀ NẴNG	
CHỦ ĐẦU TƯ: CÔNG TY CỔ PHẦN ĐỊA ỐC FOODINCO ĐỊA CHỈ: 58 BẠCH ĐẰNG, P. HẢI CHÂU 1, Q. HẢI CHÂU, TP. ĐÀ NẴNG	
BAN QUẢN LÝ DỰ ÁN:	
TƯ VẤN GIÁM SÁT: CN CÔNG TY TNHH APAVE CHÂU Á - THÁI BÌNH DƯƠNG TẠI ĐÀ NẴNG NGUYỄN ĐĂNG HÙNG	
ĐƠN VỊ NHÀ THẦU CHÍNH: CÔNG TY CỔ PHẦN ALPHANAM E&C	
NHÀ THẦU THI CÔNG:  CÔNG TY TNHH VIỄN THÔNG SÁNG TẠO THUẬN PHONG (INNOTEL) 55/31 TRẦN ĐÌNH XU, P. CẦU KHO, Q. 1, HCM Tel: (84 28) 3 862 1119 Fax: (84 28) 3 863 0366	
CHỈ HUY TRƯỞNG:	
NGUYỄN ĐỨC TIẾN	
NGƯỜI KIỂM TRA:	
NGƯỜI LẬP:	
TÊN BẢN VẼ: RACK LAYOUT IDF-M.23F	
NGÀY HT:	01/09/2022
CHỈNH SỬA:	01
MÃ BẢN VẼ:	IDF-M.23F
HỒ SƠ THAM CHIẾU:	220726 ELV - CAP NHAT CCTV THEO Y KIEN MI GS&S

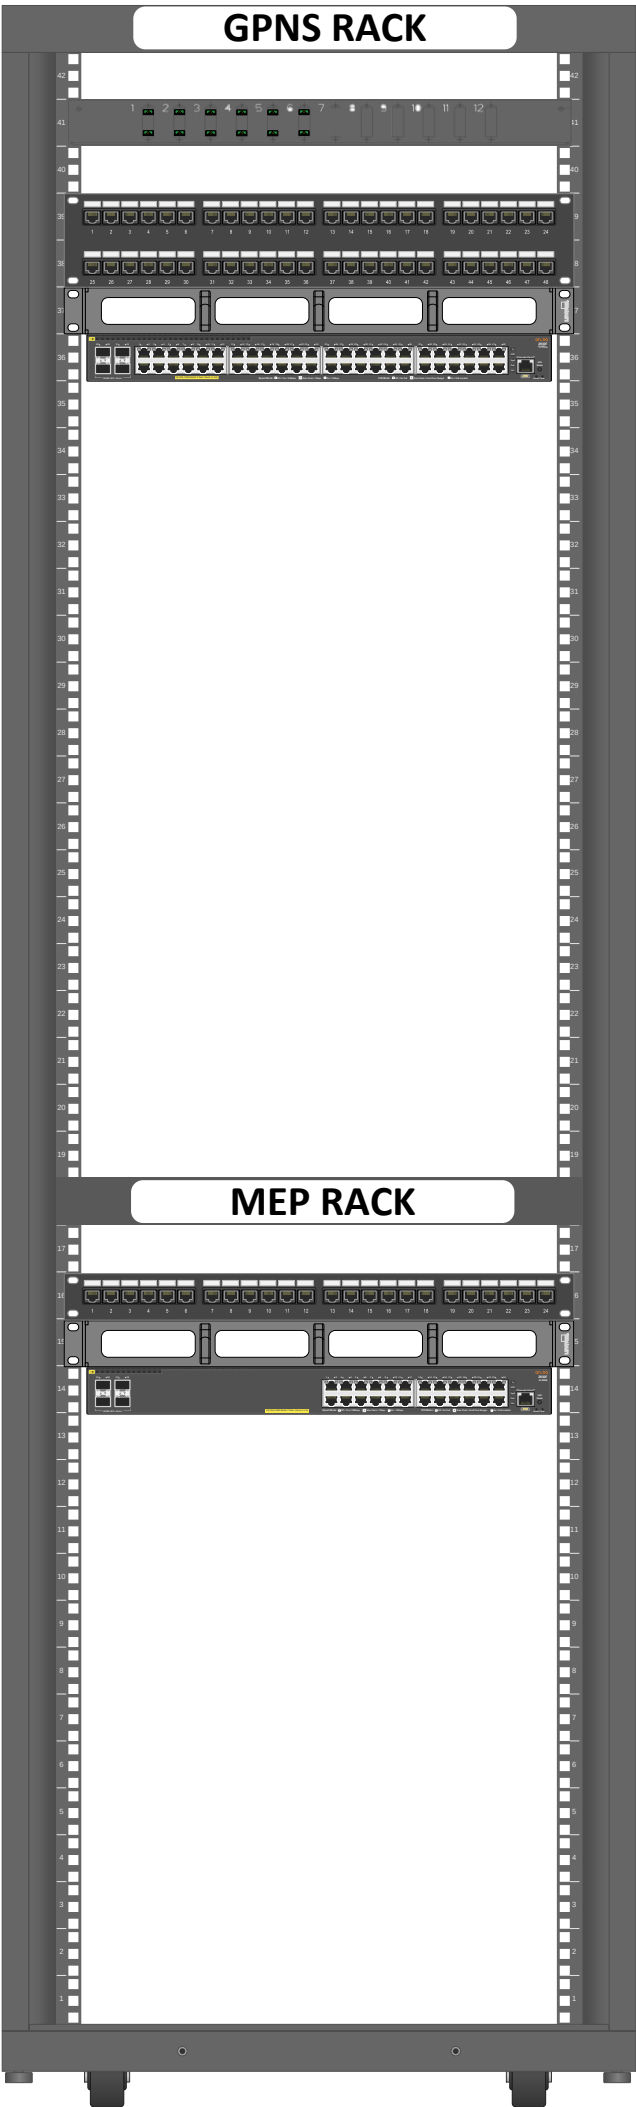


Dự Án: TỔ HỢP KHÁCH SẠN, CĂN HỘ DỊCH VỤ MARRIOTT VÀ NHÀ Ở ĐỂ BÁN Địa điểm xây dựng: 58 Bạch Đằng, P. Hải Châu 1, Q. Hải Châu, TP. Đà Nẵng	
Chủ đầu tư: CÔNG TY CỔ PHẦN ĐỊA ỐC FOODINCO Địa chỉ: 58 Bạch Đằng, P. Hải Châu 1, Q. Hải Châu, TP. Đà Nẵng	
Ban quản lý dự án:	
Tư vấn giám sát: CN CÔNG TY TNHH APAVE CHÂU Á - THÁI BÌNH DƯƠNG TẠI ĐÀ NẴNG NGUYỄN ĐĂNG HÙNG	
Đơn vị nhà thầu chính: CÔNG TY CỔ PHẦN ALPHANAM E&C	
Nhà thầu thi công: innotel maximizing your access CÔNG TY TNHH VIỄN THÔNG SÁNG TẠO THUẬN PHONG (INNOTEL) 55/31 TRẦN ĐÌNH XU, P. CẦU KHO, Q. 1, HCM Tel: (84 28) 3 862 1119 Fax: (84 28) 3 863 0366	
Chỉ huy trưởng:	
NGUYỄN ĐỨC TIẾN	
Người kiểm tra:	
Người lập:	
Tên bản vẽ: RACK LAYOUT IDF-A.24AF (MLM)	
Ngày HT:	01/09/2022
Chỉnh sửa:	01
Mã bản vẽ:	IDF-A.24AF
Hồ sơ tham chiếu:	220726 ELV - CAP NHAT CCTV THEO Y KIẾN MI GS&S

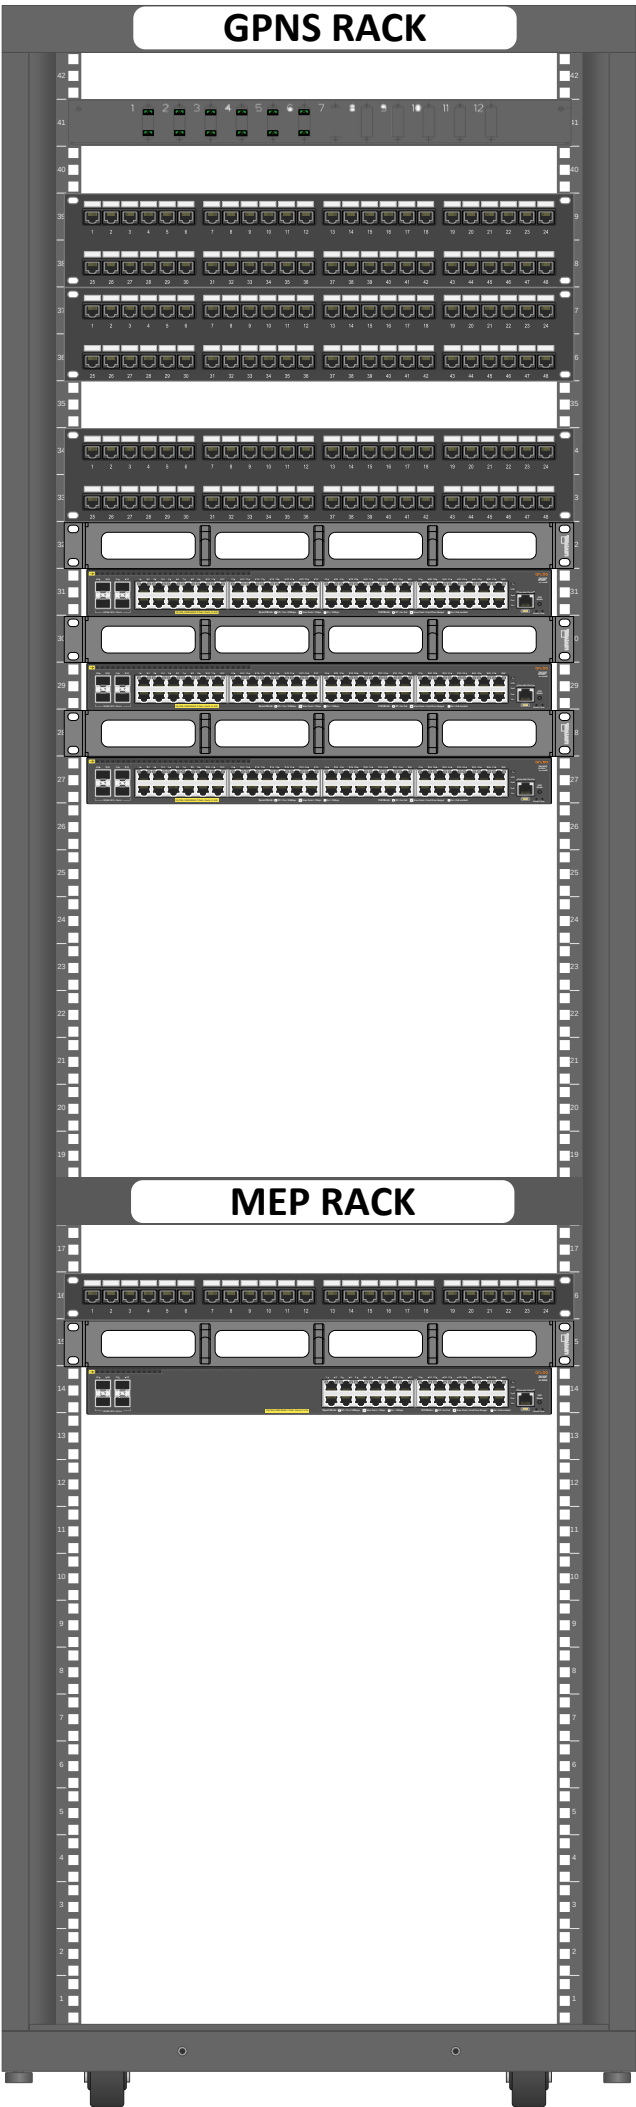


DỰ ÁN: TỔ HỢP KHÁCH SẠN, CĂN HỘ DỊCH VỤ MARRIOTT VÀ NHÀ Ở ĐỂ BÁN ĐỊA ĐIỂM XÂY DỰNG: 58 BẠCH ĐẰNG, P. HẢI CHÂU 1, Q. HẢI CHÂU, TP. ĐÀ NẴNG	
CHỦ ĐẦU TƯ: CÔNG TY CỔ PHẦN ĐỊA ỐC FOODINCO ĐỊA CHỈ: 58 BẠCH ĐẰNG, P. HẢI CHÂU 1, Q. HẢI CHÂU, TP. ĐÀ NẴNG	
BAN QUẢN LÝ DỰ ÁN:	
TƯ VẤN GIÁM SÁT: CN CÔNG TY TNHH APAVE CHÂU Á - THÁI BÌNH DƯƠNG TẠI ĐÀ NẴNG NGUYỄN ĐĂNG HÙNG	
ĐƠN VỊ NHÀ THẦU CHÍNH: CÔNG TY CỔ PHẦN ALPHANAM E&C	
NHÀ THẦU THI CÔNG:  CÔNG TY TNHH VIỄN THÔNG SÁNG TẠO THUẬN PHONG (INNOTEL) 55/31 TRẦN ĐÌNH XU, P. CẦU KHO, Q. 1, HCM Tel: (84 28) 3 862 1119 Fax: (84 28) 3 863 0366	
CHỈ HUY TRƯỞNG:	
NGUYỄN ĐỨC TIẾN	
NGƯỜI KIỂM TRA:	
NGƯỜI LẬP:	
TÊN BẢN VẼ: RACK LAYOUT IDF-A.26F (MLM)	
NGÀY HT:	01/09/2022
CHỈNH SỬA:	01
MÃ BẢN VẼ:	IDF-A.26F
HỒ SƠ THAM CHIẾU:	220726 ELV - CAP NHAT CCTV THEO Y KIEN MI GS&S

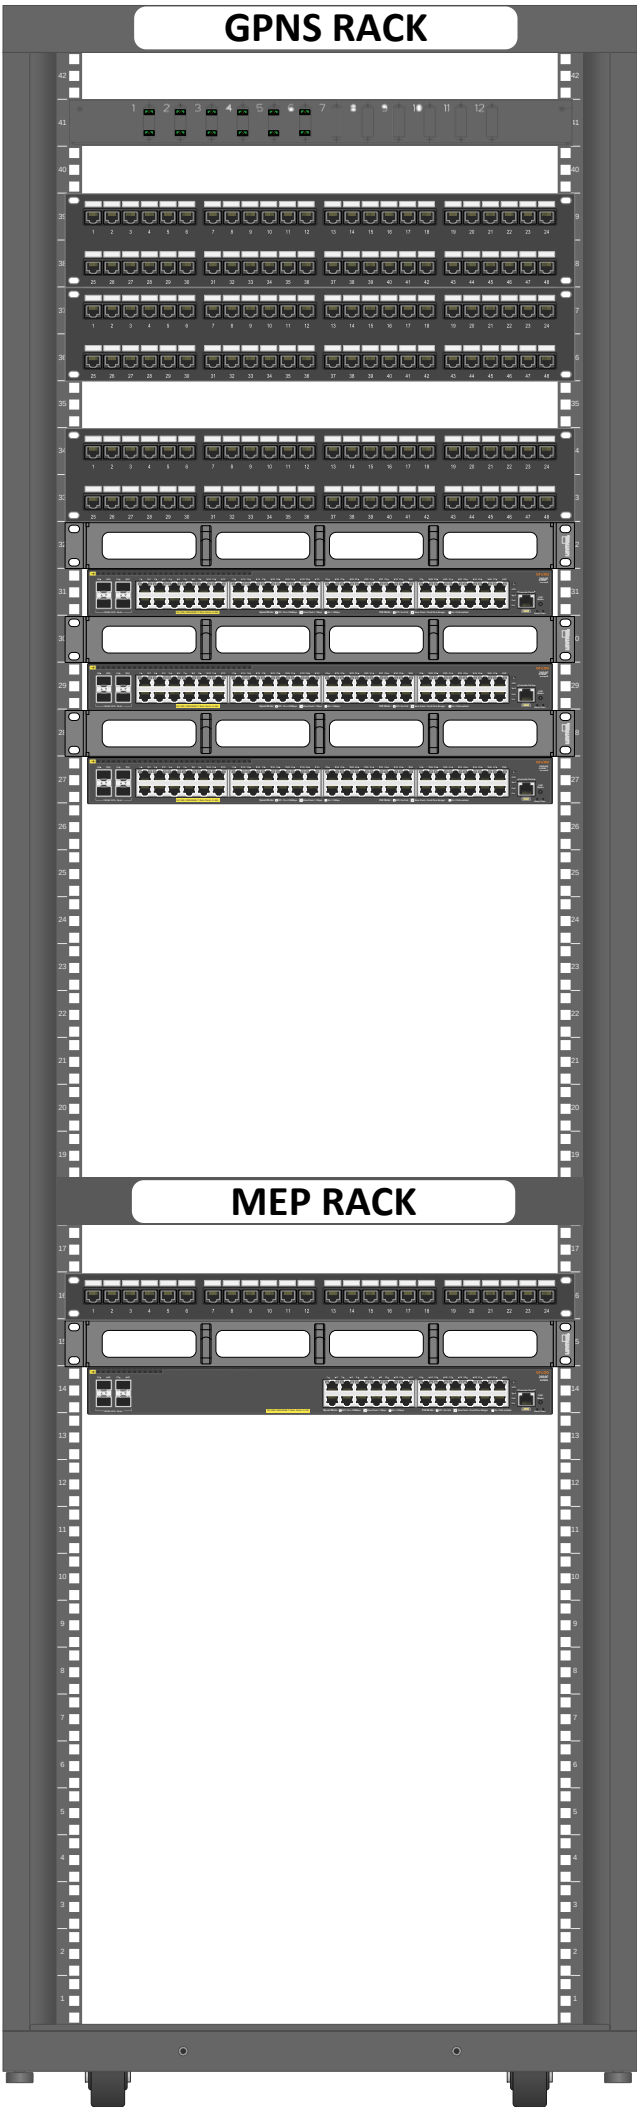


DỰ ÁN: TỔ HỢP KHÁCH SẠN, CĂN HỘ DỊCH VỤ MARRIOTT VÀ NHÀ Ở ĐỂ BÁN ĐỊA ĐIỂM XÂY DỰNG: 58 BẠCH ĐẰNG, P. HẢI CHÂU 1, Q. HẢI CHÂU, TP. ĐÀ NẴNG	
CHỦ ĐẦU TƯ: CÔNG TY CỔ PHẦN ĐỊA ỐC FOODINCO ĐỊA CHỈ: 58 BẠCH ĐẰNG, P. HẢI CHÂU 1, Q. HẢI CHÂU, TP. ĐÀ NẴNG	
BAN QUẢN LÝ DỰ ÁN:	
TƯ VẤN GIÁM SÁT: CN CÔNG TY TNHH APAVE CHÂU Á - THÁI BÌNH DƯƠNG TẠI ĐÀ NẴNG NGUYỄN ĐĂNG HÙNG	
ĐƠN VỊ NHÀ THẦU CHÍNH: CÔNG TY CỔ PHẦN ALPHANAM E&C	
NHÀ THẦU THI CÔNG:  CÔNG TY TNHH VIỄN THÔNG SÁNG TẠO THUẬN PHONG (INNOTEL) 55/31 TRẦN ĐÌNH XU, P. CẦU KHO, Q. 1, HCM Tel: (84 28) 3 862 1119 Fax: (84 28) 3 863 0366	
CHỈ HUY TRƯỞNG:	
NGUYỄN ĐỨC TIẾN	
NGƯỜI KIỂM TRA:	
NGƯỜI LẬP:	
TÊN BẢN VẼ: RACK LAYOUT IDF-A.29F (MLM)	
NGÀY HT:	01/09/2022
CHỈNH SỬA:	01
MÃ BẢN VẼ:	IDF-A.29F
HỒ SƠ THAM CHIẾU:	220726 ELV - CAP NHAT CCTV THEO Y KIEN MI GS&S

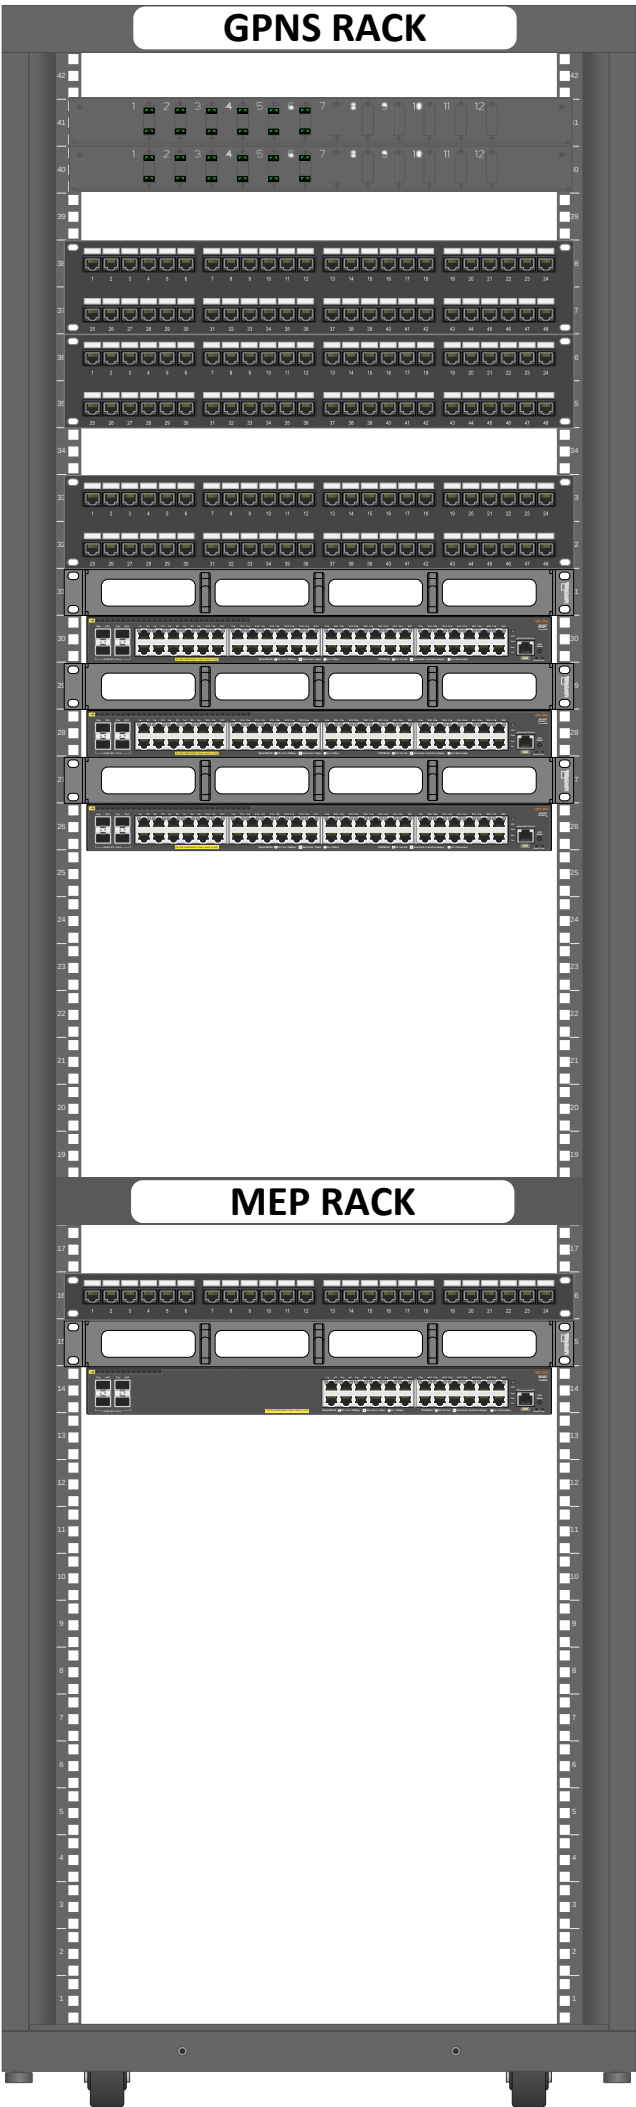


DỰ ÁN: TỔ HỢP KHÁCH SẠN, CĂN HỘ DỊCH VỤ MARRIOTT VÀ NHÀ Ở ĐỂ BÁN ĐỊA ĐIỂM XÂY DỰNG: 58 BẠCH ĐẰNG, P. HẢI CHÂU 1, Q. HẢI CHÂU, TP. ĐÀ NẴNG	
CHỦ ĐẦU TƯ: CÔNG TY CỔ PHẦN ĐỊA ỐC FOODINCO ĐỊA CHỈ: 58 BẠCH ĐẰNG, P. HẢI CHÂU 1, Q. HẢI CHÂU, TP. ĐÀ NẴNG	
BAN QUẢN LÝ DỰ ÁN:	
TƯ VẤN GIÁM SÁT: CN CÔNG TY TNHH APAVE CHÂU Á - THÁI BÌNH DƯƠNG TẠI ĐÀ NẴNG NGUYỄN ĐĂNG HÙNG	
ĐƠN VỊ NHÀ THẦU CHÍNH: CÔNG TY CỔ PHẦN ALPHANAM E&C	
NHÀ THẦU THI CÔNG:  CÔNG TY TNHH VIỄN THÔNG SÁNG TẠO THUẬN PHONG (INNOTEL) 55/31 TRẦN ĐÌNH XU, P. CẦU KHO, Q. 1, HCM Tel: (84 28) 3 862 1119 Fax: (84 28) 3 863 0366	
CHỈ HUY TRƯỞNG:	
NGUYỄN ĐỨC TIẾN	
NGƯỜI KIỂM TRA:	
NGƯỜI LẬP:	
TÊN BẢN VẼ: RACK LAYOUT IDF-A.32F (MLM)	
NGÀY HT:	01/09/2022
CHỈNH SỬA:	01
MÃ BẢN VẼ:	IDF-A.32F
HỒ SƠ THAM CHIẾU:	220726 ELV - CAP NHAT CCTV THEO Y KIEN MI GS&S

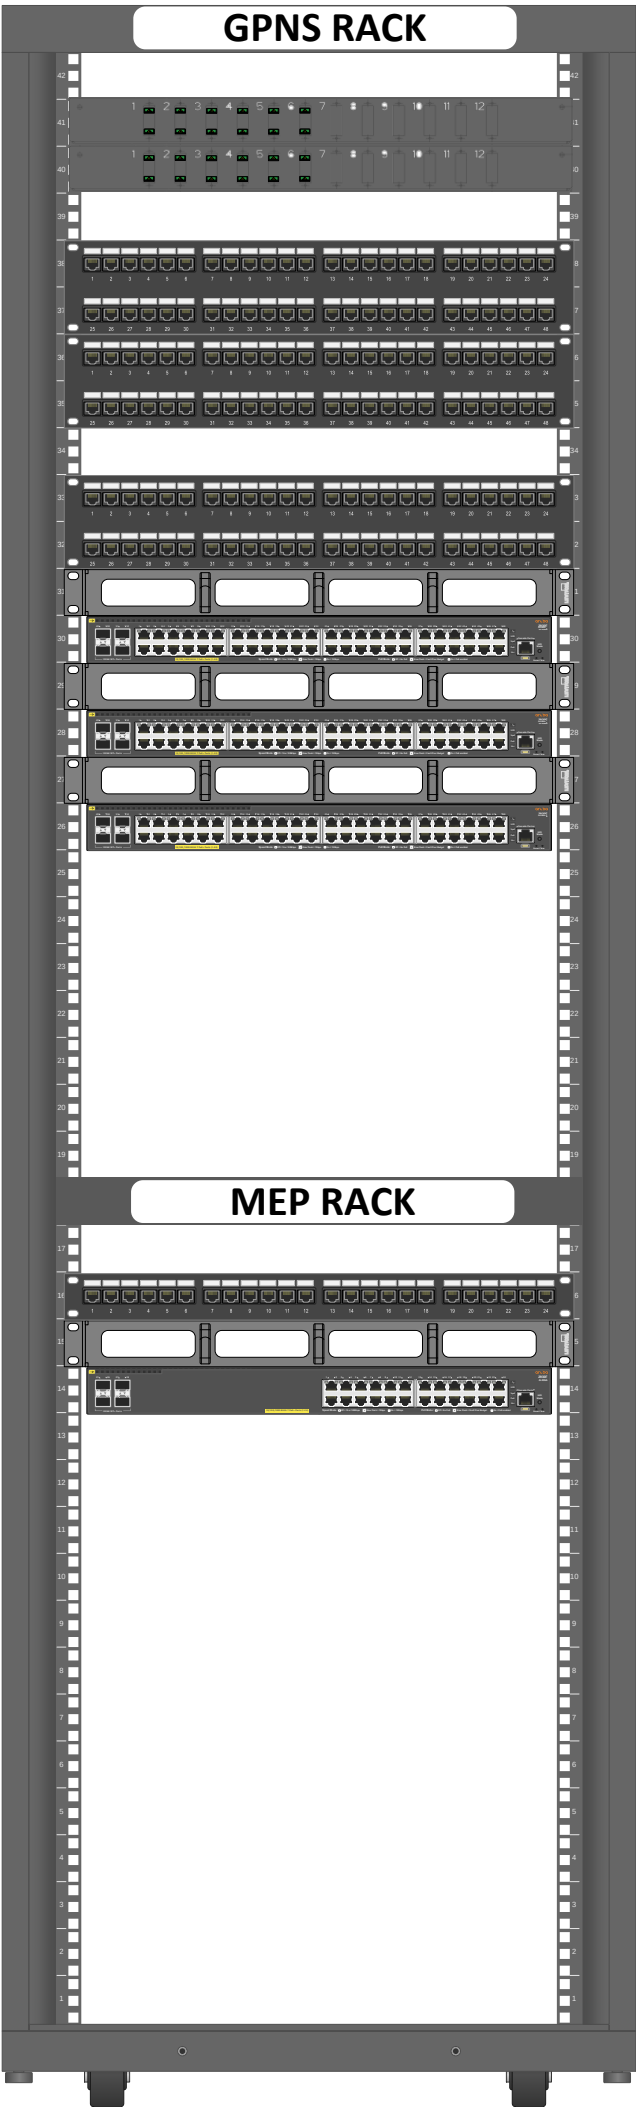


DỰ ÁN: TỔ HỢP KHÁCH SẠN, CĂN HỘ DỊCH VỤ MARRIOTT VÀ NHÀ Ở ĐỂ BÁN ĐỊA ĐIỂM XÂY DỰNG: 58 BẠCH ĐẰNG, P. HẢI CHÂU 1, Q. HẢI CHÂU, TP. ĐÀ NẴNG	
CHỦ ĐẦU TƯ: CÔNG TY CỔ PHẦN ĐỊA ỐC FOODINCO ĐỊA CHỈ: 58 BẠCH ĐẰNG, P. HẢI CHÂU 1, Q. HẢI CHÂU, TP. ĐÀ NẴNG	
BAN QUẢN LÝ DỰ ÁN:	
TƯ VẤN GIÁM SÁT: CN CÔNG TY TNHH APAVE CHÂU Á - THÁI BÌNH DƯƠNG TẠI ĐÀ NẴNG NGUYỄN ĐĂNG HÙNG	
ĐƠN VỊ NHÀ THẦU CHÍNH: CÔNG TY CỔ PHẦN ALPHANAM E&C	
NHÀ THẦU THI CÔNG:  CÔNG TY TNHH VIỄN THÔNG SÁNG TẠO THUẬN PHONG (INNOTEL) 55/31 TRẦN ĐÌNH XU, P. CẦU KHO, Q. 1, HCM Tel: (84 28) 3 862 1119 Fax: (84 28) 3 863 0366	
CHỈ HUY TRƯỞNG:	
NGUYỄN ĐỨC TIẾN	
NGƯỜI KIỂM TRA:	
NGƯỜI LẬP:	
TÊN BẢN VẼ: RACK LAYOUT IDF-A.35F (MLM)	
NGÀY HT:	01/09/2022
CHỈNH SỬA:	01
MÃ BẢN VẼ:	IDF-A.35F
HỒ SƠ THAM CHIẾU:	220726 ELV - CAP NHAT CCTV THEO Y KIEN MI GS&S

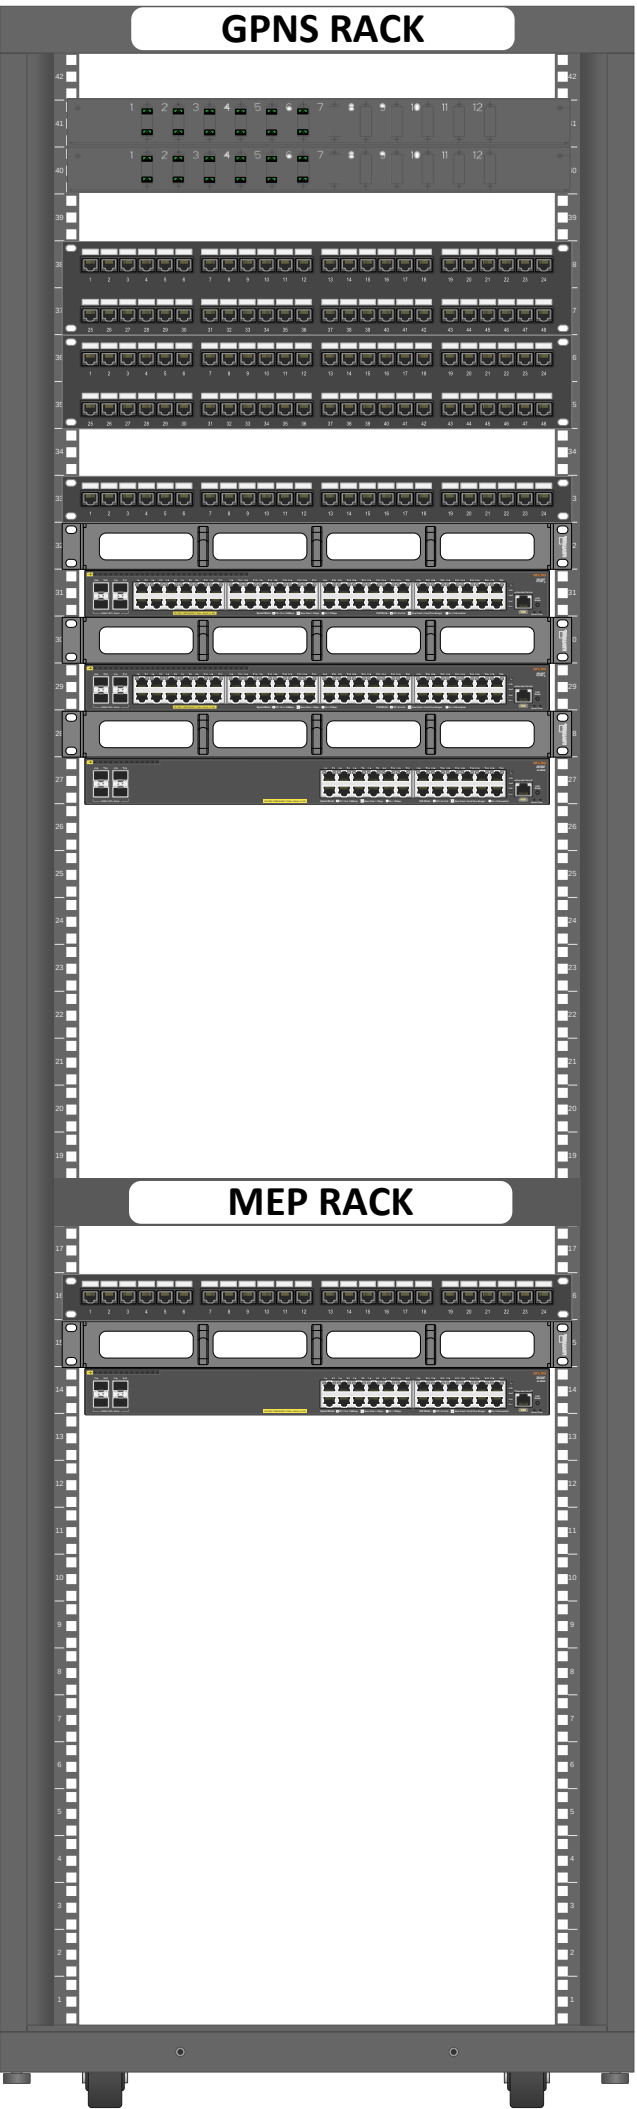

Dự án: TỔ HỢP KHÁCH SẠN, CĂN HỘ DỊCH VỤ MARRIOTT VÀ NHÀ Ở ĐỂ BÁN Địa điểm xây dựng: 58 Bạch Đằng, P. Hải Châu 1, Q. Hải Châu, TP. Đà Nẵng	
Chủ đầu tư: CÔNG TY CỔ PHẦN ĐỊA ỐC FOODINCO Địa chỉ: 58 Bạch Đằng, P. Hải Châu 1, Q. Hải Châu, TP. Đà Nẵng	
Ban quản lý dự án:	
Tư vấn giám sát: CN CÔNG TY TNHH APAVE CHÂU Á - THÁI BÌNH DƯƠNG TẠI ĐÀ NẴNG NGUYỄN ĐĂNG HÙNG	
Đơn vị nhà thầu chính: CÔNG TY CỔ PHẦN ALPHANAM E&C	
Nhà thầu thi công:  maximizing your access CÔNG TY TNHH VIỄN THÔNG SÁNG TẠO THUẬN PHONG (INNOTEL) 55/31 TRẦN ĐÌNH XU, P. CẦU KHO, Q. 1, HCM Tel: (84 28) 3 862 1119 Fax: (84 28) 3 863 0366	
Chỉ huy trưởng:	
NGUYỄN ĐỨC TIẾN	
Người kiểm tra:	
Người lập:	
Tên bản vẽ: RACK LAYOUT IDF-A.38F (MLM)	
Ngày HT:	01/09/2022
Chỉnh sửa:	01
Mã bản vẽ:	IDF-A.38F
Hồ sơ tham chiếu:	220726 ELV - CAP NHAT CCTV THEO Y KIẾN MI GS&S

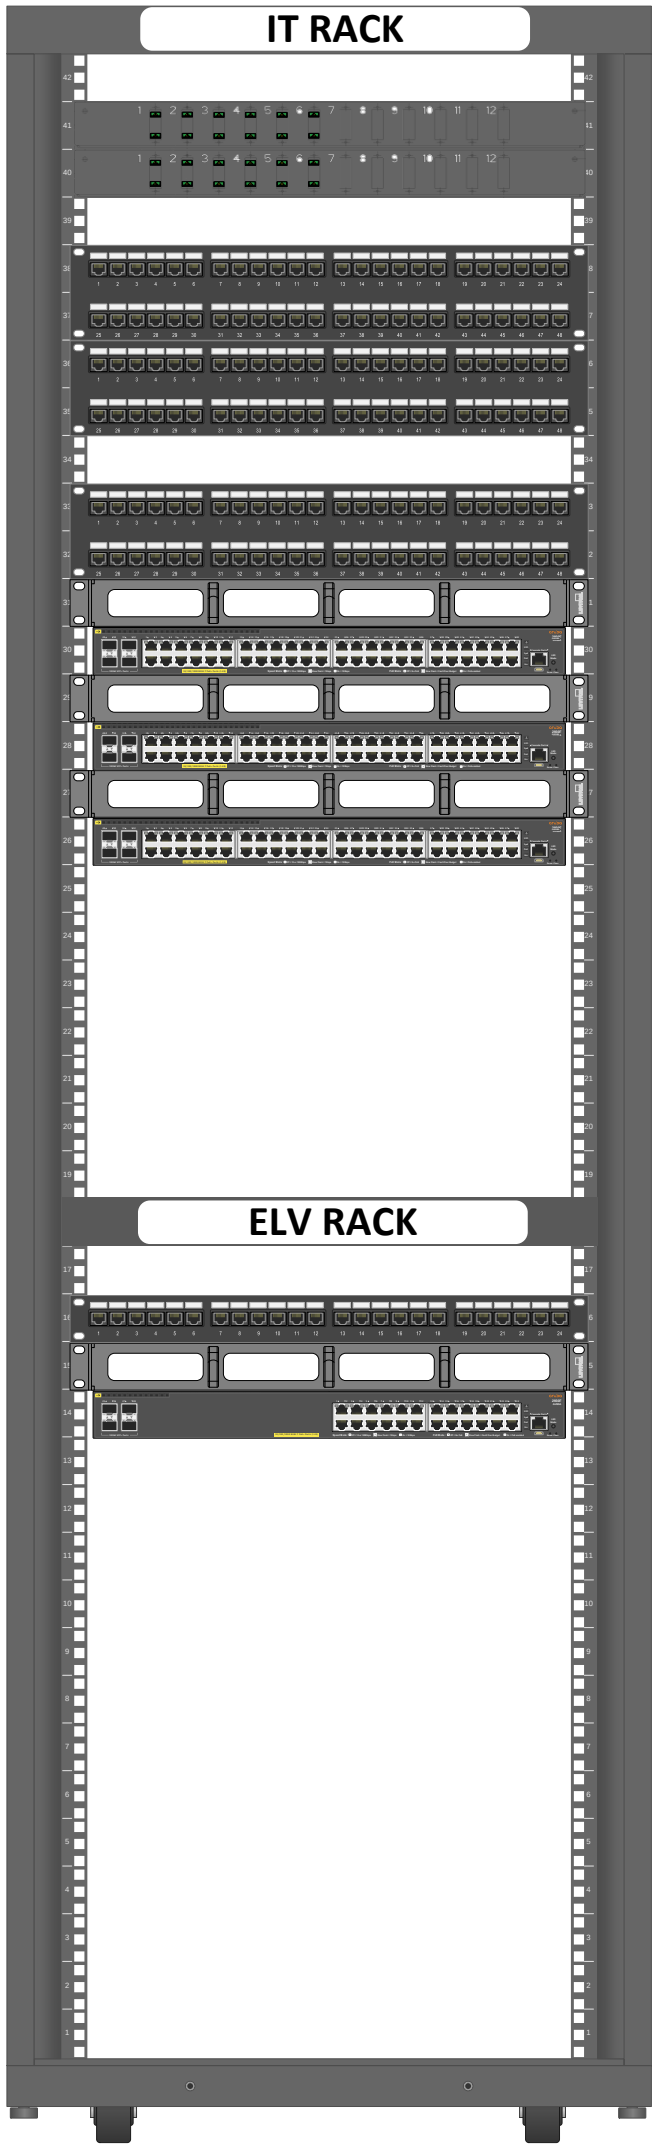

DỰ ÁN: TỔ HỢP KHÁCH SẠN, CĂN HỘ DỊCH VỤ MARRIOTT VÀ NHÀ Ở ĐỂ BÁN ĐỊA ĐIỂM XÂY DỰNG: 58 BẠCH ĐẰNG, P. HẢI CHÂU 1, Q. HẢI CHÂU, TP. ĐÀ NẴNG	
CHỦ ĐẦU TƯ: CÔNG TY CỔ PHẦN ĐỊA ỐC FOODINCO ĐỊA CHỈ: 58 BẠCH ĐẰNG, P. HẢI CHÂU 1, Q. HẢI CHÂU, TP. ĐÀ NẴNG	
BAN QUẢN LÝ DỰ ÁN:	
TƯ VẤN GIÁM SÁT: CN CÔNG TY TNHH APAVE CHÂU Á - THÁI BÌNH DƯƠNG TẠI ĐÀ NẴNG NGUYỄN ĐĂNG HÙNG	
ĐƠN VỊ NHÀ THẦU CHÍNH: CÔNG TY CỔ PHẦN ALPHANAM E&C	
NHÀ THẦU THI CÔNG:  CÔNG TY TNHH VIỄN THÔNG SÁNG TẠO THUẬN PHONG (INNOTEL) 55/31 TRẦN ĐÌNH XU, P. CẦU KHO, Q. 1, HCM Tel: (84 28) 3 862 1119 Fax: (84 28) 3 863 0366	
CHỈ HUY TRƯỞNG:	
NGUYỄN ĐỨC TIẾN	
NGƯỜI KIỂM TRA:	
NGƯỜI LẬP:	
TÊN BẢN VẼ: RACK LAYOUT – MEA BLOCK 25~38th FLOOR (~5 IDF RACK)	
NGÀY HT:	01/09/2022
CHỈNH SỬA:	01
MÃ BẢN VẼ:	IDF-MEA BLOCK
HỒ SƠ THAM CHIẾU:	220726 ELV - CAP NHAT CCTV THEO Y KIEN MI GS&S

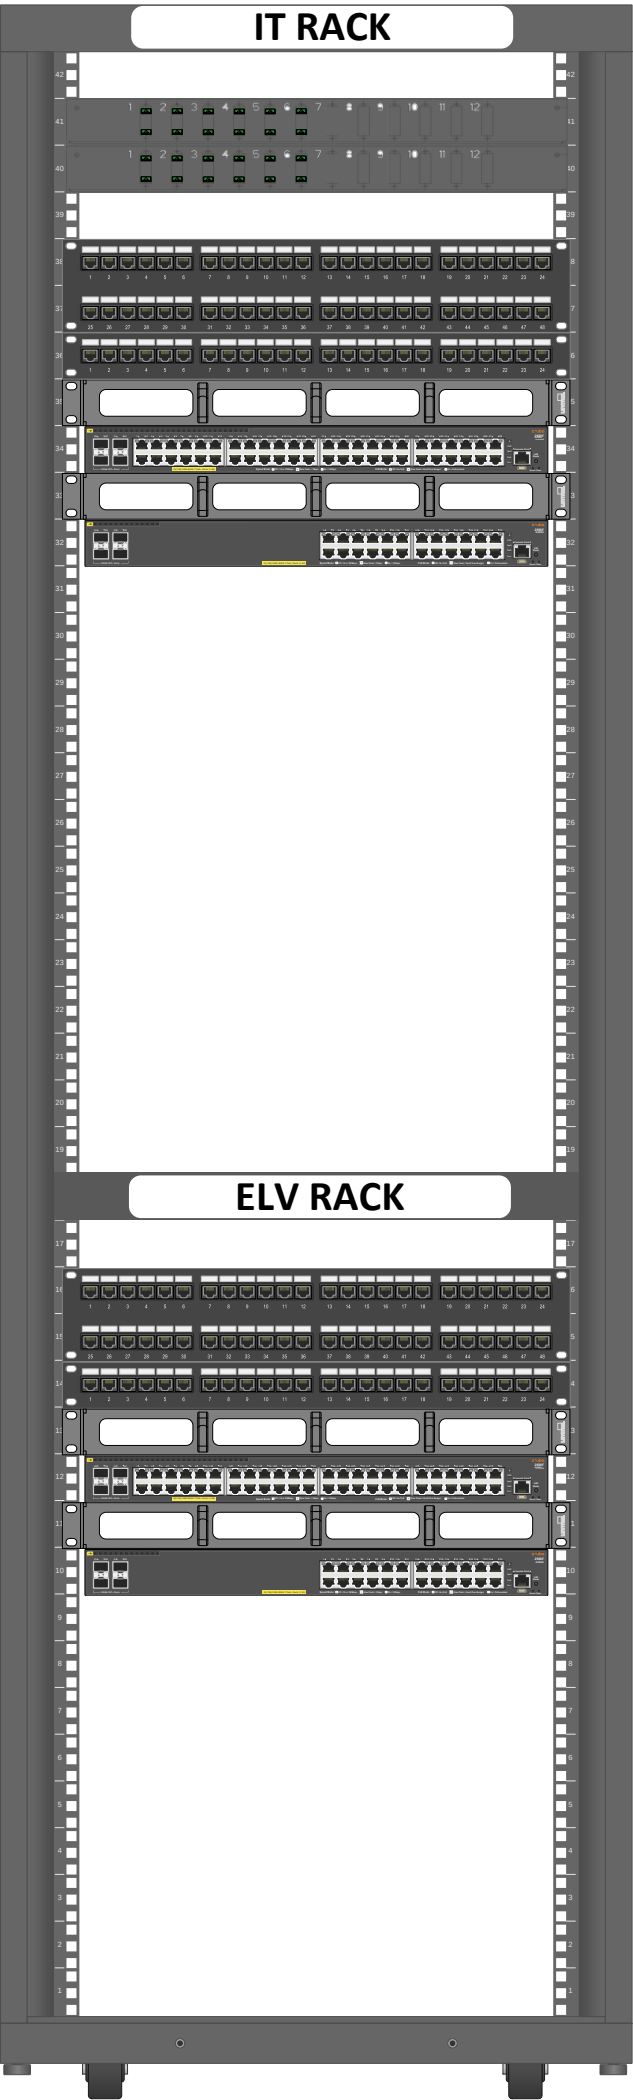

DỰ ÁN: TỔ HỢP KHÁCH SẠN, CĂN HỘ DỊCH VỤ MARRIOTT VÀ NHÀ Ở ĐỂ BÁN ĐỊA ĐIỂM XÂY DỰNG: 58 BẠCH ĐẰNG, P. HẢI CHÂU 1, Q. HẢI CHÂU, TP. ĐÀ NẴNG	
CHỦ ĐẦU TƯ: CÔNG TY CỔ PHẦN ĐỊA ỐC FOODINCO ĐỊA CHỈ: 58 BẠCH ĐẰNG, P. HẢI CHÂU 1, Q. HẢI CHÂU, TP. ĐÀ NẴNG	
BAN QUẢN LÝ DỰ ÁN:	
TƯ VẤN GIÁM SÁT: CN CÔNG TY TNHH APAVE CHÂU Á - THÁI BÌNH DƯƠNG TẠI ĐÀ NẴNG NGUYỄN ĐĂNG HÙNG	
ĐƠN VỊ NHÀ THẦU CHÍNH: CÔNG TY CỔ PHẦN ALPHANAM E&C	
NHÀ THẦU THI CÔNG:  CÔNG TY TNHH VIỄN THÔNG SÁNG TẠO THUẬN PHONG (INNOTEL) 55/31 TRẦN ĐÌNH XU, P. CẦU KHO, Q. 1, HCM Tel: (84 28) 3 862 1119 Fax: (84 28) 3 863 0366	
CHỈ HUY TRƯỞNG:	
NGUYỄN ĐỨC TIẾN	
NGƯỜI KIỂM TRA:	
NGƯỜI LẬP:	
TÊN BẢN VẼ: RACK LAYOUT IDF-M.39F	
NGÀY HT:	01/09/2022
CHỈNH SỬA:	01
MÃ BẢN VẼ:	IDF-M.39F
HỒ SƠ THAM CHIẾU:	220726 ELV - CAP NHAT CCTV THEO Y KIEN MI GS&S