

HỆ THỐNG ĐIỆN NHỆ

DANH MỤC BẢN VẼ.

STT	KÝ HIỆU BẢN VẼ	TÊN BẢN VẼ	TỶ LỆ	GHI CHÚ
1	ĐNH-01	DANH MỤC BẢN VẼ HỆ THỐNG ĐIỆN NHỆ	-	
2	ĐNH-02	SƠ ĐỒ NGUYÊN LÝ HỆ THỐNG CAMERA	-	
3	ĐNH-03	MẶT BẰNG BỐ TRÍ CAMERA TẦNG HẦM	-	
4	ĐNH-04	MẶT BẰNG BỐ TRÍ CAMERA TẦNG 1	-	
5	ĐNH-05	MẶT BẰNG BỐ TRÍ CAMERA TẦNG 2	-	
6	ĐNH-06	MẶT BẰNG BỐ TRÍ CAMERA TẦNG 3	-	
7	ĐNH-07	MẶT BẰNG BỐ TRÍ CAMERA TẦNG 4	-	
8	ĐNH-08	MẶT BẰNG BỐ TRÍ CAMERA TẦNG 5	-	
9	ĐNH-09	SƠ ĐỒ NGUYÊN LÝ HỆ THỐNG MẠNG, ĐIỆN THOẠI	-	
10	ĐNH-10	MẶT BẰNG BỐ TRÍ MẠNG TẦNG HẦM	-	
11	ĐNH-11	MẶT BẰNG BỐ TRÍ MẠNG TẦNG 1	-	
12	ĐNH-12	MẶT BẰNG BỐ TRÍ MẠNG TẦNG 2	-	
13	ĐNH-13	MẶT BẰNG BỐ TRÍ MẠNG TẦNG 3	-	
14	ĐNH-14	MẶT BẰNG BỐ TRÍ MẠNG TẦNG 4	-	
15	ĐNH-15	MẶT BẰNG BỐ TRÍ MẠNG TẦNG 5	-	
16	ĐNH-16	SƠ ĐỒ NGUYÊN LÝ HỆ THỐNG LOA	-	
17	ĐNH-17	MẶT BẰNG BỐ TRÍ LOA TẦNG HẦM	-	
18	ĐNH-18	MẶT BẰNG BỐ TRÍ LOA TẦNG 1	-	
19	ĐNH-19	MẶT BẰNG BỐ TRÍ LOA TẦNG 2	-	
20	ĐNH-20	MẶT BẰNG BỐ TRÍ LOA TẦNG 3	-	
21	ĐNH-21	MẶT BẰNG BỐ TRÍ LOA TẦNG 4	-	
22	ĐNH-22	MẶT BẰNG BỐ TRÍ LOA TẦNG 5	-	

CÁC BẢN VẼ KIẾN TRÚC ĐƯỢC ĐỌC CHUNG VỚI BẢN VẼ KẾT CẤU VÀ CƠ ĐIỆN LIÊN QUAN.
CÁC THÔNG TIN THUỘC VỀ KẾT CẤU VÀ CƠ ĐIỆN THẺ HIỆN TRÊN BẢN VẼ KIẾN TRÚC CHỈ ĐỂ THAM KHẢO.
BỐ TRÍ NỘI THẤT CHỈ MANG TÍNH THAM KHẢO, KỊCH THUỘC ĐINH VỊ TƯỜNG, HOÀN THIÊN NƠI THẬT XEM BẢN VẼ THIÊN KHAI NỘI THẤT.

BÊN THỦ HƯỚNG (———)

GIÁM ĐỐC: PHẠM THỊ NGUYỄN TRANG

CHỦ ĐẦU TƯ (CLIENT)

CÔNG TY TNHH MTV ĐẦU TƯ ĐỊA ỐC
THẢO ĐIỀN XANH

TU VẤN THIẾT KẾ (LEAD CONSULTANT)

IAM CÔNG TY CỔ PHẦN KIẾN TRÚC
IAMARCHITECTS
3F - 47G HOÀ HỒNG - PHƯỜNG 2
QUẬN PHÚ NHUẬN - TP. HCM - VN
EMAIL: INFO@IAM.VN
WEBSITE: IAM.VN

TỔNG GIÁM ĐỐC: NGUYỄN HOÀNG DŨNG

CÔNG TRÌNH (PROJECT)

BIS SCHOOL

242 NGUYỄN VĂN HƯỚNG
PHƯỜNG THẢO ĐIỀN , Q.2, TP. HCM

DỰ ÁN (PROJECT NO.)

18006

CHỦ TRÌ

(MANAGED BY)

KTS. NGÔ THÀNH VINH

THIẾT KẾ

(DESIGNED BY)

KS. NGUYỄN BẢO NĂNG

VẼ

(DRAWN BY)

KS. NGUYỄN BẢO NĂNG

KIỂM

(CHECK BY)

KTS. NGUYỄN NGỌC TOÀN

GHAI ĐOẠN

(STAGES)

TÊN BẢN VẼ (DRAWING TITLE)

HẸU CHỈNH

(REVISION NO.)

KHỔ GIẤY

(PAPER SIZE)

A2

NGÀY PHÁT HÀNH

(ISSUED DATE)

TỈ LỆ


(DWG. SCALE)

SỐ BẢN VẼ


(DRAWING NUMBER)

ĐNH-01


© IAM Architects 2018

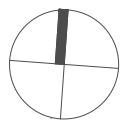

TẦNG : T2 -T3 -T4 -T5

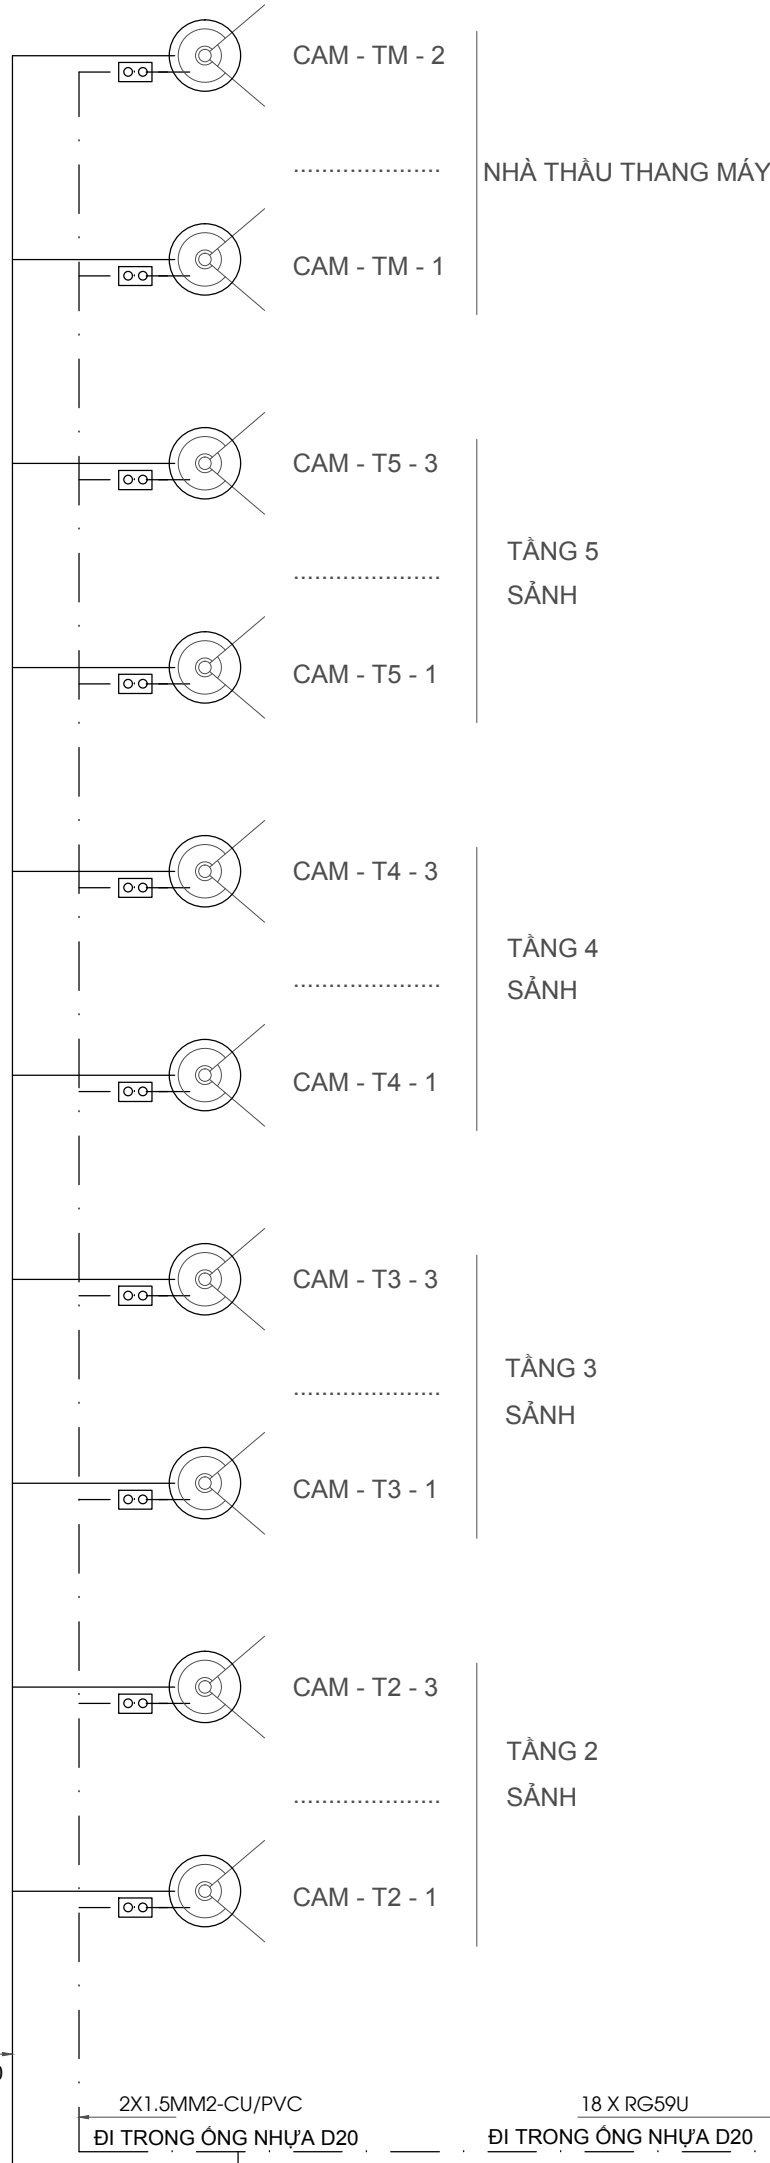


TẦNG HẦM -TẦNG 1

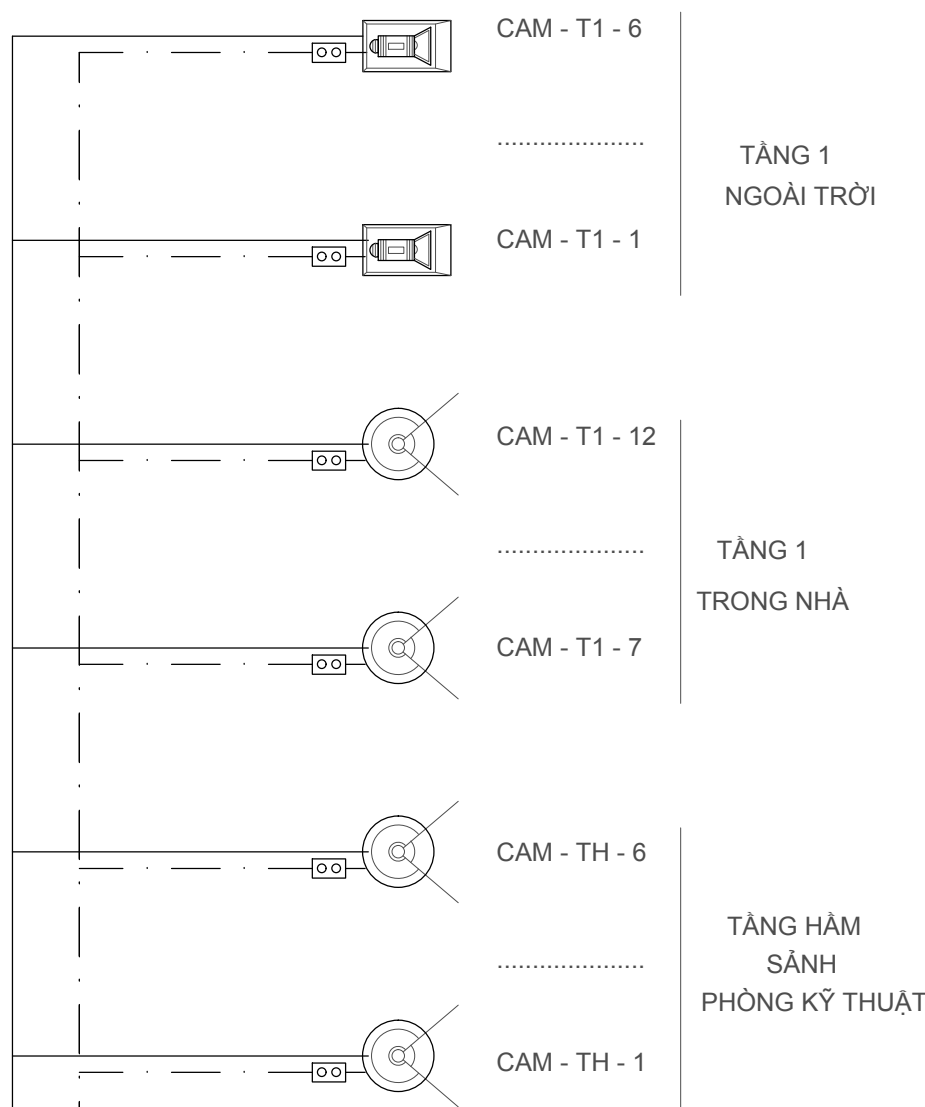

SƠ ĐỒ NGUYÊN LÝ HỆ THỐNG CAMERA QUAN SÁT

CHÚ THÍCH

KÝ HIỆU	TÊN VẬT TƯ THIẾT BỊ
	HỘP KỸ THUẬT 110x110x50
	CAMERA HỒNG NGOẠI HÌNH BÀN CẦU 2.0MP, 1/2.9" SONY IMX322 CMOS sensor, ỜNG KÍNH 4.0MM, HỒNG NGOẠI 15M
	CAMERA HỒNG NGOẠI HÌNH BÀN CẦU 2.0MP, LẮP TRONG THANG MÁY, 1/2.9" SONY IMX322 CMOS sensor,ỜNG KÍNH 2.8-12MM, HỒNG NGOẠI 15M
	CAMERA HỒNG NGOẠI HÌNH BÀN CẦU 2.0MP, 1/2.9" SONY IMX322 CMOS sensor, ỜNG KÍNH 4.0MM,HỒNG NGOẠI 25M, IP 66
	ĐẦU GHI HÌNH CAMERA - 32 KÊNH (Ồ CỨNG 16TB)
	CÁP ĐỒNG TRỰC RG59
	DÂY CÁP NGUỒN Cu/PVC 2x1C-1.5mm2

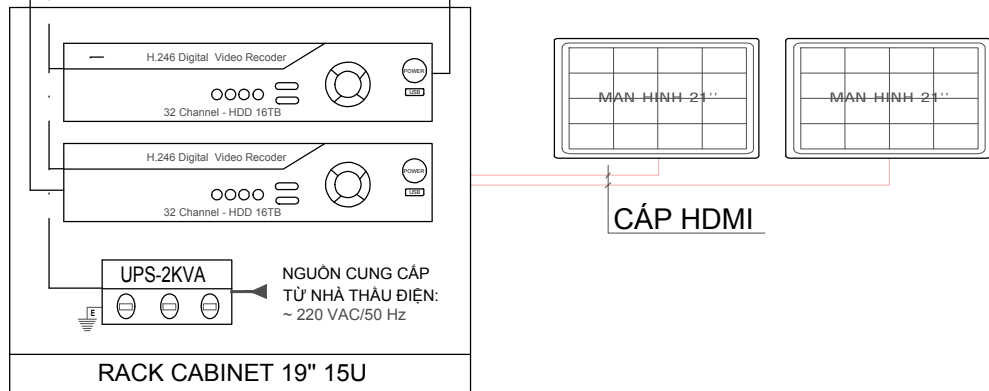

TỦ RACK 19"-15U ĐẶT TẠI PHÒNG KỸ THUẬT - TẦNG HẦM

CÁC BẢN VẼ KIẾN TRÚC ĐƯỢC CHUNG VỚI BẢN VẼ KẾT CẤU VÀ CƠ ĐIỆN LIÊN QUAN.
CÁC THÔNG TIN THUỘC VỀ KẾT CẤU VÀ CƠ ĐIỆN THỂ HIỆN TRÊN BẢN VẼ KIẾN TRÚC CHỈ ĐỂ THAM KHẢO.
BỘ TỜ NỘI THẤT CHỈ MANG TÍNH THAM KHẢO, KỊCH THUỘC ĐỊNH VỊ TƯỜNG, HOÀN THIÊN NỘI THẤT XEM BẢN VẼ THIÊN KHAI NỘI THẤT.

BÊN THỦ HƯỚNG (.....)

GIÁM ĐỐC: PHẠM THỊ NGUYỄN TRANG

CHỦ ĐẦU TƯ (CLIENT)

CÔNG TY TNHH MTV ĐẦU TƯ ĐỊA ỐC
THẢO ĐIỆN XANH

TƯ VẤN THIẾT KẾ (LEAD CONSULTANT)

IAM CÔNG TY CỔ PHẦN KIẾN TRÚC
IAMARCHITECTS 3F - 47G HOA HỒNG - PHƯỜNG 2
QUẬN PHÚ NHUẬN - TP. HCM - VN
EMAIL: INFO@IAM.VN
WEBSITE: IAMA.VN

TỔNG GIÁM ĐỐC: NGUYỄN HOÀNG DŨNG

CÔNG TRÌNH (PROJECT)

BIS SCHOOL

242 NGUYỄN VĂN HƯỚNG
PHƯỜNG THẢO ĐIỆN, Q.2, TP. HCM

DỰ ÁN (PROJECT NO.)

18006

CHỦ TRÌ

(MANAGED BY)

KTS. NGÔ THÀNH VINH

THIẾT KẾ

(DESIGNED BY)

KS. NGUYỄN BẢO NĂNG

VẼ

(DRAWN BY)

KS. NGUYỄN BẢO NĂNG

KIỂM

(CHECK BY)

KTS. NGUYỄN NGỌC TOÀN

GIẢI ĐOẠN

(STAGE)

TÊN BẢN VẼ (DRAWING TITLE)

HIỆU CHỈNH

(REVISION NO.)

KHỔ GIẤY

(PAPER SIZE)

A2

TỈ LỆ

(DWG. SCALE)

NGÀY PHÁT HÀNH


(ISSUED DATE)

SỐ BẢN VẼ

(DRAWING NUMBER)

ĐNH-02


© IAM Architects 2018

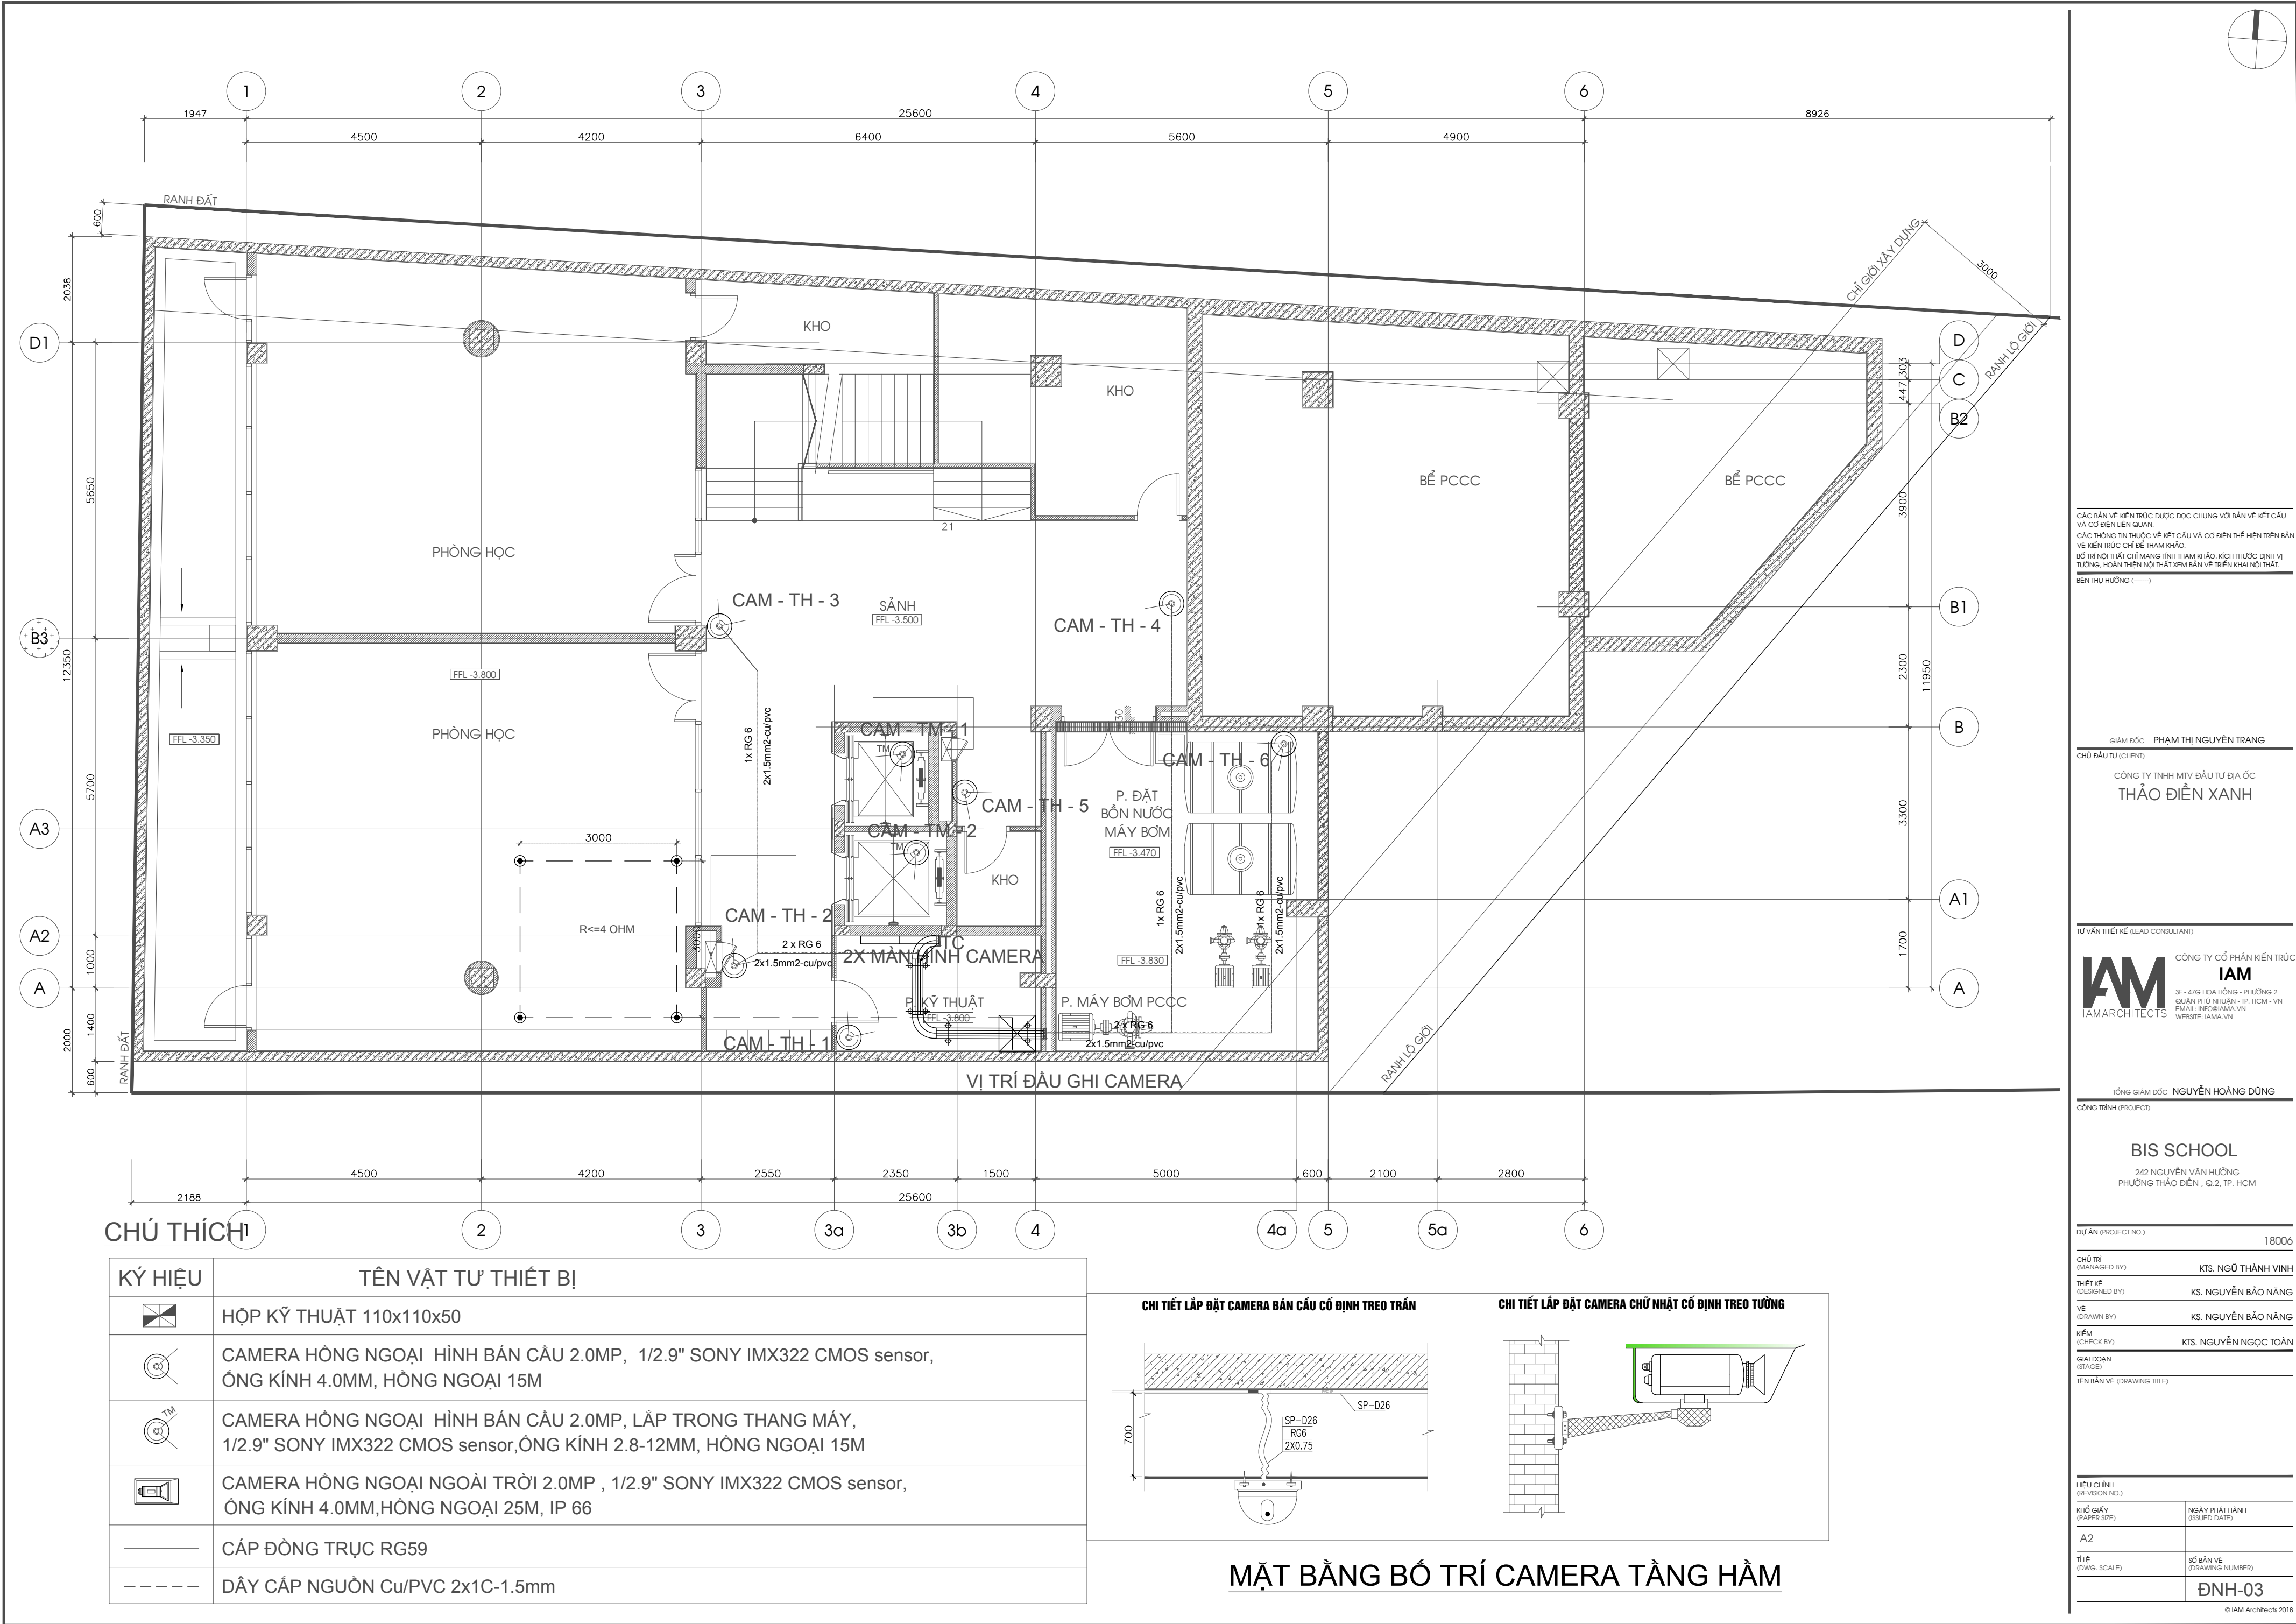


CHÚ THÍCH

KÝ HIỆU	TÊN VẬT TƯ THIẾT BỊ
	HỘP KỸ THUẬT 110x110x50
	CAMERA HỒNG NGOẠI HÌNH BÁN CẦU 2.0MP, 1/2.9" SONY IMX322 CMOS sensor, ỜNG KÍNH 4.0MM, HỒNG NGOẠI 15M
	CAMERA HỒNG NGOẠI HÌNH BÁN CẦU 2.0MP, LẮP TRONG THANG MÁY, 1/2.9" SONY IMX322 CMOS sensor, ỜNG KÍNH 2.8-12MM, HỒNG NGOẠI 15M
	CAMERA HỒNG NGOẠI NGOÀI TRỜI 2.0MP, 1/2.9" SONY IMX322 CMOS sensor, ỜNG KÍNH 4.0MM, HỒNG NGOẠI 25M, IP 66
	CÁP ĐỒNG TRỤC RG59
	DÂY CẤP NGUỒN Cu/PVC 2x1C-1.5mm

CHI TIẾT LẮP ĐẶT CAMERA BÁN CẦU CỐ ĐỊNH TREO TRẦN

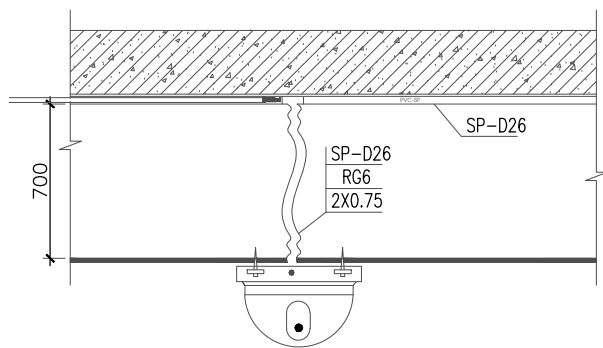

CHI TIẾT LẮP ĐẶT CAMERA CHỮ NHẬT CỐ ĐỊNH TREO TƯỜNG

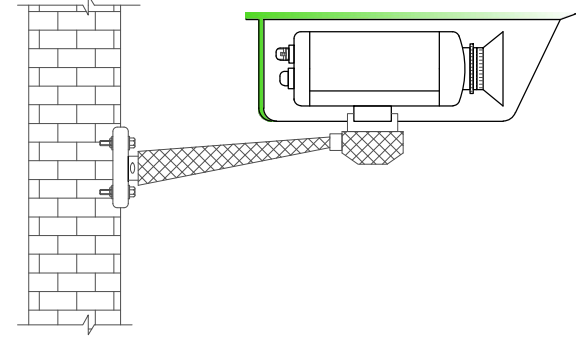

MẶT BẰNG BỐ TRÍ CAMERA TẦNG HẦM

CÁC BẢN VẼ KIẾN TRÚC ĐƯỢC CHUNG VỚI BẢN VẼ KẾT CẤU VÀ CƠ ĐIỆN LIÊN QUAN.
CÁC THÔNG TIN THUỘC VỀ KẾT CẤU VÀ CƠ ĐIỆN THỂ HIỆN TRÊN BẢN VẼ KIẾN TRÚC CHỈ ĐỂ THAM KHẢO.
BỐ TRÍ NỘI THẤT CHỈ MANG TÍNH THAM KHẢO, KỊCH THUỘC ĐỊNH VỊ TƯỜNG, HOÀN THIÊN NƠI THẬT XEM BẢN VẼ THIÊN KHAI NỘI THẤT.

BÊN THỦ HƯỚNG (.....)

GIÁM ĐỐC: PHẠM THỊ NGUYỄN TRANG

CHỦ ĐẦU TƯ (CLIENT):

CÔNG TY TNHH MTV ĐẦU TƯ ĐỊA ỐC
THẢO ĐIỀN XANH

TƯ VẤN THIẾT KẾ (LEAD CONSULTANT):

CÔNG TY CỔ PHẦN KIẾN TRÚC
IAM
IAMARCHITECTS
3F - 47G HOÀ HỒNG - PHƯỜNG 2
QUẬN PHÚ NHUẬN - TP. HCM - VN
EMAIL: INFO@IAM.VN
WEBSITE: IAM.VN

TỔNG GIÁM ĐỐC: NGUYỄN HOÀNG DŨNG

CÔNG TRÌNH (PROJECT):

BIS SCHOOL
242 NGUYỄN VĂN HƯỚNG
PHƯỜNG THẢO ĐIỀN, Q.2, TP. HCM

DỰ ÁN (PROJECT NO.): 18006

CHỦ TRÌ (MANAGED BY): KTS. NGÔ THÀNH VINH

THIẾT KẾ (DESIGNED BY): KS. NGUYỄN BẢO NANG

VẼ (DRAWN BY): KS. NGUYỄN BẢO NANG

KIỂM (CHECK BY): KTS. NGUYỄN NGỌC TOÀN

GIẢI ĐOẠN (STAGE):

TÊN BẢN VẼ (DRAWING TITLE):


HIỆU CHỈNH (REVISION NO.):

KHỔ GIẤY (PAPER SIZE): A2

TÌT (DWG. SCALE):


SỐ BẢN VẼ (DRAWING NUMBER): ĐNH-03

© IAM Architects 2018

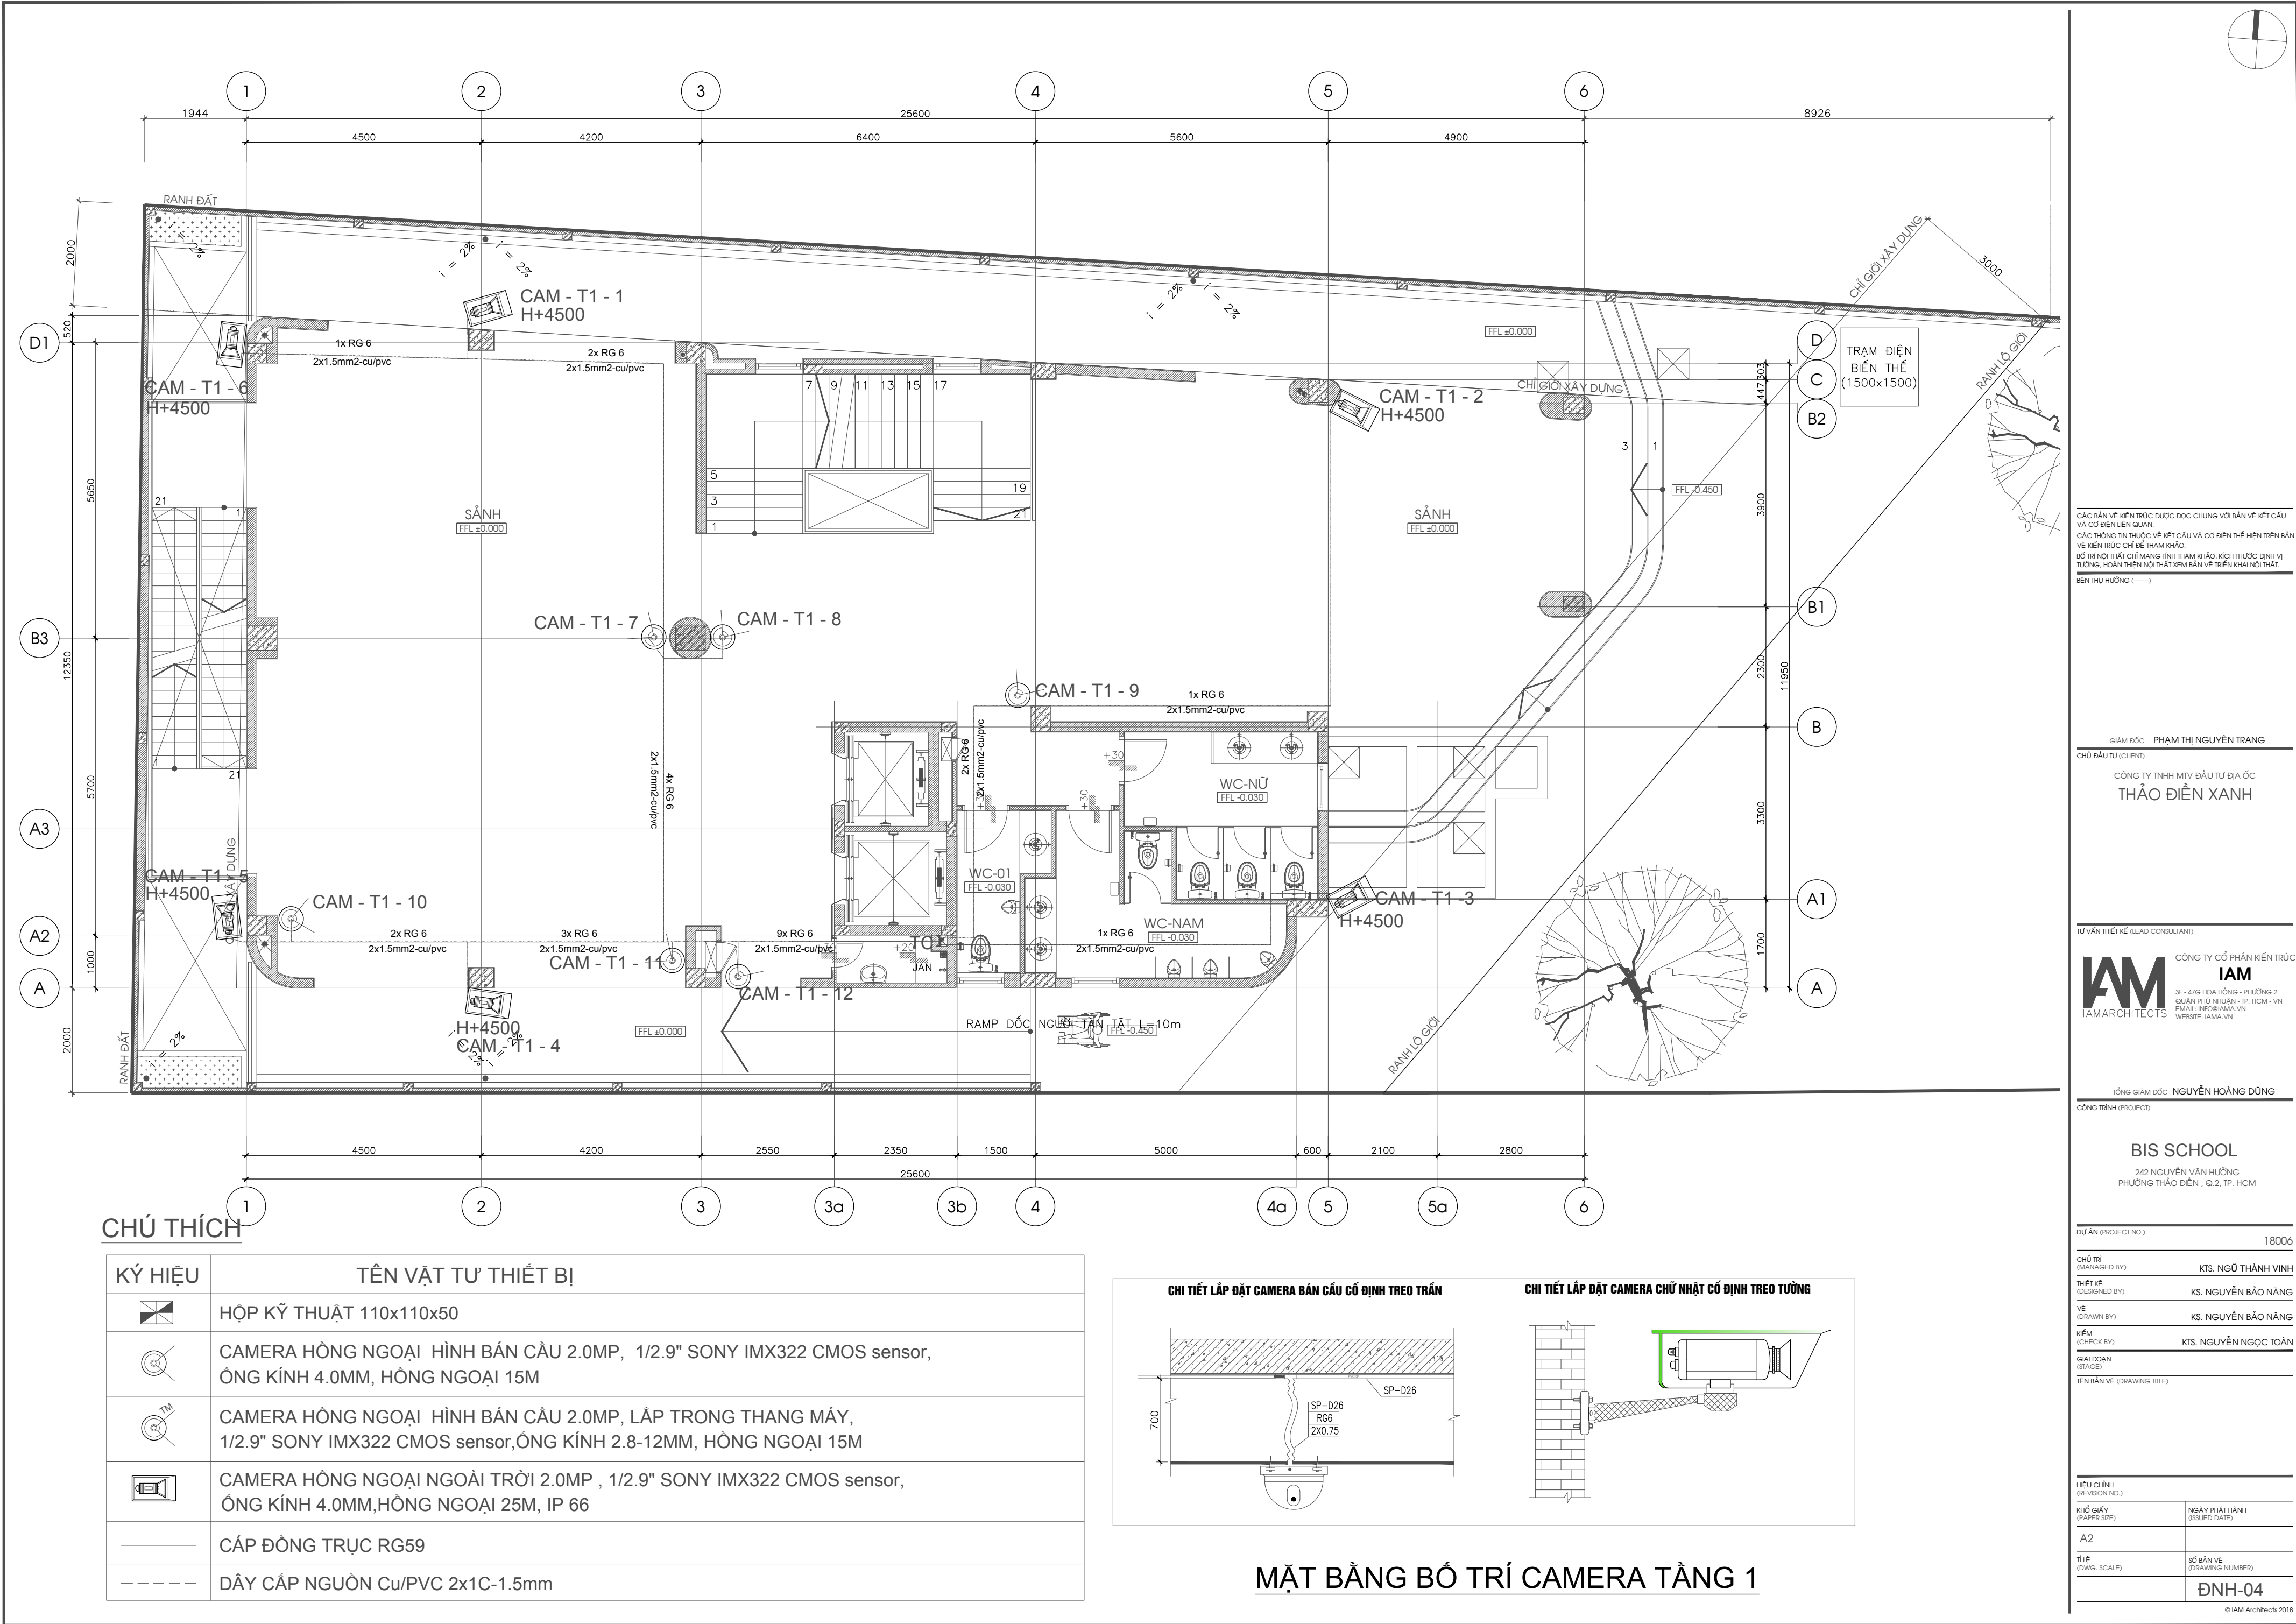

CHÚ THÍCH

KÝ HIỆU	TÊN VẬT TƯ THIẾT BỊ
	HỘP KỸ THUẬT 110x110x50
	CAMERA HỒNG NGOẠI HÌNH BÁN CẦU 2.0MP, 1/2.9" SONY IMX322 CMOS sensor, ỜNG KÍNH 4.0MM, HỒNG NGOẠI 15M
	CAMERA HỒNG NGOẠI HÌNH BÁN CẦU 2.0MP, LẮP TRONG THANG MÁY, 1/2.9" SONY IMX322 CMOS sensor, ỜNG KÍNH 2.8-12MM, HỒNG NGOẠI 15M
	CAMERA HỒNG NGOẠI NGOÀI TRỜI 2.0MP , 1/2.9" SONY IMX322 CMOS sensor, ỜNG KÍNH 4.0MM,HỒNG NGOẠI 25M, IP 66
	CÁP ĐỒNG TRỤC RG59
	DÂY CÁP NGUỒN Cu/PVC 2x1C-1.5mm

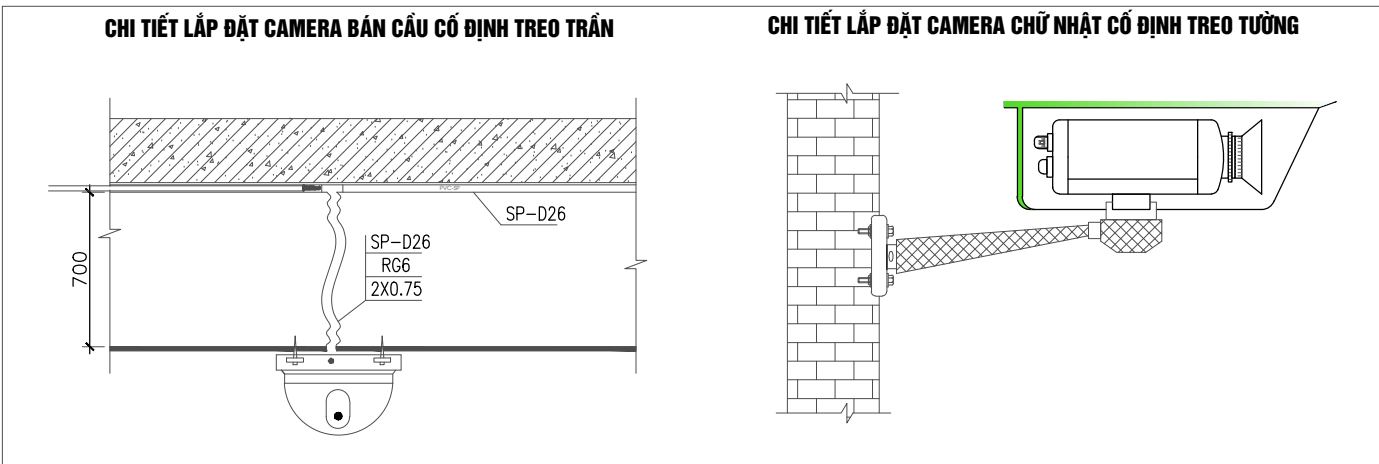

MẶT BẰNG BỐ TRÍ CAMERA TẦNG 1

CÁC BẢN VẼ KIẾN TRÚC ĐƯỢC CHUNG VỚI BẢN VẼ KẾT CẤU VÀ CƠ ĐIỆN LIÊN QUAN.
CÁC THÔNG TIN THUỘC VỀ KẾT CẤU VÀ CƠ ĐIỆN THỂ HIỆN TRÊN BẢN VẼ KIẾN TRÚC CHỈ ĐỂ THAM KHẢO.
BỐ TRÍ NỘI THẤT CHỈ MANG TÍNH THAM KHẢO, KỊCH THUỘC ĐỊNH VỊ TƯỜNG, HOÀN THIÊN NƠI THẬT XEM BẢN VẼ THIÊN KHAI NỘI THẤT.

BÊN THỦ HƯỚNG (.....)

GIÁM ĐỐC: PHẠM THỊ NGUYỄN TRANG
CHỦ ĐẦU TƯ (CLIENT):

CÔNG TY TNHH MTV ĐẦU TƯ ĐỊA ỐC
THẢO DIỆN XANH

TƯ VẤN THIẾT KẾ (LEAD CONSULTANT):
CÔNG TY CỔ PHẦN KIẾN TRÚC
IAM
IAMARCHITECTS
3F - 47G HOÀ HỒNG - PHƯỜNG 2
QUẬN PHÚ NHUẬN - TP. HCM - VN
EMAIL: INFO@IAM.VN
WEBSITE: IAM.VN

TỔNG GIÁM ĐỐC: NGUYỄN HOÀNG DŨNG
CÔNG TRÌNH (PROJECT):

BIS SCHOOL
242 NGUYỄN VĂN HƯỚNG
PHƯỜNG THẢO DIỆN, Q.2, TP. HCM

DỰ ÁN (PROJECT NO.): 18006

CHỦ TRÌ (MANAGED BY): KTS. NGÔ THÀNH VINH

THIẾT KẾ (DESIGNED BY): KS. NGUYỄN BẢO NANG

VẼ (DRAWN BY): KS. NGUYỄN BẢO NANG

KIỂM (CHECK BY): KTS. NGUYỄN NGỌC TOÀN

GIẢI ĐOẠN (STAGE):

TÊN BẢN VẼ (DRAWING TITLE):

HIỆU CHỈNH (REVISION NO.):



KHỔ GIẤY (PAPER SIZE): A2

TỈ LỆ (DWG. SCALE):

NGÀY PHÁT HÀNH (ISSUED DATE):

SỐ BẢN VẼ (DRAWING NUMBER): ĐNH-04


© IAM Architects 2018

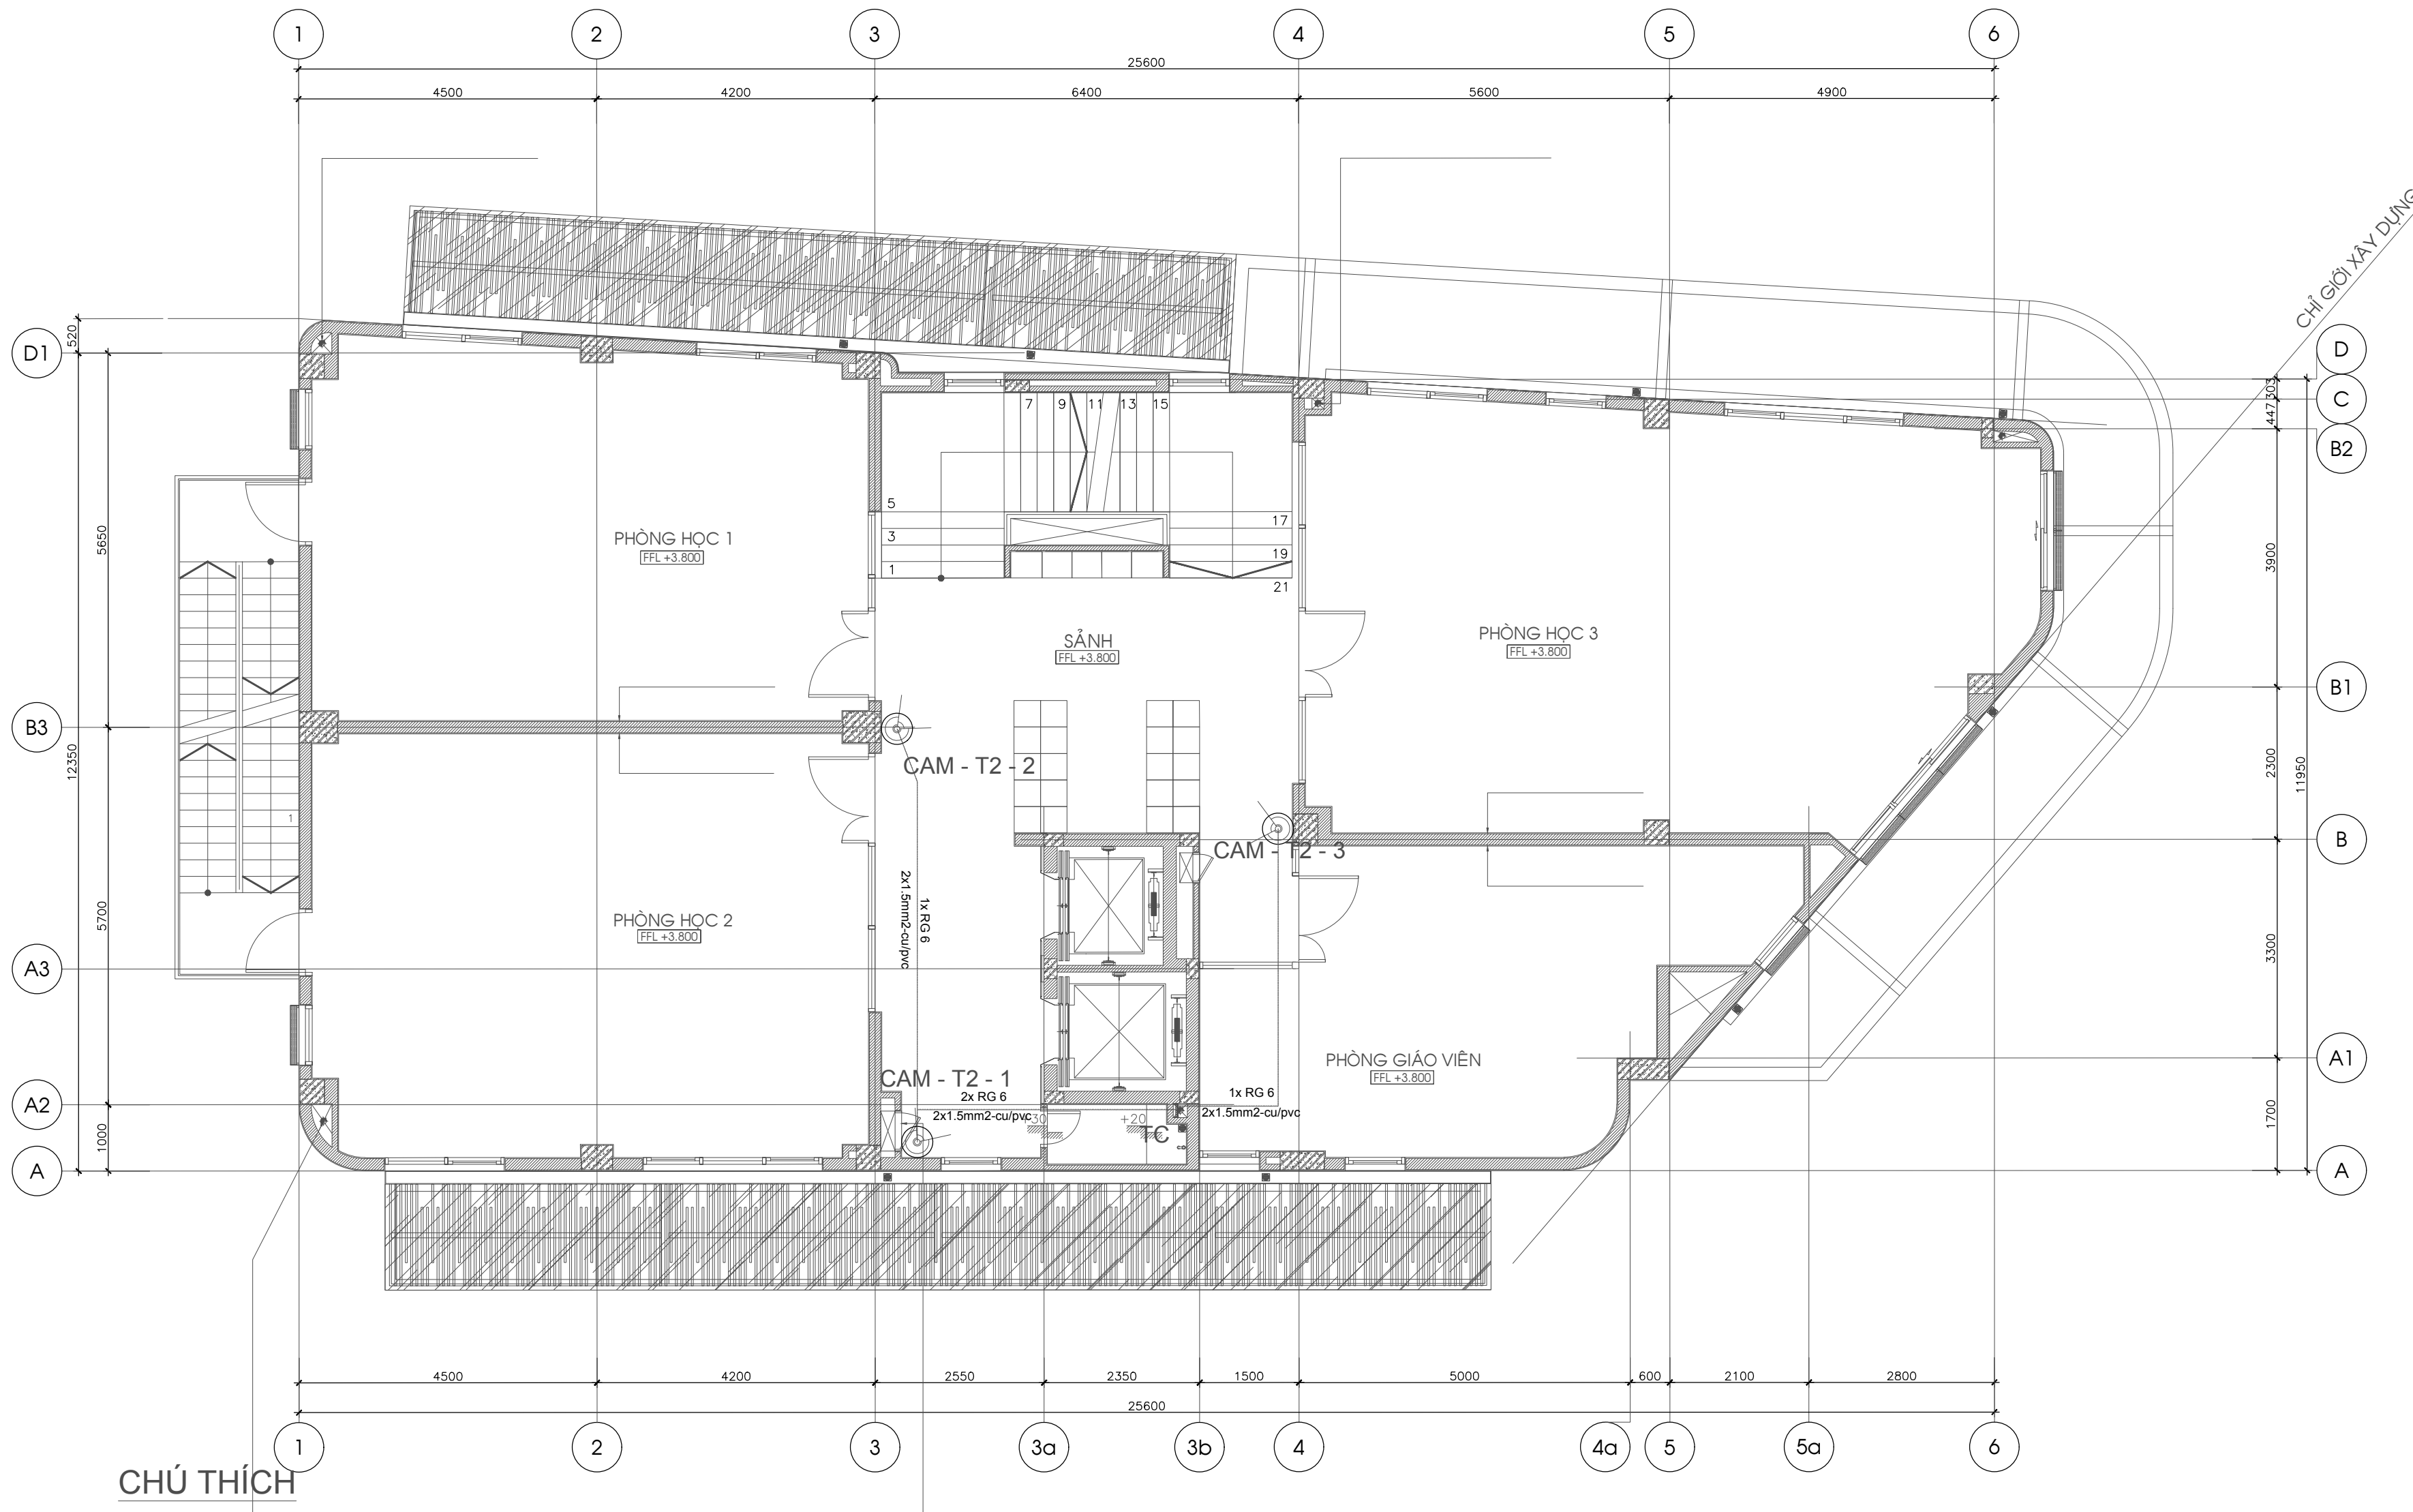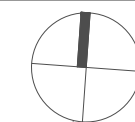


CHÚ THÍCH

KÝ HIỆU	TÊN VẬT TƯ THIẾT BỊ
	HỘP KỸ THUẬT 110x110x50
	CAMERA HỒNG NGOẠI HÌNH BÁN CẦU 2.0MP, 1/2.9" SONY IMX322 CMOS sensor, ống kính 4.0MM, HỒNG NGOẠI 15M
	CAMERA HỒNG NGOẠI HÌNH BÁN CẦU 2.0MP, LẮP TRONG THANG MÁY, 1/2.9" SONY IMX322 CMOS sensor, ống kính 2.8-12MM, HỒNG NGOẠI 15M
	CAMERA HỒNG NGOẠI NGOÀI TRỜI 2.0MP, 1/2.9" SONY IMX322 CMOS sensor, ống kính 4.0MM, HỒNG NGOẠI 25M, IP 66
	CÁP ĐỒNG TRỰC RG59
	DÂY CÁP NGUỒN Cu/PVC 2x1C-1.5mm

CHI TIẾT LẮP ĐẶT CAMERA BÁN CẦU CỐ ĐỊNH TREO TRẦN

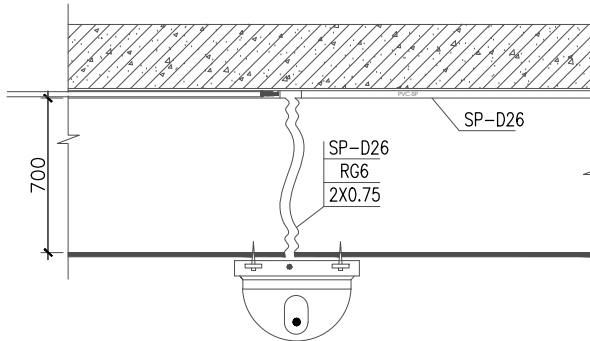

CHI TIẾT LẮP ĐẶT CAMERA CHỮ NHẬT CỐ ĐỊNH TREO TƯỜNG

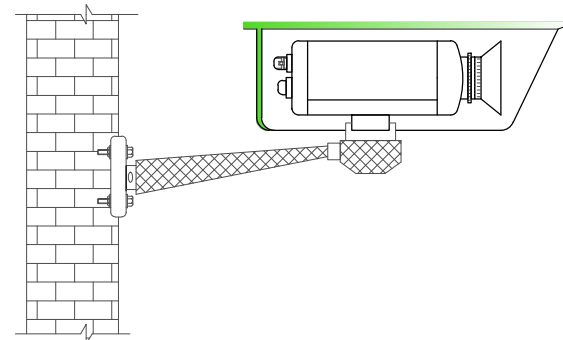

MẶT BẰNG BỐ TRÍ CAMERA TẦNG 2

CÁC BẢN VẼ KIẾN TRÚC ĐƯỢC ĐỌC CHUNG VỚI BẢN VẼ KẾT CẤU VÀ CƠ ĐIỆN LIÊN QUAN.
CÁC THÔNG TIN THUỘC VỀ KẾT CẤU VÀ CƠ ĐIỆN THỂ HIỆN TRÊN BẢN VẼ KIẾN TRÚC CHỈ ĐỂ THAM KHẢO.
BỐ TRÍ NƠI THẮT CHỈ MANG TÍNH THAM KHẢO, KỊCH THUỘC ĐỊNH VỊ TƯỜNG, HOÀN THIÊN NƠI THẮT XEM BẢN VẼ THIÊN KHAI NỘI THẤT.

BÊN THỦ HƯỚNG (.....)

GIÁM ĐỐC: PHẠM THỊ NGUYỄN TRANG

CHỦ ĐẦU TƯ (CLIENT)

CÔNG TY TNHH MTV ĐẦU TƯ ĐỊA ỐC
THẢO ĐIỆN XANH

TƯ VẤN THIẾT KẾ (LEAD CONSULTANT)

CÔNG TY CỔ PHẦN KIẾN TRÚC
IAM
IAMARCHITECTS
3F - 47G HOÀ HỒNG - PHƯỜNG 2
QUẬN PHÚ NHUẬN - TP. HCM - VN
EMAIL: INFO@IAM.VN
WEBSITE: IAMA.VN

TỔNG GIÁM ĐỐC: NGUYỄN HOÀNG DŨNG

CÔNG TRÌNH (PROJECT)

BIS SCHOOL
242 NGUYỄN VĂN HƯỚNG
PHƯỜNG THẢO ĐIỆN, Q.2, TP. HCM

DỰ ÁN (PROJECT NO.) 18006

CHỦ TRÌ (MANAGED BY) KTS. NGŨ THÀNH VINH

THIẾT KẾ (DESIGNED BY) KS. NGUYỄN BẢO NĂNG

VẼ (DRAWN BY) KS. NGUYỄN BẢO NĂNG

KIỂM (CHECK BY) KTS. NGUYỄN NGỌC TOÀN

GIẢI ĐOẠN (STAGE)

TÊN BẢN VẼ (DRAWING TITLE)

HIỆU CHỈNH (REVISION NO.)



KHỔ GIẤY (PAPER SIZE) NGÀY PHÁT HÀNH (ISSUED DATE)

A2

TỈ LỆ (DWG. SCALE) SỐ BẢN VẼ (DRAWING NUMBER)


ĐNH-05

© IAM Architects 2018

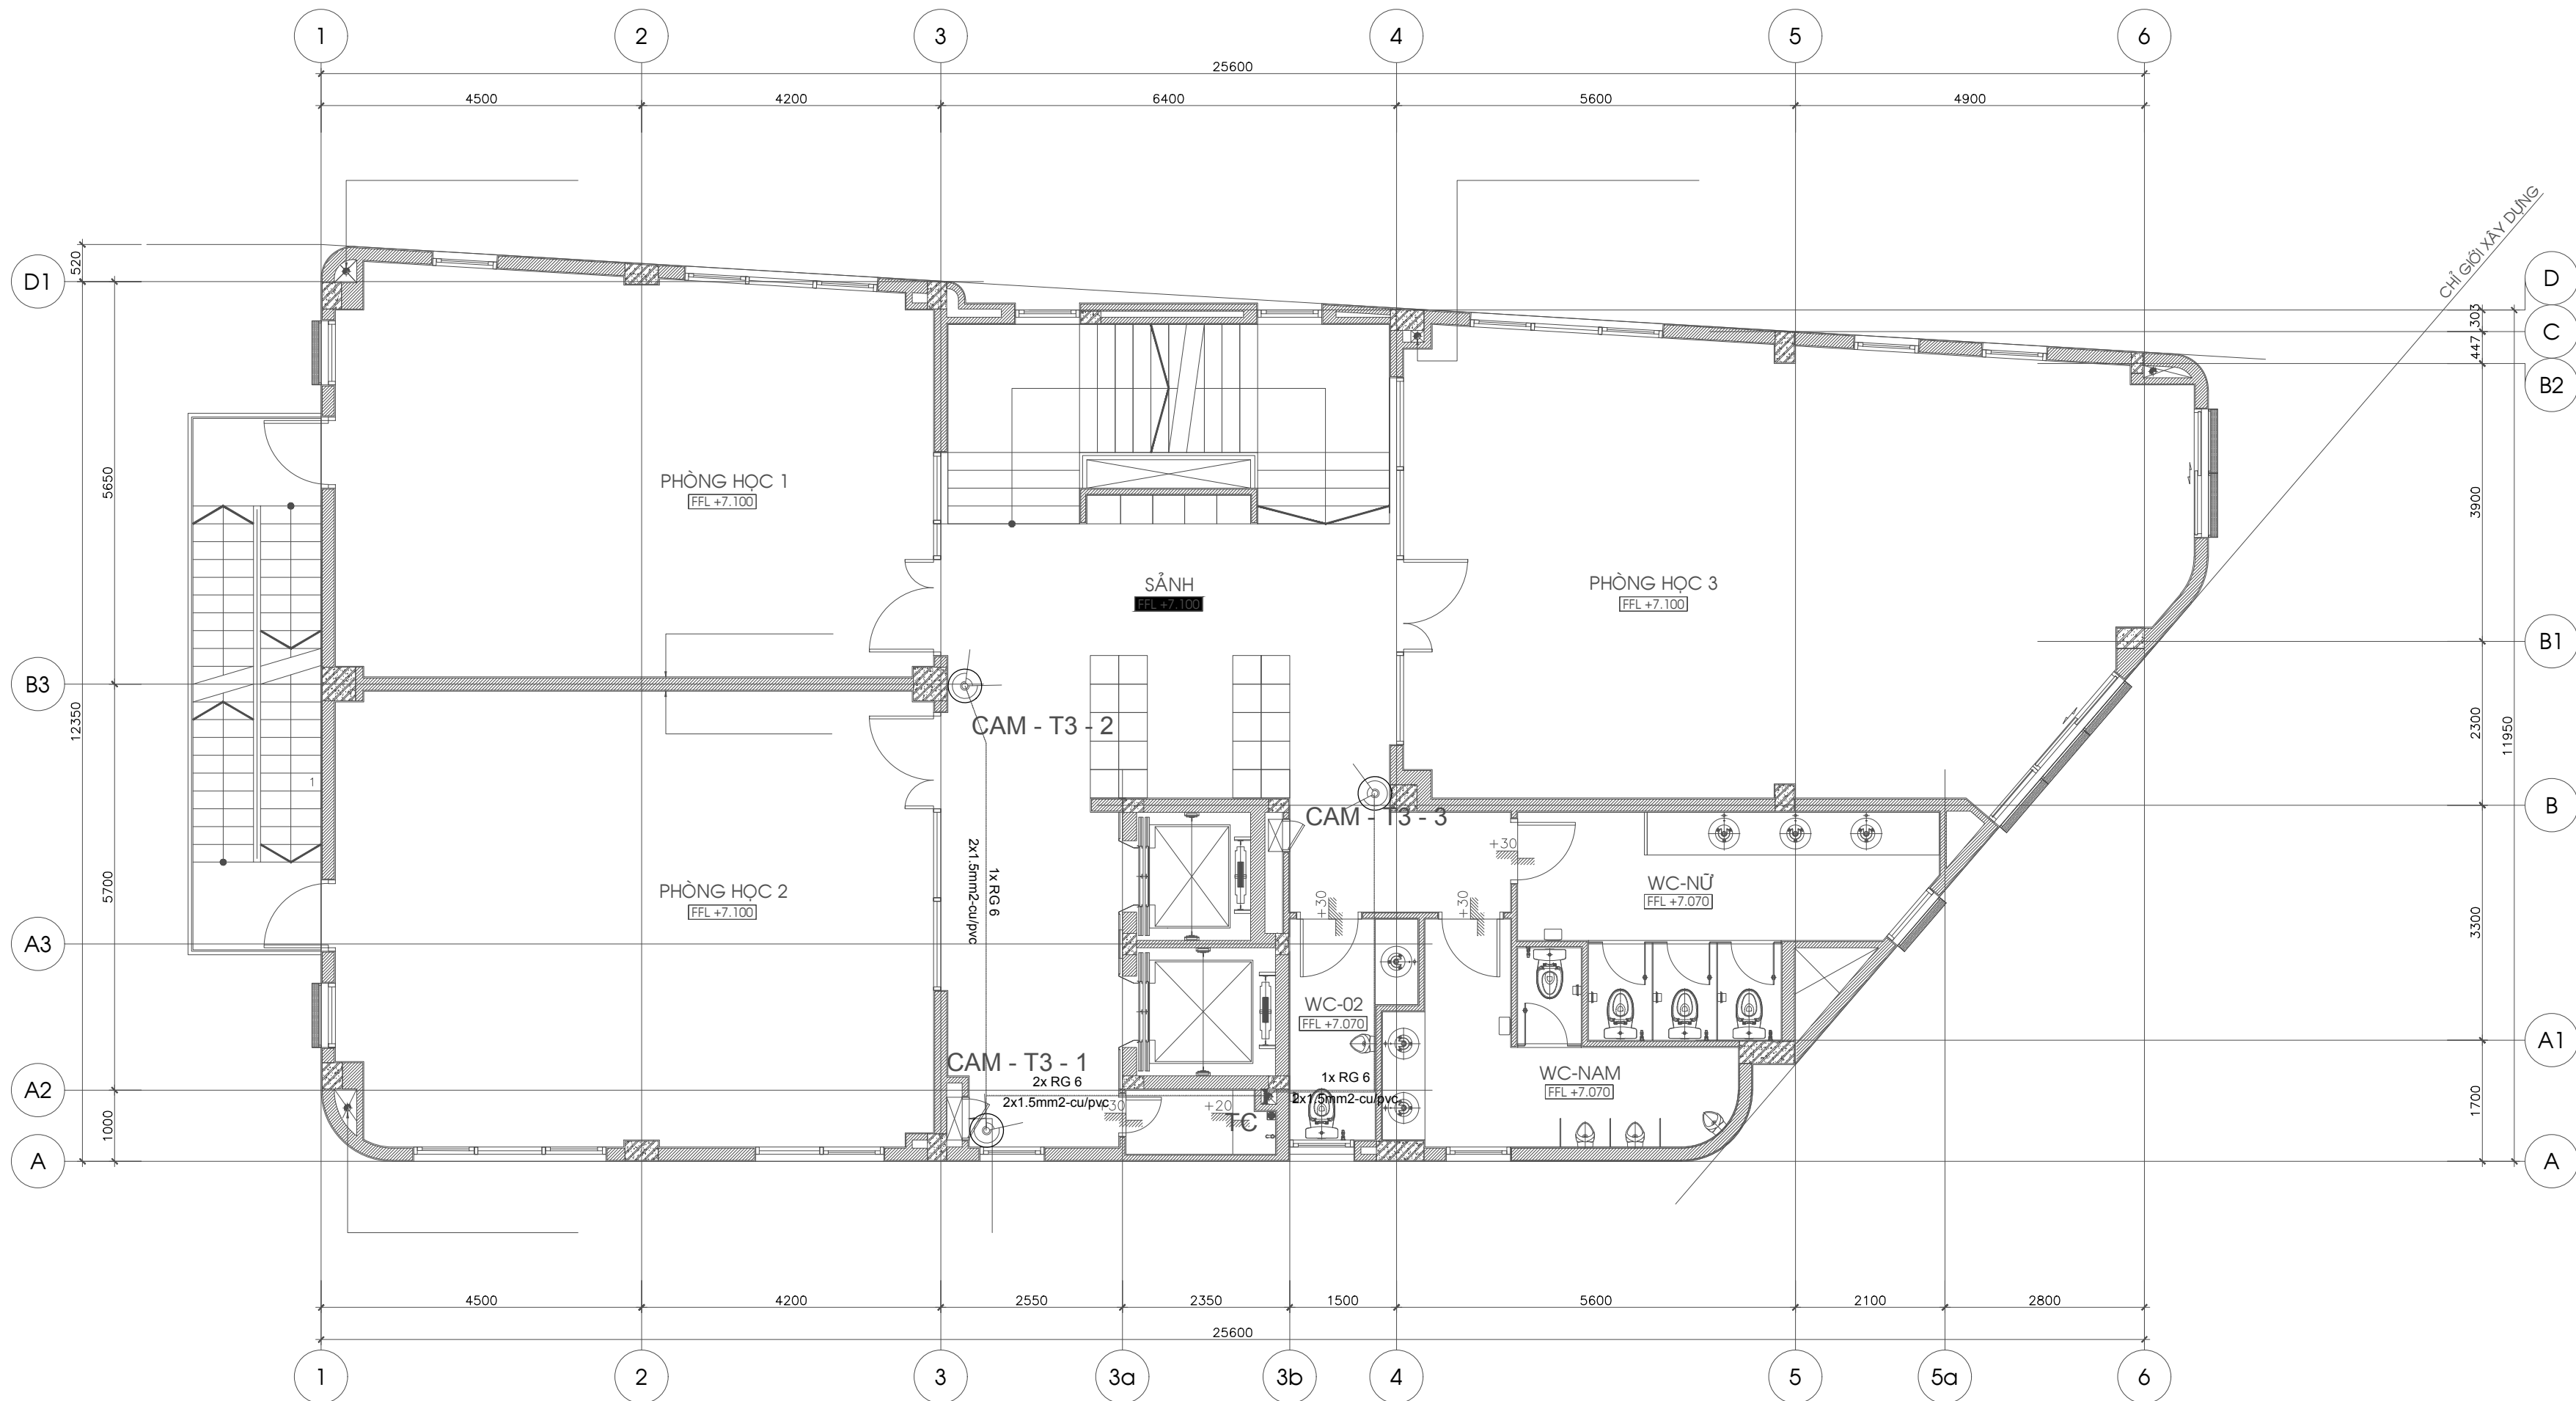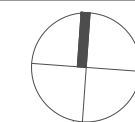

CHÚ THÍCH

KÝ HIỆU	TÊN VẬT TƯ THIẾT BỊ
	HỘP KỸ THUẬT 110x110x50
	CAMERA HỒNG NGOẠI HÌNH BÁN CẦU 2.0MP, 1/2.9" SONY IMX322 CMOS sensor, ống kính 4.0MM, HỒNG NGOẠI 15M
	CAMERA HỒNG NGOẠI HÌNH BÁN CẦU 2.0MP, LẮP TRONG THANG MÁY, 1/2.9" SONY IMX322 CMOS sensor, ống kính 2.8-12MM, HỒNG NGOẠI 15M
	CAMERA HỒNG NGOẠI NGOÀI TRỜI 2.0MP, 1/2.9" SONY IMX322 CMOS sensor, ống kính 4.0MM, HỒNG NGOẠI 25M, IP 66
	CÁP ĐỒNG TRỤC RG59
	DÂY CÁP NGUỒN Cu/PVC 2x1C-1.5mm

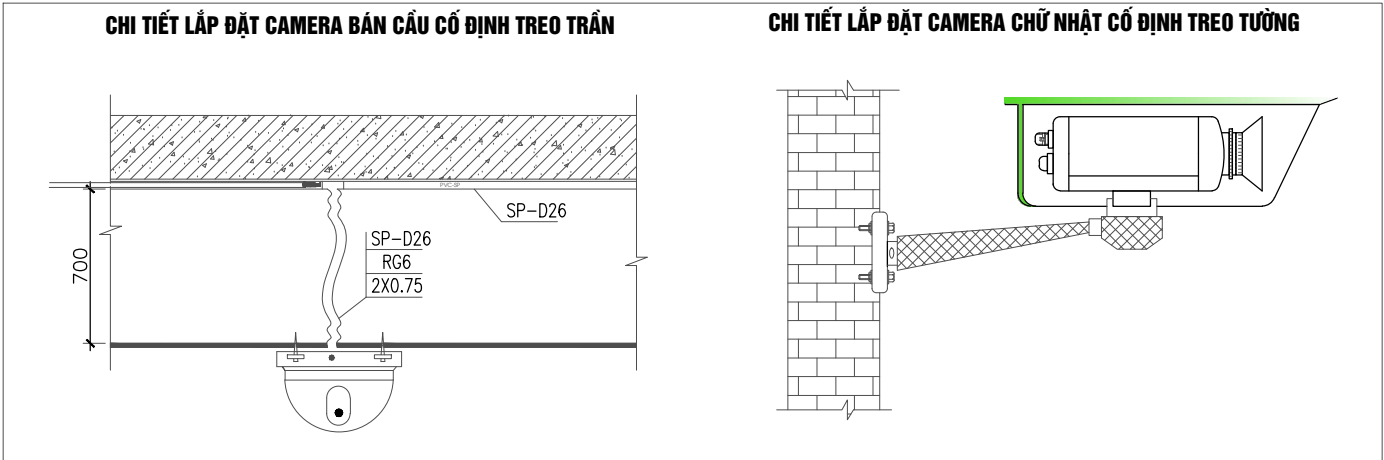

MẶT BẰNG BỐ TRÍ CAMERA TẦNG 3

CÁC BẢN VẼ KIẾN TRÚC ĐƯỢC CHUNG VỚI BẢN VẼ KẾT CẤU VÀ CƠ ĐIỆN LIÊN QUAN.
CÁC THÔNG TIN THUỘC VỀ KẾT CẤU VÀ CƠ ĐIỆN THỂ HIỆN TRÊN BẢN VẼ KIẾN TRÚC CHỈ ĐỂ THAM KHẢO.
BỐ TRÍ NỘI THẤT CHỈ MANG TÍNH THAM KHẢO, KỊCH THUỘC ĐỊNH VỊ TƯỜNG, HOÀN THIÊN NỘI THẤT XEM BẢN VẼ THIẾT KẾ NỘI THẤT.

BÊN THỦ HƯỚNG (.....)

GIÁM ĐỐC: PHẠM THỊ NGUYỄN TRANG
CHỦ ĐẦU TƯ (CLIENT):

CÔNG TY TNHH MTV ĐẦU TƯ ĐỊA ỐC
THẢO ĐIỆN XANH

TƯ VẤN THIẾT KẾ (LEAD CONSULTANT):
IAM ARCHITECTS
CÔNG TY CỔ PHẦN KIẾN TRÚC
3F - 47G HOÀ HỒNG - PHƯỜNG 2
QUẬN PHÚ NHUẬN - TP. HCM - VN
EMAIL: INFO@IAM.VN
WEBSITE: IAMA.VN



TỔNG GIÁM ĐỐC: NGUYỄN HOÀNG DŨNG
CÔNG TRÌNH (PROJECT):

BIS SCHOOL
242 NGUYỄN VĂN HƯỚNG
PHƯỜNG THẢO ĐIỆN, Q.2, TP. HCM

DỰ ÁN (PROJECT NO.): 18006


CHỦ TRÌ (MANAGED BY): KTS. NGÔ THÀNH VINH
THIẾT KẾ (DESIGNED BY): KS. NGUYỄN BẢO NĂNG
VẼ (DRAWN BY): KS. NGUYỄN BẢO NĂNG
KIỂM (CHECK BY): KTS. NGUYỄN NGỌC TOÀN
GIAI ĐOẠN (STAGE):
TÊN BẢN VẼ (DRAWING TITLE):

HIỆU CHỈNH (REVISION NO.):
KHỔ GIẤY (PAPER SIZE): A2
NGÀY PHÁT HÀNH (ISSUED DATE):
TỈ LỆ (DWG. SCALE):
SỐ BẢN VẼ (DRAWING NUMBER): ĐNH-06
© IAM Architects 2018

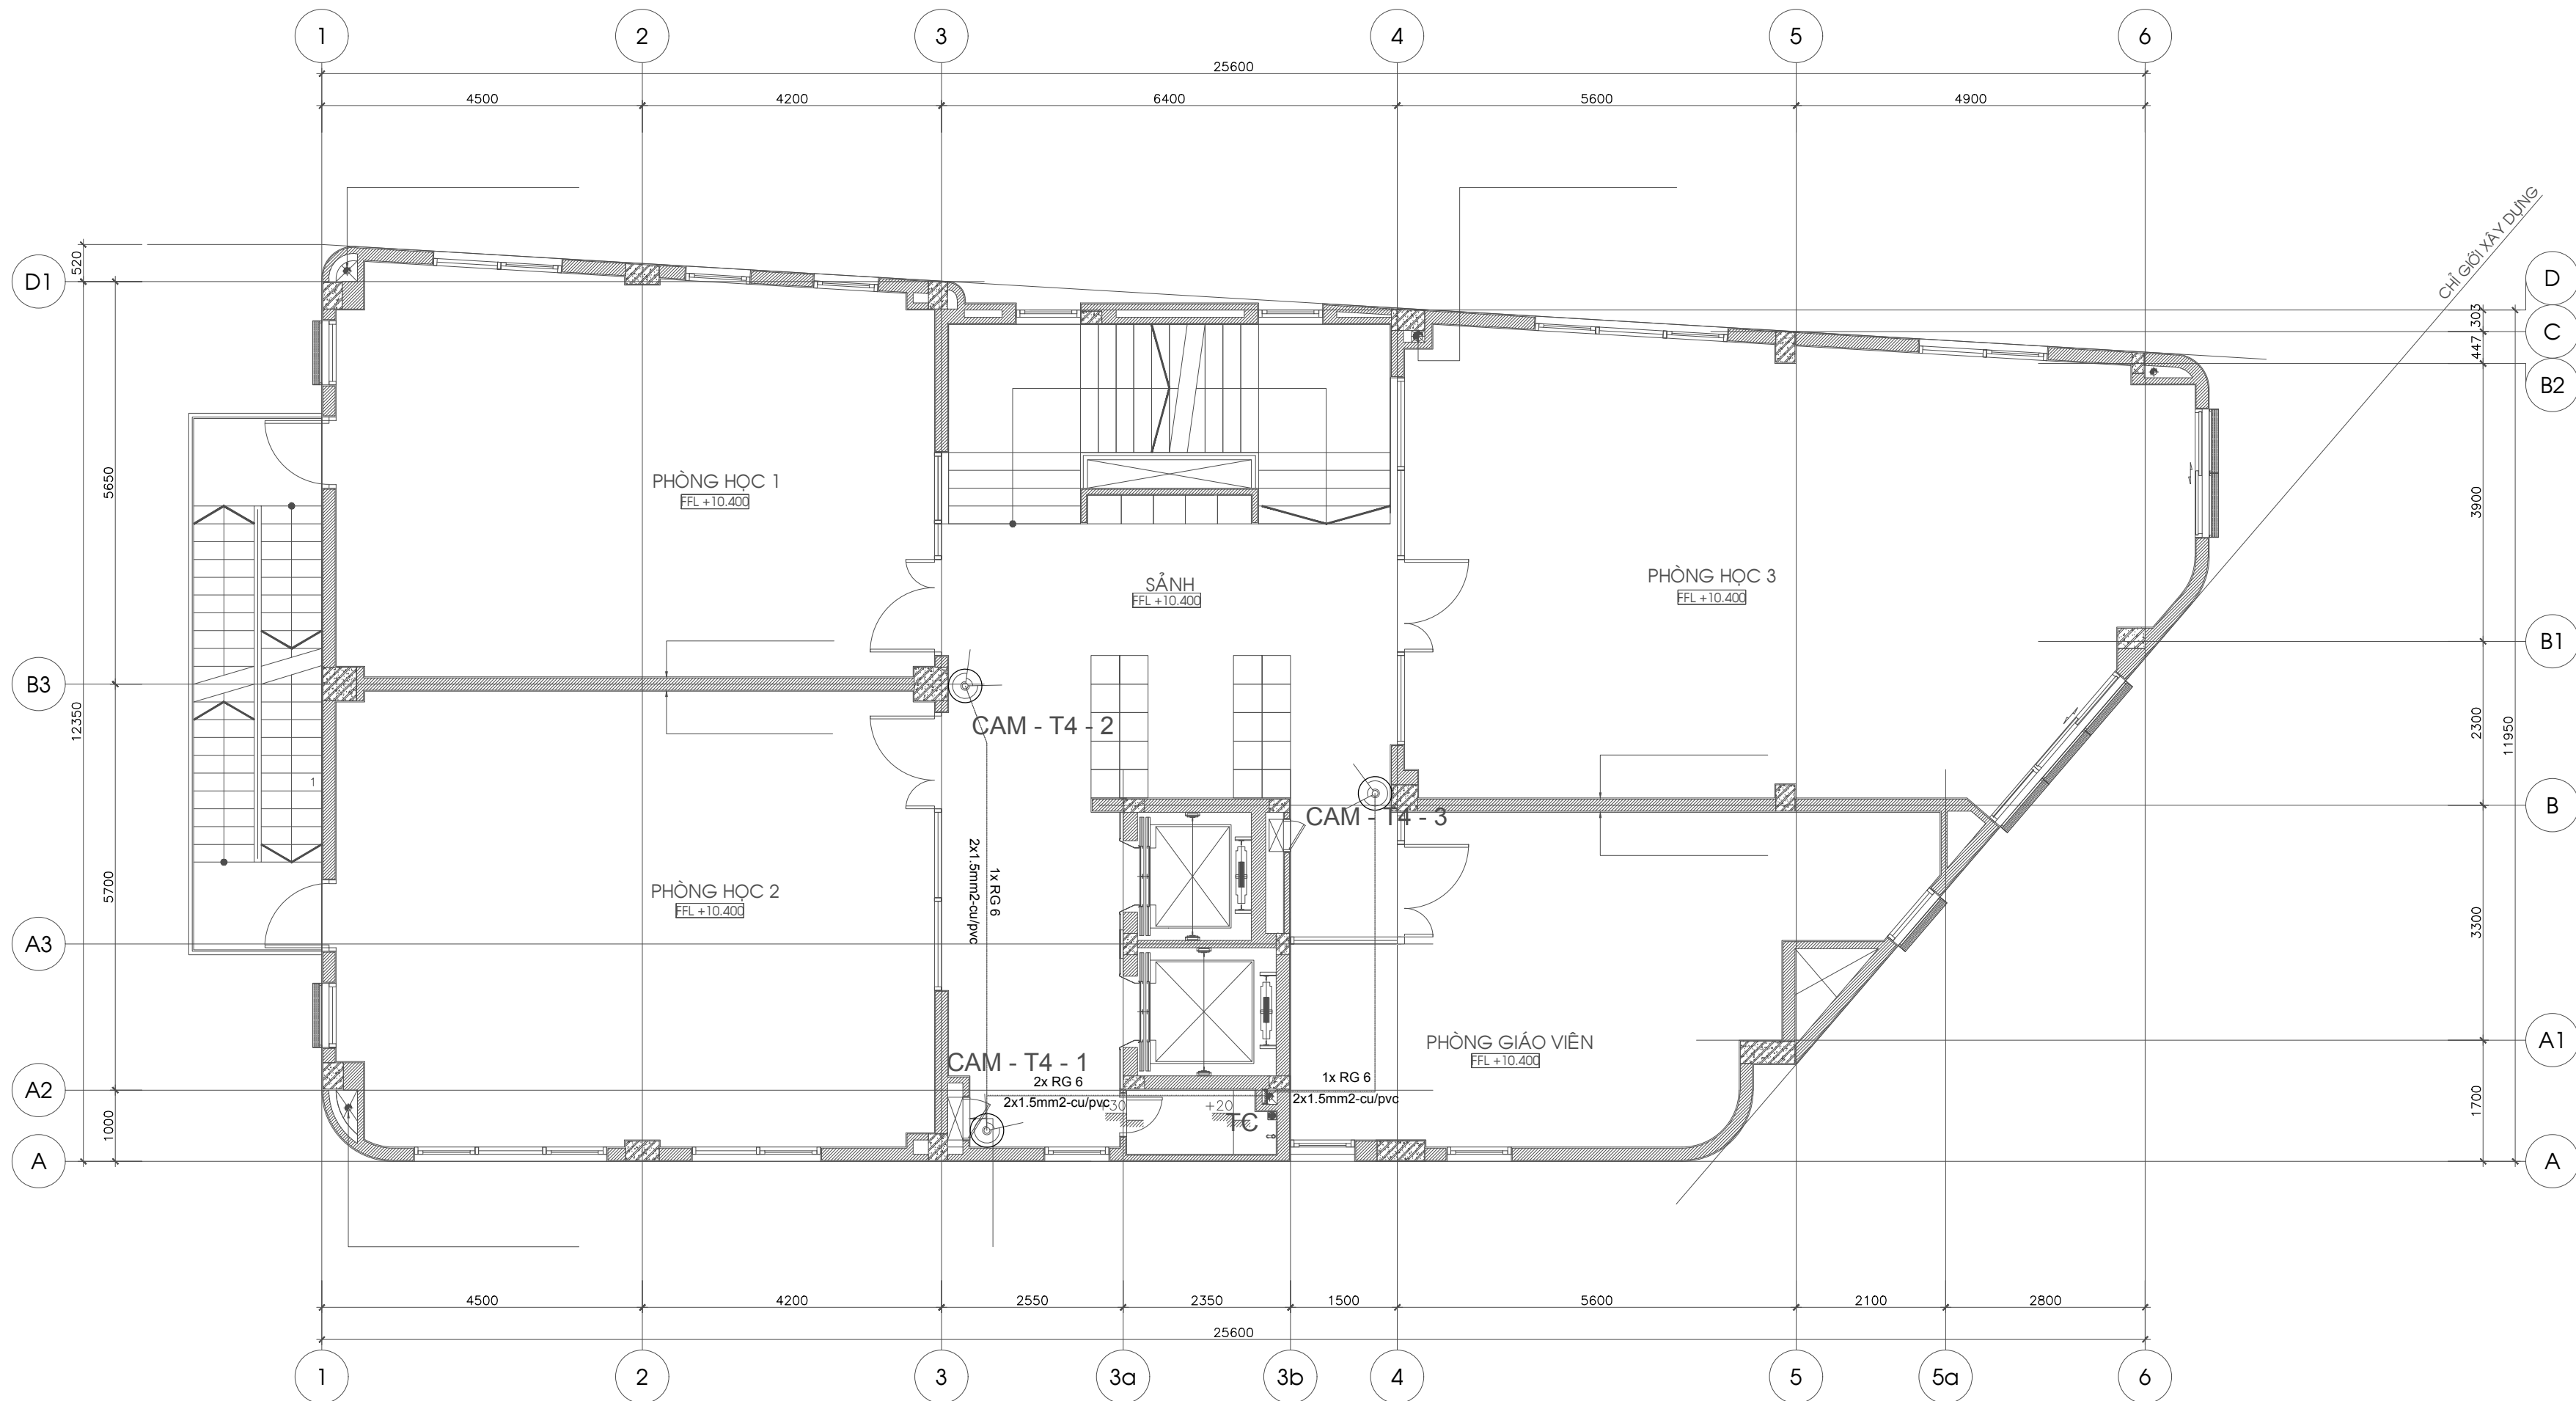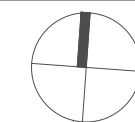

CHÚ THÍCH

KÝ HIỆU	TÊN VẬT TƯ THIẾT BỊ
	HỘP KỸ THUẬT 110x110x50
	CAMERA HỒNG NGOẠI HÌNH BÁN CẦU 2.0MP, 1/2.9" SONY IMX322 CMOS sensor, ống kính 4.0MM, HỒNG NGOẠI 15M
	CAMERA HỒNG NGOẠI HÌNH BÁN CẦU 2.0MP, LẮP TRONG THANG MÁY, 1/2.9" SONY IMX322 CMOS sensor, ống kính 2.8-12MM, HỒNG NGOẠI 15M
	CAMERA HỒNG NGOẠI NGOÀI TRỜI 2.0MP, 1/2.9" SONY IMX322 CMOS sensor, ống kính 4.0MM, HỒNG NGOẠI 25M, IP 66
	CÁP ĐỒNG TRỤC RG59
	DÂY CÁP NGUỒN Cu/PVC 2x1C-1.5mm

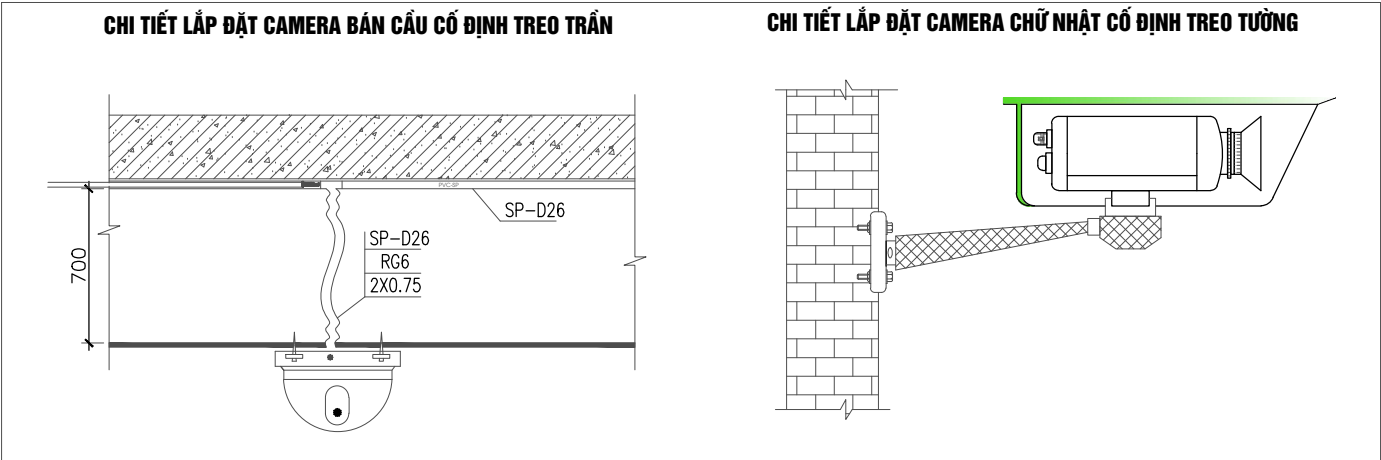

MẶT BẰNG BỐ TRÍ CAMERA TẦNG 4

CÁC BẢN VẼ KIẾN TRÚC ĐƯỢC CHUNG VỚI BẢN VẼ KẾT CẤU VÀ CƠ ĐIỆN LIÊN QUAN.
CÁC THÔNG TIN THUỘC VỀ KẾT CẤU VÀ CƠ ĐIỆN THỂ HIỆN TRÊN BẢN VẼ KIẾN TRÚC CHỈ ĐỂ THAM KHẢO.
BỐ TRÍ NỘI THẤT CHỈ MANG TÍNH THAM KHẢO, KỊCH THUỘC ĐỊNH VỊ TƯỜNG, HOÀN THIÊN NỘI THẤT XEM BẢN VẼ TRÊN KHAI NỘ THẤT.

BÊN THỦ HƯỚNG (.....)

GIÁM ĐỐC: PHẠM THỊ NGUYỄN TRANG

CHỦ ĐẦU TƯ (CLIENT)

CÔNG TY TNHH MTV ĐẦU TƯ ĐỊA ỐC
THẢO ĐIỀN XANH

TƯ VẤN THIẾT KẾ (LEAD CONSULTANT)

CÔNG TY CỔ PHẦN KIẾN TRÚC
IAM
IAMARCHITECTS
3F - 47G HOÀ HỒNG - PHƯỜNG 2
QUẬN PHÚ NHUẬN - TP. HCM - VN
EMAIL: INFO@IAM.VN
WEBSITE: IAMA.VN

TỔNG GIÁM ĐỐC: NGUYỄN HOÀNG DŨNG

CÔNG TRÌNH (PROJECT)

BIS SCHOOL
242 NGUYỄN VĂN HƯỚNG
PHƯỜNG THẢO ĐIỀN, Q.2, TP. HCM

DỰ ÁN (PROJECT NO.) 18006

CHỦ TRÌ (MANAGED BY) KTS. NGÔ THÀNH VINH

THIẾT KẾ (DESIGNED BY) KS. NGUYỄN BẢO NĂNG

VẼ (DRAWN BY) KS. NGUYỄN BẢO NĂNG

KIỂM (CHECK BY) KTS. NGUYỄN NGỌC TOÀN

GIẢI ĐOẠN (STAGE)

TÊN BẢN VẼ (DRAWING TITLE)

HIỆU CHỈNH (REVISION NO.)

KHỔ GIẤY (PAPER SIZE) A2



NGÀY PHÁT HÀNH (ISSUED DATE)

TỈ LỆ (DWG. SCALE)

SỐ BẢN VẼ (DRAWING NUMBER)


ĐNH-07

© IAM Architects 2018

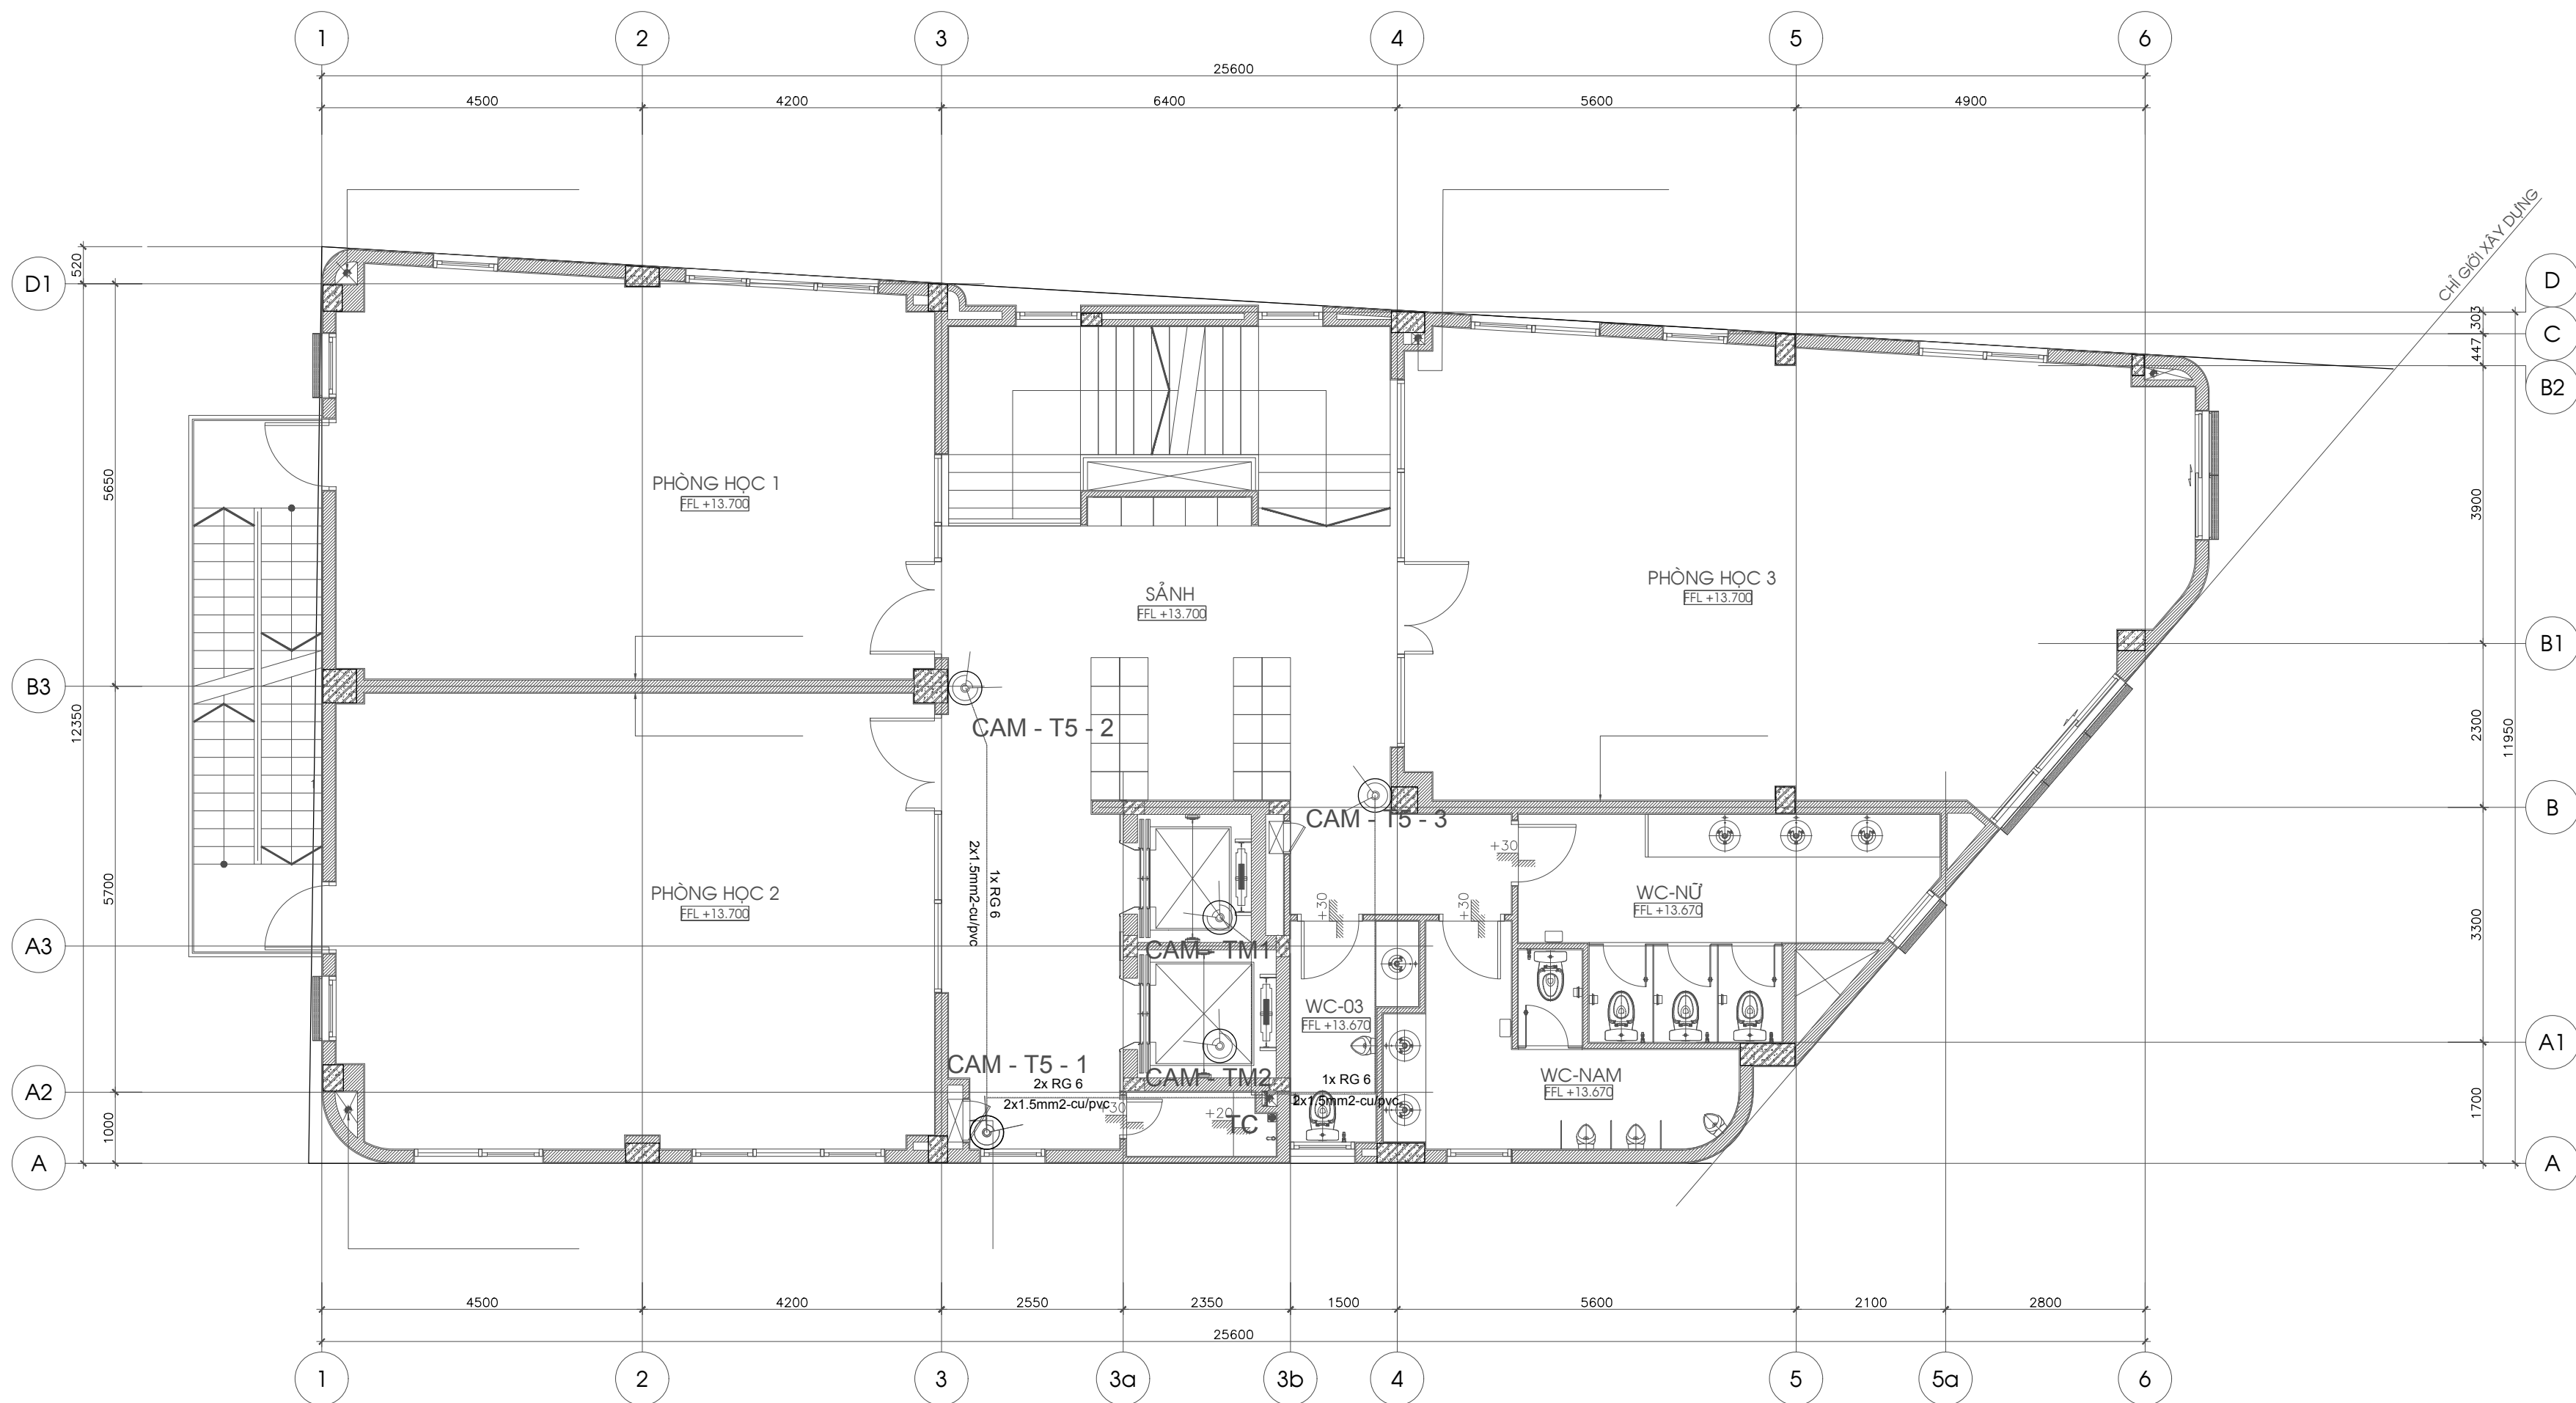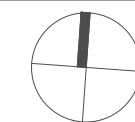

CHÚ THÍCH

KÝ HIỆU	TÊN VẬT TƯ THIẾT BỊ
	HỘP KỸ THUẬT 110x110x50
	CAMERA HỒNG NGOẠI HÌNH BÁN CẦU 2.0MP, 1/2.9" SONY IMX322 CMOS sensor, ống kính 4.0MM, HỒNG NGOẠI 15M
	CAMERA HỒNG NGOẠI HÌNH BÁN CẦU 2.0MP, LẮP TRONG THANG MÁY, 1/2.9" SONY IMX322 CMOS sensor, ống kính 2.8-12MM, HỒNG NGOẠI 15M
	CAMERA HỒNG NGOẠI NGOÀI TRỜI 2.0MP, 1/2.9" SONY IMX322 CMOS sensor, ống kính 4.0MM, HỒNG NGOẠI 25M, IP 66
	CÁP ĐỒNG TRỤC RG59
	DÂY CÁP NGUỒN Cu/PVC 2x1C-1.5mm

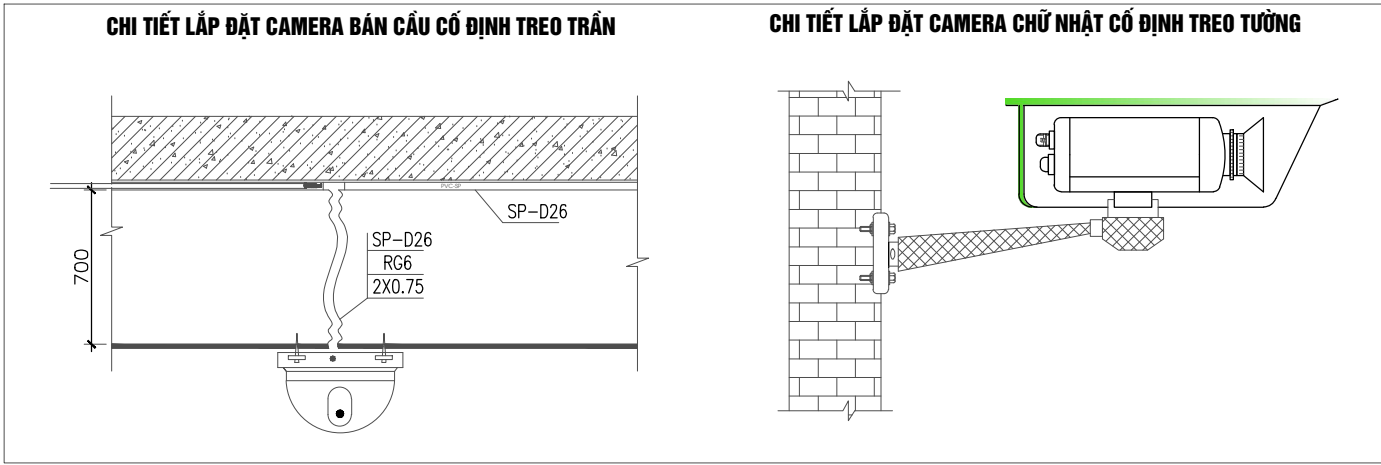

MẶT BẰNG BỐ TRÍ CAMERA TẦNG 5

CÁC BẢN VẼ KIẾN TRÚC ĐƯỢC CHUNG VỚI BẢN VẼ KẾT CẤU VÀ CƠ ĐIỆN LIÊN QUAN.
CÁC THÔNG TIN THUỘC VỀ KẾT CẤU VÀ CƠ ĐIỆN THỂ HIỆN TRÊN BẢN VẼ KIẾN TRÚC CHỈ ĐỂ THAM KHẢO.
BỐ TRÍ NỘI THẤT CHỈ MANG TÍNH THAM KHẢO, KỊCH THUỘC ĐỊNH VỊ TƯỜNG, HOÀN THIÊN NỘI THẤT XEM BẢN VẼ THIÊN KHAI NỘI THẤT.

BÊN THỦ HƯỚNG (.....)

GIÁM ĐỐC: PHẠM THỊ NGUYỄN TRANG

CHỦ ĐẦU TƯ (CLIENT)

CÔNG TY TNHH MTV ĐẦU TƯ ĐỊA ỐC
THẢO ĐIỆN XANH

TƯ VẤN THIẾT KẾ (LEAD CONSULTANT)

CÔNG TY CỔ PHẦN KIẾN TRÚC
IAM
IAMARCHITECTS
3F - 47G HOÀ HỒNG - PHƯỜNG 2
QUẬN PHÚ NHUẬN - TP. HCM - VN
EMAIL: INFO@IAM.VN
WEBSITE: IAMA.VN

TỔNG GIÁM ĐỐC: NGUYỄN HOÀNG DŨNG

CÔNG TRÌNH (PROJECT)

BIS SCHOOL
242 NGUYỄN VĂN HƯỚNG
PHƯỜNG THẢO ĐIỆN, Q.2, TP. HCM

DỰ ÁN (PROJECT NO.) 18006

CHỦ TRÌ (MANAGED BY) KTS. NGÔ THÀNH VINH

THIẾT KẾ (DESIGNED BY) KS. NGUYỄN BẢO NĂNG

VẼ (DRAWN BY) KS. NGUYỄN BẢO NĂNG

KIỂM (CHECK BY) KTS. NGUYỄN NGỌC TOÀN

GIẢI ĐOẠN (STAGE)

TÊN BẢN VẼ (DRAWING TITLE)

HIỆU CHỈNH (REVISION NO.)


KHỔ GIẤY (PAPER SIZE) NGÀY PHÁT HÀNH (ISSUED DATE)

A2

TỈ LỆ (DWG. SCALE) SỐ BẢN VẼ (DRAWING NUMBER)

ĐNH-08

© IAM Architects 2018

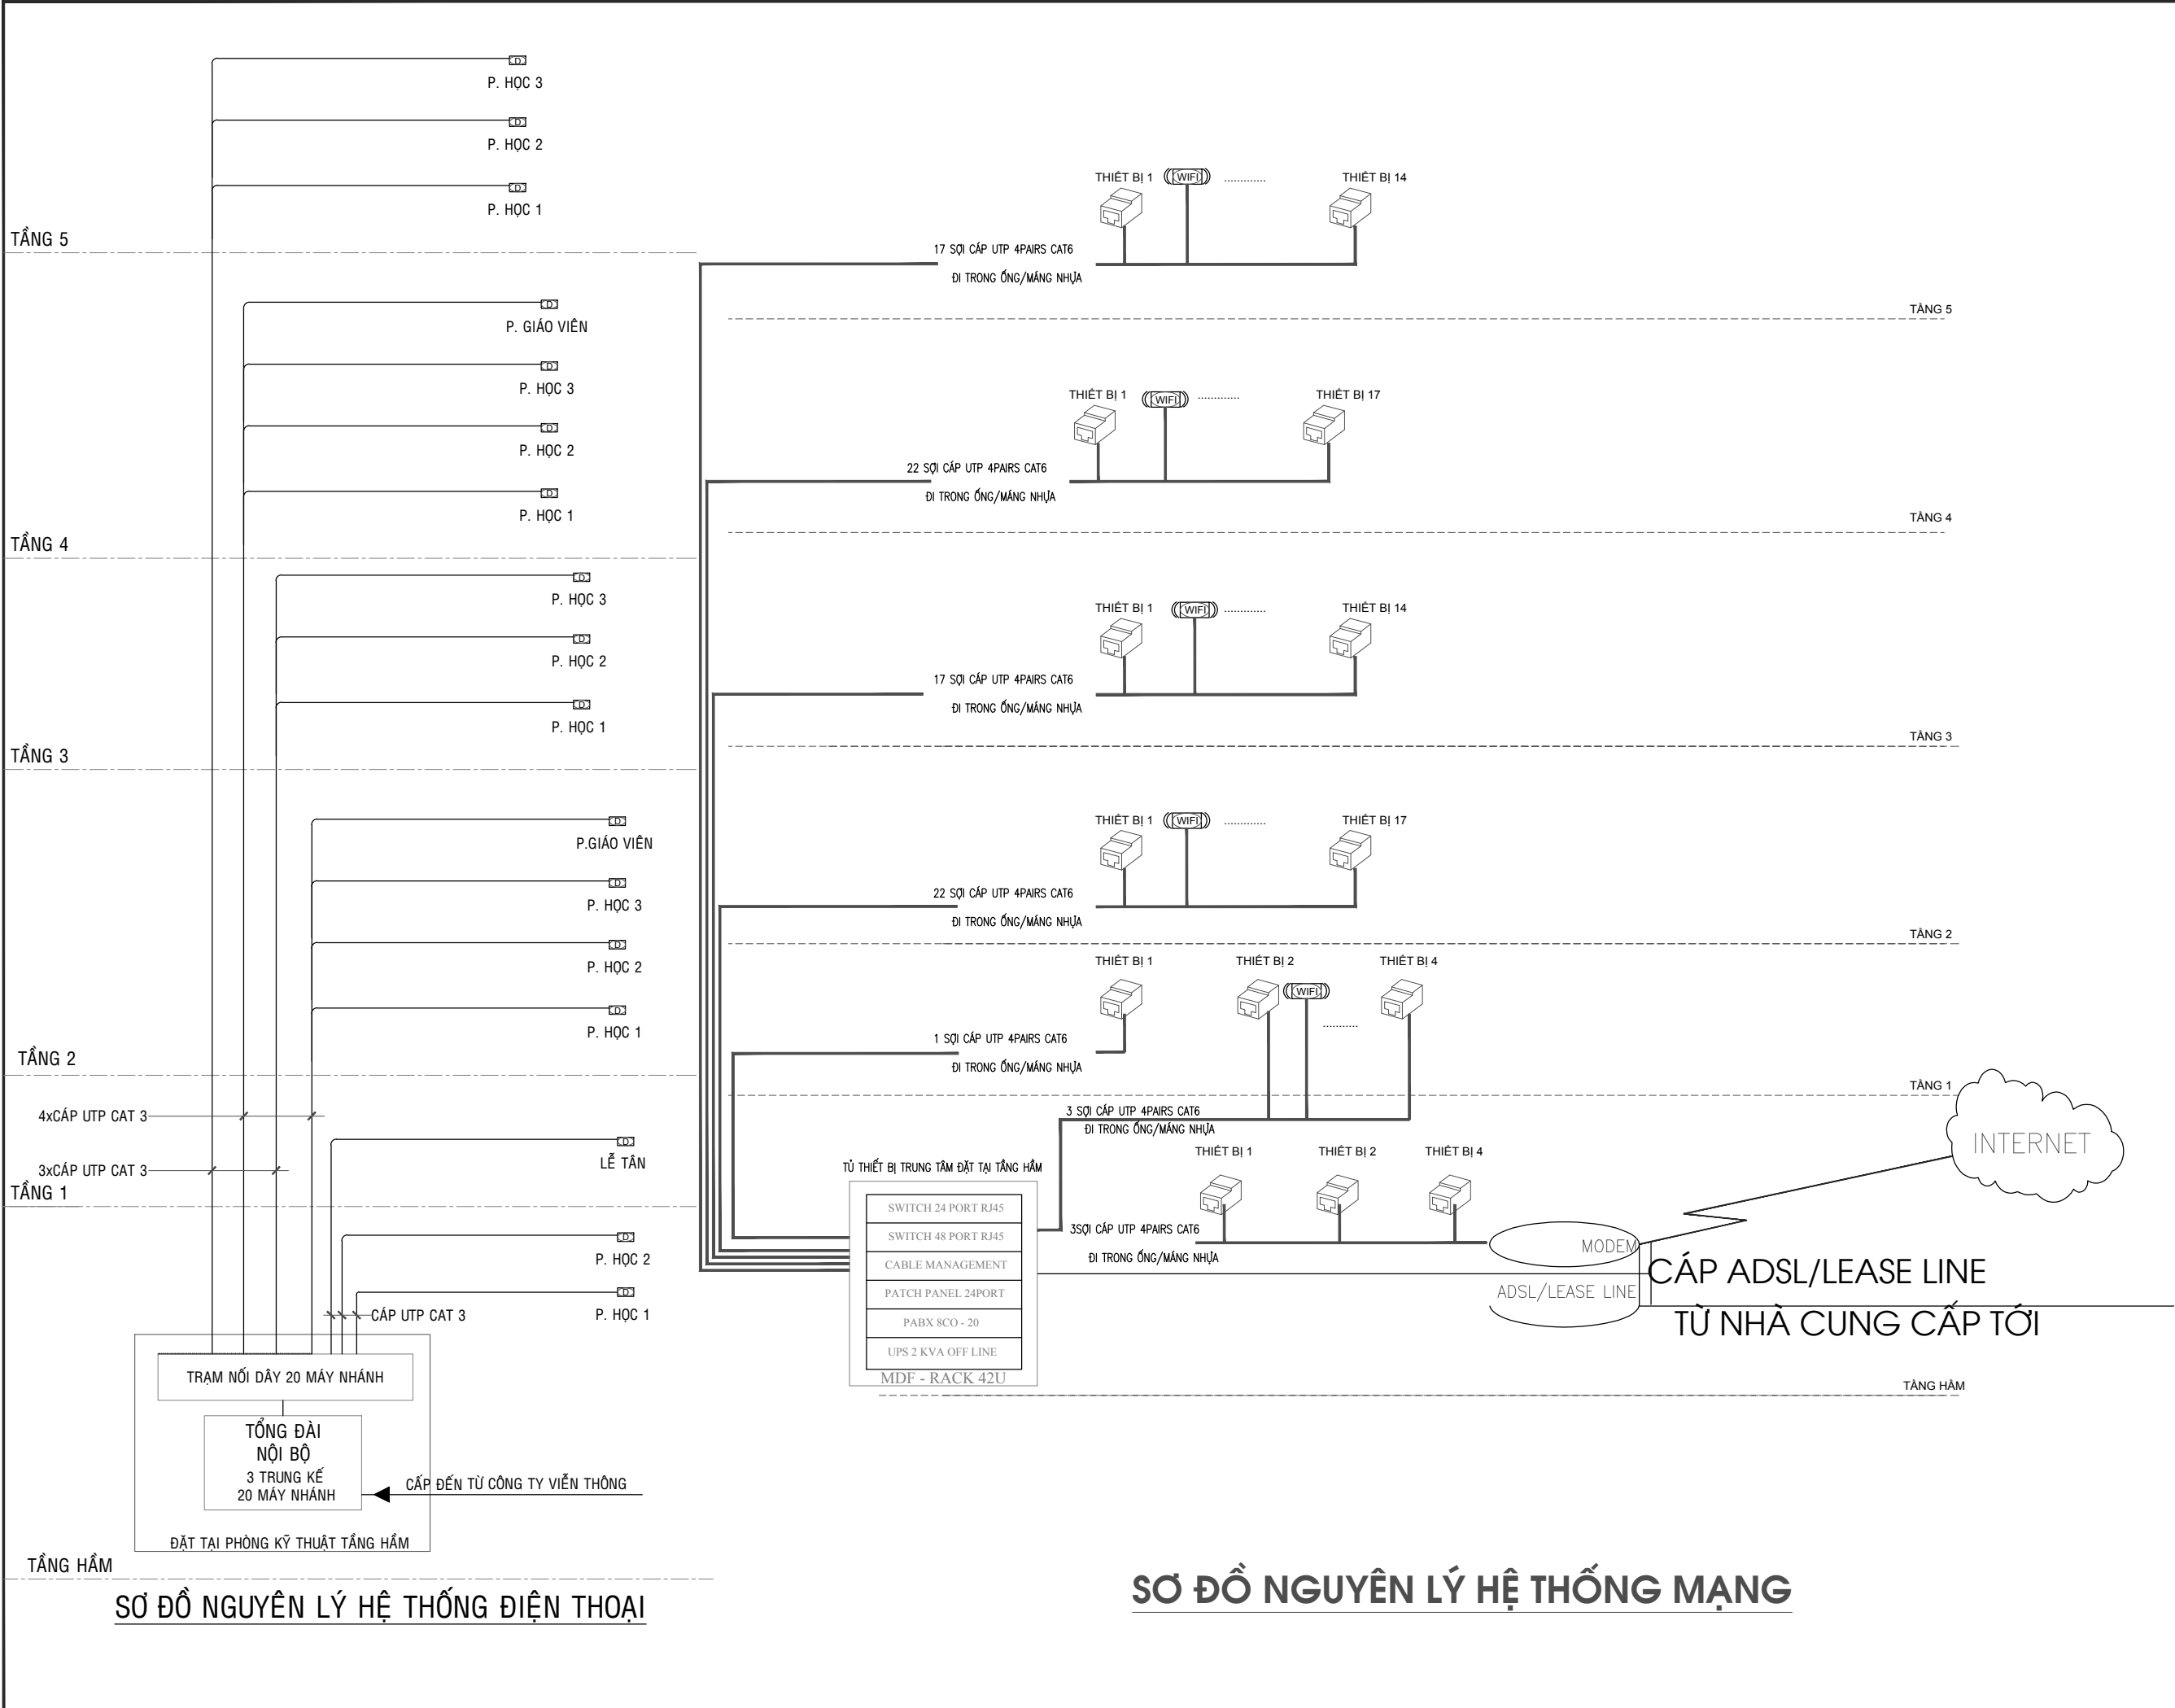

CÁC BẢN VẼ KIẾN TRÚC ĐƯỢC CHUNG VỚI BẢN VẼ KẾT CẤU VÀ CƠ ĐIỆN LIÊN QUAN.
CÁC THÔNG TIN THUỘC VỀ KẾT CẤU VÀ CƠ ĐIỆN THỂ HIỆN TRÊN BẢN VẼ KIẾN TRÚC CHỈ ĐỂ THAM KHẢO.
BỒ TRỢ NỘI THẤT CHỈ MANG TÍNH THAM KHẢO, KÍCH THƯỚC ĐỊNH VỊ TƯỜNG, HOÀN THIÊN NỘI THẤT XEM BẢN VẼ TRÊN KHAI NÓI THẬT.

BÊN THỤ HƯỚNG (-----)

GIÁM ĐỐC: PHẠM THỊ NGUYỄN TRANG

CHỦ ĐẦU TƯ (CLIENT)

CÔNG TY TNHH MTV ĐẦU TƯ ĐỊA ỐC
THẢO ĐIỀN XANH

TƯ VẤN THIẾT KẾ (LEAD CONSULTANT)

IAM CÔNG TY CỔ PHẦN KIẾN TRÚC
IAMARCHITECTS
3F - 47/6 HOÀ HỒNG - PHƯỜNG 2
QUẬN PHÚ NHUẬN - TP. HCM - VN
EMAIL: INFO@IAM.VN
WEBSITE: IAM.VN

TỔNG GIÁM ĐỐC: NGUYỄN HOÀNG DŨNG

CÔNG TRÌNH (PROJECT)

BIS SCHOOL
242 NGUYỄN VĂN HƯỜNG
PHƯỜNG THẢO ĐIỀN, Q.2, TP. HCM

DỰ ÁN (PROJECT NO.) 18006

CHỦ TRÌ (MANAGED BY) KTS. NGŨ THÀNH VINH

THIẾT KẾ (DESIGNED BY) KS. NGUYỄN BẢO NĂNG

VẼ (DRAWN BY) KS. NGUYỄN BẢO NĂNG

KIỂM (CHECK BY) KTS. NGUYỄN NGỌC TOÀN

GIẢI ĐOẠN (STAGE)

TÊN BẢN VẼ (DRAWING TITLE)

HIỆU CHỈNH (REVISION NO.)


KHỔ GIẤY (PAPER SIZE) NGÀY PHÁT HÀNH (ISSUED DATE)

A2

TỈ LỆ (DWG. SCALE) SỐ BẢN VẼ (DRAWING NUMBER)

ĐNH-09

© IAM Architects 2018

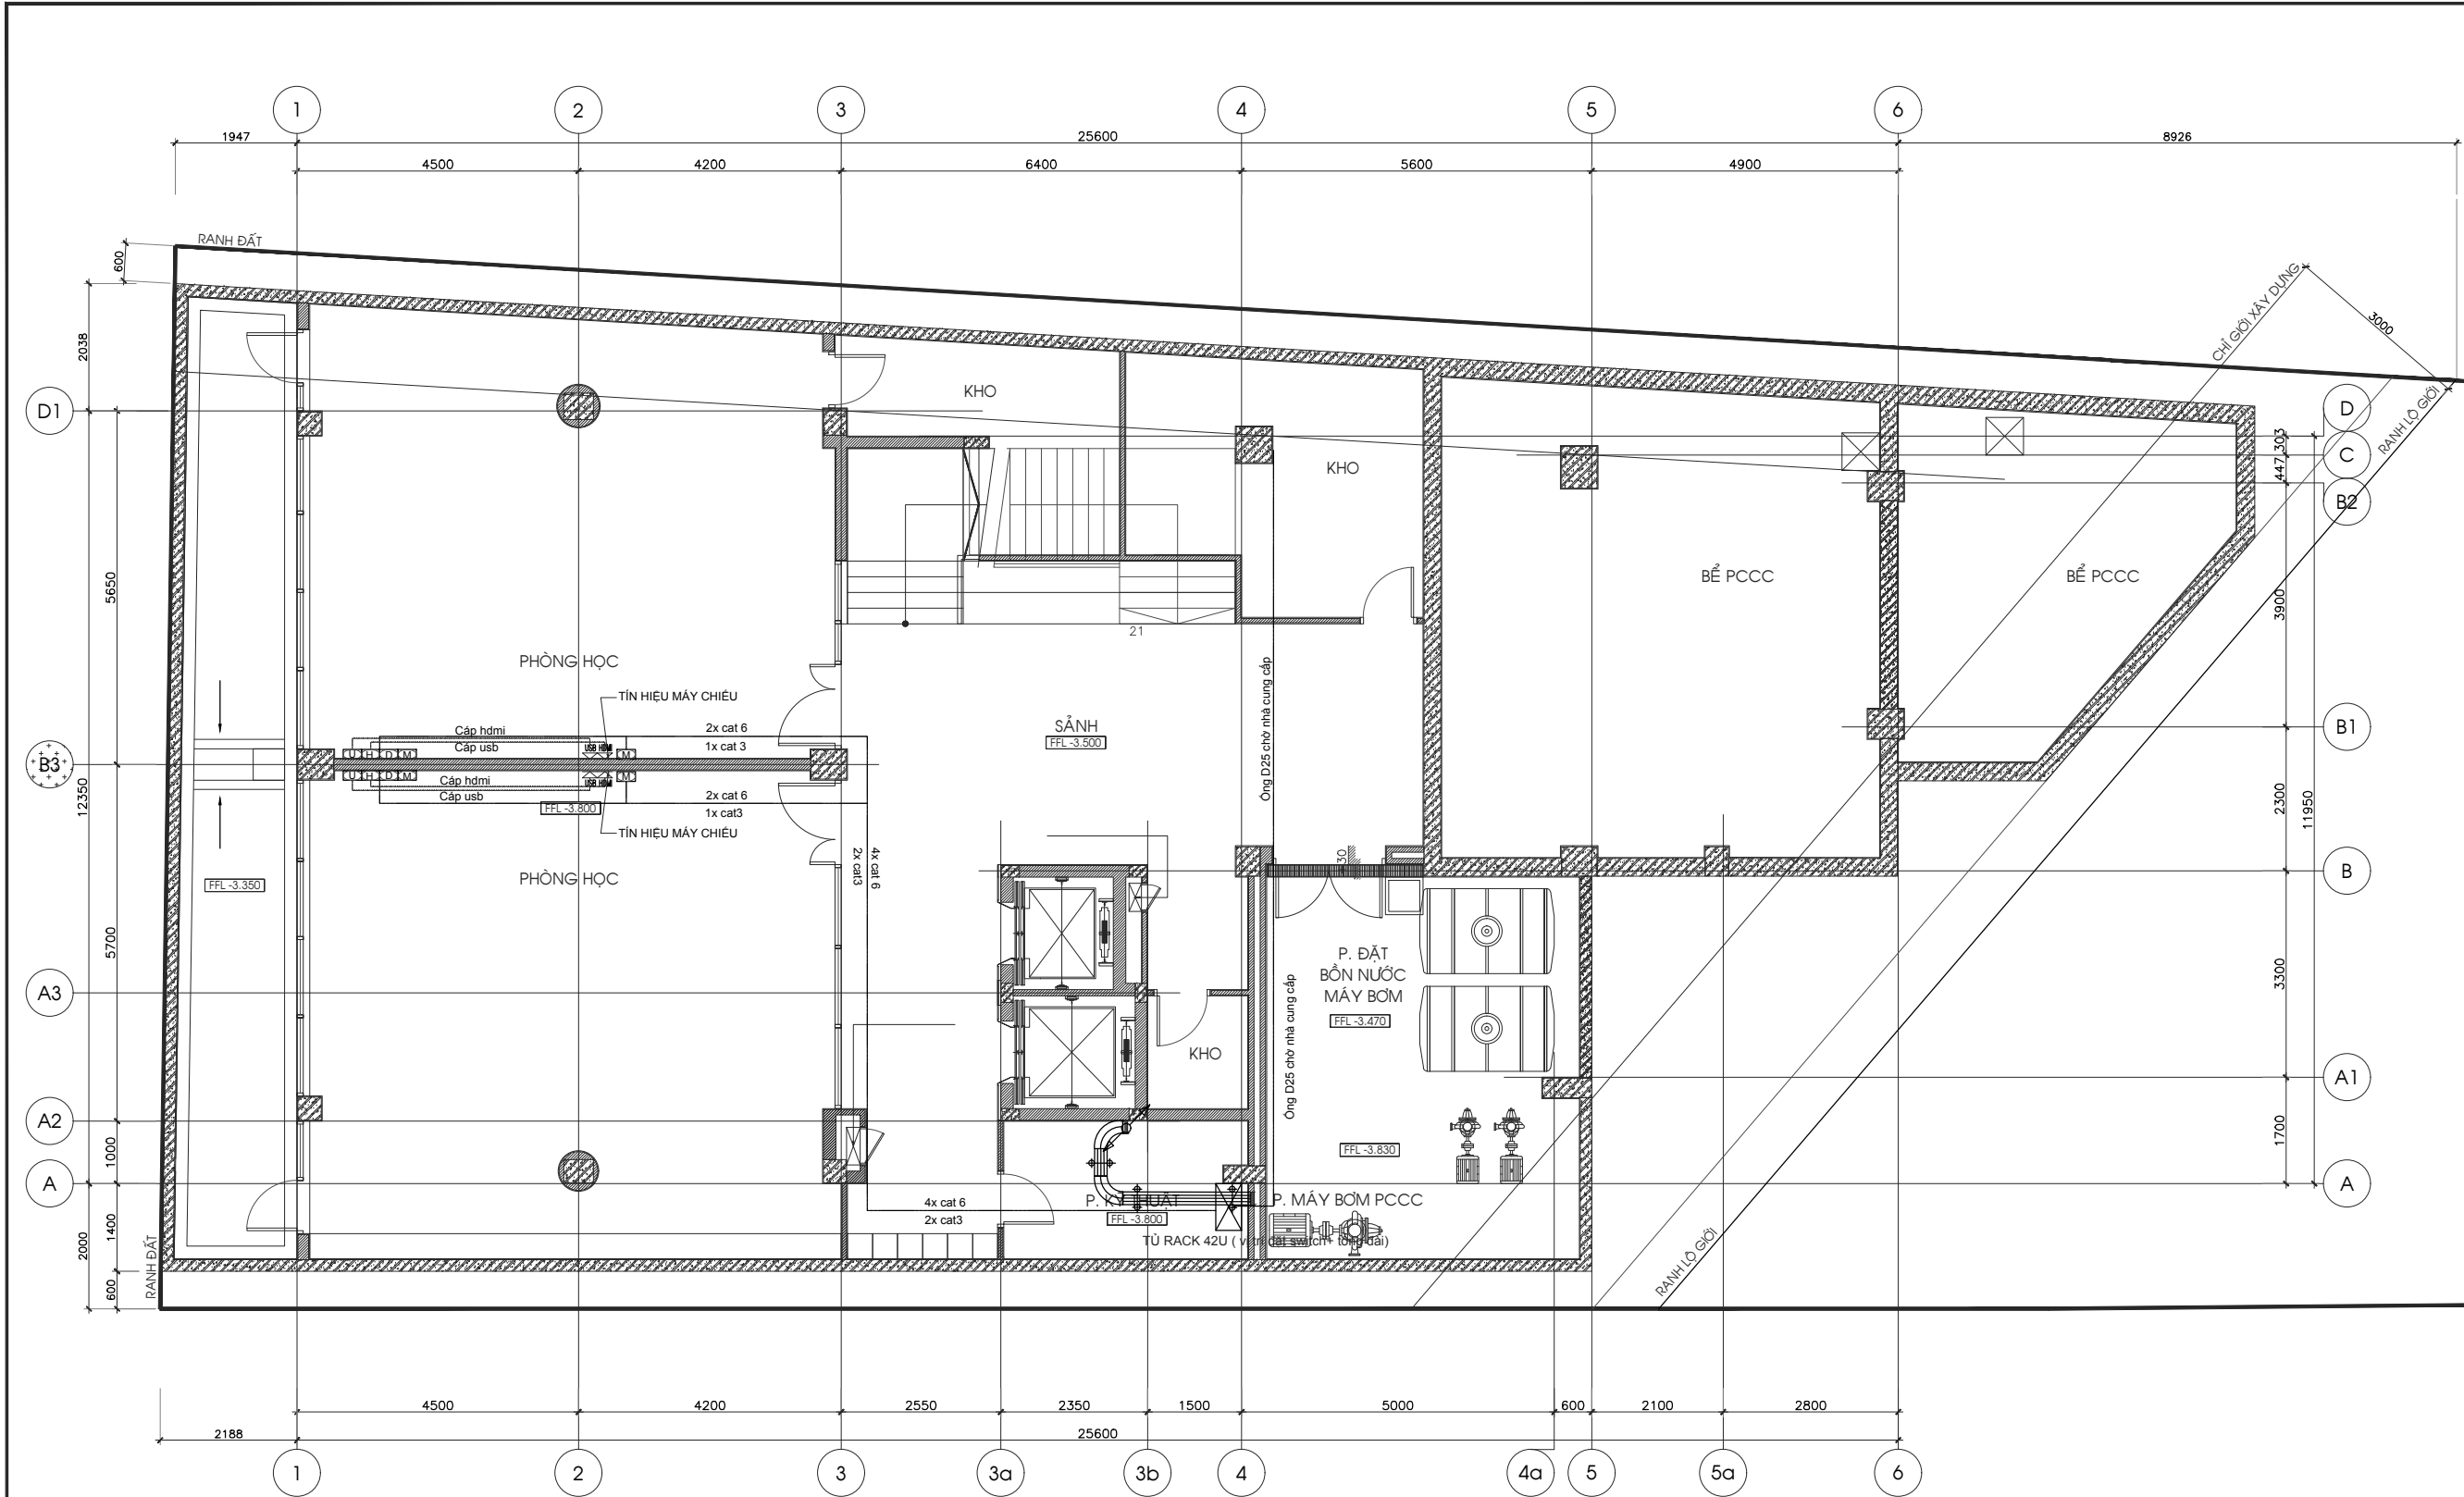

KÝ HIỆU	MÔ TẢ	KÝ HIỆU	MÔ TẢ
	MĂNG CÁP GA 100 ĐI NGOÀI HÀNH LANG		HỘP KỸ THUẬT TẮNG MẠNG TRUYỀN HÌNH
	VỊ TRÍ CÁP ĐI LÊN, XUỐNG		TỦ KỸ THUẬT TẮNG MẠNG MÂY TÍNH, ĐIỆN THOẠI VÀ DOORPHONE
	Ổ CẮM HDMI		HỘP KỸ THUẬT PHÒNG SƠN TÍNH ĐIỆN KÍCH THƯỚC 35X45X15CM
	Ổ MÁY TÍNH		Nx cat 6
	Ổ CẮM ĐIỆN THOẠI		THANG CÁP XUYÊN TẦNG
	Ổ CẮM USB		TOÀN BỘ Ổ ĐIỆN THOẠI TRONG PHÒNG HỌC CAO ĐỘ +400MM . VỊ TRÍ MÁY CHIẾU +2500MM GẮN TƯỜNG VỊ TRÍ BÀN GIÁO VIÊN +800MM, Ổ MẠNG HÀNH LANG LẮP TRÊN TRẦN
	ĐẦU RA CÁP HDMI CHỜ KẾT NỐI MÁY CHIẾU		
	ĐẦU RA CÁP USB CHỜ KẾT NỐI MÁY CHIẾU		

MẶT BẰNG BỐ TRÍ TH MẠNG TẦNG HÀM

CÁC BẢN VẼ KIẾN TRÚC ĐƯỢC CHUNG VỚI BẢN VẼ KẾT CẤU VÀ CƠ ĐIỆN LIÊN QUAN.
CÁC THÔNG TIN THUỘC VỀ KẾT CẤU VÀ CƠ ĐIỆN THỂ HIỆN TRÊN BẢN VẼ KIẾN TRÚC CHỈ ĐỂ THAM KHẢO.
BỐ TRÍ NỘI THẤT CHỈ MANG TÍNH THAM KHẢO, KỊCH THUỘC ĐÌNH VỊ TƯỜNG. HOÀN THIÊN NỘI THẤT XEM BẢN VẼ TRẦN KHAI NỘI THẤT.
BÊN THỤ HƯỚNG (-----)

GIÁM ĐỐC: PHẠM THỊ NGUYỄN TRANG
CHỦ ĐẦU TƯ (CLIENT):

CÔNG TY TNHH MTV ĐẦU TƯ ĐỊA ỐC
THẢO ĐIỀN XANH

TƯ VẤN THIẾT KẾ (LEAD CONSULTANT):
CÔNG TY CỔ PHẦN KIẾN TRÚC
IAM
IAMARCHITECTS
3F - 47/6 HOÀ HỒNG - PHƯỜNG 2
QUẬN PHÚ NHUẬN - TP. HCM - VN
EMAIL: INFO@IAM.VN
WEBSITE: IAM.VN

TỔNG GIÁM ĐỐC: NGUYỄN HOÀNG DŨNG
CÔNG TRÌNH (PROJECT):

BIS SCHOOL
242 NGUYỄN VĂN HƯỜNG
PHƯỜNG THẢO ĐIỀN, Q.2, TP. HCM

DỰ ÁN (PROJECT NO.): 18006

CHỦ TRƯ (MANAGED BY): KTS. NGŨ THÀNH VINH

THIẾT KẾ (DESIGNED BY): KS. NGUYỄN BẢO NĂNG

VẼ (DRAWN BY): KS. NGUYỄN BẢO NĂNG

KIỂM (CHECK BY): KTS. NGUYỄN NGỌC TOÀN

GIẢI ĐOẠN (STAGE):

TÊN BẢN VẼ (DRAWING TITLE):


HIỆU CHỈNH (REVISION NO.):

KHỔ GIẤY (PAPER SIZE): NGÀY PHÁT HÀNH (ISSUED DATE):

A2

TỈ LỆ (DWG. SCALE): SỐ BẢN VẼ (DRAWING NUMBER):

ĐNH-10

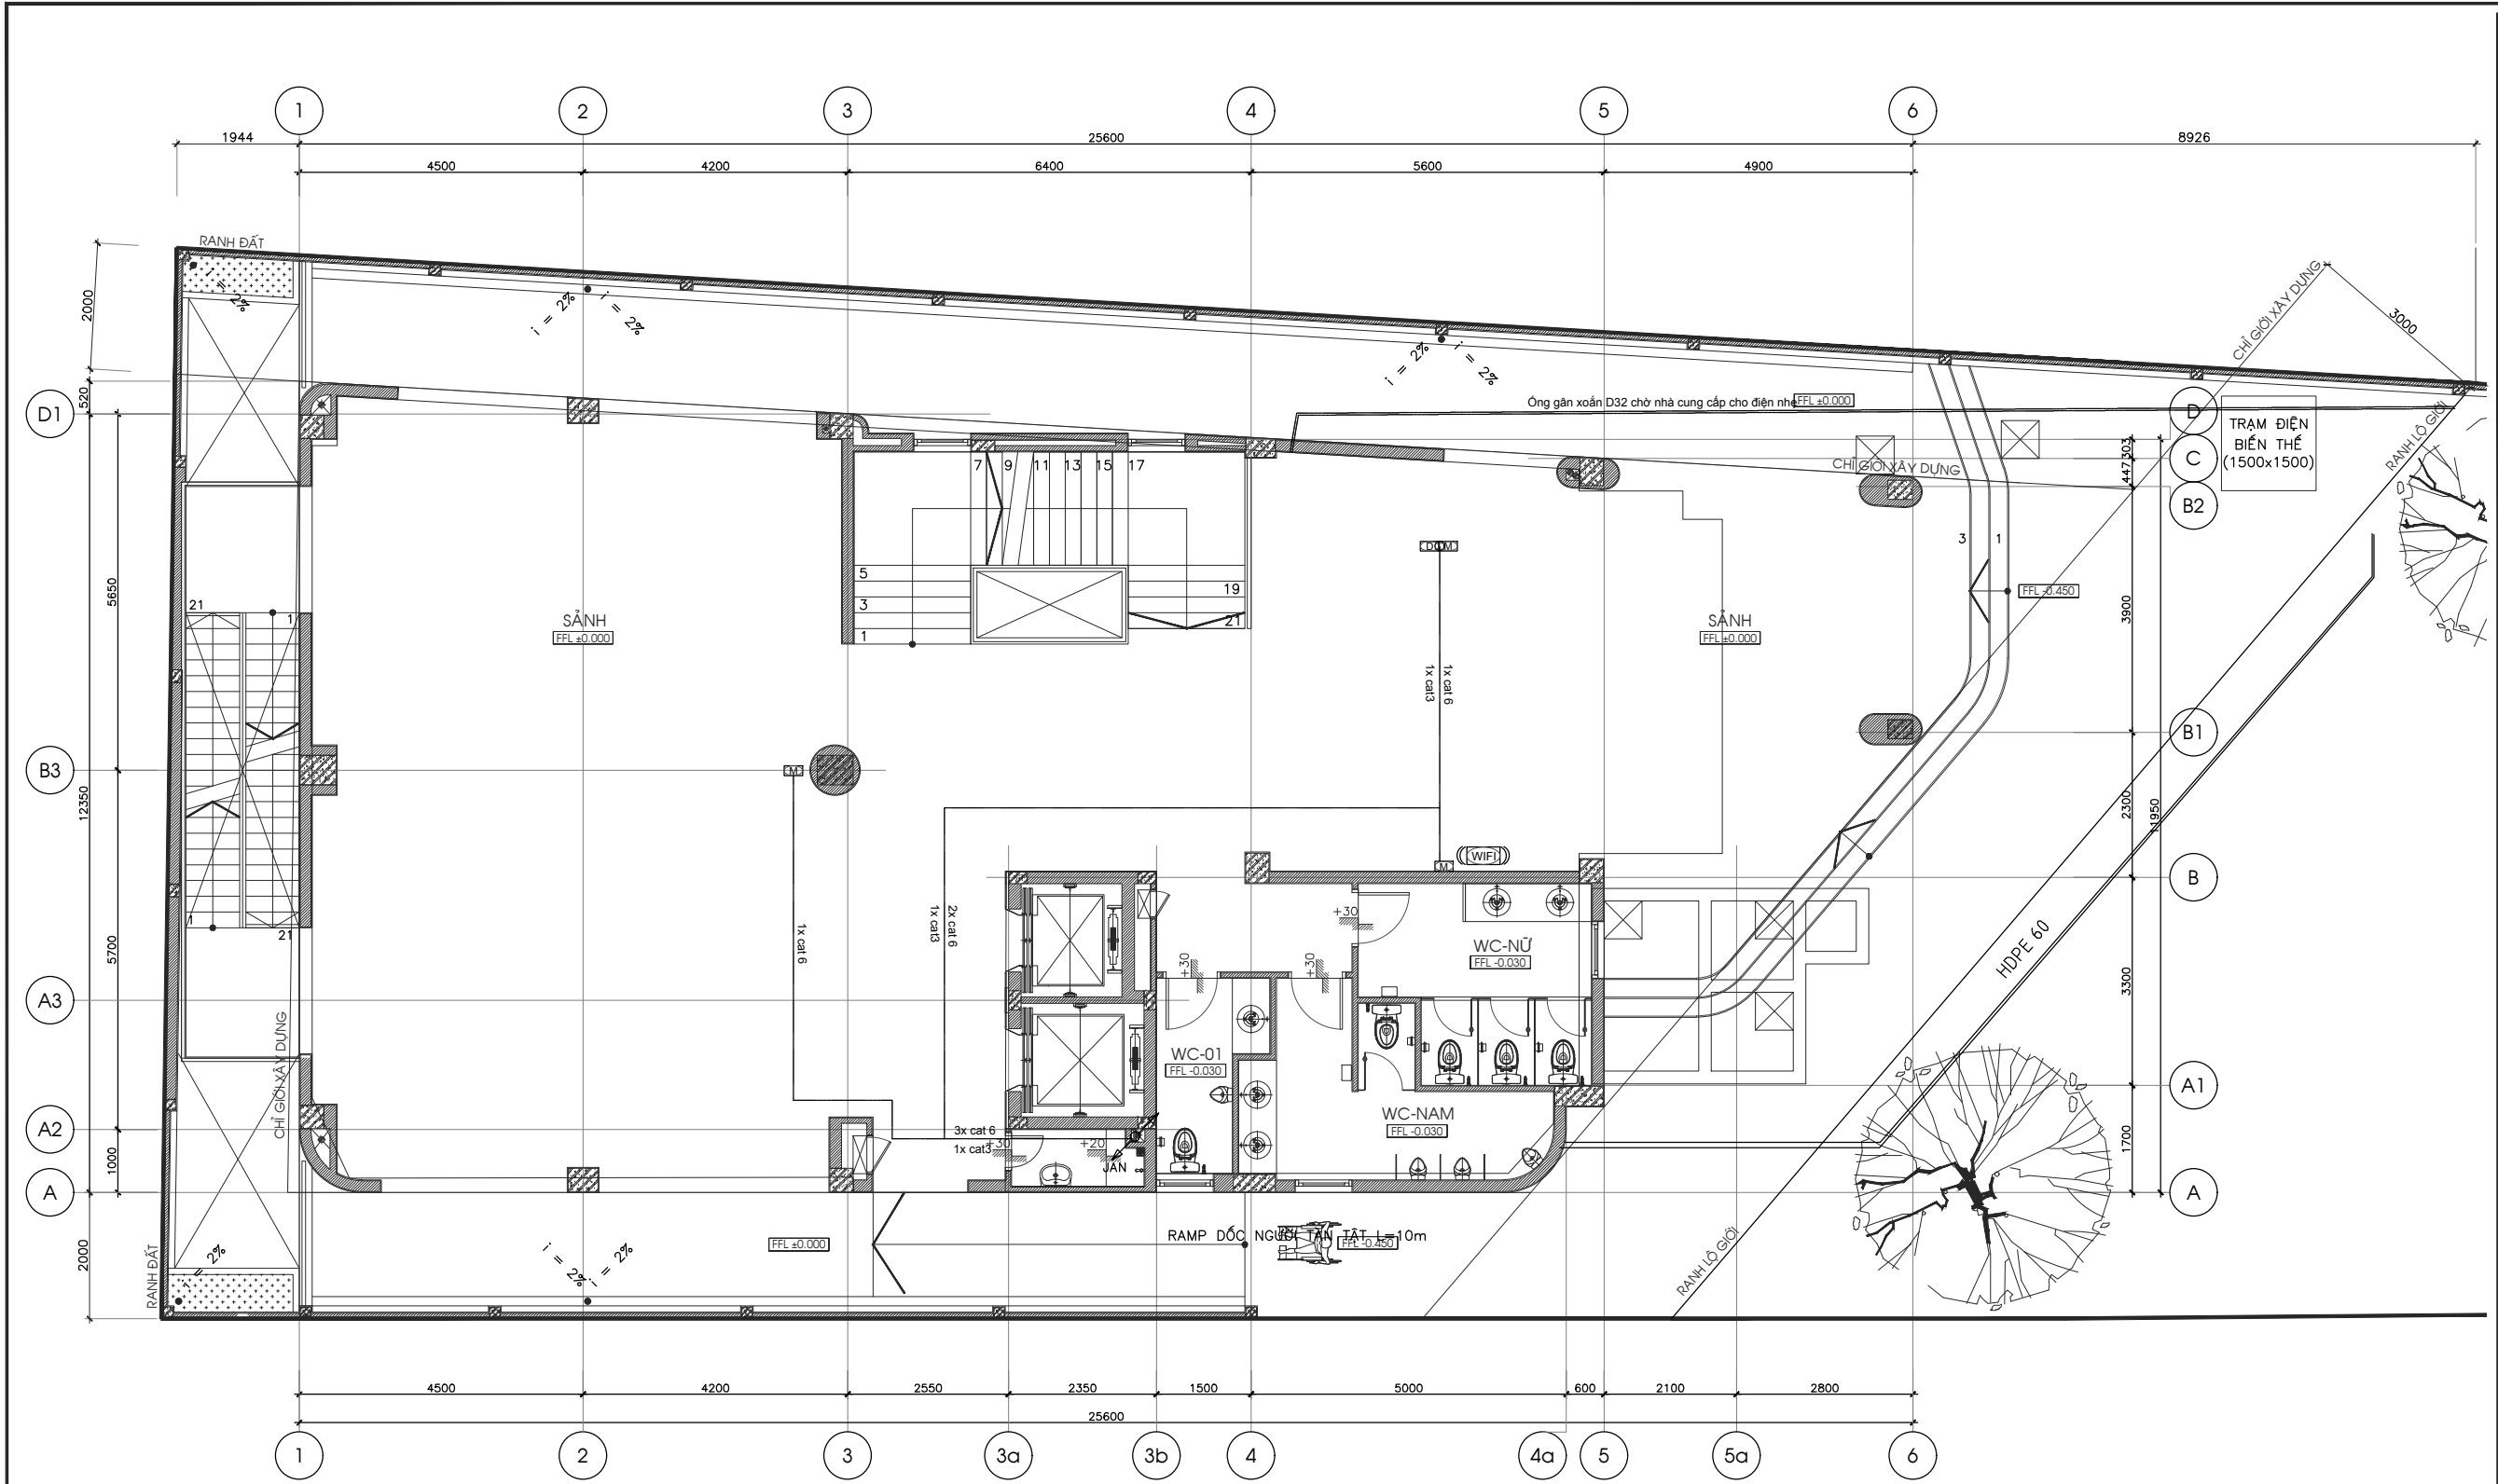

KÝ HIỆU	MÔ TẢ	KÝ HIỆU	MÔ TẢ
	MẢNG CÁP GA 100 ĐI NGOÀI HÀNH LANG		HỘP KỸ THUẬT TẮNG MẠNG TRUYỀN HÌNH
	VỊ TRÍ CÁP ĐI LÊN, XUỐNG		TỦ KỸ THUẬT TẮNG MẠNG MÂY TÍNH, ĐIỆN THOẠI VÀ DOORPHONE
	Ổ CẮM HDMI		HỘP KỸ THUẬT PHÒNG SƠN TÍNH ĐIỆN KÍCH THƯỚC 35X45X15CM
	Ổ MÂY TÍNH		N CÁP TRÊN TUYẾN
	Ổ CẮM ĐIỆN THOẠI		THANG CÁP XUYÊN TẦNG
	Ổ CẮM USB		TOÀN BỘ Ổ ĐIỆN THOẠI TRONG PHÒNG HỌC CAO ĐỘ +400MM . VỊ TRÍ MÂY CHIẾU +2500MM GẮN TƯỜNG VỊ TRÍ BÀN GIÁO VIÊN +800MM, Ổ MẠNG HÀNH LANG LẮP TRÊN TRẦN
	ĐẦU RA CÁP HDMI CHỜ KẾT NỐI MÂY CHIẾU		
	ĐẦU RA CÁP USB CHỜ KẾT NỐI MÂY CHIẾU		

MẶT BẰNG BỐ TRÍ Ổ CẮM TẦNG 1

GIÁM ĐỐC: PHẠM THỊ NGUYỄN TRANG

CHỦ ĐẦU TƯ (CLIENT): CÔNG TY TNHH MTV ĐẦU TƯ ĐÀO TẠO THẢO ĐIỀN XANH

THẢO ĐIỀN XANH

TƯ VẤN THIẾT KẾ (LEAD CONSULTANT): CÔNG TY CỔ PHẦN KIẾN TRÚC IAM

3F - 47/6 HOÀ HỒNG - PHƯỜNG 2, QUẬN PHÚ NHUẬN - TP. HCM - VN

EMAIL: INFO@IAM.VN, WEB: IAM.VN

TỔNG GIÁM ĐỐC: NGUYỄN HOÀNG DŨNG

CÔNG TRÌNH (PROJECT): BIS SCHOOL

242 NGUYỄN VĂN HƯỜNG, PHƯỜNG THẢO ĐIỀN, Q.2, TP. HCM

DỰ ÁN (PROJECT NO.): 18006

CHỦ TRƯ (MANAGED BY): KTS. NGŨ THÀNH VINH

THIẾT KẾ (DESIGNED BY): KTS. NGUYỄN BẢO NĂNG

VẼ (DRAWN BY): KTS. NGUYỄN BẢO NĂNG

KIỂM (CHECK BY): KTS. NGUYỄN NGỌC TOÀN

GIẢI ĐOẠN (STAGE):

TÊN BẢN VẼ (DRAWING TITLE):

HỒ CHỮ (REVISION NO.):

KHỔ GIẤY (PAPER SIZE): A2


TỈ LỆ (DWG. SCALE):

NGÀY PHÁT HÀNH (ISSUED DATE):

SỐ BẢN VẼ (DRAWING NUMBER): ĐNH-11

CÁC BẢN VẼ KIẾN TRÚC ĐƯỢC CHUNG VỚI BẢN VẼ KẾT CẤU VÀ CƠ ĐIỆN LIÊN QUAN. CÁC THÔNG TIN THUỘC VỀ KẾT CẤU VÀ CƠ ĐIỆN THỂ HIỆN TRÊN BẢN VẼ KIẾN TRÚC CHỈ ĐỂ THAM KHẢO. KỊCH THUỘC ĐÌNH VỊ TƯỜNG, HOÀN THIÊN NỘI THẤT XEM BẢN VẼ TRÊN KHAI NƠI THẤT. BÊN THU HƯỚNG (-----)

BẢN VẼ VÀ THIẾT KẾ NÀY THUỘC SỞ HỮU CỦA IAM ARCHITECTS KHÔNG SẠO CHÉP HOẶC SỬ DỤNG LẠI THÔNG TIN KH CHỊU ĐƯỢC SỬ DỤNG Y. TẤT CẢ CÁC KỊCH THUỘC TRÊN BẢN VẼ PHẢI ĐƯỢC KIỂM TRA THỰC TẾ TẠI CÔNG TRƯỜNG TRƯỚC KHI THI CÔNG.

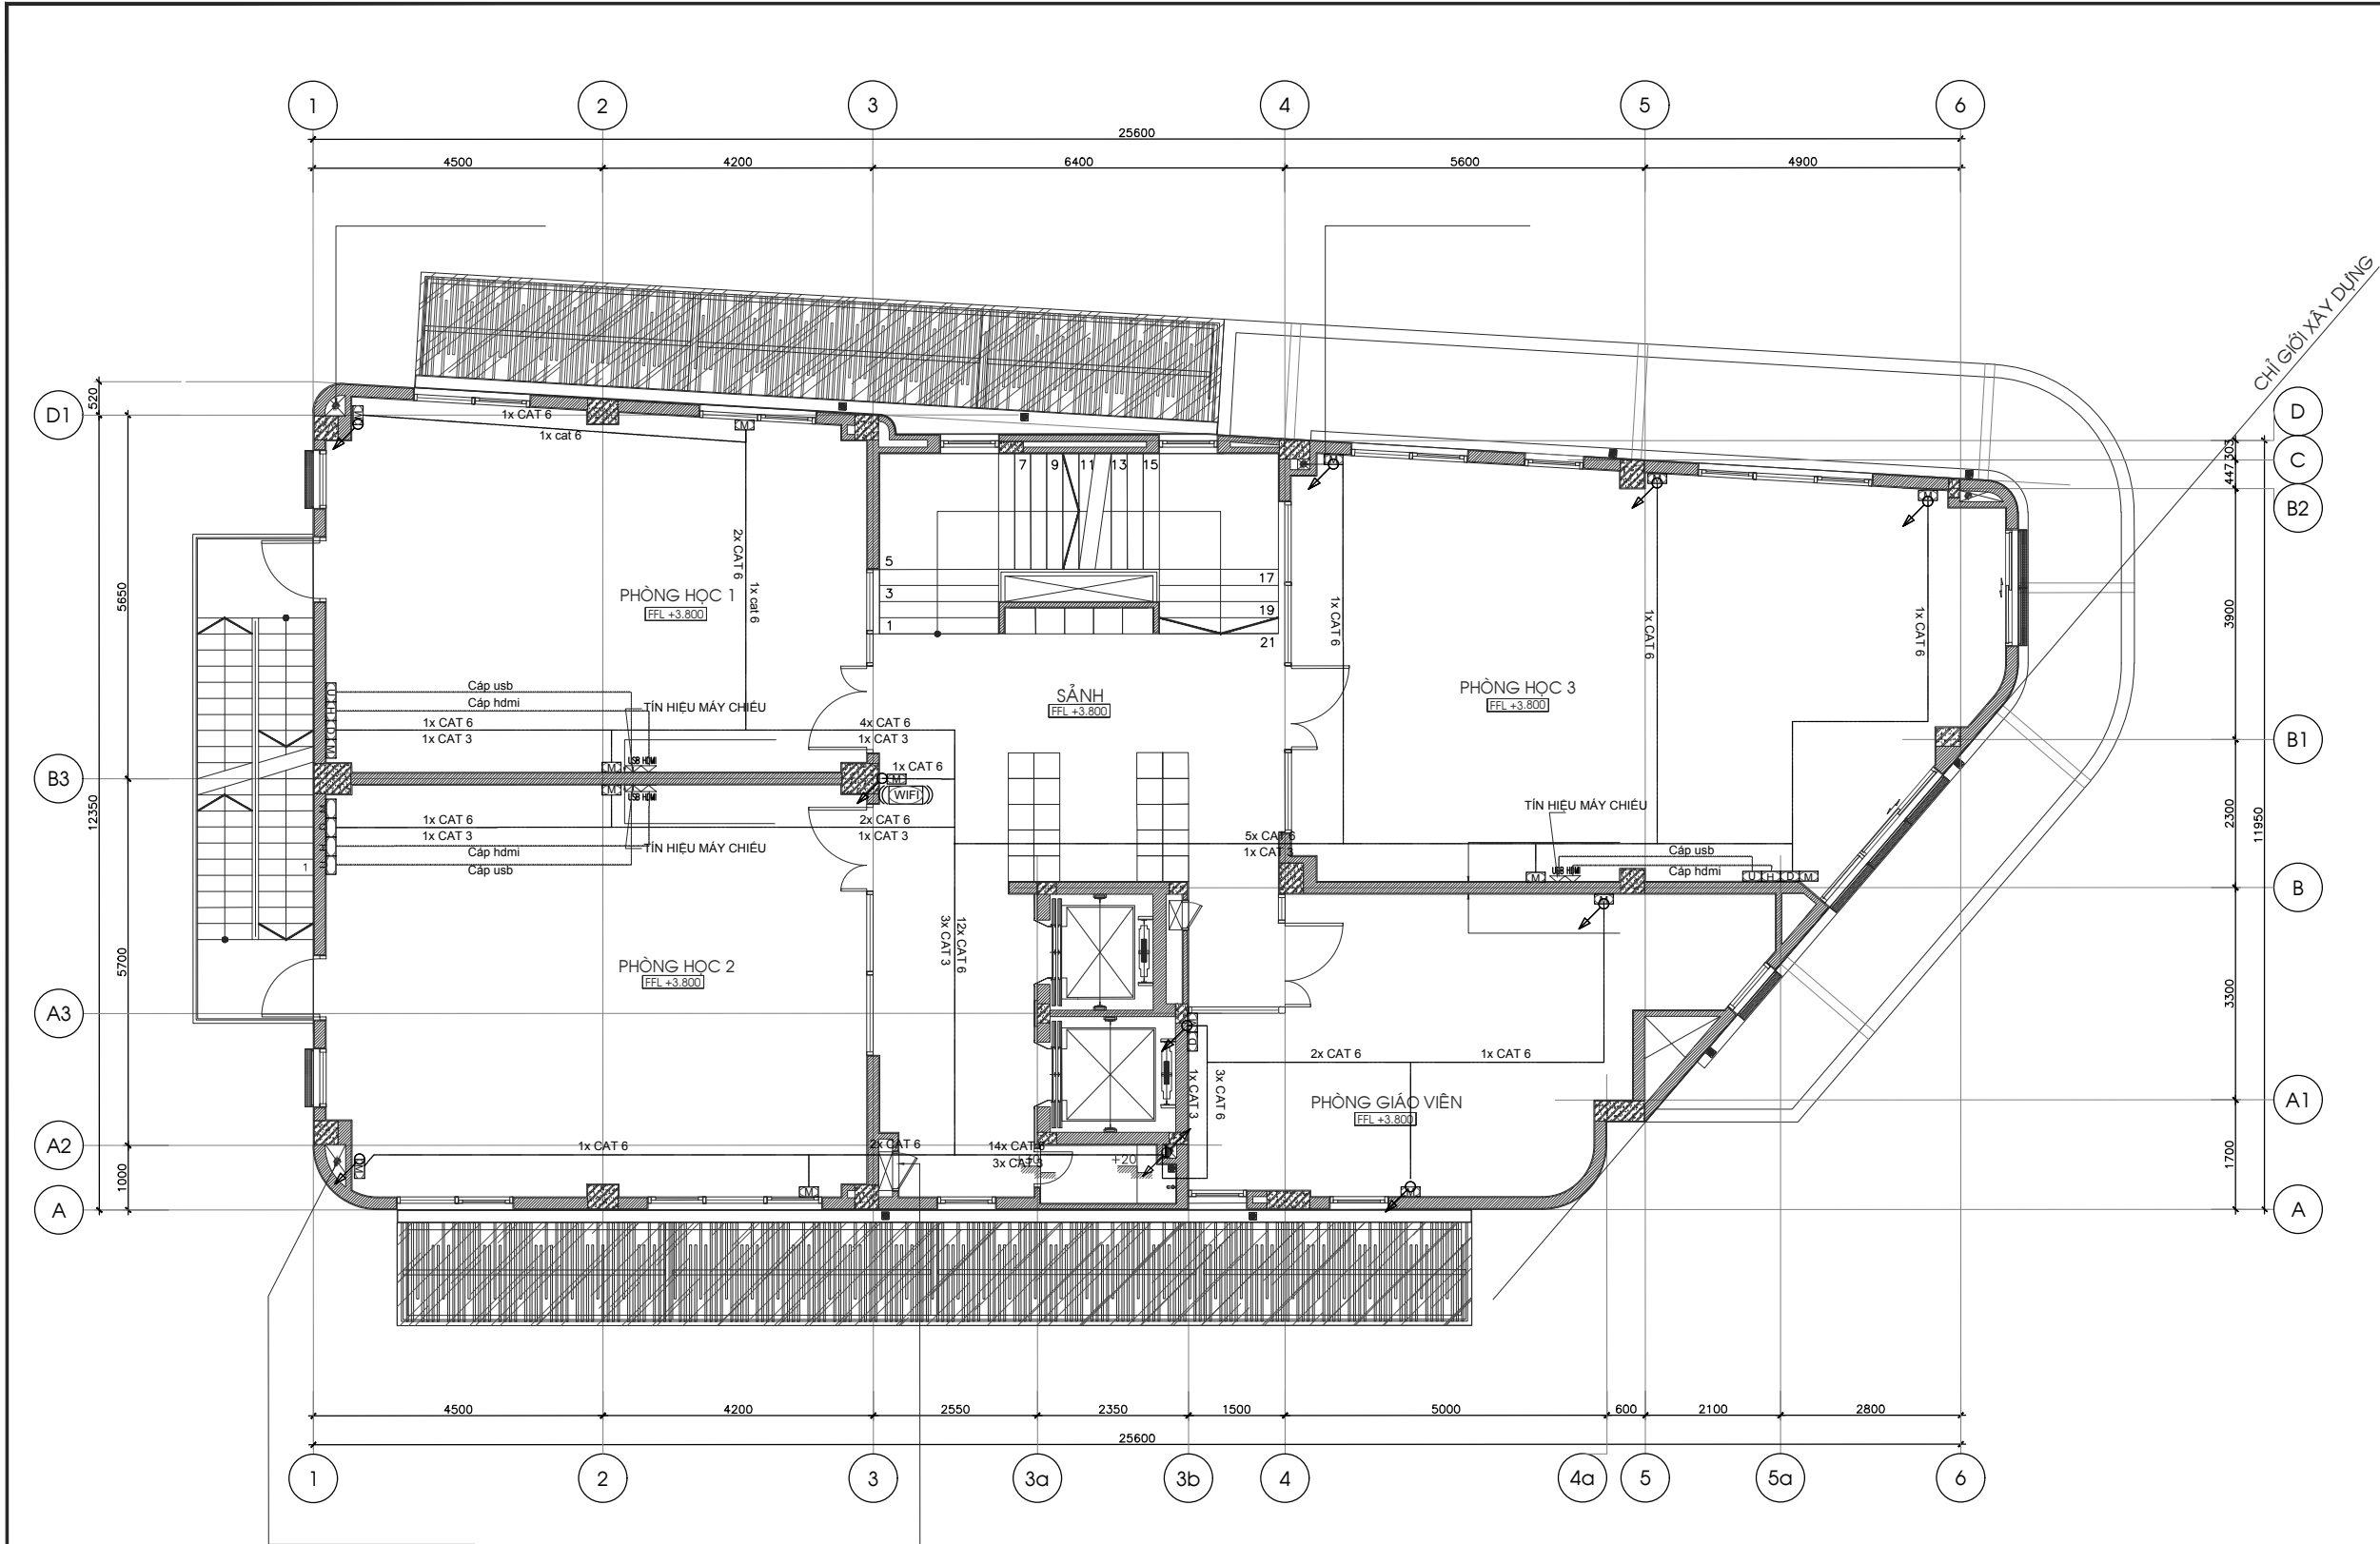

KÝ HIỆU	MÔ TẢ	KÝ HIỆU	MÔ TẢ
	MĂNG CÁP GA 100 ĐI NGOÀI HÀNH LANG		HỘP KỸ THUẬT TẮNG MẠNG TRUYỀN HÌNH
	VỊ TRÍ CÁP ĐI LÊN, XUỐNG		TỦ KỸ THUẬT TẮNG MẠNG MÂY TÍNH, ĐIỆN THOẠI VÀ DOORPHONE
	Ổ CẮM HDMI		HỘP KỸ THUẬT PHÒNG SƠN TÍNH ĐIỆN KÍCH THƯỚC 35X45X15CM
	Ổ MÁY TÍNH		N CÁP TRÊN TUYẾN
	Ổ CẮM ĐIỆN THOẠI		THANG CÁP XUYÊN TẦNG
	Ổ CẮM USB		TOÀN BỘ Ổ ĐIỆN THOẠI TRONG PHÒNG HỌC CAO ĐỘ +400MM , VỊ TRÍ MÁY CHIẾU +2500MM GẮN TƯỜNG
	ĐẦU RA CÁP HDMI CHỜ KẾT NỐI MÁY CHIẾU		VỊ TRÍ BÀN GIÁO VIÊN +800MM, Ổ MẠNG HÀNH LANG LẮP TRÊN TRẦN
	ĐẦU RA CÁP USB CHỜ KẾT NỐI MÁY CHIẾU		

MẶT BẰNG BỐ TRÍ HT MẠNG TẦNG 2

CÁC BẢN VẼ KIẾN TRÚC ĐƯỢC CHUNG VỚI BẢN VẼ KẾT CẤU VÀ CƠ ĐIỆN LIÊN QUAN.
CÁC THÔNG TIN THUỘC VỀ KẾT CẤU VÀ CƠ ĐIỆN THỂ HIỆN TRÊN BẢN VẼ KIẾN TRÚC CHỈ ĐỂ THAM KHẢO.
BỐ TRÍ NỘI THẤT CHỈ MANG TÍNH THAM KHẢO, KÍCH THƯỚC ĐỊNH VỊ TƯỜNG, HOÀN THIÊN NỘI THẤT XEM BẢN VẼ TRÊN KHAI NÓI THẬT.
BÊN THỤ HƯỚNG (-----)

GIÁM ĐỐC: PHẠM THỊ NGUYỄN TRANG
CHỦ ĐẦU TƯ (CLIENT):

CÔNG TY TNHH MTV ĐẦU TƯ ĐỊA ĐỐC
THẢO ĐIỀN XANH

TƯ VẤN THIẾT KẾ (LEAD CONSULTANT):
IAM
IAMARCHITECTS
3F - 47G HOÀ HỒNG - PHƯỜNG 2
QUẬN PHÚ NHUẬN - TP. HCM - VN
EMAIL: INFO@IAM.VN
WEBSITE: IAM.VN

TỔNG GIÁM ĐỐC: NGUYỄN HOÀNG DŨNG
CÔNG TRÌNH (PROJECT):

BIS SCHOOL
242 NGUYỄN VĂN HƯỜNG
PHƯỜNG THẢO ĐIỀN , Q.2, TP. HCM

DỰ ÁN (PROJECT NO.): 18006

CHỦ TRƯ (MANAGED BY): KTS. NGŨ THÀNH VINH

THIẾT KẾ (DESIGNED BY): KS. NGUYỄN BẢO NĂNG

VẼ (DRAWN BY): KS. NGUYỄN BẢO NĂNG

KIỂM (CHECK BY): KTS. NGUYỄN NGỌC TOÀN

GIẢI ĐOẠN (STAGE):


TÊN BẢN VẼ (DRAWING TITLE):

HIỆU CHỈNH (REVISION NO.):

KHỔ GIẤY (PAPER SIZE): A2

TỈ LỆ (DWG. SCALE):

SỐ BẢN VẼ (DRAWING NUMBER): ĐNH-12

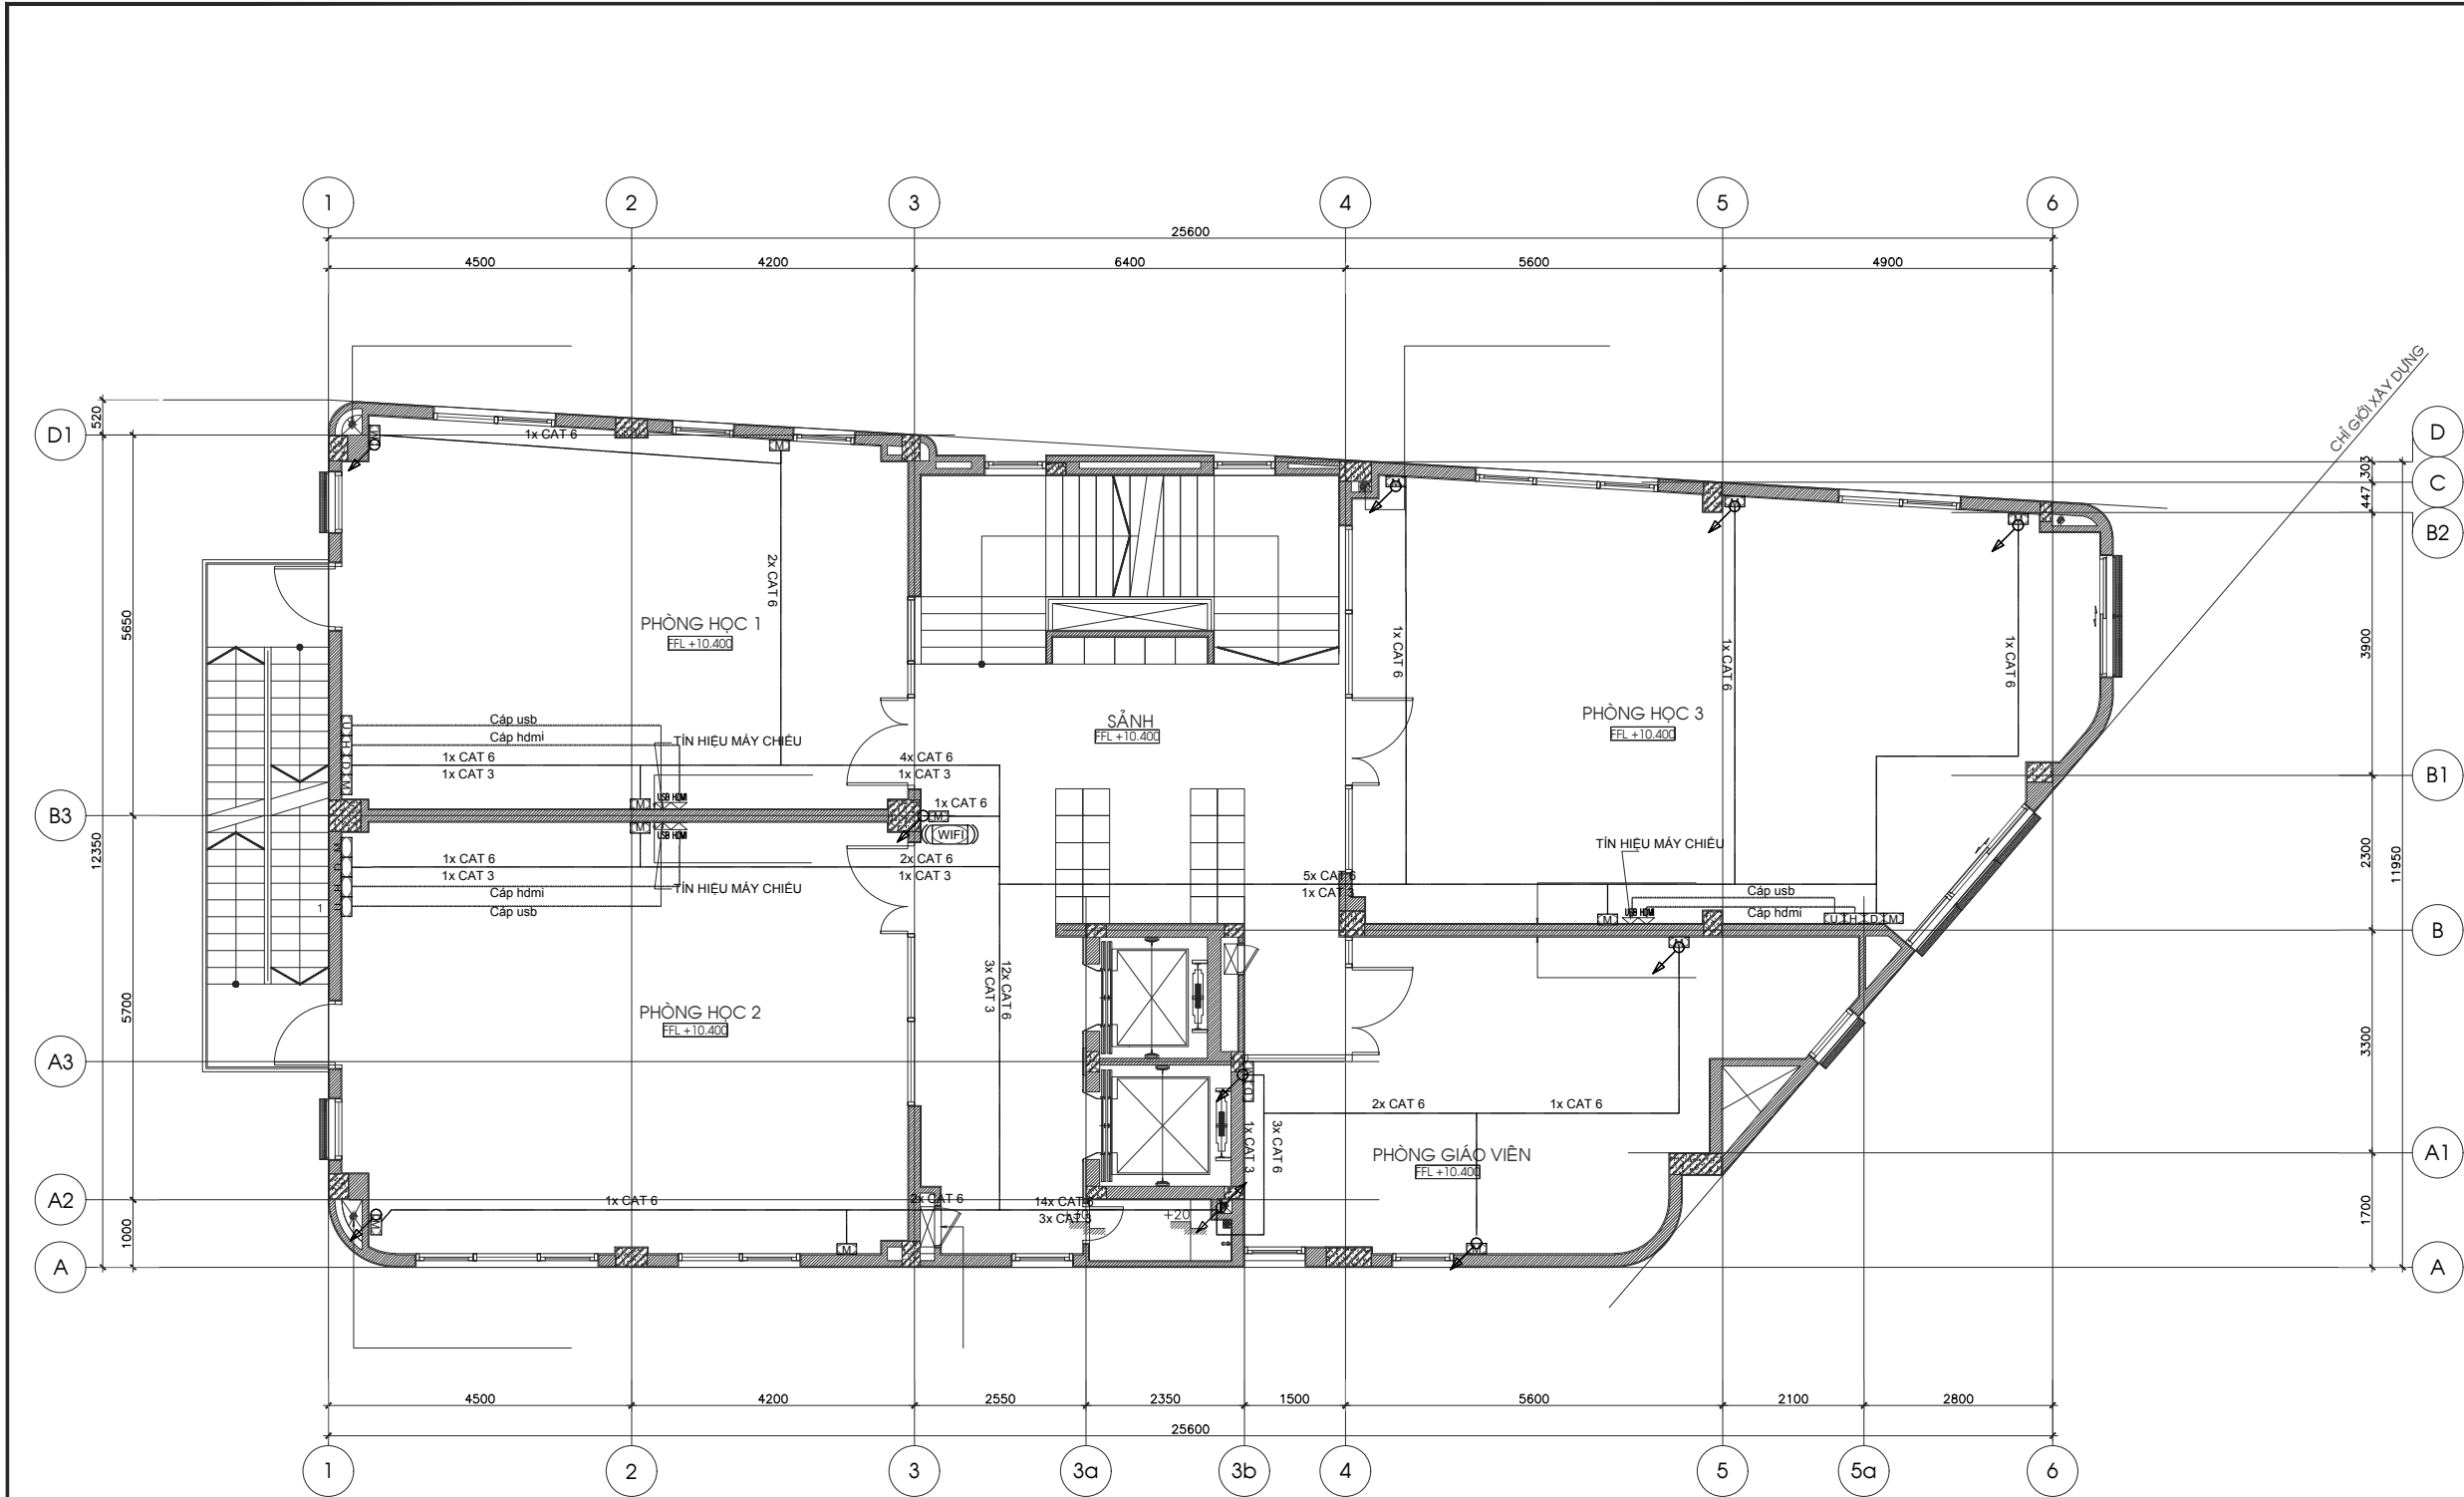

KÝ HIỆU	MÔ TẢ	KÝ HIỆU	MÔ TẢ
	MĂNG CÁP GA 100 ĐI NGOÀI HÀNH LANG		HỘP KỸ THUẬT TẮNG MẠNG TRUYỀN HÌNH
	VỊ TRÍ CÁP ĐI LÊN, XUỐNG		TỦ KỸ THUẬT TẮNG MẠNG MÂY TÍNH, ĐIỆN THOẠI VÀ DOORPHONE
	Ổ CẮM HDMI		HỘP KỸ THUẬT PHÒNG SƠN TÍNH ĐIỆN KÍCH THƯỚC 35X45X15CM
	Ổ MÁY TÍNH		N CÁP TRÊN TUYẾN
	Ổ CẮM ĐIỆN THOẠI		THANG CÁP XUYÊN TẦNG
	Ổ CẮM USB		TOÀN BỘ Ổ ĐIỆN THOẠI TRONG PHÒNG HỌC CAO ĐỘ +400MM . VỊ TRÍ MÁY CHIẾU +2500MM GẮN TƯỜNG VỊ TRÍ BÀN GIÁO VIÊN +800MM, Ổ MẠNG HÀNH LANG LẮP TRÊN TRẦN
	ĐẦU RA CÁP HDMI CHỜ KẾT NỐI MÁY CHIẾU		
	ĐẦU RA CÁP USB CHỜ KẾT NỐI MÁY CHIẾU		

MẶT BẰNG BỐ TRÍ HT MẠNG TẦNG 4

CÁC BẢN VẼ KIẾN TRÚC ĐƯỢC CHUNG VỚI BẢN VẼ KẾT CẤU VÀ CƠ ĐIỆN LIÊN QUAN.
CÁC THÔNG TIN THUỘC VỀ KẾT CẤU VÀ CƠ ĐIỆN THỂ HIỆN TRÊN BẢN VẼ KIẾN TRÚC CHỈ ĐỂ THAM KHẢO.
BỐ TRÍ NỘI THẤT CHỈ MANG TÍNH THAM KHẢO, KÍCH THƯỚC ĐỊNH VỊ TƯỜNG, HOÀN THIỆN NỘI THẤT XEM BẢN VẼ TRÊN KHAI NỘI THẤT.
BÊN THỤ HƯỚNG (-----)

GIÁM ĐỐC: PHẠM THỊ NGUYỄN TRANG
CHỦ ĐẦU TƯ (CLIENT):

CÔNG TY TNHH MTV ĐẦU TƯ ĐỊA ỐC
THẢO ĐIỀN XANH

TƯ VẤN THIẾT KẾ (LEAD CONSULTANT):
CÔNG TY CỔ PHẦN KIẾN TRÚC
IAM
IAMARCHITECTS
3F - 47G HOÀ HỒNG - PHƯỜNG 2
QUẬN PHÚ NHUẬN - TP. HCM - VN
EMAIL: INFO@IAM.VN
WEBSITE: IAMA.VN

TỔNG GIÁM ĐỐC: NGUYỄN HOÀNG DŨNG
CÔNG TRÌNH (PROJECT):

BIS SCHOOL
242 NGUYỄN VĂN HƯỜNG
PHƯỜNG THẢO ĐIỀN, Q.2, TP. HCM

DỰ ÁN (PROJECT NO.): 18006

CHỦ TRƯ (MANAGED BY): KTS. NGŨ THÀNH VINH

THIẾT KẾ (DESIGNED BY): KTS. NGUYỄN BẢO NĂNG

VẼ (DRAWN BY): KTS. NGUYỄN BẢO NĂNG

KIỂM (CHECK BY): KTS. NGUYỄN NGỌC TOÀN

GIẢI ĐOẠN (STAGE):

TÊN BẢN VẼ (DRAWING TITLE):

HIỆU CHỈNH (REVISION NO.):


KHỔ GIẤY (PAPER SIZE):

NGÀY PHÁT HÀNH (ISSUED DATE):

TỈ LỆ (DWG. SCALE):

SỐ BẢN VẼ (DRAWING NUMBER):

ĐNH-14

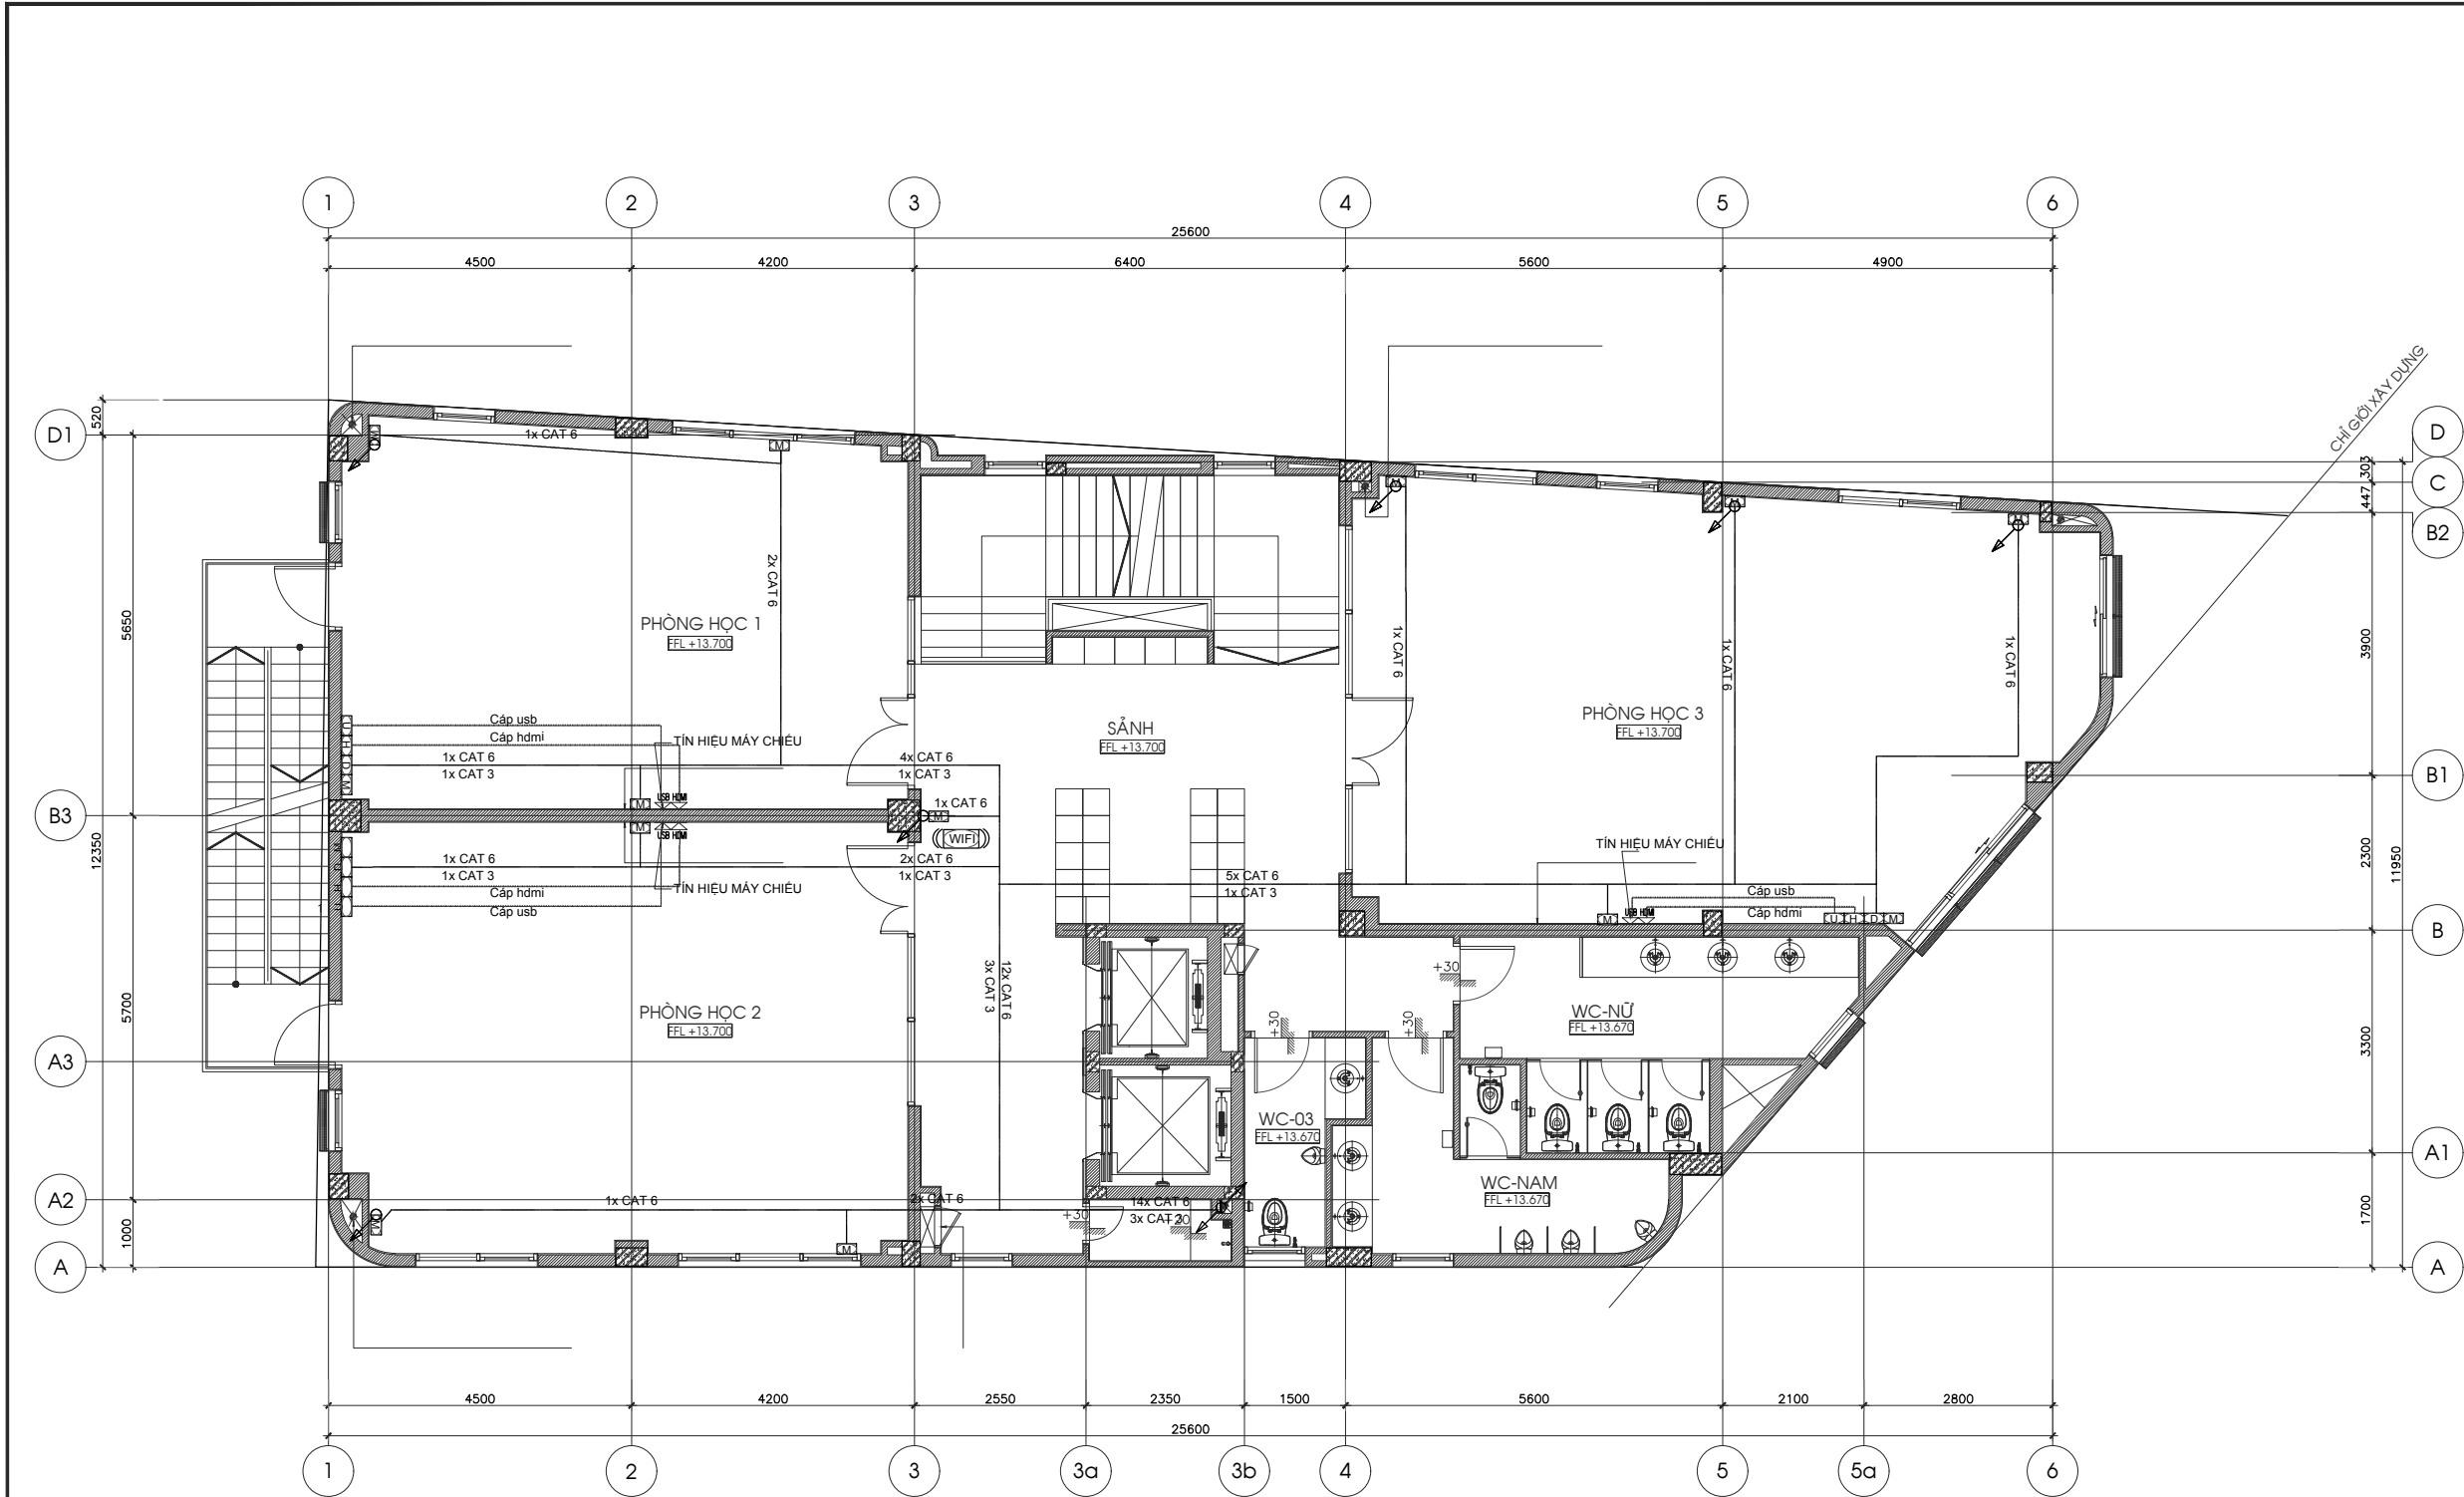

KÝ HIỆU	MÔ TẢ	KÝ HIỆU	MÔ TẢ
	MĂNG CÁP GA 100 ĐI NGOÀI HÀNH LANG		HỘP KỸ THUẬT TẮNG MẠNG TRUYỀN HÌNH
	VỊ TRÍ CÁP ĐI LÊN, XUỐNG		TỦ KỸ THUẬT TẮNG MẠNG MÂY TÍNH, ĐIỆN THOẠI VÀ DOORPHONE
	Ổ CẮM HDMI		HỘP KỸ THUẬT PHÒNG SƠN TÍNH ĐIỆN KÍCH THƯỚC 35X45X15CM
	Ổ MÁY TÍNH		N CÁP TRÊN TUYẾN
	Ổ CẮM ĐIỆN THOẠI		THANG CÁP XUYÊN TẦNG
	Ổ CẮM USB	TOÀN BỘ Ổ ĐIỆN THOẠI TRONG PHÒNG HỌC CAO ĐỘ +400MM , VỊ TRÍ MÁY CHIẾU +2500MM GẮN TƯỜNG	
	ĐẦU RA CÁP HDMI CHỜ KẾT NỐI MÁY CHIẾU	VỊ TRÍ BÀN GIÁO VIÊN +800MM, Ổ MẠNG HÀNH LANG LẮP TRÊN TRẦN	
	ĐẦU RA CÁP USB CHỜ KẾT NỐI MÁY CHIẾU		

MẶT BẰNG BỐ TRÍ HT MẠNG TẦNG 5

CÁC BẢN VẼ KIẾN TRÚC ĐƯỢC CHUNG VỚI BẢN VẼ KẾT CẤU VÀ CƠ ĐIỆN LIÊN QUAN.
CÁC THÔNG TIN THUỘC VỀ KẾT CẤU VÀ CƠ ĐIỆN THỂ HIỆN TRÊN BẢN VẼ KIẾN TRÚC CHỈ ĐỂ THAM KHẢO.
BỐ TRÍ NỘI THẤT CHỈ MANG TÍNH THAM KHẢO, KÍCH THƯỚC ĐỊNH VỊ TƯỜNG, HOÀN THIÊN NỘI THẤT XEM BẢN VẼ TRÊN KHAI NỘI THẤT.
BÊN THỤ HƯỚNG (-----)

GIÁM ĐỐC: PHẠM THỊ NGUYỄN TRANG
CHỦ ĐẦU TƯ (CLIENT):

CÔNG TY TNHH MTV ĐẦU TƯ ĐỊA ĐỐC
THẢO ĐIỀN XANH

TƯ VẤN THIẾT KẾ (LEAD CONSULTANT):
CÔNG TY CỔ PHẦN KIẾN TRÚC
IAM
IAMARCHITECTS
3F - 47G HOÀ HỒNG - PHƯỜNG 2
QUẬN PHÚ NHUẬN - TP. HCM - VN
EMAIL: INFO@IAM.VN
WEBSITE: IAM.VN

TỔNG GIÁM ĐỐC: NGUYỄN HOÀNG DŨNG
CÔNG TRÌNH (PROJECT):

BIS SCHOOL
242 NGUYỄN VĂN HƯỜNG
PHƯỜNG THẢO ĐIỀN , Q.2, TP. HCM

DỰ ÁN (PROJECT NO.): 18006

CHỦ TRƯ (MANAGED BY): KTS. NGŨ THÀNH VINH

THIẾT KẾ (DESIGNED BY): KS. NGUYỄN BẢO NĂNG

VẼ (DRAWN BY): KS. NGUYỄN BẢO NĂNG

KIỂM (CHECK BY): KTS. NGUYỄN NGỌC TOÀN

GIẢI ĐOẠN (STAGE):

TÊN BẢN VẼ (DRAWING TITLE):


HIỆU CHỈNH (REVISION NO.):

KHỔ GIẤY (PAPER SIZE): NGÀY PHÁT HÀNH (ISSUED DATE):


A2

TỈ LỆ (DWG. SCALE): SỐ BẢN VẼ (DRAWING NUMBER):

ĐNH-15

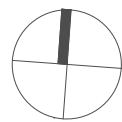

KÝ HIỆU	MÔ TẢ
	LOA ÂM TRẦN 6W
	LOA GÁN TƯỜNG 6W
	CẤP ÂM THANH
	THANG CẤP XUYỀN TẦNG

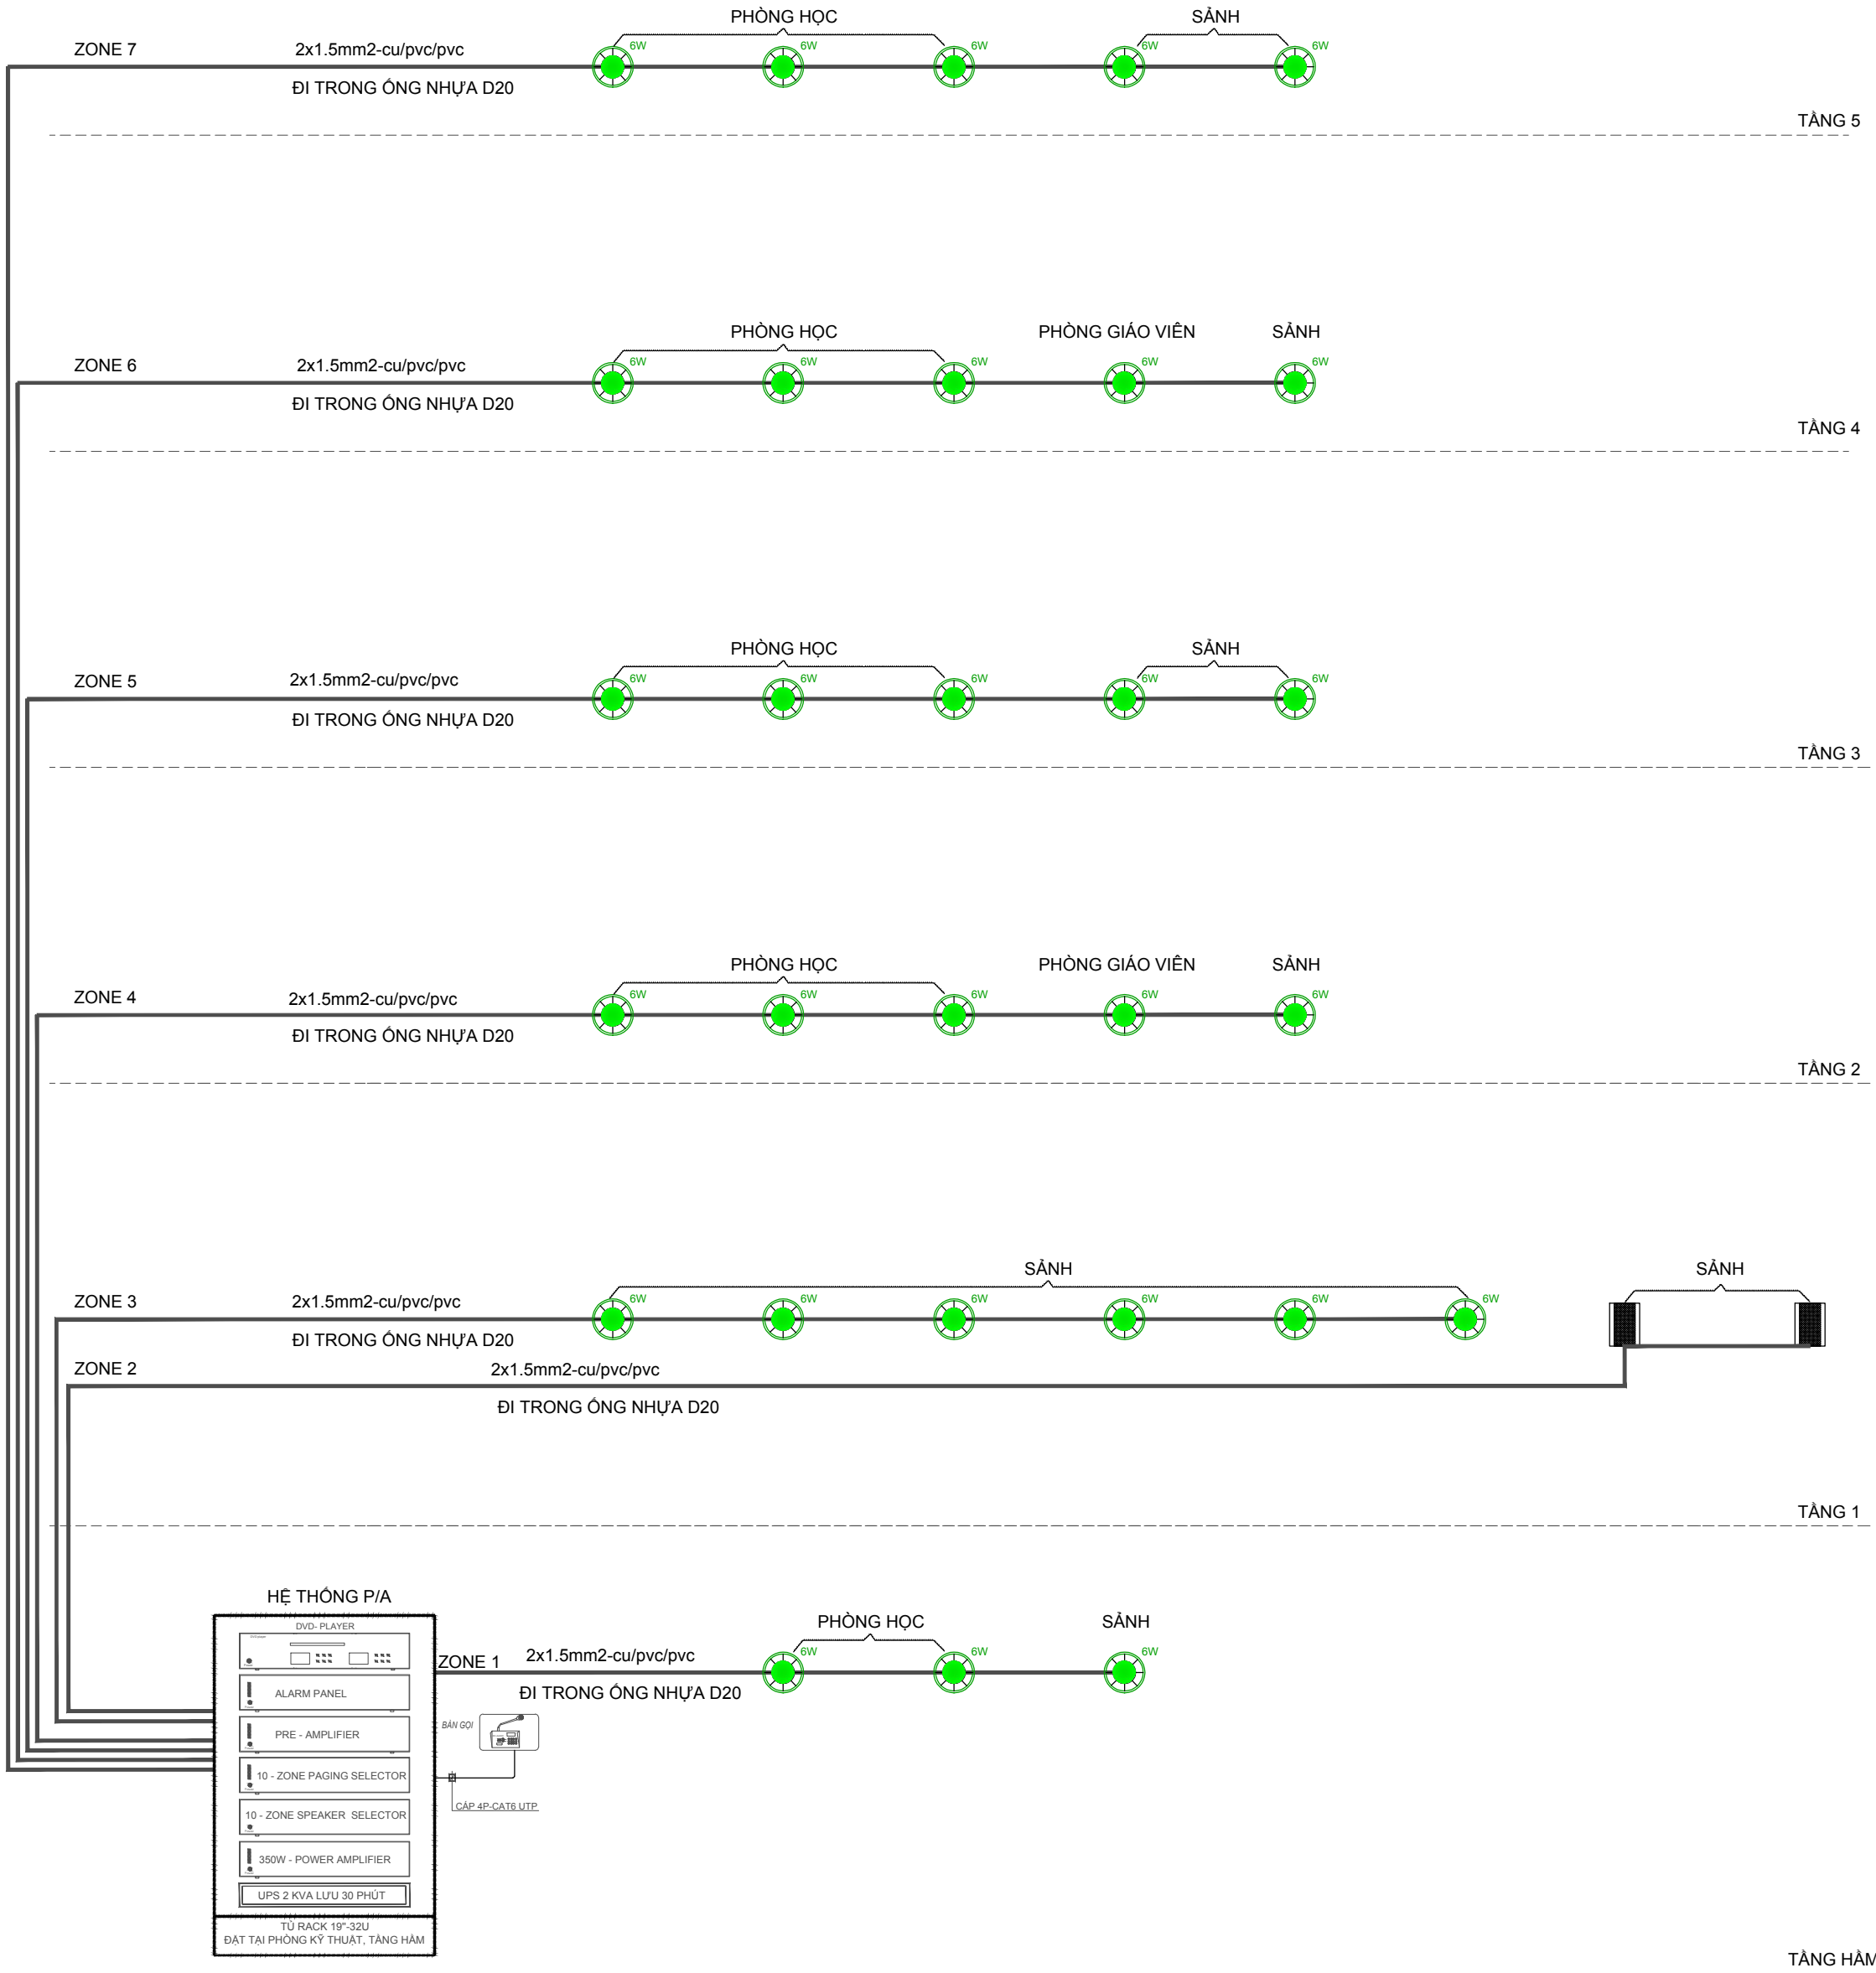

SƠ ĐỒ NGUYÊN LÝ HỆ THỐNG LOA

CÁC BẢN VẼ KIẾN TRÚC ĐƯỢC ĐỌC CHUNG VỚI BẢN VẼ KẾT CẤU VÀ CƠ ĐIỆN LIÊN QUAN.
CÁC THÔNG TIN THUỘC VỀ KẾT CẤU VÀ CƠ ĐIỆN THỂ HIỆN TRÊN BẢN VẼ KIẾN TRÚC CHỈ ĐỂ THAM KHẢO.
BỐ TRÍ NỘI THẤT CHỈ MANG TÍNH THAM KHẢO, KỊCH THUỘC ĐƠN VỊ TƯỞNG. HOÀN THIỆN NỘI THẤT XEM BẢN VẼ TRÊN KHAI NỘ THẤT.

BÊN THỤ HƯỚNG (—>)

GIÁM ĐỐC: PHẠM THỊ NGUYỄN TRANG

CHỦ ĐẦU TƯ (CLIENT)

CÔNG TY TNHH MTV ĐẦU TƯ ĐỊA ỐC
THẢO ĐIỆN XANH

TƯ VẤN THIẾT KẾ (LEAD CONSULTANT)

IAM CÔNG TY CỔ PHẦN KIẾN TRÚC
IAMARCHITECTS
3F - 47G HOÀ HỒNG - PHƯỜNG 2
QUẬN PHÚ NHUẬN - TP. HCM - VN
EMAIL: INFO@IAM.VN
WEBSITE: IAM.VN

TỔNG GIÁM ĐỐC: NGUYỄN HOÀNG DŨNG

CÔNG TRÌNH (PROJECT)

BIS SCHOOL
242 NGUYỄN VĂN HƯỚNG
PHƯỜNG THẢO ĐIỆN , Q.2, TP. HCM

DỰ ÁN (PROJECT NO.) 18006

CHỦ TRÌ (MANAGED BY) KTS. NGŨ THÀNH VINH

THIẾT KẾ (DESIGNED BY) KS. NGUYỄN BẢO NĂNG

VẼ (DRAWN BY) KS. NGUYỄN BẢO NĂNG

KÈM (CHECK BY) KTS. NGUYỄN NGỌC TOÀN

GIẢI ĐOẠN (STAGE)

TÊN BẢN VẼ (DRAWING TITLE)

HIỆU CHỈNH (REVISION NO.)


KHỔ GIẤY (PAPER SIZE) NGÀY PHÁT HÀNH (ISSUED DATE)

A2

TỈ LỆ (DWG. SCALE) SỐ BẢN VẼ (DRAWING NUMBER)

ĐNH-16

© IAM Architects 2018

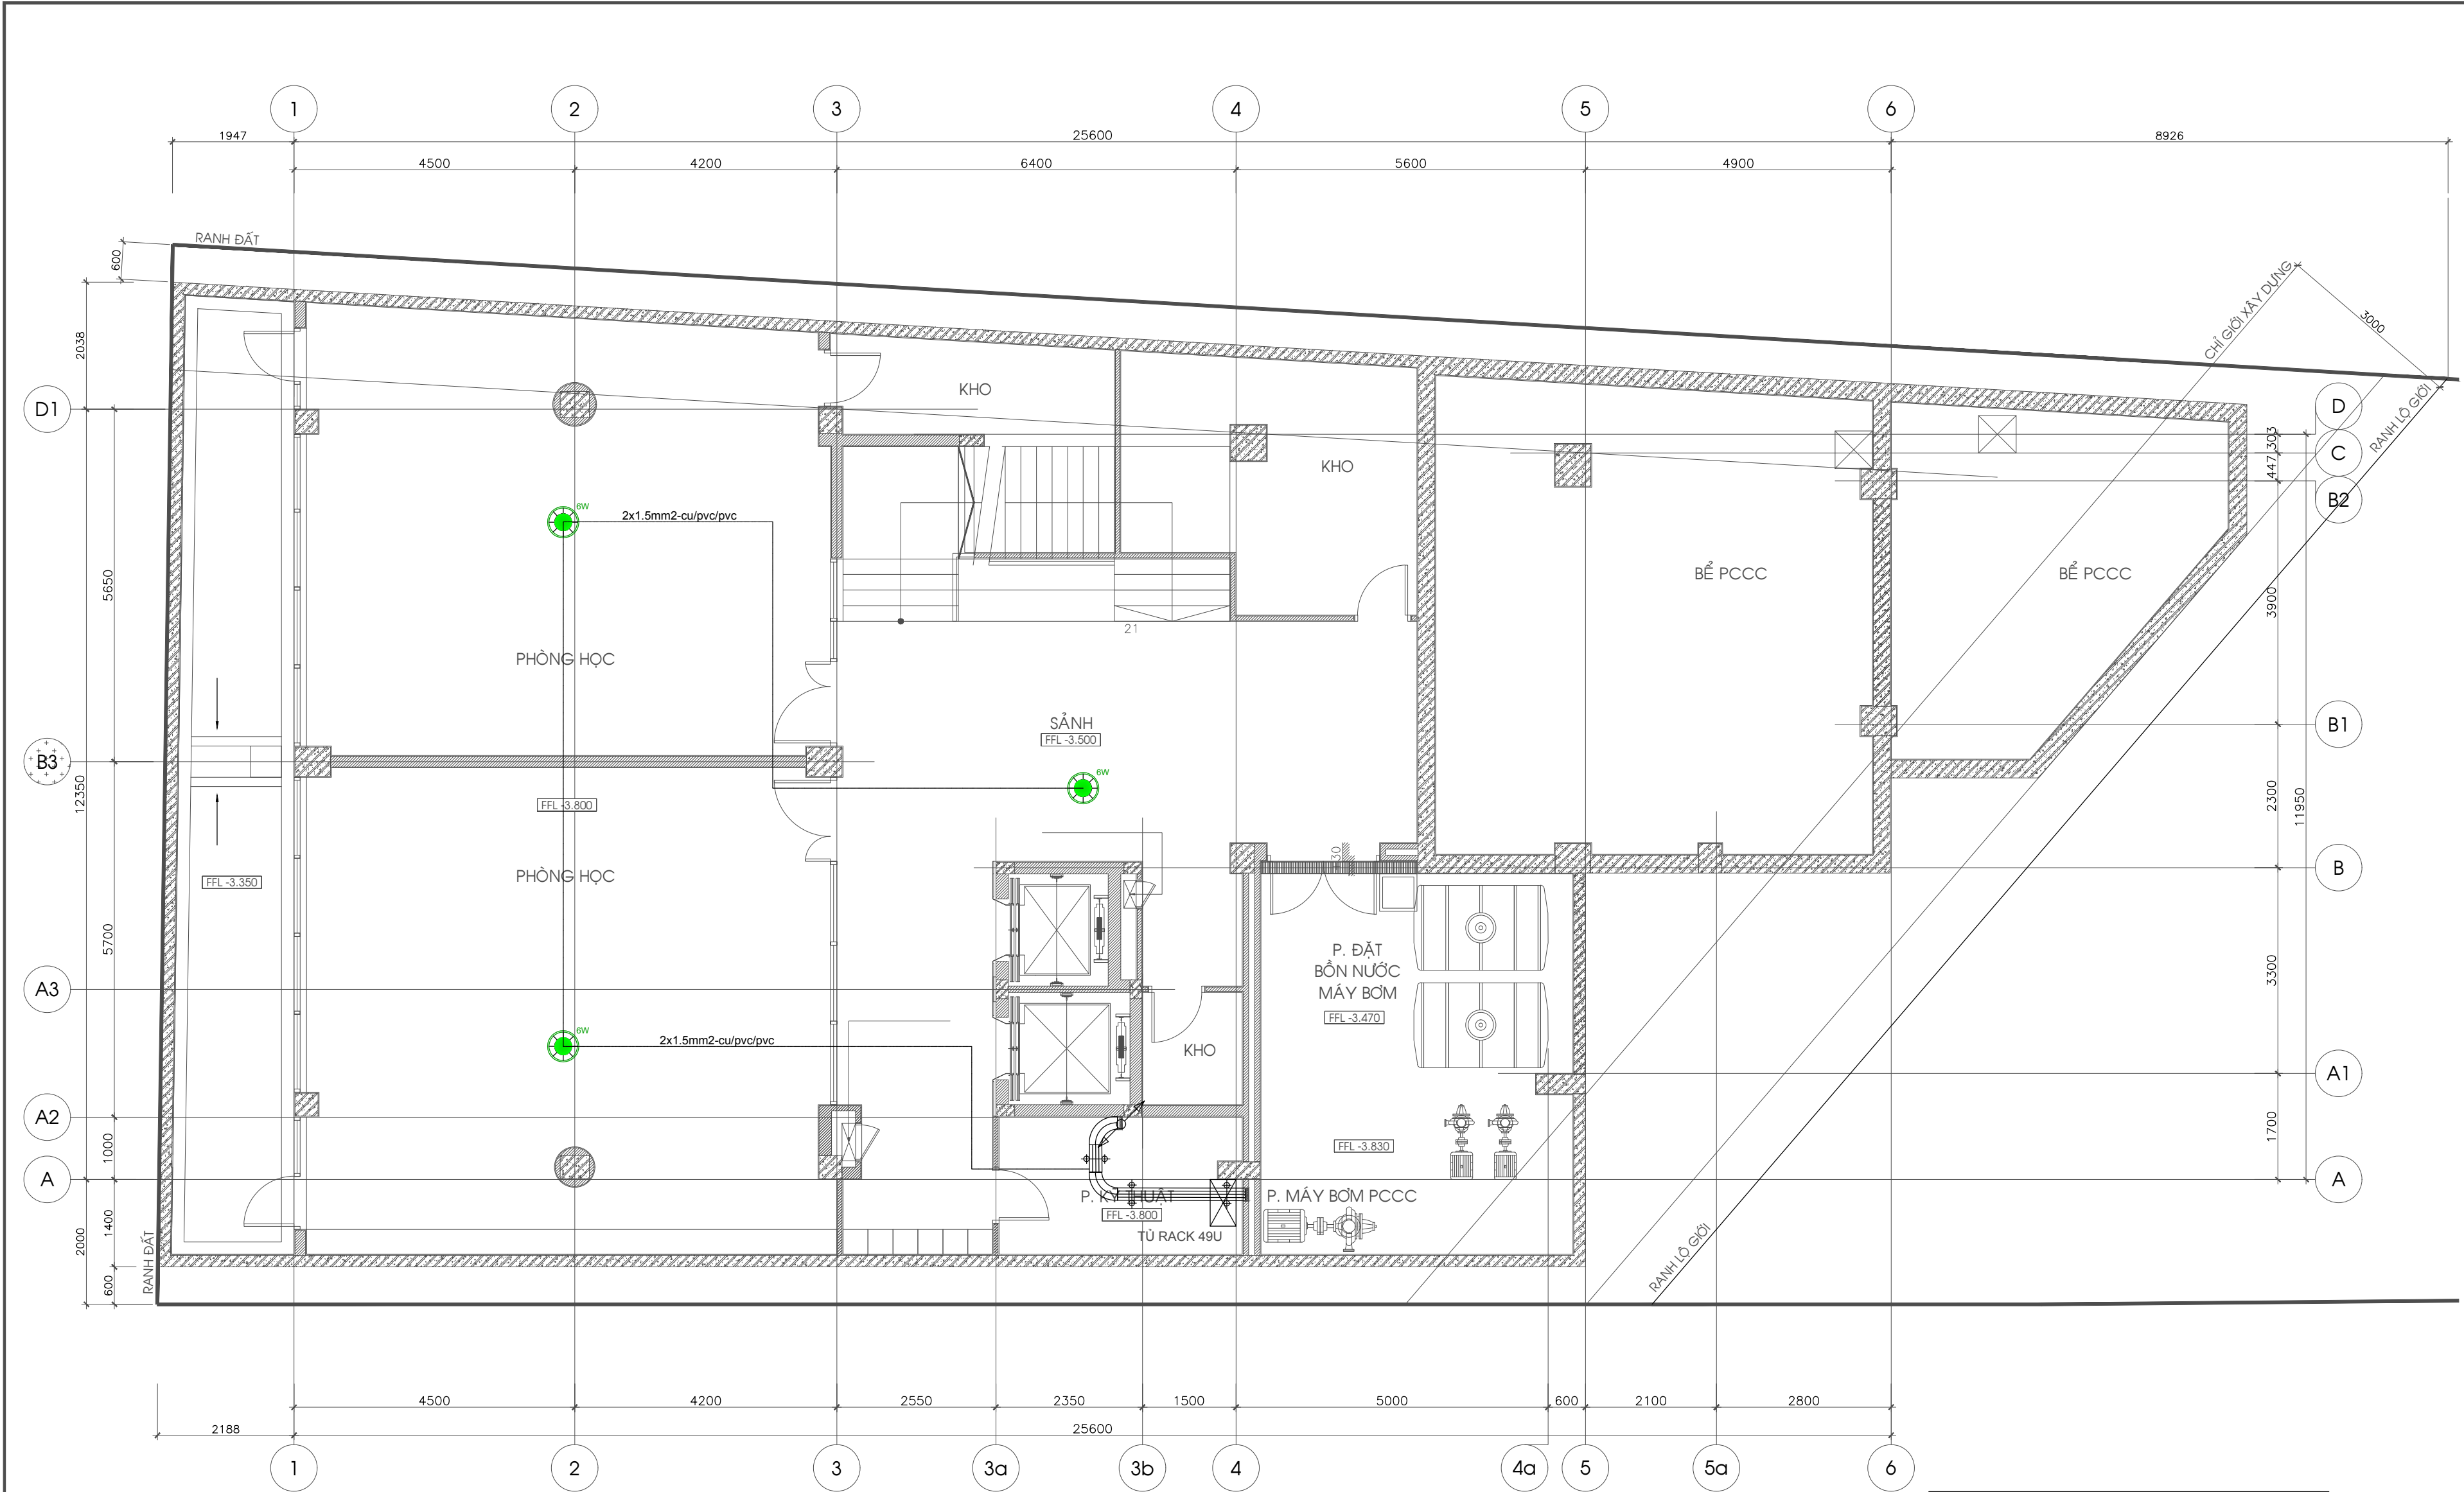

KÝ HIỆU	MÔ TẢ
	LOA ẨM TRẦN
	LOA GẮN TƯỜNG
	CÁP ẨM THANH
	THANG CÁP XUYÊN TẦNG

MẶT BẰNG BỐ TRÍ TH LOA THÔNG BÁO TẦNG HẦM

CÁC BẢN VẼ KIẾN TRÚC ĐƯỢC CHUNG VỚI BẢN VẼ KẾT CẤU VÀ CƠ ĐIỆN LIÊN QUAN.
CÁC THÔNG TIN THUỘC VỀ KẾT CẤU VÀ CƠ ĐIỆN THÌ HẸN TRÊN BẢN VẼ KIẾN TRÚC CHỈ ĐỂ THAM KHẢO.
BỐ TRÍ NƠI THẮT CHỈ MANG TÍNH THAM KHẢO, KỊCH THUỘC ĐỊNH VỊ TƯỜNG, HOÀN THIÊN NƠI THẮT XEM BẢN VẼ THIÊN KHAI NỘI THẤT.

BÊN THỦ HƯỚNG (.....)

GIÁM ĐỐC: PHẠM THỊ NGUYỄN TRANG

CHỦ ĐẦU TƯ (CLIENT)

CÔNG TY TNHH MTV ĐẦU TƯ ĐỊA ỐC
THẢO ĐIỀN XANH

TƯ VẤN THIẾT KẾ (LEAD CONSULTANT)

CÔNG TY CỔ PHẦN KIẾN TRÚC
IAM
IAMARCHITECTS
3F - 47G HOÀ HỒNG - PHƯỜNG 2
QUẬN PHÚ NHUẬN - TP. HCM - VN
EMAIL: INFO@IAM.VN
WEBSITE: IAMA.VN

TỔNG GIÁM ĐỐC: NGUYỄN HOÀNG DŨNG

CÔNG TRÌNH (PROJECT)

BIS SCHOOL
242 NGUYỄN VĂN HƯỚNG
PHƯỜNG THẢO ĐIỀN, Q. 2, TP. HCM

DỰ ÁN (PROJECT NO.)

18006

CHỦ TRÌ (MANAGED BY) KTS. NGÔ THÀNH VINH

THIẾT KẾ (DESIGNED BY) KS. NGUYỄN BẢO NĂNG

VẼ (DRAWN BY) KS. NGUYỄN BẢO NĂNG

KIỂM (CHECK BY) KTS. NGUYỄN NGỌC TOÀN

GIẢI ĐOẠN (STAGE)

TÊN BẢN VẼ (DRAWING TITLE)

HẸU CHỈNH (REVISION NO.)


KHỔ GIẤY (PAPER SIZE) NGAY PHÁT HÀNH (ISSUED DATE)

A2

TỈ LỆ (DWG. SCALE) SỐ BẢN VẼ (DRAWING NUMBER)

ĐNH-17

© IAM Architects 2018

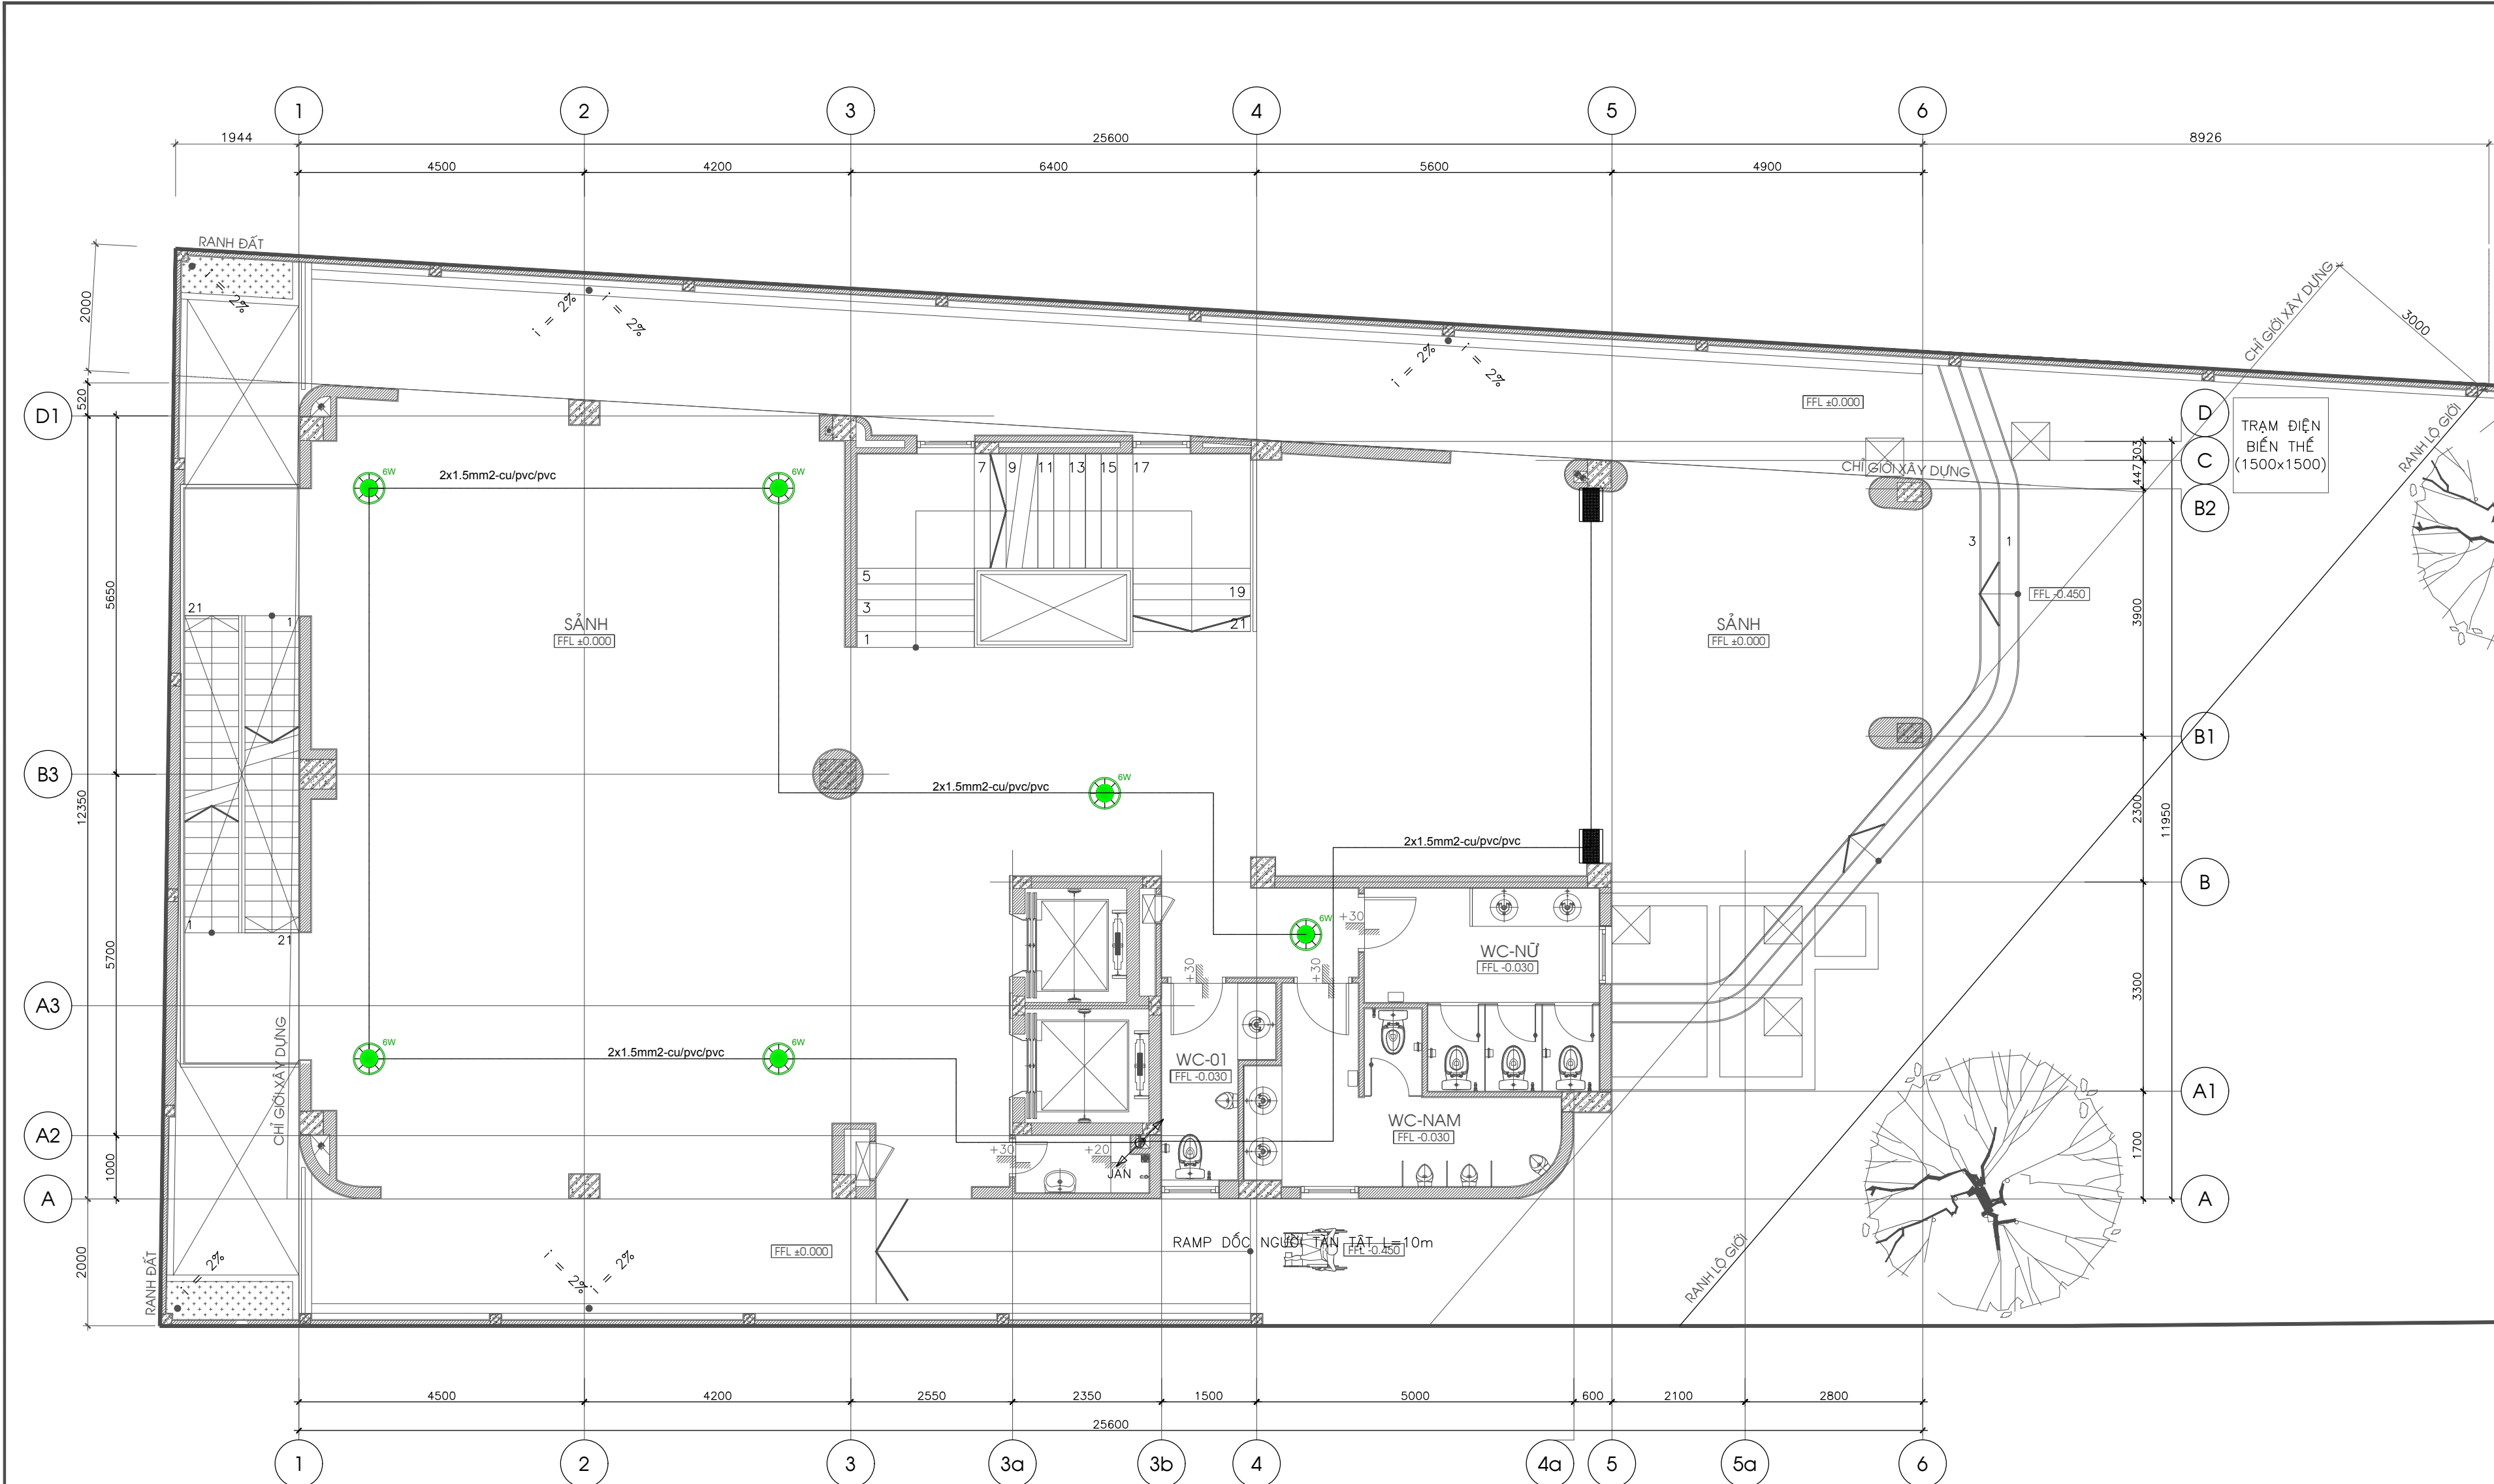

KÝ HIỆU	MÔ TẢ
	LOA ÂM TRẦN
	LOA GÁN TƯỜNG
	CÁP ÂM THANH
	THANG CÁP XUYÊN TẦNG

MẶT BẰNG BỐ TRÍ TH LOA THÔNG BÁO TẦNG 1

CÁC BẢN VẼ KIẾN TRÚC ĐƯỢC CHUNG VỚI BẢN VẼ KẾT CẤU VÀ CƠ ĐIỆN LIÊN QUAN.
CÁC THÔNG TIN THUỘC VỀ KẾT CẤU VÀ CƠ ĐIỆN THỂ HIỆN TRÊN BẢN VẼ KIẾN TRÚC CHỈ ĐỂ THAM KHẢO.
BỐ TRÍ NỘI THẤT CHỈ MANG TÍNH THAM KHẢO, KỊCH THUỘC ĐỊNH VỊ TƯỜNG, HOÀN THIÊN NỘI THẤT XEM BẢN VẼ THIẾT KẾ NỘI THẤT.

BÊN THỦ HƯỚNG (.....)

GIÁM ĐỐC: PHẠM THỊ NGUYỄN TRANG
CHỦ ĐẦU TƯ (CLIENT):
CÔNG TY TNHH MTV ĐẦU TƯ ĐỊA ỐC
THẢO ĐIỀN XANH

TƯ VẤN THIẾT KẾ (LEAD CONSULTANT):
CÔNG TY CỔ PHẦN KIẾN TRÚC
IAM
IAMARCHITECTS
3F - 47G HOÀ HỒNG - PHƯỜNG 2
QUẬN PHÚ NHUẬN - TP. HCM - VN
EMAIL: INFO@IAM.VN
WEBSITE: IAMA.VN


TỔNG GIÁM ĐỐC: NGUYỄN HOÀNG DŨNG
CÔNG TRÌNH (PROJECT):

BIS SCHOOL
242 NGUYỄN VĂN HƯỚNG
PHƯỜNG THẢO ĐIỀN, Q.2, TP. HCM

DỰ ÁN (PROJECT NO.): 18006

CHỦ TRÌ (MANAGED BY): KTS. NGÔ THÀNH VINH
THIẾT KẾ (DESIGNED BY): KS. NGUYỄN BẢO NĂNG
VẼ (DRAWN BY): KS. NGUYỄN BẢO NĂNG
KIỂM (CHECK BY): KTS. NGUYỄN NGỌC TOÀN
GIAI ĐOẠN (STAGE):
TÊN BẢN VẼ (DRAWING TITLE):

HIỆU CHỈNH (REVISION NO.):
KHỔ GIẤY (PAPER SIZE): A2
NGÀY PHÁT HÀNH (ISSUED DATE):
TỈ LỆ (DWG. SCALE):
SỐ BẢN VẼ (DRAWING NUMBER): ĐNH-18

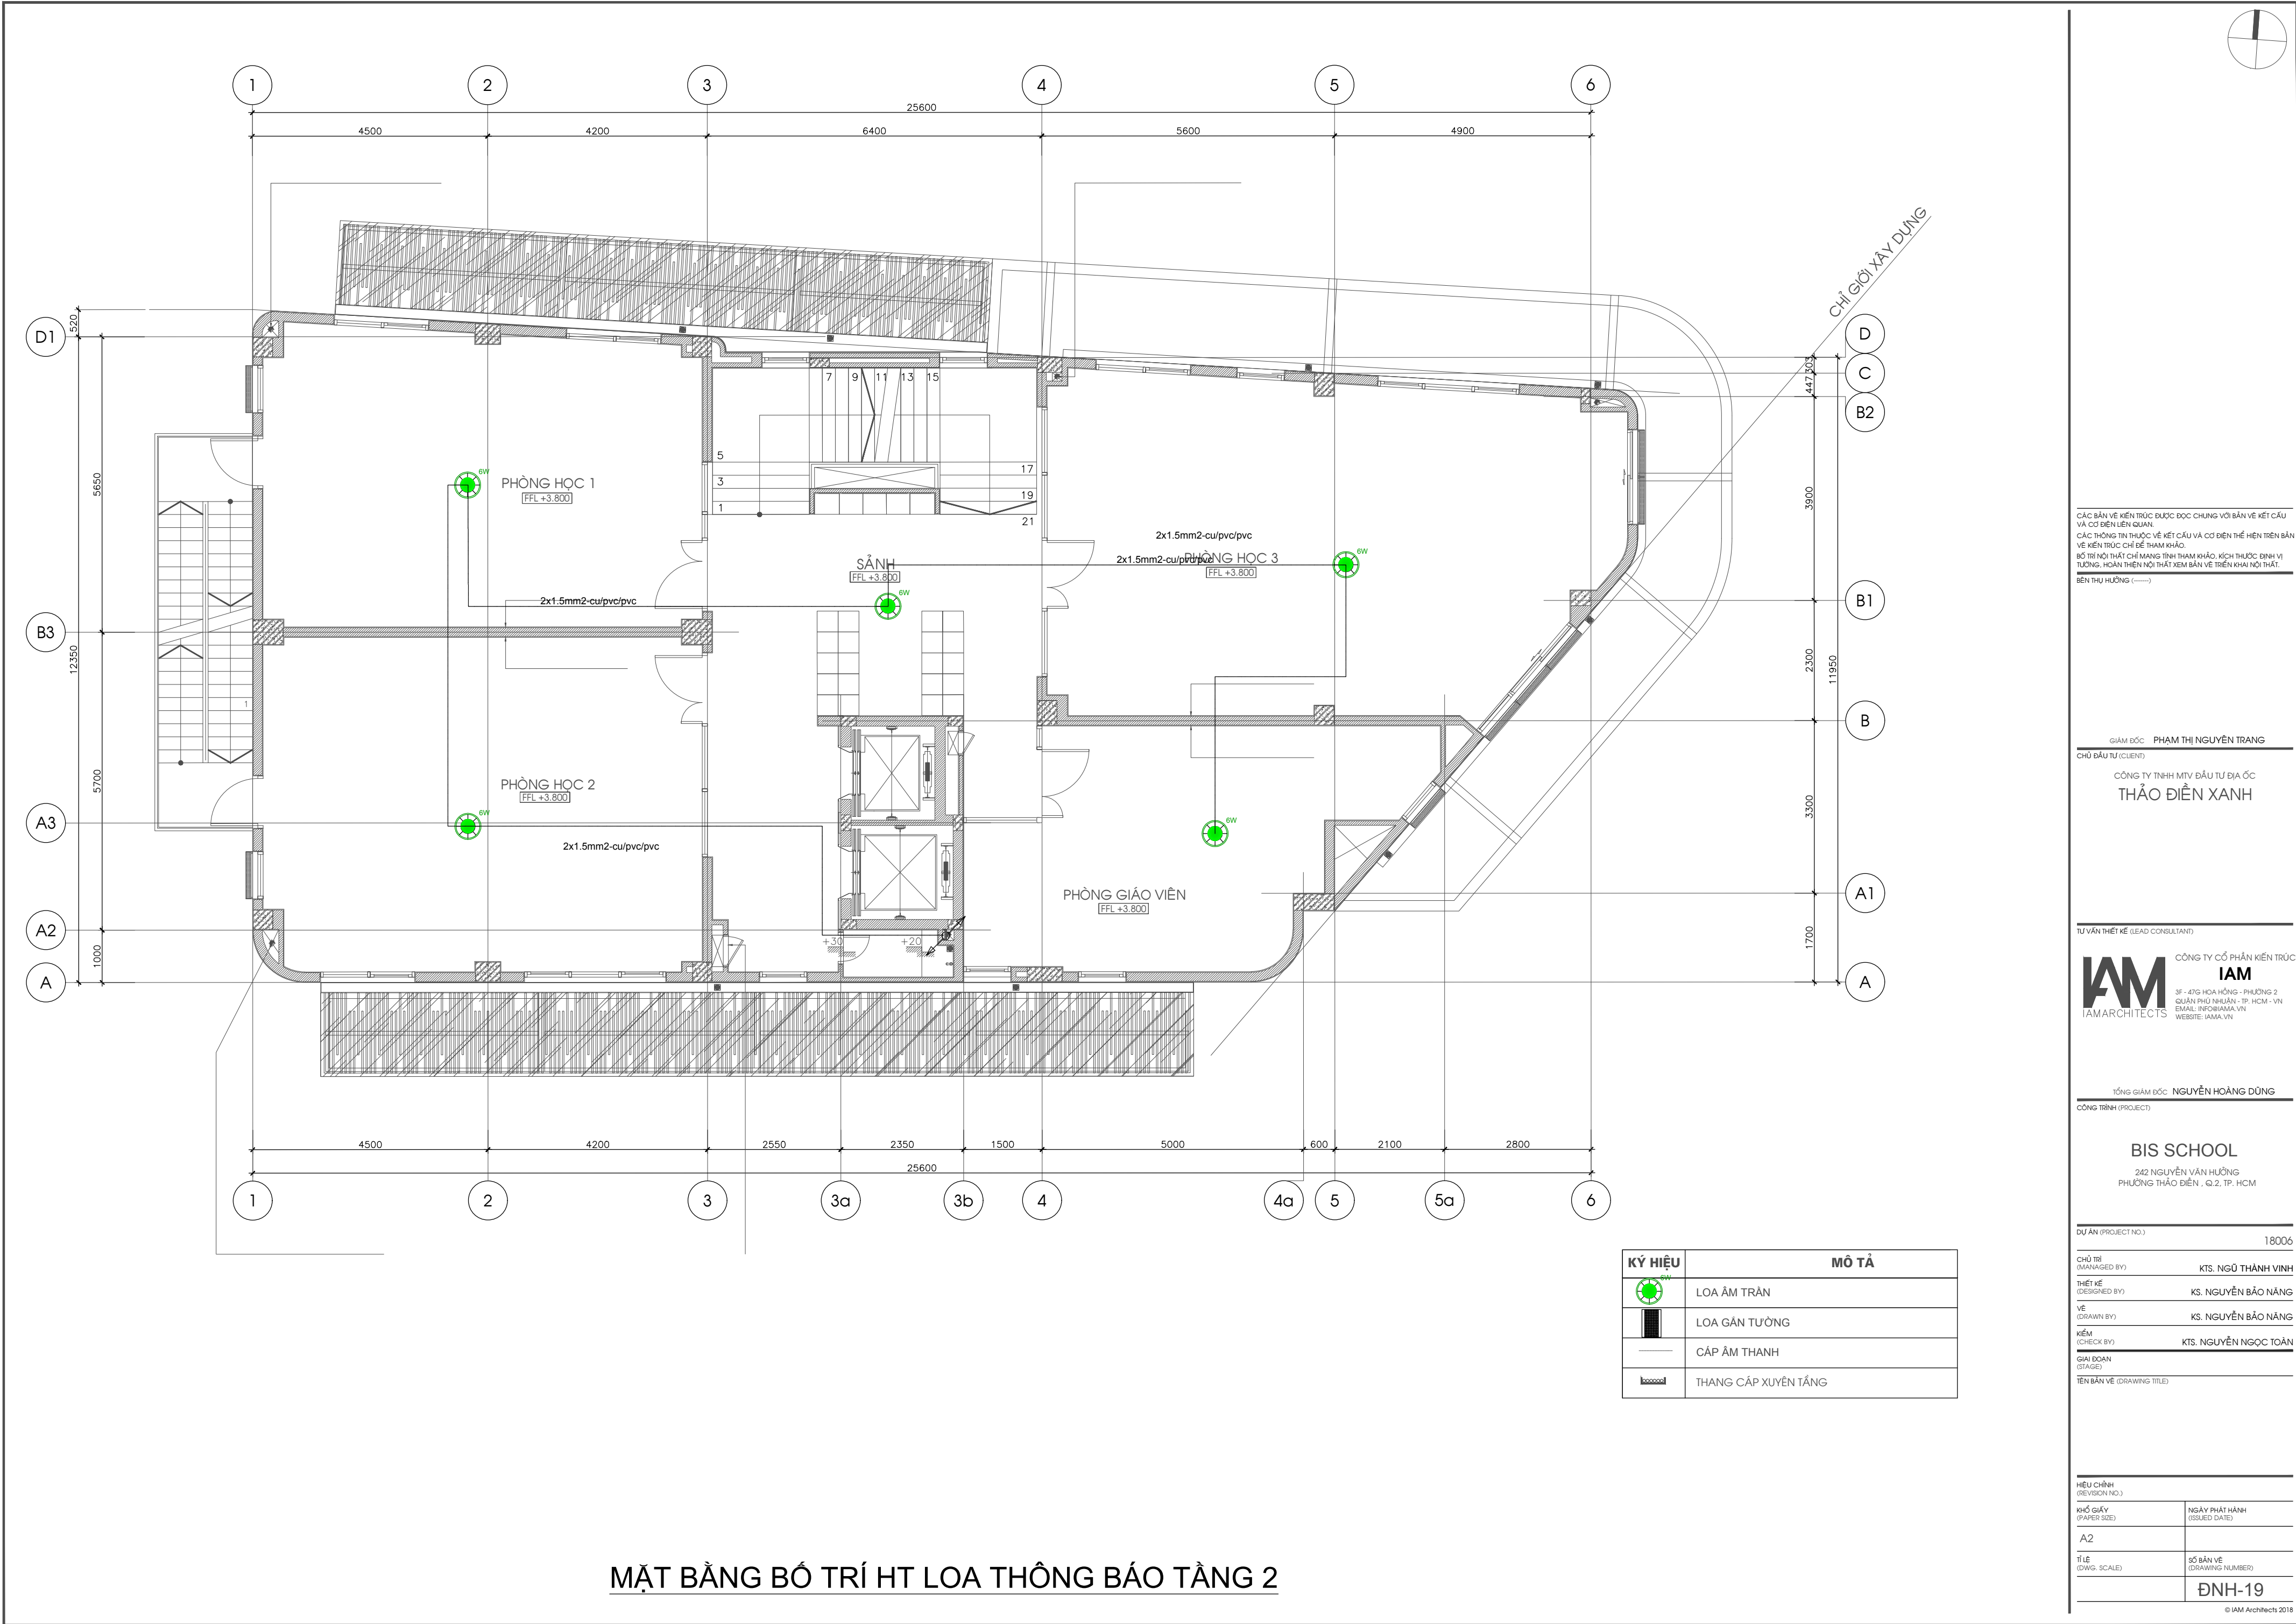

MẶT BẰNG BỐ TRÍ HT LOA THÔNG BÁO TẦNG 2

KÝ HIỆU	MÔ TẢ
	LOA ÂM TRẦN
	LOA GẮN TƯỜNG
	CÁP ÂM THANH
	THANG CẤP XUYÊN TẦNG

CÁC BẢN VẼ KIẾN TRÚC ĐƯỢC ĐỌC CHUNG VỚI BẢN VẼ KẾT CẤU VÀ CƠ ĐIỆN LIÊN QUAN.
CÁC THÔNG TIN THUỘC VỀ KẾT CẤU VÀ CƠ ĐIỆN THỂ HIỆN TRÊN BẢN VẼ KIẾN TRÚC CHỈ ĐỂ THAM KHẢO.
BỐ TRÍ NỘI THẤT CHỈ MANG TÍNH THAM KHẢO, KỊCH THUỘC ĐỊNH VỊ TƯỜNG, HOÀN THIÊN NỘI THẤT XEM BẢN VẼ THIÊN KHAI NỘI THẤT.

GIÁM ĐỐC: PHẠM THỊ NGUYỄN TRANG
CHỦ ĐẦU TƯ (CLIENT):

CÔNG TY TNHH MTV ĐẦU TƯ ĐỊA ỐC
THẢO ĐIỀN XANH

TƯ VẤN THIẾT KẾ (LEAD CONSULTANT):
IAM ARCHITECTS
CÔNG TY CỔ PHẦN KIẾN TRÚC
3F - 47G HOÀ HỒNG - PHƯỜNG 2
QUẬN PHÚ NHUẬN - TP. HCM - VN
EMAIL: INFO@IAM.VN
WEBSITE: IAMA.VN


TỔNG GIÁM ĐỐC: NGUYỄN HOÀNG DŨNG
CÔNG TRÌNH (PROJECT):

BIS SCHOOL
242 NGUYỄN VĂN HƯỚNG
PHƯỜNG THẢO ĐIỀN, Q.2, TP. HCM

DỰ ÁN (PROJECT NO.): 18006

CHỦ TRÌ (MANAGED BY): KTS. NGÔ THÀNH VINH
THIẾT KẾ (DESIGNED BY): KS. NGUYỄN BẢO NĂNG
VẼ (DRAWN BY): KS. NGUYỄN BẢO NĂNG
KIỂM (CHECK BY): KTS. NGUYỄN NGỌC TOÀN
GIAI ĐOẠN (STAGE):
TÊN BẢN VẼ (DRAWING TITLE):

HIỆU CHỈNH (REVISION NO.):
KHỔ GIẤY (PAPER SIZE): A2
TỈ LỆ (DWG. SCALE):
NGÀY PHÁT HÀNH (ISSUED DATE):
SỐ BẢN VẼ (DRAWING NUMBER): ĐNH-19

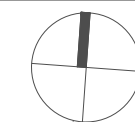

KÝ HIỆU	MÔ TẢ
	LOA ÂM TRẦN
	LOA GẮN TƯỜNG
	CÁP ÂM THANH
	THANG CẤP XUYÊN TẦNG

MẶT BẰNG BỐ TRÍ HT LOA THÔNG BÁO TẦNG 3

CÁC BẢN VẼ KIẾN TRÚC ĐƯỢC CHUNG VỚI BẢN VẼ KẾT CẤU VÀ CƠ ĐIỆN LIÊN QUAN.
CÁC THÔNG TIN THUỘC VỀ KẾT CẤU VÀ CƠ ĐIỆN THỂ HIỆN TRÊN BẢN VẼ KIẾN TRÚC CHỈ ĐỂ THAM KHẢO.
BỘ TƯ VẤN THIẾT KẾ CHỈ MANG TÍNH THAM KHẢO, KỊCH THUỘC ĐỊNH VỊ TƯỜNG, HOÀN THIÊN NỘI THẤT XEM BẢN VẼ THIẾT KẾ NỘI THẤT.

BÊN THỤ HƯỚNG (.....)

GIÁM ĐỐC: PHẠM THỊ NGUYỄN TRANG

CHỦ ĐẦU TƯ (CLIENT)

CÔNG TY TNHH MTV ĐẦU TƯ ĐỊA ỐC
THẢO ĐIỀN XANH

TƯ VẤN THIẾT KẾ (LEAD CONSULTANT)

IAM CÔNG TY CỔ PHẦN KIẾN TRÚC
IAMARCHITECTS
3F - 47G HOÀ HỒNG - PHƯỜNG 2
QUẬN PHÚ NHUẬN - TP. HCM - VN
EMAIL: INFO@IAM.VN
WEBSITE: IAM.VN

TỔNG GIÁM ĐỐC: NGUYỄN HOÀNG DŨNG

CÔNG TRÌNH (PROJECT)

BIS SCHOOL

242 NGUYỄN VĂN HƯỚNG
PHƯỜNG THẢO ĐIỀN, Q.2, TP. HCM

DỰ ÁN (PROJECT NO.)

18006

CHỦ TRÌ

(MANAGED BY)

KTS. NGÔ THÀNH VINH

THIẾT KẾ

(DESIGNED BY)

KS. NGUYỄN BẢO NĂNG

VẼ

(DRAWN BY)

KS. NGUYỄN BẢO NĂNG

KIỂM

(CHECK BY)

KTS. NGUYỄN NGỌC TOÀN

GIẢI ĐOẠN

(STAGE)

TÊN BẢN VẼ (DRAWING TITLE)

HIỆU CHỈNH

(REVISION NO.)

KHỔ GIẤY

(PAPER SIZE)

A2

TỈ LỆ

(DWG. SCALE)

NGÀY PHÁT HÀNH


(ISSUED DATE)

SỐ BẢN VẼ

(DRAWING NUMBER)

ĐNH-20

© IAM Architects 2018

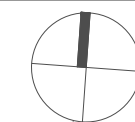

KÝ HIỆU	MÔ TẢ
	LOA ÂM TRẦN
	LOA GẮN TƯỜNG
	CÁP ÂM THANH
	THANG CẤP XUYÊN TẦNG

MẶT BẰNG BỐ TRÍ HT LOA THÔNG BÁO TẦNG 4

CÁC BẢN VẼ KIẾN TRÚC ĐƯỢC ĐỌC CHUNG VỚI BẢN VẼ KẾT CẤU VÀ CƠ ĐIỆN LIÊN QUAN.
CÁC THÔNG TIN THUỘC VỀ KẾT CẤU VÀ CƠ ĐIỆN THỂ HIỆN TRÊN BẢN VẼ KIẾN TRÚC CHỈ ĐỂ THAM KHẢO.
BỐ TRÍ NỘI THẤT CHỈ MANG TÍNH THAM KHẢO, KỊCH THUỘC ĐỊNH VỊ TƯỜNG, HOÀN THIÊN NỘI THẤT XEM BẢN VẼ THIẾT KẾ NỘI THẤT.

BÊN THỦ HƯỚNG (.....)

GIÁM ĐỐC: PHẠM THỊ NGUYỄN TRANG
CHỦ ĐẦU TƯ (CLIENT):
CÔNG TY TNHH MTV ĐẦU TƯ ĐỊA ỐC
THẢO ĐIỀN XANH

TƯ VẤN THIẾT KẾ (LEAD CONSULTANT):
IAM ARCHITECTS
CÔNG TY CỔ PHẦN KIẾN TRÚC
3F - 47G HOÀ HỒNG - PHƯỜNG 2
QUẬN PHÚ NHUẬN - TP. HCM - VN
EMAIL: INFO@IAM.VN
WEBSITE: IAMA.VN

TỔNG GIÁM ĐỐC: NGUYỄN HOÀNG DŨNG
CÔNG TRÌNH (PROJECT):



BIS SCHOOL
242 NGUYỄN VĂN HƯỚNG
PHƯỜNG THẢO ĐIỀN, Q.2, TP. HCM

DỰ ÁN (PROJECT NO.): 18006

CHỦ TRÌ (MANAGED BY): KTS. NGÔ THÀNH VINH
THIẾT KẾ (DESIGNED BY): KS. NGUYỄN BẢO NĂNG
VẼ (DRAWN BY): KS. NGUYỄN BẢO NĂNG
KIỂM (CHECK BY): KTS. NGUYỄN NGỌC TOÀN
GIAI ĐOẠN (STAGE):
TÊN BẢN VẼ (DRAWING TITLE):

HIỆU CHỈNH (REVISION NO.):
KHỔ GIẤY (PAPER SIZE): A2
TỈ LỆ (DWG. SCALE):
NGÀY PHÁT HÀNH (ISSUED DATE):
SỐ BẢN VẼ (DRAWING NUMBER): ĐNH-21

© IAM Architects 2018

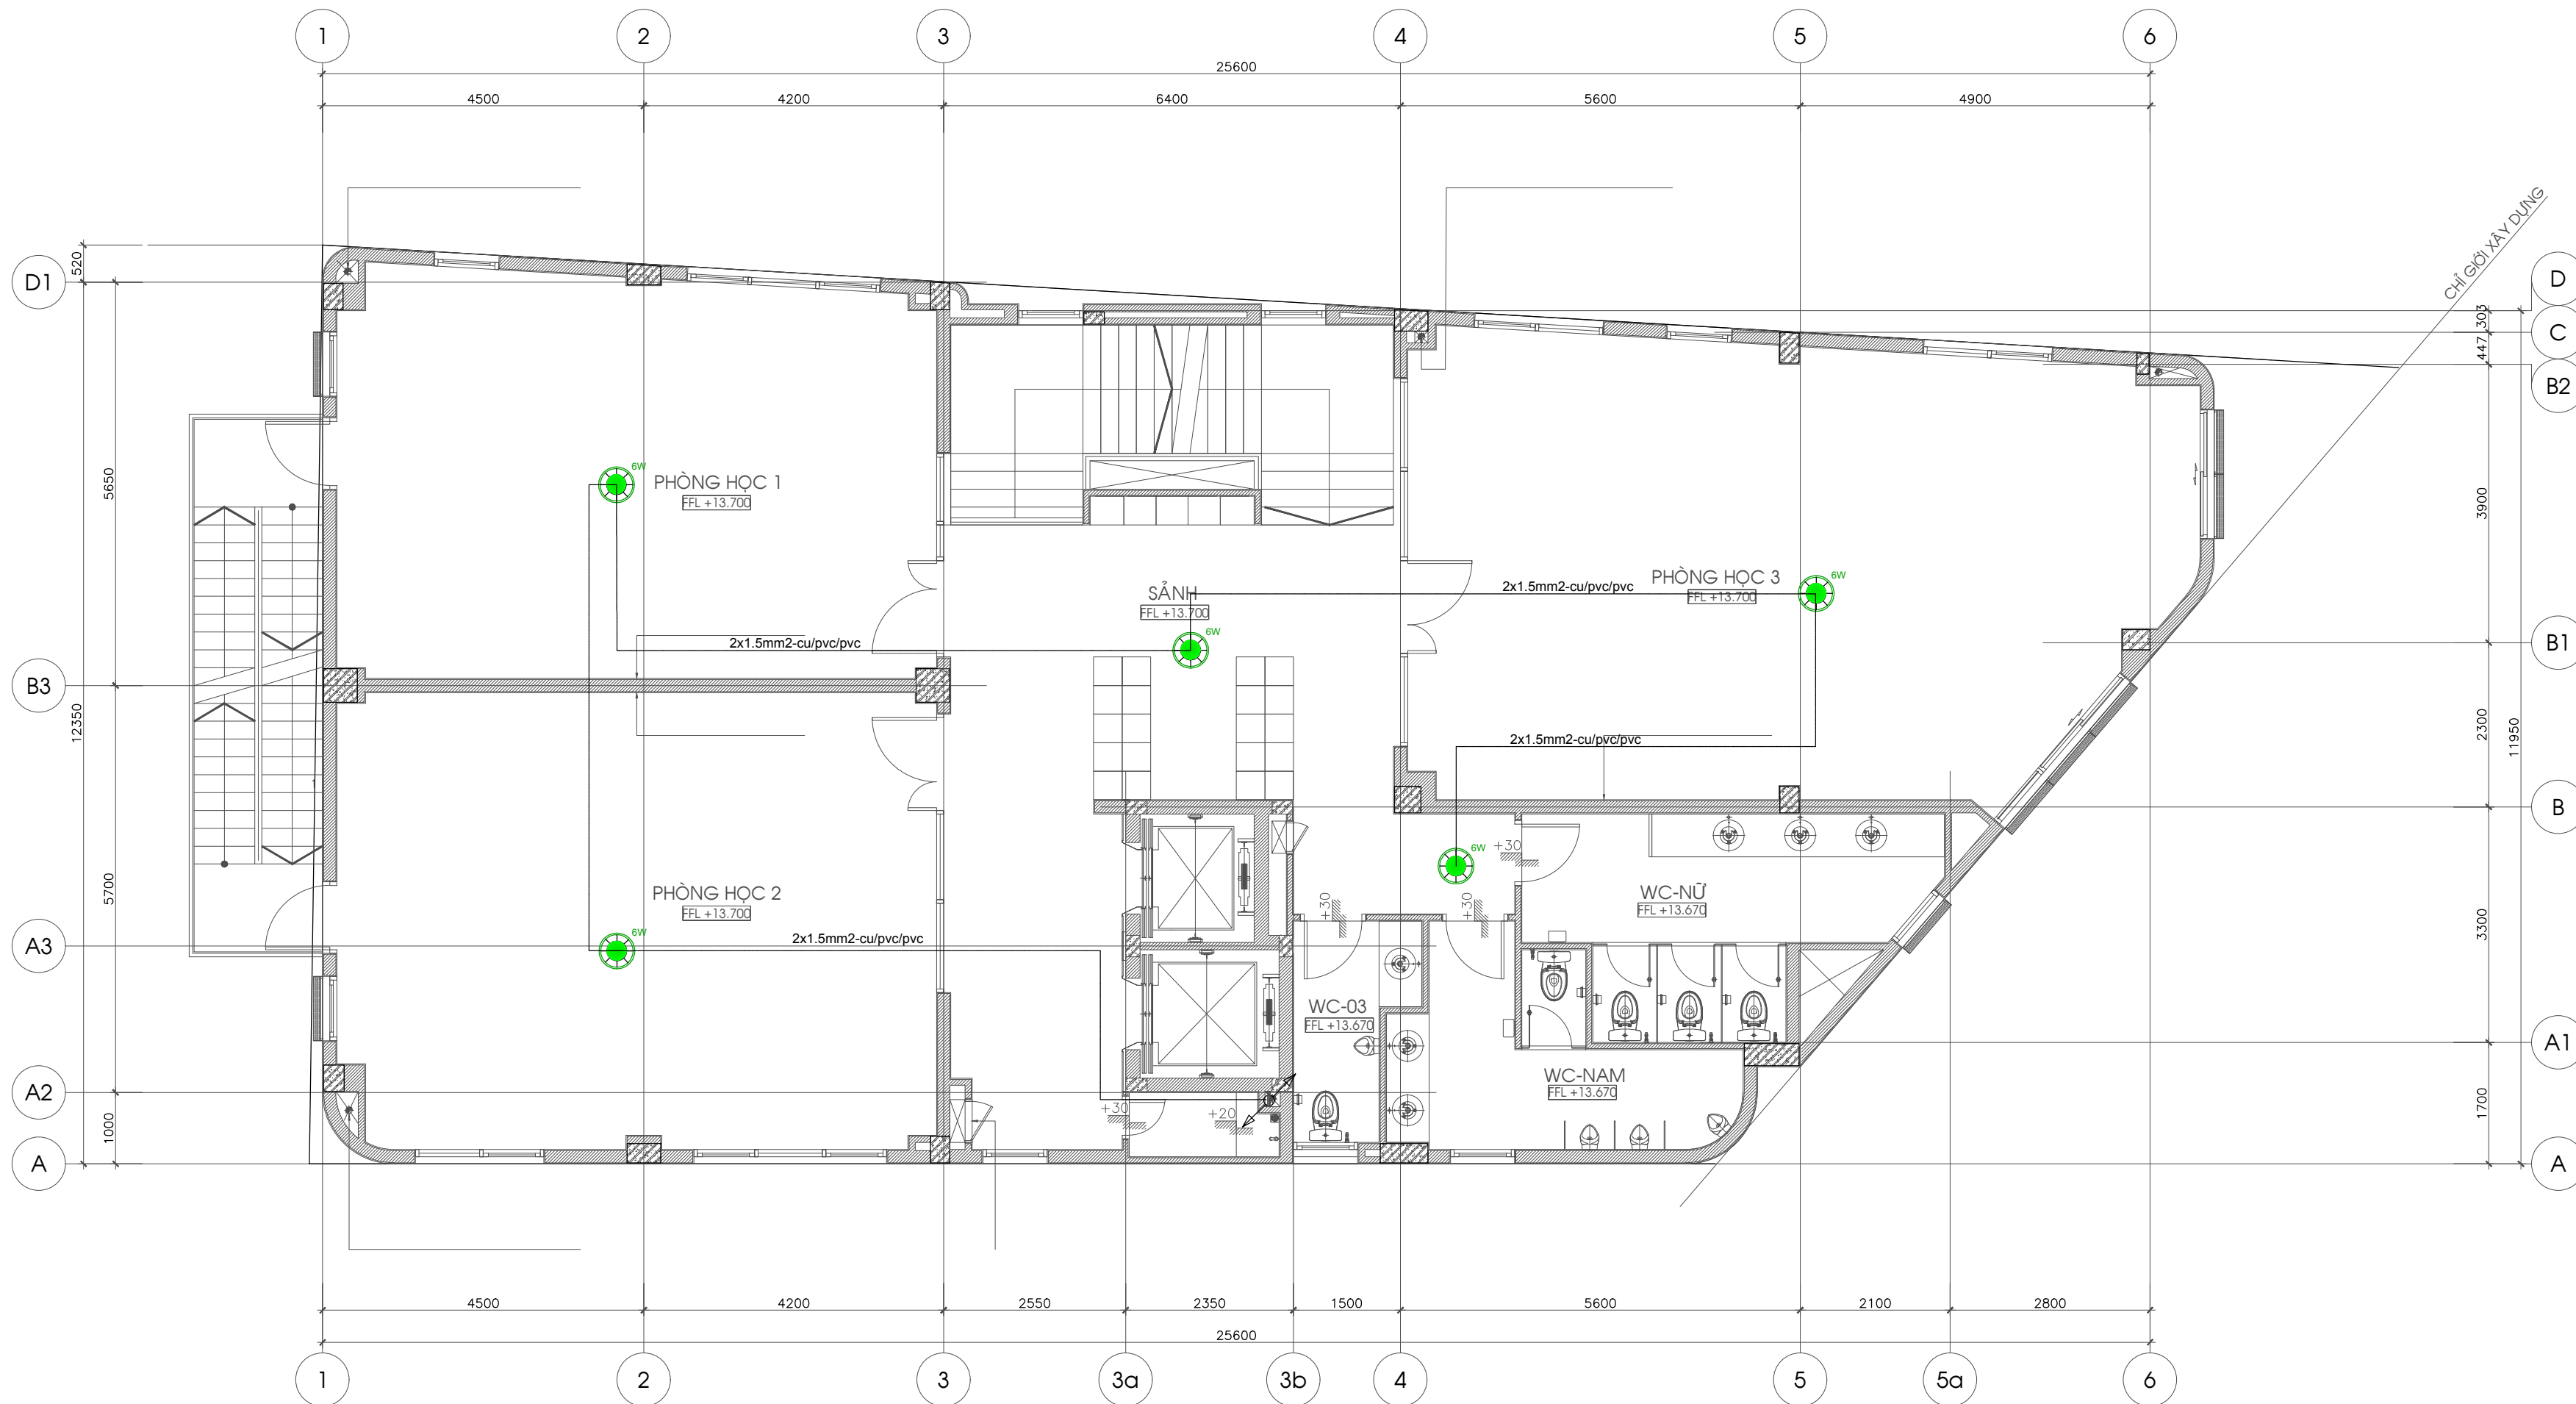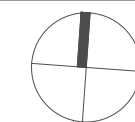

KÝ HIỆU	MÔ TẢ
	LOA ÂM TRẦN
	LOA GẮN TƯỜNG
	CÁP ÂM THANH
	THANG CÁP XUYÊN TẦNG

MẶT BẰNG BỐ TRÍ HT LOA THÔNG BÁO TẦNG 5

CÁC BẢN VẼ KIẾN TRÚC ĐƯỢC CHUNG VỚI BẢN VẼ KẾT CẤU VÀ CƠ ĐIỆN LIÊN QUAN.
CÁC THÔNG TIN THUỘC VỀ KẾT CẤU VÀ CƠ ĐIỆN THỂ HIỆN TRÊN BẢN VẼ KIẾN TRÚC CHỈ ĐỂ THAM KHẢO.
BỐ TRÍ NỘI THẤT CHỈ MANG TÍNH THAM KHẢO, KỊCH THUỘC ĐỊNH VỊ TƯỜNG, HOÀN THIÊN NỘI THẤT XEM BẢN VẼ THIẾT KẾ NỘI THẤT.

BÊN THỦ HƯỚNG (.....)

GIÁM ĐỐC: PHẠM THỊ NGUYỄN TRANG

CHỦ ĐẦU TƯ (CLIENT)

CÔNG TY TNHH MTV ĐẦU TƯ ĐỊA ỐC
THẢO ĐIỀN XANH

TƯ VẤN THIẾT KẾ (LEAD CONSULTANT)

IAM CÔNG TY CỔ PHẦN KIẾN TRÚC
IAMARCHITECTS
3F - 47G HOÀ HỒNG - PHƯỜNG 2
QUẬN PHÚ NHUẬN - TP. HCM - VN
EMAIL: INFO@IAM.VN
WEBSITE: IAMA.VN

TỔNG GIÁM ĐỐC: NGUYỄN HOÀNG DŨNG

CÔNG TRÌNH (PROJECT)

BIS SCHOOL

242 NGUYỄN VĂN HƯỚNG
PHƯỜNG THẢO ĐIỀN, Q.2, TP. HCM

DỰ ÁN (PROJECT NO.)

18006

CHỦ TRÌ

(MANAGED BY)

KTS. NGÔ THÀNH VINH

THIẾT KẾ

(DESIGNED BY)

KS. NGUYỄN BẢO NĂNG

VẼ

(DRAWN BY)

KS. NGUYỄN BẢO NĂNG

KIỂM

(CHECK BY)

KTS. NGUYỄN NGỌC TOÀN

GIẢI ĐOẠN

(STAGE)

TÊN BẢN VẼ (DRAWING TITLE)

HIỆU CHỈNH

(REVISION NO.)

KHỔ GIẤY

(PAPER SIZE)

A2

TỈ LỆ

(DWG. SCALE)

NGÀY PHÁT HÀNH

(ISSUED DATE)

SỐ BẢN VẼ

(DRAWING NUMBER)

ĐNH-22

© IAM Architects 2018