

DANH MỤC BẢN VẼ	
MÃ BẢN VẼ	TÊN BẢN VẼ / DRAWING NAME
IT-01	DRAWING LIST
IT-02	LEGEND AND SYMBOL LIST
CY-MEA-DIAGRAM	NETWORK DIAGRAM_CY & MEA
IT-LIFT	LIFT
DC-4BF	RACK LAYOUT DATA CENTER – 4BF
IDF-M.B3F	RACK LAYOUT IDF-M.B3F
IDF-M.B1F	RACK LAYOUT IDF-M.B1F
IDF-M.1F	RACK LAYOUT IDF-M.1F
IDF-M.2F	RACK LAYOUT IDF-M.2F
IDF-M.3F	RACK LAYOUT IDF-M.3F
IDF-MF	RACK LAYOUT IDF-MF
IDF-M.5F	RACK LAYOUT IDF-M.5F
IDF-M.6F	RACK LAYOUT IDF-M.6F
IDF-M.7F	RACK LAYOUT IDF-M.7F
IDF-M.8F	RACK LAYOUT IDF-M.8F
IDF-M.10F	RACK LAYOUT IDF-M.10F
IDF-M.12F	RACK LAYOUT IDF-M.12F
IDF-M.15F	RACK LAYOUT IDF-M.15F
IDF-M.17F	RACK LAYOUT IDF-M.17F
IDF-M.19F	RACK LAYOUT IDF-M.19F
IDF-M.22F	RACK LAYOUT IDF-M.22F
IDF-M.25F	RACK LAYOUT IDF-M.25F
IDF-M.29F	RACK LAYOUT IDF-M.29F
IDF-M.45F	RACK LAYOUT IDF-M.45F

DỰ ÁN:

TỔ HỢP KHÁCH SẠN, CĂN HỘ
DỊCH VỤ MARRIOTT VÀ NHÀ Ở
ĐỂ BÁN

ĐỊA ĐIỂM XÂY DỰNG:
58 BẠCH ĐẰNG, P. HẢI CHÂU 1, Q. HẢI CHÂU, TP. ĐÀ NẴNG

CHỦ ĐẦU TƯ:

CÔNG TY CỔ PHẦN ĐỊA ỐC
FOODINCO

ĐỊA CHỈ:
58 BẠCH ĐẰNG, P. HẢI CHÂU 1, Q. HẢI CHÂU, TP. ĐÀ NẴNG

BAN QUẢN LÝ DỰ ÁN:

TƯ VẤN GIÁM SÁT:

CN CÔNG TY TNHH APAVE CHÂU Á - THÁI
BÌNH DƯƠNG TẠI ĐÀ NẴNG

NGUYỄN ĐĂNG HÙNG

ĐƠN VỊ NHÀ THẦU CHÍNH:

CÔNG TY CỔ PHẦN ALPHANAM E&C

NHÀ THẦU THI CÔNG:


CÔNG TY TNHH VIỄN THÔNG SÁNG TẠO
THUẬN PHONG (INNOTEL)
55/31 TRẦN ĐÌNH XU, P. CẦU KHO, Q. 1, HCM
Tel: (84 28) 3 862 1119 || Fax: (84 28) 3 863 0366

CHỈ HUY TRƯỞNG:

NGUYỄN ĐỨC TIẾN

NGƯỜI KIỂM TRA:

NGƯỜI LẬP:

TÊN BẢN VẼ:

DRAWING LIST

NGÀY HT:

07/11/2022

CHỈNH SỬA:


01

MÃ BẢN VẼ:

IT-01

HỒ SƠ
THAM CHIẾU:

- ELV1-1-ELV1-02 - SDNL KHOI KS
- ELV1-1-ELV1-02 - SDNL KHOI MLM

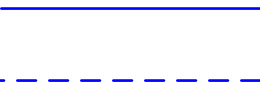DANH MỤC KÝ HIỆU VÀ CHÚ THÍCH	
KÝ HIỆU / HÌNH ẢNH	TÊN / MÔ TẢ
	10G (MM fiber)
	DAC 40G (for Stacking)
	DAC 10G (for Stacking)
	CORE SWITCH
	ACCESS SWITCH
	WIRELESS CONTROLLER

DỰ ÁN:

TỔ HỢP KHÁCH SẠN, CĂN HỘ DỊCH VỤ MARRIOTT VÀ NHÀ Ở ĐỂ BÁN

ĐỊA ĐIỂM XÂY DỰNG:

58 BẠCH ĐẰNG, P. HẢI CHÂU 1, Q. HẢI CHÂU, TP. ĐÀ NẴNG

CHỦ ĐẦU TƯ:

CÔNG TY CỔ PHẦN ĐỊA ỐC FOODINCO

ĐỊA CHỈ:

58 BẠCH ĐẰNG, P. HẢI CHÂU 1, Q. HẢI CHÂU, TP. ĐÀ NẴNG

BAN QUẢN LÝ DỰ ÁN:

TƯ VẤN GIÁM SÁT:

CN CÔNG TY TNHH APAVE CHÂU Á - THÁI BÌNH DƯƠNG TẠI ĐÀ NẴNG

NGUYỄN ĐĂNG HÙNG

ĐƠN VỊ NHÀ THẦU CHÍNH:

CÔNG TY CỔ PHẦN ALPHANAM E&C

NHÀ THẦU THI CÔNG:



CÔNG TY TNHH VIỄN THÔNG SÁNG TẠO THUẬN PHONG (INNOTEL)

55/31 TRẦN ĐÌNH XU, P. CẦU KHO, Q. 1, HCM
Tel: (84 28) 3 862 1119 || Fax: (84 28) 3 863 0366

CHỈ HUY TRƯỞNG:

NGUYỄN ĐỨC TIẾN

NGƯỜI KIỂM TRA:

NGƯỜI LẬP:

TÊN BẢN VẼ:

LEGEND AND SYMBOL LIST

NGÀY HT:

07/11/2022

CHỈNH SỬA:

01


MÃ BẢN VẼ:

IT-02


HỒ SƠ THAM CHIẾU:

- ELV1-1-ELV1-02 - SDNL KHOI KS


- ELV1-1-ELV1-02 - SDNL KHOI MLM

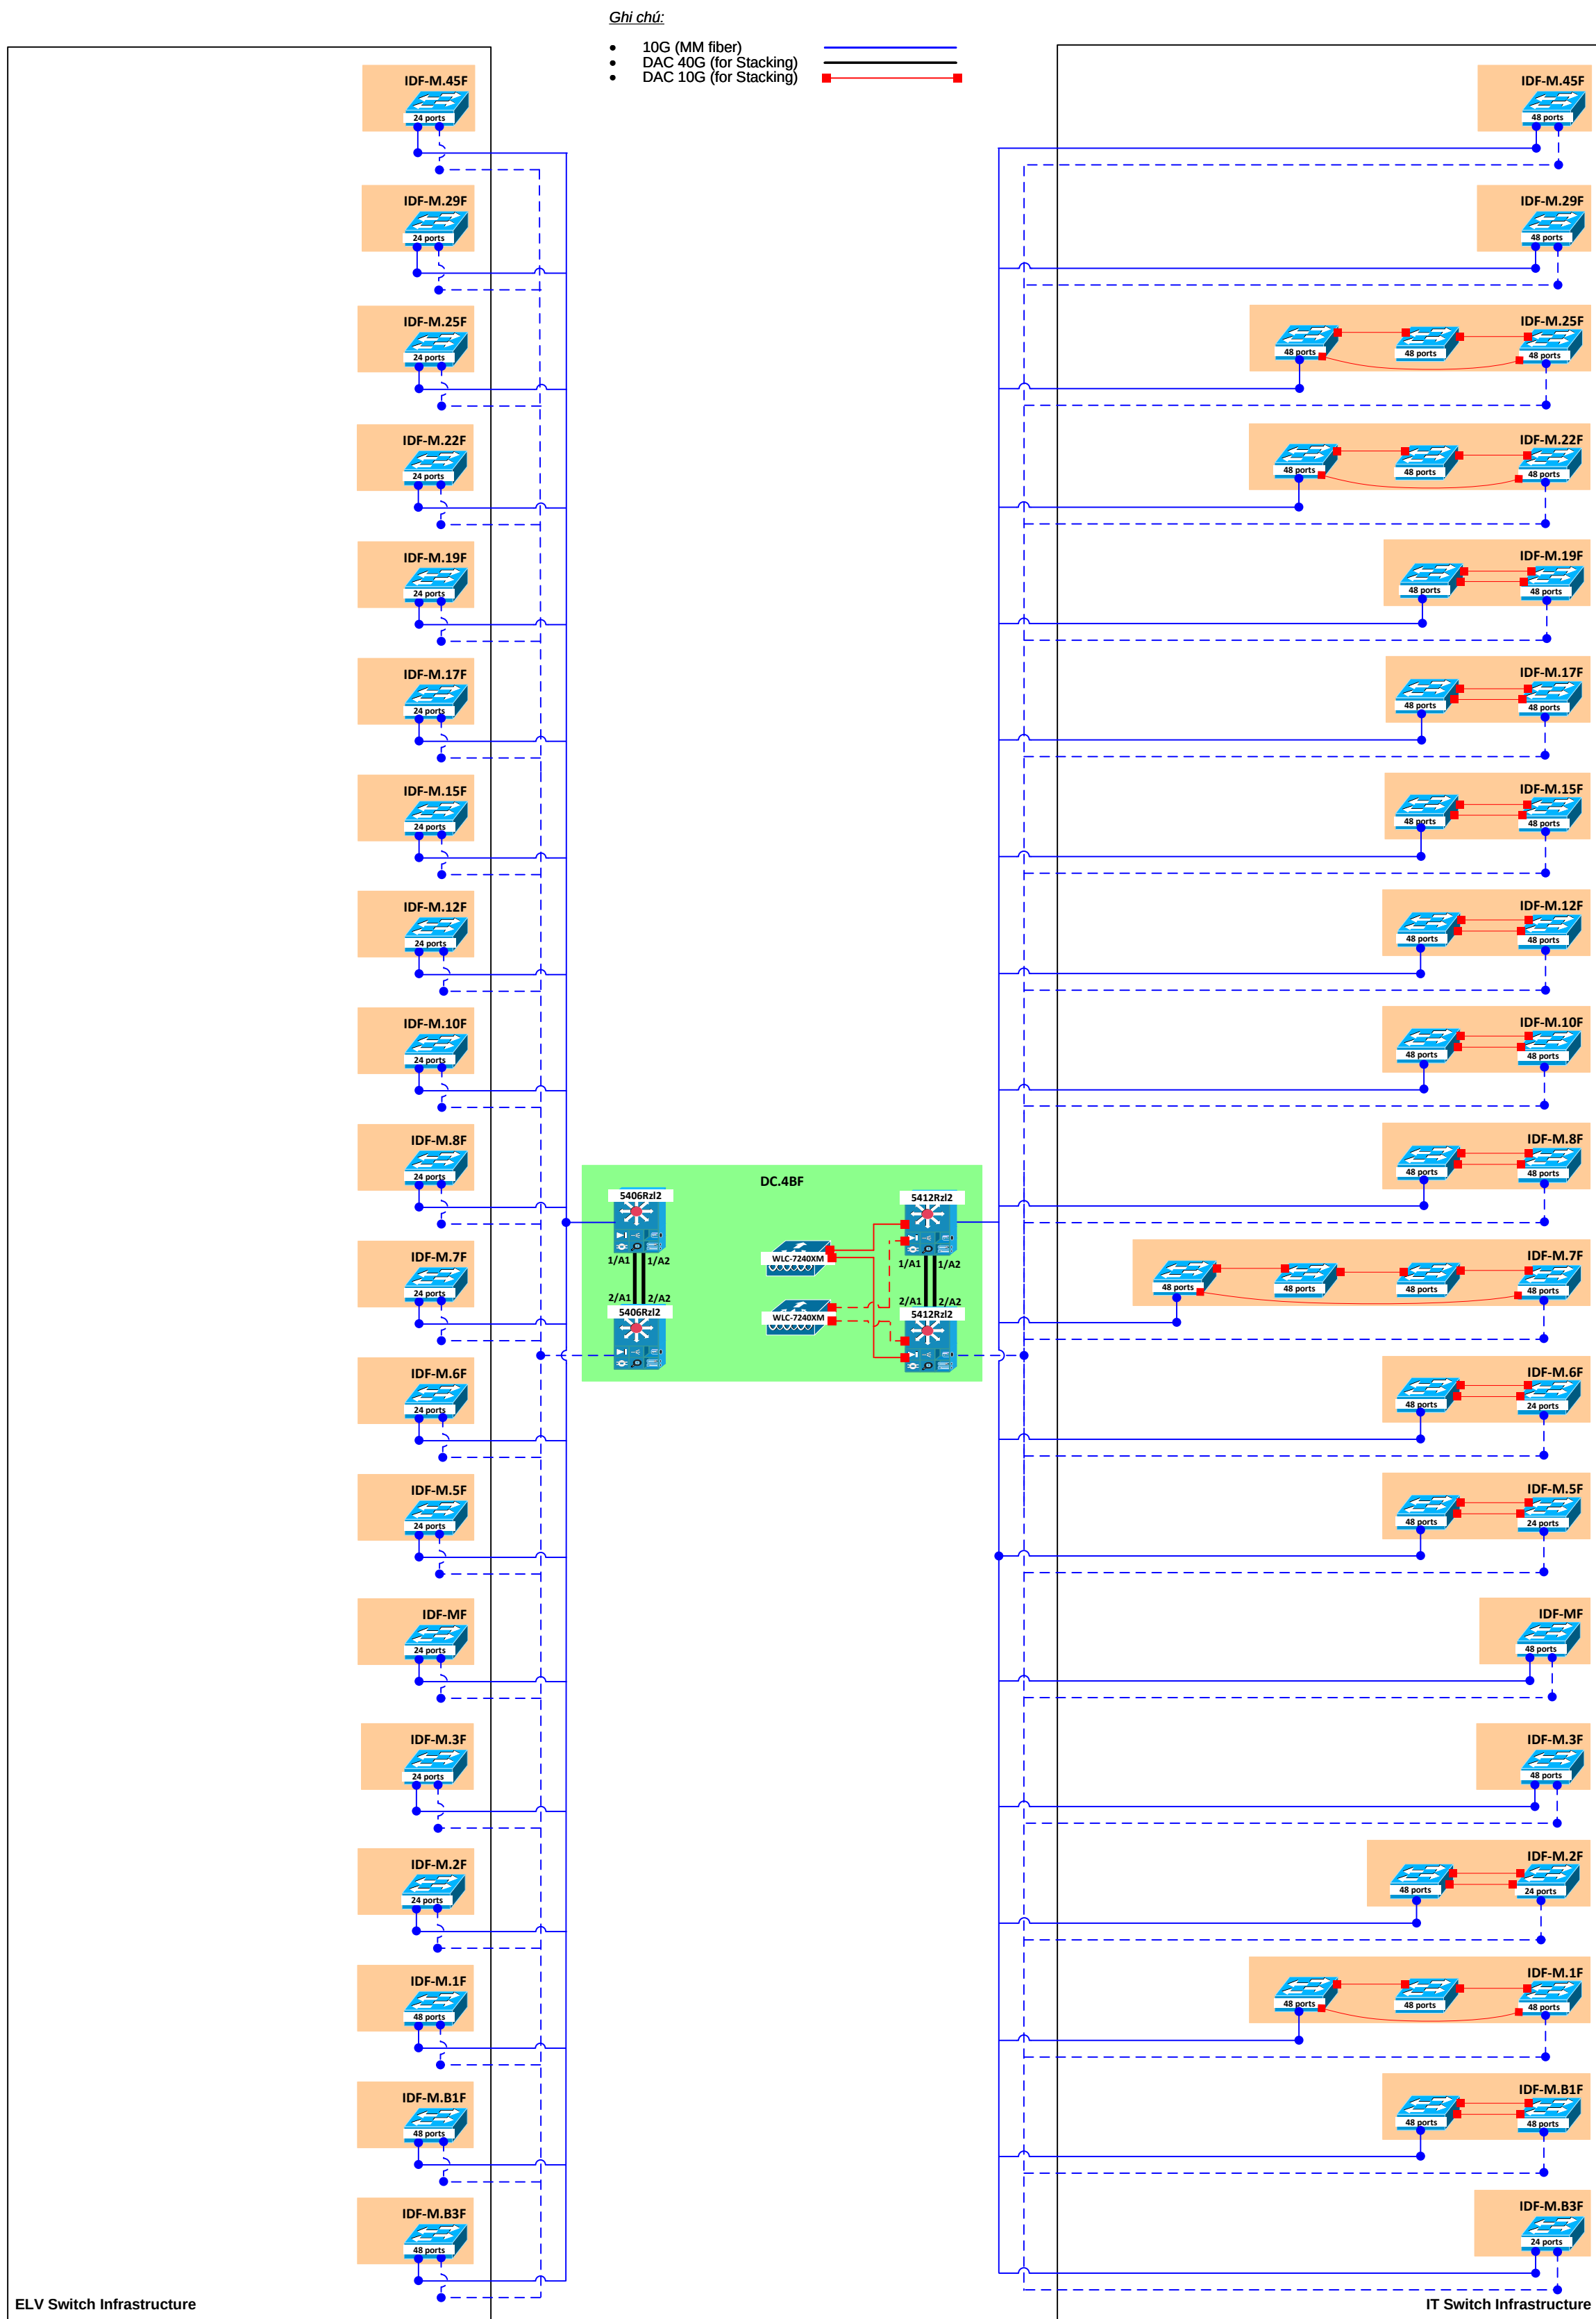


DỰ ÁN:	
TỔ HỢP KHÁCH SẠN, CĂN HỘ DỊCH VỤ MARRIOTT VÀ NHÀ Ở ĐỂ BÁN	
ĐỊA ĐIỂM XÂY DỰNG: 58 BẠCH ĐẰNG, P. HẢI CHÂU 1, Q. HẢI CHÂU, TP. ĐÀ NẴNG	
CHỦ ĐẦU TƯ: CÔNG TY CỔ PHẦN ĐỊA ỐC FOODINCO	
ĐỊA CHỈ: 58 BẠCH ĐẰNG, P. HẢI CHÂU 1, Q. HẢI CHÂU, TP. ĐÀ NẴNG	
BAN QUẢN LÝ DỰ ÁN:	
TƯ VẤN GIÁM SÁT:	
CN CÔNG TY TNHH APAVE CHÂU Á - THÁI BÌNH DƯƠNG TẠI ĐÀ NẴNG	
NGUYỄN ĐĂNG HÙNG	
ĐƠN VỊ NHÀ THẦU CHÍNH:	
CÔNG TY CỔ PHẦN ALPHANAM E&C	
NHÀ THẦU THI CÔNG:	
 CÔNG TY TNHH VIỄN THÔNG SÁNG TẠO THUẬN PHONG (INNOTEL)	
55/31 TRẦN ĐÌNH XU, P. CẦU KHO, Q. 1, HCM Tel: (84 28) 3 862 1119 Fax: (84 28) 3 863 0366	
CHỈ HUY TRƯỞNG:	
NGUYỄN ĐỨC TIẾN	
NGƯỜI KIỂM TRA:	
NGƯỜI LẬP:	
TÊN BẢN VẼ:	
NETWORK DIAGRAM_CY & MEA	
NGÀY HT:	07/11/2022
CHÍNH SỬA:	01
MÃ BẢN VẼ:	CY-MEA-DIAGRAM
HỒ SƠ THAM CHIẾU:	- ELV1-1-ELV1-02 - SDNL KHOI KS - ELV1-1-ELV1-02 - SDNL KHOI MLM

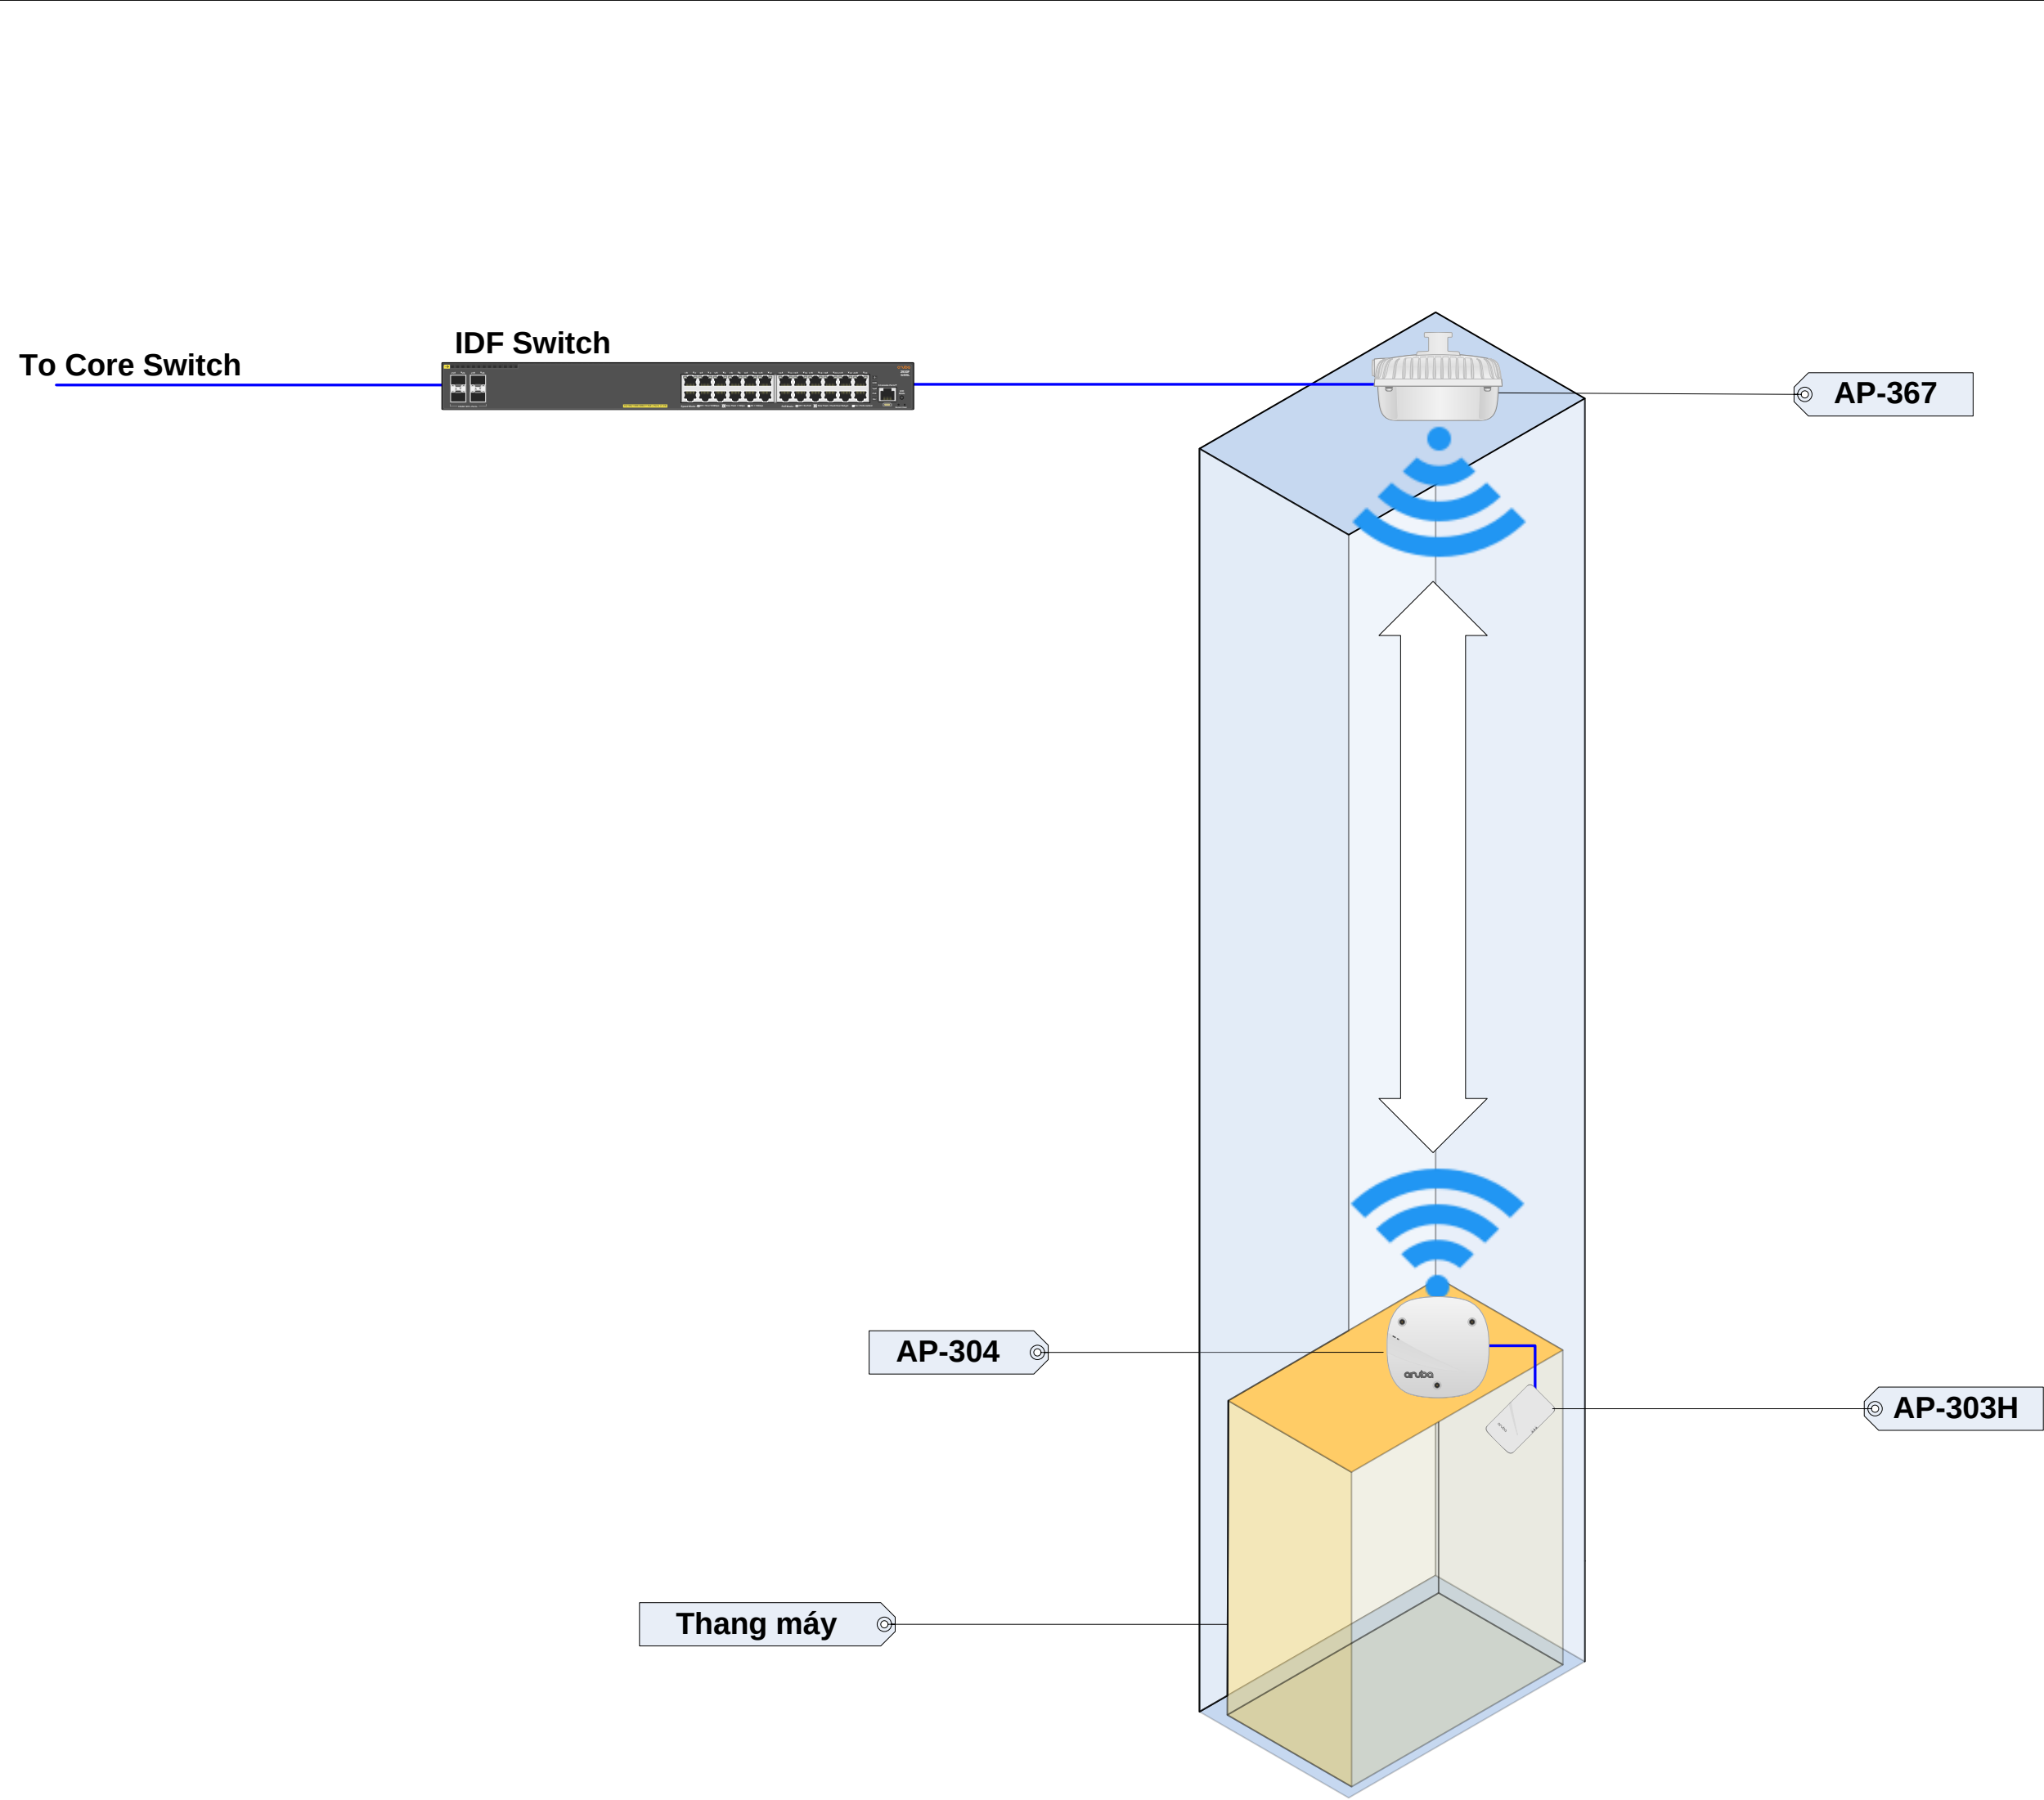


Dự án:		TỔ HỢP KHÁCH SẠN, CĂN HỘ DỊCH VỤ MARRIOTT VÀ NHÀ Ở ĐỂ BÁN	
Địa điểm xây dựng:		58 Bạch Đằng, P. Hải Châu 1, Q. Hải Châu, TP. Đà Nẵng	
Chủ đầu tư:		CÔNG TY CỔ PHẦN ĐỊA ỐC FOODINCO	
Địa chỉ:		58 Bạch Đằng, P. Hải Châu 1, Q. Hải Châu, TP. Đà Nẵng	
Ban quản lý dự án:			
Tư vấn giám sát:		CN CÔNG TY TNHH APAVE CHÂU Á - THÁI BÌNH DƯƠNG TẠI ĐÀ NẴNG	
		NGUYỄN ĐĂNG HÙNG	
Đơn vị nhà thầu chính:		CÔNG TY CỔ PHẦN ALPHANAM E&C	
Nhà thầu thi công:		innotel maximizing your access CÔNG TY TNHH VIỄN THÔNG SÁNG TẠO THUẬN PHONG (INNOTEL) 55/31 TRẦN ĐÌNH XU, P. CẦU KHO, Q. 1, HCM Tel: (84 28) 3 862 1119 Fax: (84 28) 3 863 0366	
Chỉ huy trưởng:		NGUYỄN ĐỨC TIẾN	
Người kiểm tra:			
Người lập:			
Tên bản vẽ:		LIFT	
Ngày HT:		07/11/2022	
Chỉnh sửa:		01	
Mã bản vẽ:		IT-LIFT	
Hồ sơ tham chiếu:		- ELV1-1-ELV1-02 - SDNL KHOI KS - ELV1-1-ELV1-02 - SDNL KHOI MLM	

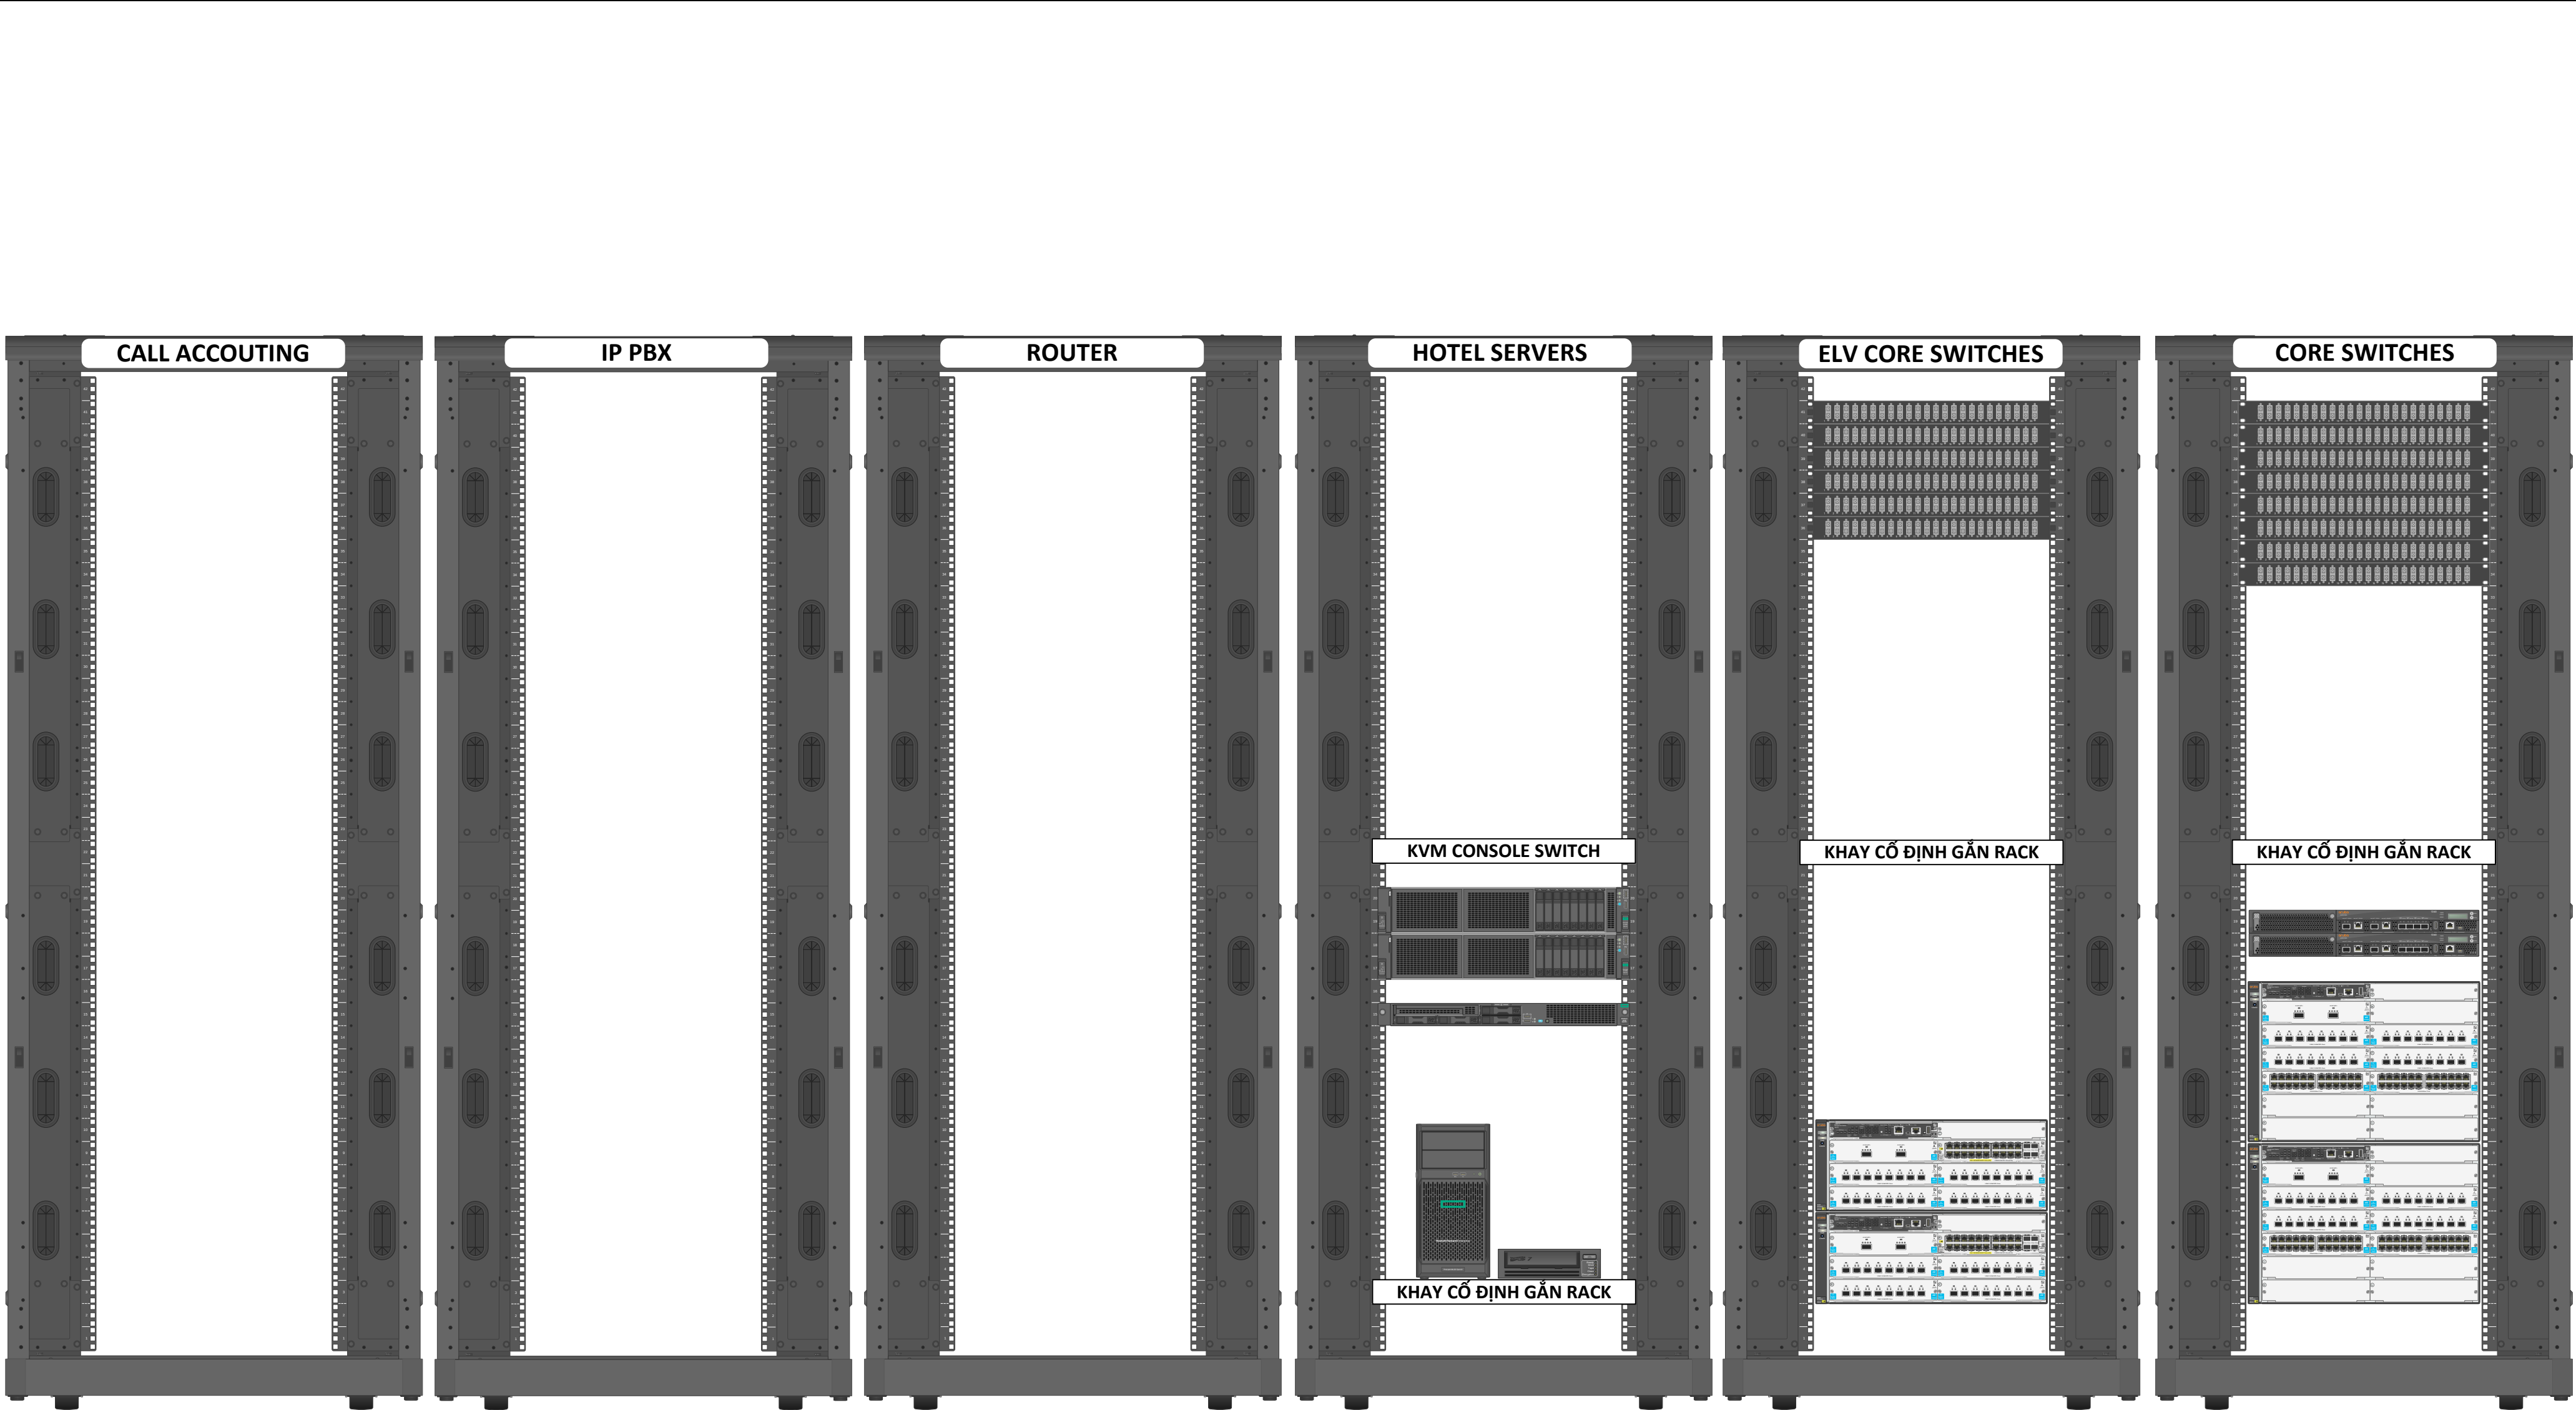


DỰ ÁN:		TỔ HỢP KHÁCH SẠN, CĂN HỘ DỊCH VỤ MARRIOTT VÀ NHÀ Ở ĐỂ BÁN	
ĐỊA ĐIỂM XÂY DỰNG:		58 BẠCH ĐẰNG, P. HẢI CHÂU 1, Q. HẢI CHÂU, TP. ĐÀ NẴNG	
CHỦ ĐẦU TƯ:		CÔNG TY CỔ PHẦN ĐỊA ỐC FOODINCO	
ĐỊA CHỈ:		58 BẠCH ĐẰNG, P. HẢI CHÂU 1, Q. HẢI CHÂU, TP. ĐÀ NẴNG	
BAN QUẢN LÝ DỰ ÁN:			
TƯ VẤN GIÁM SÁT:		CN CÔNG TY TNHH APAVE CHÂU Á - THÁI BÌNH DƯƠNG TẠI ĐÀ NẴNG	
		NGUYỄN ĐĂNG HÙNG	
ĐƠN VỊ NHÀ THẦU CHÍNH:		CÔNG TY CỔ PHẦN ALPHANAM E&C	
NHÀ THẦU THI CÔNG:		 CÔNG TY TNHH VIỄN THÔNG SÁNG TẠO THUẬN PHONG (INNOTEL) 55/31 TRẦN ĐÌNH XU, P. CẦU KHO, Q. 1, HCM Tel: (84 28) 3 862 1119 Fax: (84 28) 3 863 0366	
CHỈ HUY TRƯỞNG:		NGUYỄN ĐỨC TIẾN	
NGƯỜI KIỂM TRA:			
NGƯỜI LẬP:			
TÊN BẢN VẼ:		RACK LAYOUT DATA CENTER – 4BF	
NGÀY HT:		07/11/2022	
CHỈNH SỬA:		01	
MÃ BẢN VẼ:		DC-4BF	
HỒ SƠ THAM CHIẾU:		- ELV1-1-ELV1-02 - SDNL KHOI KS - ELV1-1-ELV1-02 - SDNL KHOI MLM	

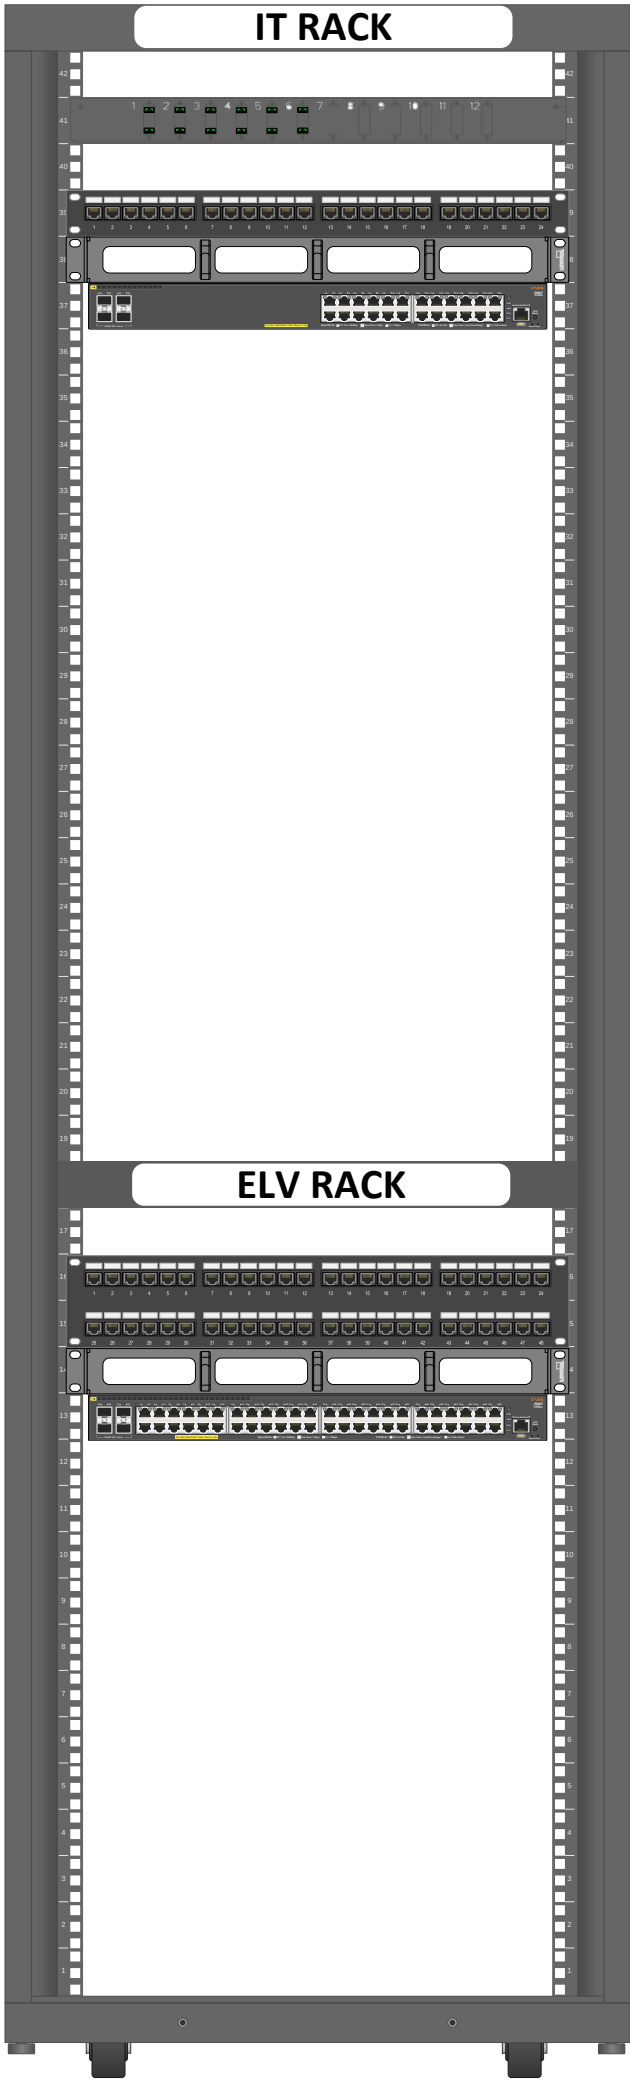


DỰ ÁN: TỔ HỢP KHÁCH SẠN, CĂN HỘ DỊCH VỤ MARRIOTT VÀ NHÀ Ở ĐỂ BÁN ĐỊA ĐIỂM XÂY DỰNG: 58 BẠCH ĐẰNG, P. HẢI CHÂU 1, Q. HẢI CHÂU, TP. ĐÀ NẴNG	
CHỦ ĐẦU TƯ: CÔNG TY CỔ PHẦN ĐỊA ỐC FOODINCO ĐỊA CHỈ: 58 BẠCH ĐẰNG, P. HẢI CHÂU 1, Q. HẢI CHÂU, TP. ĐÀ NẴNG	
BAN QUẢN LÝ DỰ ÁN:	
TƯ VẤN GIÁM SÁT: CN CÔNG TY TNHH APAVE CHÂU Á - THÁI BÌNH DƯƠNG TẠI ĐÀ NẴNG NGUYỄN ĐĂNG HÙNG	
ĐƠN VỊ NHÀ THẦU CHÍNH: CÔNG TY CỔ PHẦN ALPHANAM E&C	
NHÀ THẦU THI CÔNG:  CÔNG TY TNHH VIỄN THÔNG SÁNG TẠO THUẬN PHONG (INNOTEL) 55/31 TRẦN ĐÌNH XU, P. CẦU KHO, Q. 1, HCM Tel: (84 28) 3 862 1119 Fax: (84 28) 3 863 0366	
CHỈ HUY TRƯỞNG: NGUYỄN ĐỨC TIẾN	
NGƯỜI KIỂM TRA:	
NGƯỜI LẬP:	
TÊN BẢN VẼ: RACK LAYOUT IDF-M.B3F	
NGÀY HT:	07/11/2022
CHỈNH SỬA:	01
MÃ BẢN VẼ:	IDF-M.B3F
HỒ SƠ THAM CHIẾU:	- ELV1-1-ELV1-02 - SDNL KHOI KS - ELV1-1-ELV1-02 - SDNL KHOI MLM

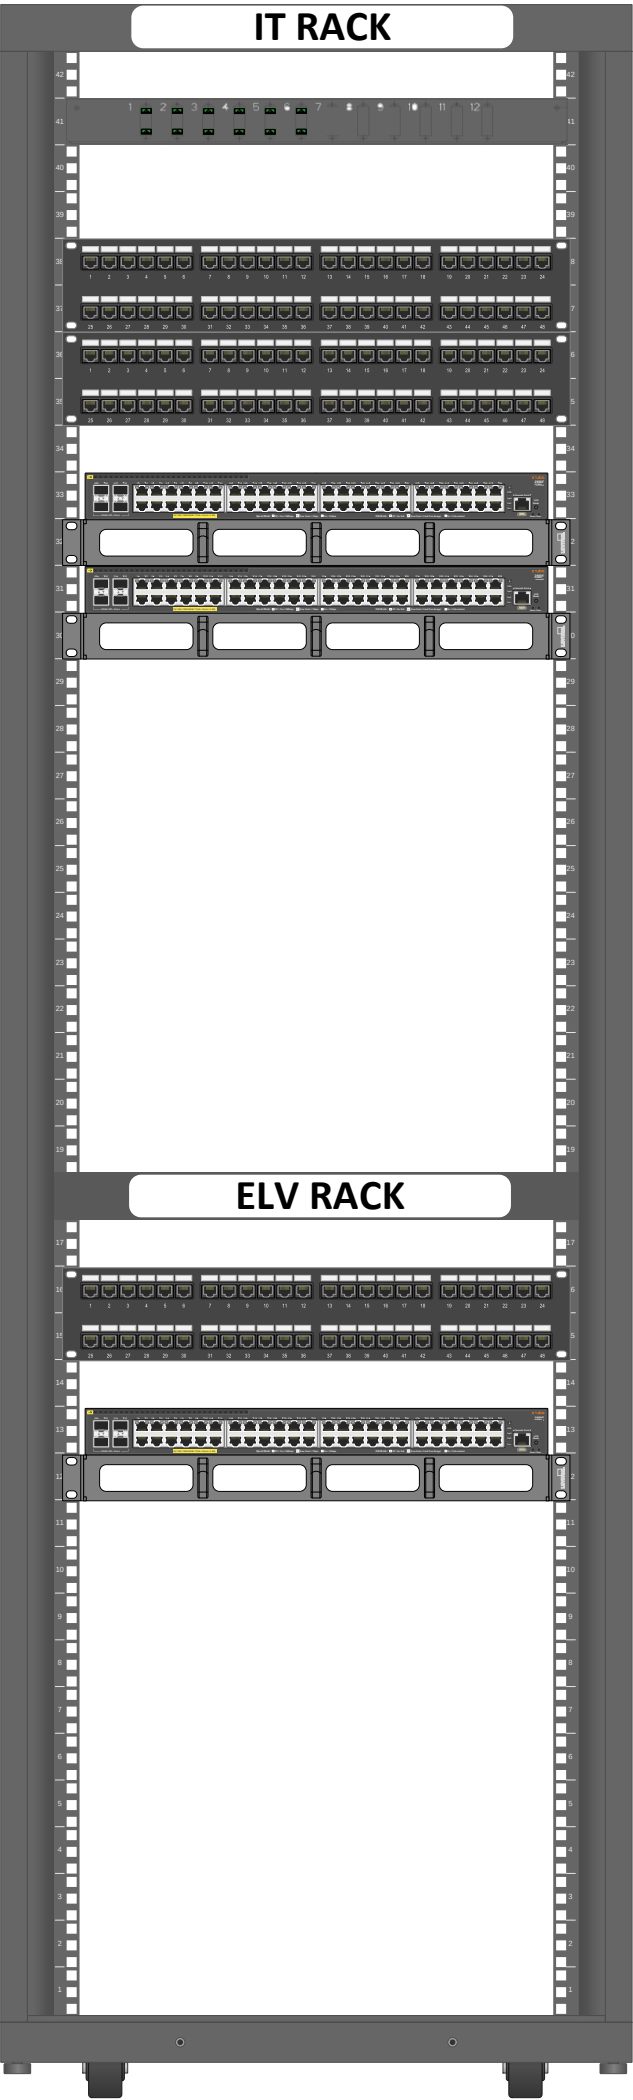


DỰ ÁN: TỔ HỢP KHÁCH SẠN, CĂN HỘ DỊCH VỤ MARRIOTT VÀ NHÀ Ở ĐỂ BÁN ĐỊA ĐIỂM XÂY DỰNG: 58 BẠCH ĐẰNG, P. HẢI CHÂU 1, Q. HẢI CHÂU, TP. ĐÀ NẴNG	
CHỦ ĐẦU TƯ: CÔNG TY CỔ PHẦN ĐỊA ỐC FOODINCO ĐỊA CHỈ: 58 BẠCH ĐẰNG, P. HẢI CHÂU 1, Q. HẢI CHÂU, TP. ĐÀ NẴNG	
BAN QUẢN LÝ DỰ ÁN:	
TƯ VẤN GIÁM SÁT: CN CÔNG TY TNHH APAVE CHÂU Á - THÁI BÌNH DƯƠNG TẠI ĐÀ NẴNG NGUYỄN ĐĂNG HÙNG	
ĐƠN VỊ NHÀ THẦU CHÍNH: CÔNG TY CỔ PHẦN ALPHANAM E&C	
NHÀ THẦU THI CÔNG:  CÔNG TY TNHH VIỄN THÔNG SÁNG TẠO THUẬN PHONG (INNOTEL) 55/31 TRẦN ĐÌNH XU, P. CẦU KHO, Q. 1, HCM Tel: (84 28) 3 862 1119 Fax: (84 28) 3 863 0366	
CHỈ HUY TRƯỞNG:	
NGUYỄN ĐỨC TIẾN	
NGƯỜI KIỂM TRA:	
NGƯỜI LẬP:	
TÊN BẢN VẼ: RACK LAYOUT IDF-M.B1F	
NGÀY HT:	07/11/2022
CHỈNH SỬA:	01
MÃ BẢN VẼ:	IDF-M.B1F
HỒ SƠ THAM CHIẾU:	- ELV1-1-ELV1-02 - SDNL KHOI KS - ELV1-1-ELV1-02 - SDNL KHOI MLM

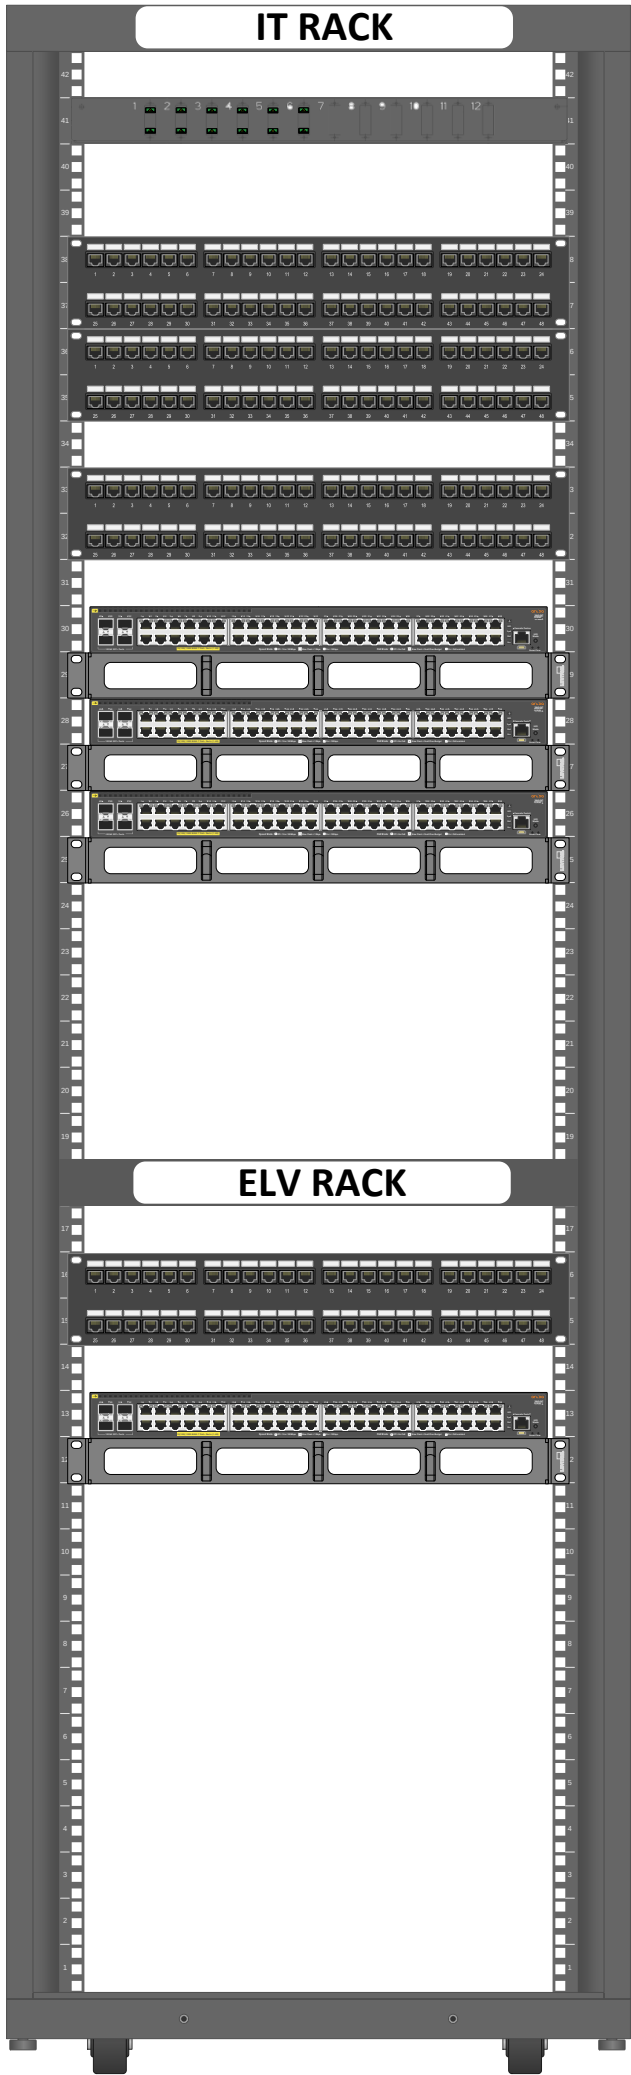


DỰ ÁN: TỔ HỢP KHÁCH SẠN, CĂN HỘ DỊCH VỤ MARRIOTT VÀ NHÀ Ở ĐỂ BÁN ĐỊA ĐIỂM XÂY DỰNG: 58 BẠCH ĐẰNG, P. HẢI CHÂU 1, Q. HẢI CHÂU, TP. ĐÀ NẴNG	
CHỦ ĐẦU TƯ: CÔNG TY CỔ PHẦN ĐỊA ỐC FOODINCO ĐỊA CHỈ: 58 BẠCH ĐẰNG, P. HẢI CHÂU 1, Q. HẢI CHÂU, TP. ĐÀ NẴNG	
BAN QUẢN LÝ DỰ ÁN:	
TƯ VẤN GIÁM SÁT: CN CÔNG TY TNHH APAVE CHÂU Á - THÁI BÌNH DƯƠNG TẠI ĐÀ NẴNG NGUYỄN ĐĂNG HÙNG	
ĐƠN VỊ NHÀ THẦU CHÍNH: CÔNG TY CỔ PHẦN ALPHANAM E&C	
NHÀ THẦU THI CÔNG:  CÔNG TY TNHH VIỄN THÔNG SÁNG TẠO THUẬN PHONG (INNOTEL) 55/31 TRẦN ĐÌNH XU, P. CẦU KHO, Q. 1, HCM Tel: (84 28) 3 862 1119 Fax: (84 28) 3 863 0366	
CHỈ HUY TRƯỞNG:	
NGƯỜI KIỂM TRA:	
NGƯỜI LẬP:	
TÊN BẢN VẼ: RACK LAYOUT IDF-M.1F	
NGÀY HT:	07/11/2022
CHỈNH SỬA:	01
MÃ BẢN VẼ:	IDF-M.1F
HỒ SƠ THAM CHIẾU:	- ELV1-1-ELV1-02 - SDNL KHOI KS - ELV1-1-ELV1-02 - SDNL KHOI MLM

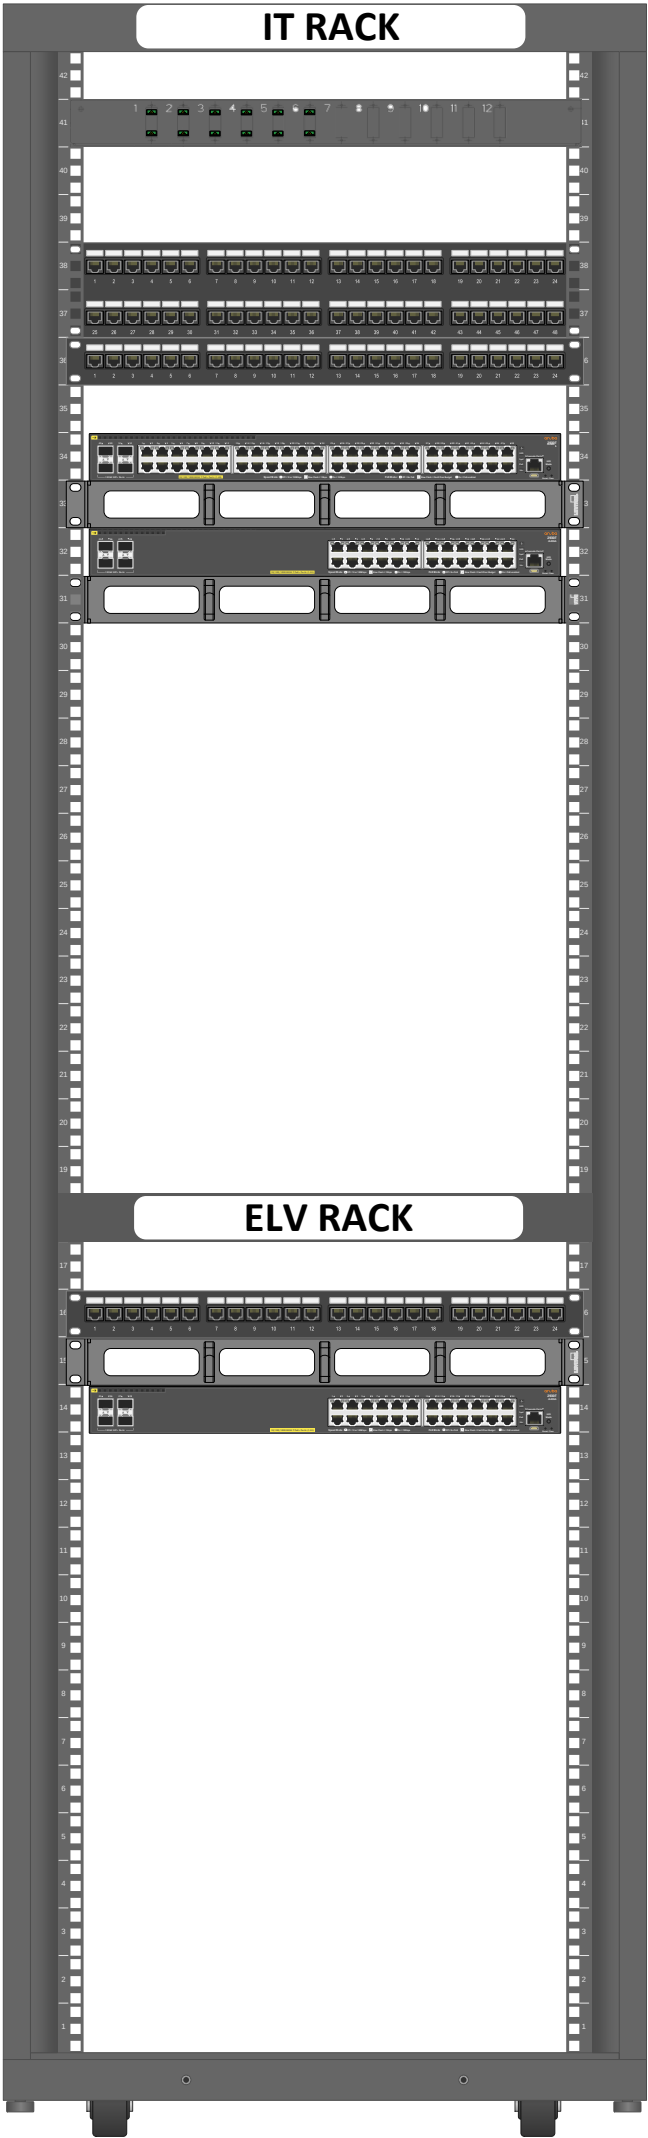


DỰ ÁN: TỔ HỢP KHÁCH SẠN, CĂN HỘ DỊCH VỤ MARRIOTT VÀ NHÀ Ở ĐỂ BÁN ĐỊA ĐIỂM XÂY DỰNG: 58 BẠCH ĐẰNG, P. HẢI CHÂU 1, Q. HẢI CHÂU, TP. ĐÀ NẴNG	
CHỦ ĐẦU TƯ: CÔNG TY CỔ PHẦN ĐỊA ỐC FOODINCO ĐỊA CHỈ: 58 BẠCH ĐẰNG, P. HẢI CHÂU 1, Q. HẢI CHÂU, TP. ĐÀ NẴNG	
BAN QUẢN LÝ DỰ ÁN:	
TƯ VẤN GIÁM SÁT: CN CÔNG TY TNHH APAVE CHÂU Á - THÁI BÌNH DƯƠNG TẠI ĐÀ NẴNG NGUYỄN ĐĂNG HÙNG	
ĐƠN VỊ NHÀ THẦU CHÍNH: CÔNG TY CỔ PHẦN ALPHANAM E&C	
NHÀ THẦU THI CÔNG:  CÔNG TY TNHH VIỄN THÔNG SÁNG TẠO THUẬN PHONG (INNOTEL) 55/31 TRẦN ĐÌNH XU, P. CẦU KHO, Q. 1, HCM Tel: (84 28) 3 862 1119 Fax: (84 28) 3 863 0366	
CHỈ HUY TRƯỞNG:	
NGUYỄN ĐỨC TIẾN	
NGƯỜI KIỂM TRA:	
NGƯỜI LẬP:	
TÊN BẢN VẼ: RACK LAYOUT IDF-M.2F	
NGÀY HT:	07/11/2022
CHỈNH SỬA:	01
MÃ BẢN VẼ:	IDF-M.2F
HỒ SƠ THAM CHIẾU:	- ELV1-1-ELV1-02 - SDNL KHOI KS - ELV1-1-ELV1-02 - SDNL KHOI MLM

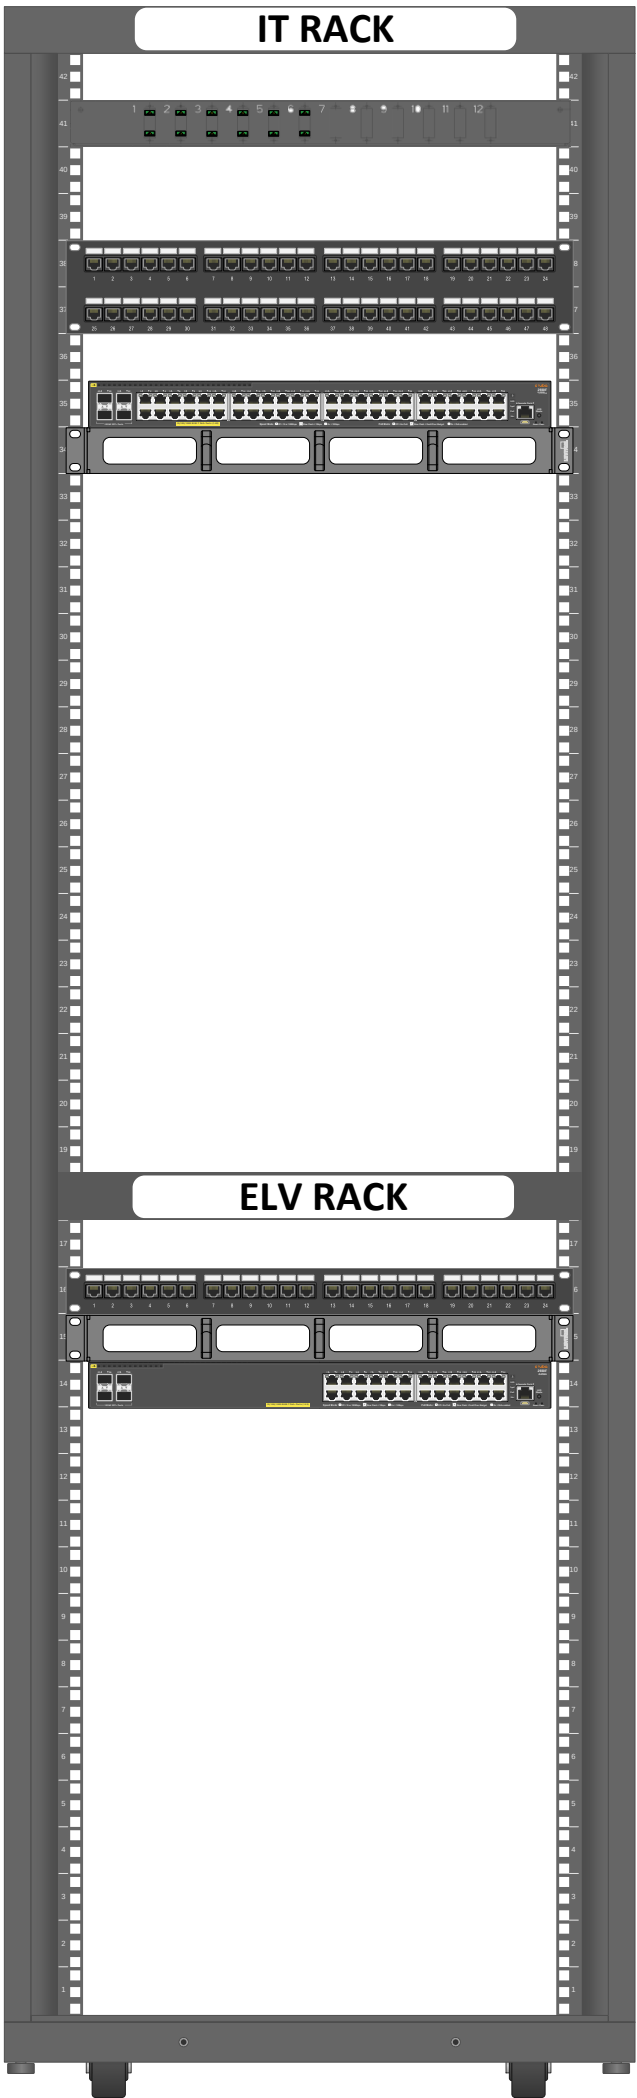


DỰ ÁN: TỔ HỢP KHÁCH SẠN, CĂN HỘ DỊCH VỤ MARRIOTT VÀ NHÀ Ở ĐỂ BÁN ĐỊA ĐIỂM XÂY DỰNG: 58 BẠCH ĐẰNG, P. HẢI CHÂU 1, Q. HẢI CHÂU, TP. ĐÀ NẴNG	
CHỦ ĐẦU TƯ: CÔNG TY CỔ PHẦN ĐỊA ỐC FOODINCO ĐỊA CHỈ: 58 BẠCH ĐẰNG, P. HẢI CHÂU 1, Q. HẢI CHÂU, TP. ĐÀ NẴNG	
BAN QUẢN LÝ DỰ ÁN:	
TƯ VẤN GIÁM SÁT: CN CÔNG TY TNHH APAVE CHÂU Á - THÁI BÌNH DƯƠNG TẠI ĐÀ NẴNG NGUYỄN ĐĂNG HÙNG	
ĐƠN VỊ NHÀ THẦU CHÍNH: CÔNG TY CỔ PHẦN ALPHANAM E&C	
NHÀ THẦU THI CÔNG:  CÔNG TY TNHH VIỄN THÔNG SÁNG TẠO THUẬN PHONG (INNOTEL) 55/31 TRẦN ĐÌNH XU, P. CẦU KHO, Q. 1, HCM Tel: (84 28) 3 862 1119 Fax: (84 28) 3 863 0366	
CHỈ HUY TRƯỞNG:	
NGUYỄN ĐỨC TIẾN	
NGƯỜI KIỂM TRA:	
NGƯỜI LẬP:	
TÊN BẢN VẼ: RACK LAYOUT IDF-M.3F	
NGÀY HT:	07/11/2022
CHỈNH SỬA:	01
MÃ BẢN VẼ:	IDF-M.3F
HỒ SƠ THAM CHIẾU:	- ELV1-1-ELV1-02 - SDNL KHOI KS - ELV1-1-ELV1-02 - SDNL KHOI MLM

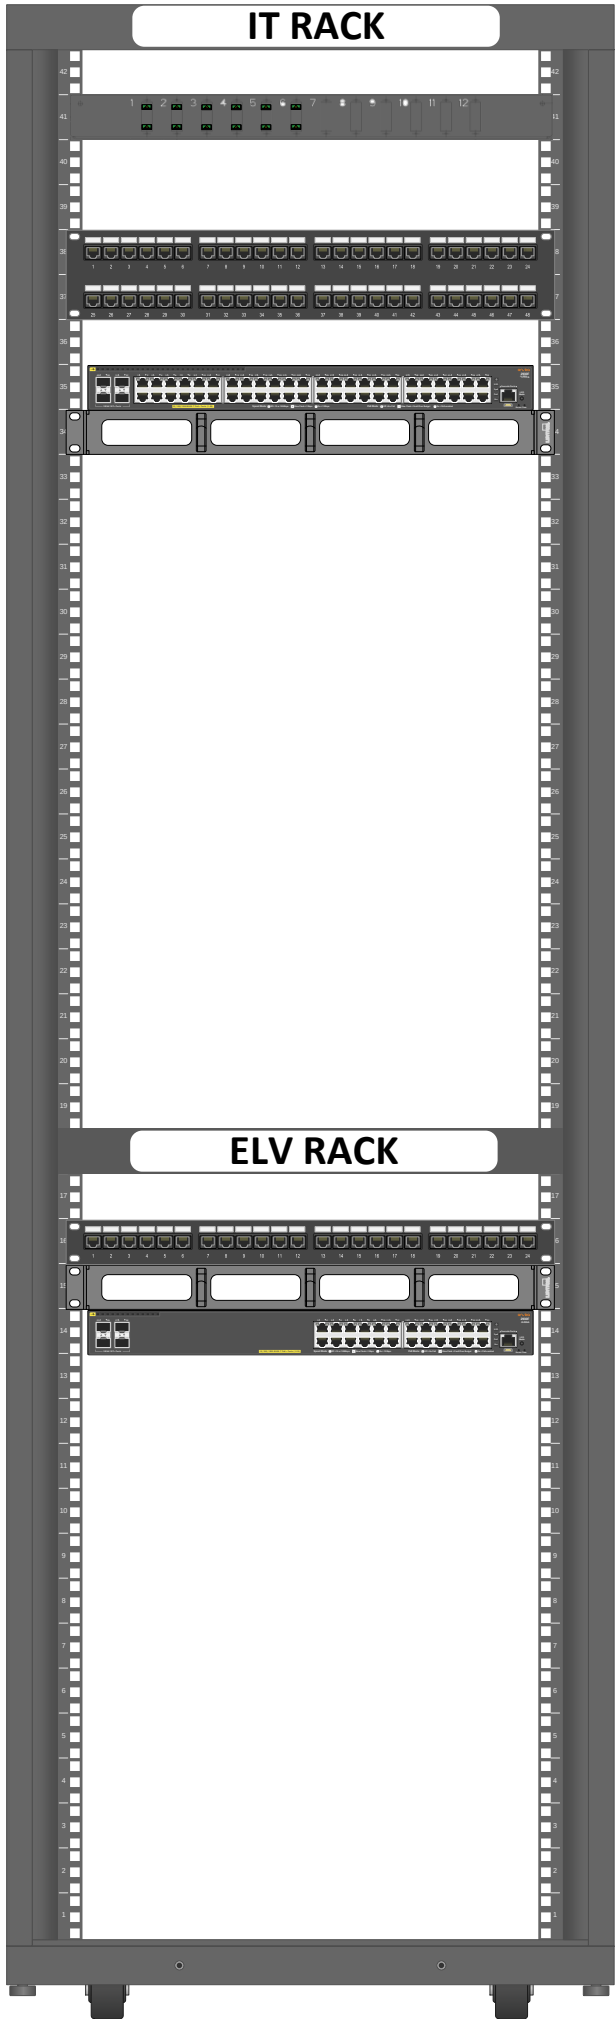


DỰ ÁN: TỔ HỢP KHÁCH SẠN, CĂN HỘ DỊCH VỤ MARRIOTT VÀ NHÀ Ở ĐỂ BÁN ĐỊA ĐIỂM XÂY DỰNG: 58 BẠCH ĐẰNG, P. HẢI CHÂU 1, Q. HẢI CHÂU, TP. ĐÀ NẴNG	
CHỦ ĐẦU TƯ: CÔNG TY CỔ PHẦN ĐỊA ỐC FOODINCO ĐỊA CHỈ: 58 BẠCH ĐẰNG, P. HẢI CHÂU 1, Q. HẢI CHÂU, TP. ĐÀ NẴNG	
BAN QUẢN LÝ DỰ ÁN:	
TƯ VẤN GIÁM SÁT: CN CÔNG TY TNHH APAVE CHÂU Á - THÁI BÌNH DƯƠNG TẠI ĐÀ NẴNG NGUYỄN ĐĂNG HÙNG	
ĐƠN VỊ NHÀ THẦU CHÍNH: CÔNG TY CỔ PHẦN ALPHANAM E&C	
NHÀ THẦU THI CÔNG:  CÔNG TY TNHH VIỄN THÔNG SÁNG TẠO THUẬN PHONG (INNOTEL) 55/31 TRẦN ĐÌNH XU, P. CẦU KHO, Q. 1, HCM Tel: (84 28) 3 862 1119 Fax: (84 28) 3 863 0366	
CHỈ HUY TRƯỞNG:	
NGUYỄN ĐỨC TIẾN	
NGƯỜI KIỂM TRA:	
NGƯỜI LẬP:	
TÊN BẢN VẼ: RACK LAYOUT IDF-MF	
NGÀY HT:	07/11/2022
CHỈNH SỬA:	01
MÃ BẢN VẼ:	IDF-MF
HỒ SƠ THAM CHIẾU:	- ELV1-1-ELV1-02 - SDNL KHOI KS - ELV1-1-ELV1-02 - SDNL KHOI MLM

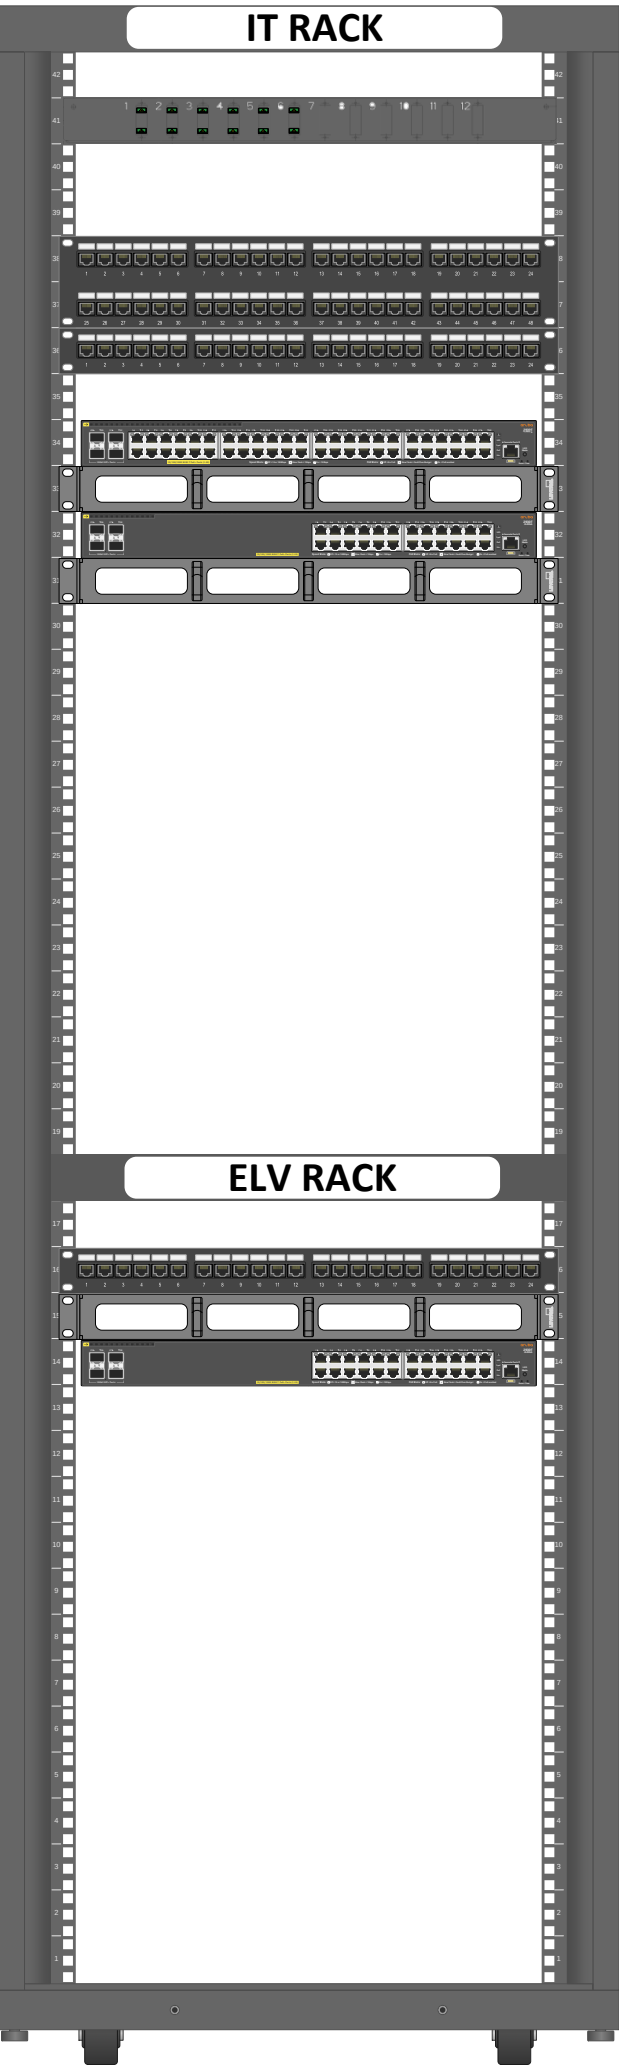


Dự án: TỔ HỢP KHÁCH SẠN, CĂN HỘ DỊCH VỤ MARRIOTT VÀ NHÀ Ở ĐỂ BÁN Địa điểm xây dựng: 58 Bạch Đằng, P. Hải Châu 1, Q. Hải Châu, TP. Đà Nẵng	
Chủ đầu tư: CÔNG TY CỔ PHẦN ĐỊA ỐC FOODINCO Địa chỉ: 58 Bạch Đằng, P. Hải Châu 1, Q. Hải Châu, TP. Đà Nẵng	
Ban quản lý dự án:	
Tư vấn giám sát: CN CÔNG TY TNHH APAVE CHÂU Á - THÁI BÌNH DƯƠNG TẠI ĐÀ NẴNG NGUYỄN ĐĂNG HÙNG	
Đơn vị nhà thầu chính: CÔNG TY CỔ PHẦN ALPHANAM E&C	
Nhà thầu thi công:  maximizing your access CÔNG TY TNHH VIỄN THÔNG SÁNG TẠO THUẬN PHONG (INNOTEL) 55/31 TRẦN ĐÌNH XU, P. CẦU KHO, Q. 1, HCM Tel: (84 28) 3 862 1119 Fax: (84 28) 3 863 0366	
Chỉ huy trưởng: NGUYỄN ĐỨC TIẾN	
Người kiểm tra:	
Người lập:	
Tên bản vẽ: RACK LAYOUT IDF-M.5F	
Ngày HT:	07/11/2022
Chỉnh sửa:	01
Mã bản vẽ:	IDF-M.5F
Hồ sơ tham chiếu:	- ELV1-1-ELV1-02 - SDNL KHOI KS - ELV1-1-ELV1-02 - SDNL KHOI MLM

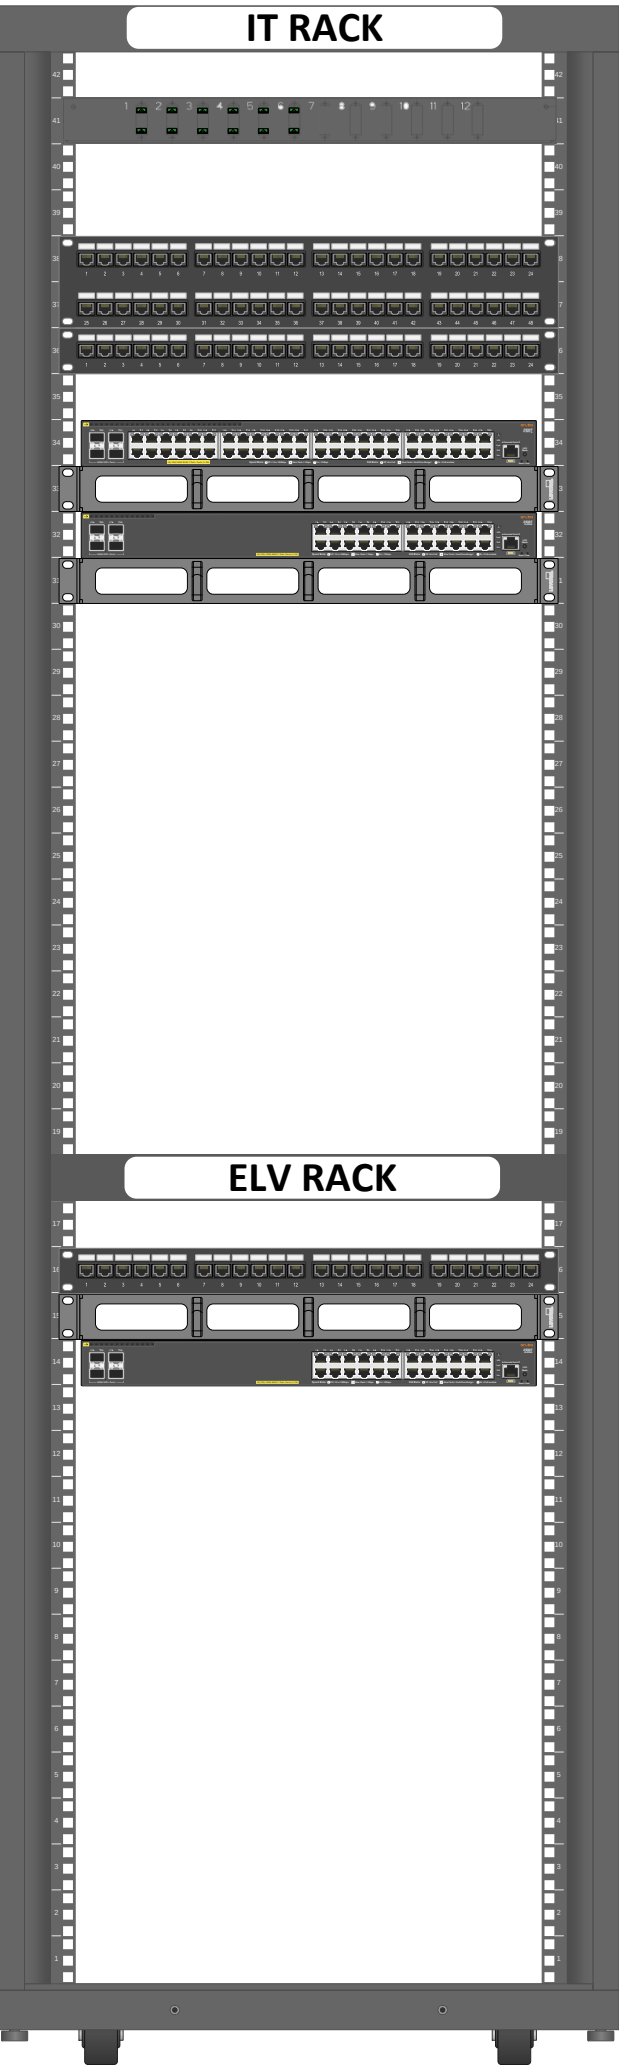


Dự án: TỔ HỢP KHÁCH SẠN, CĂN HỘ DỊCH VỤ MARRIOTT VÀ NHÀ Ở ĐỂ BÁN Địa điểm xây dựng: 58 Bạch Đằng, P. Hải Châu 1, Q. Hải Châu, TP. Đà Nẵng	
Chủ đầu tư: CÔNG TY CỔ PHẦN ĐỊA ỐC FOODINCO Địa chỉ: 58 Bạch Đằng, P. Hải Châu 1, Q. Hải Châu, TP. Đà Nẵng	
Ban quản lý dự án:	
Tư vấn giám sát: CN CÔNG TY TNHH APAVE CHÂU Á - THÁI BÌNH DƯƠNG TẠI ĐÀ NẴNG NGUYỄN ĐĂNG HÙNG	
Đơn vị nhà thầu chính: CÔNG TY CỔ PHẦN ALPHANAM E&C	
Nhà thầu thi công:  CÔNG TY TNHH VIỄN THÔNG SÁNG TẠO THUẬN PHONG (INNOTEL) 55/31 TRẦN ĐÌNH XU, P. CẦU KHO, Q. 1, HCM Tel: (84 28) 3 862 1119 Fax: (84 28) 3 863 0366	
Chỉ huy trưởng: NGUYỄN ĐỨC TIẾN	
Người kiểm tra:	
Người lập:	
Tên bản vẽ: RACK LAYOUT IDF-M.6F	
Ngày HT:	07/11/2022
Chỉnh sửa:	01
Mã bản vẽ:	IDF-M.6F
Hồ sơ tham chiếu:	- ELV1-1-ELV1-02 - SDNL KHOI KS - ELV1-1-ELV1-02 - SDNL KHOI MLM

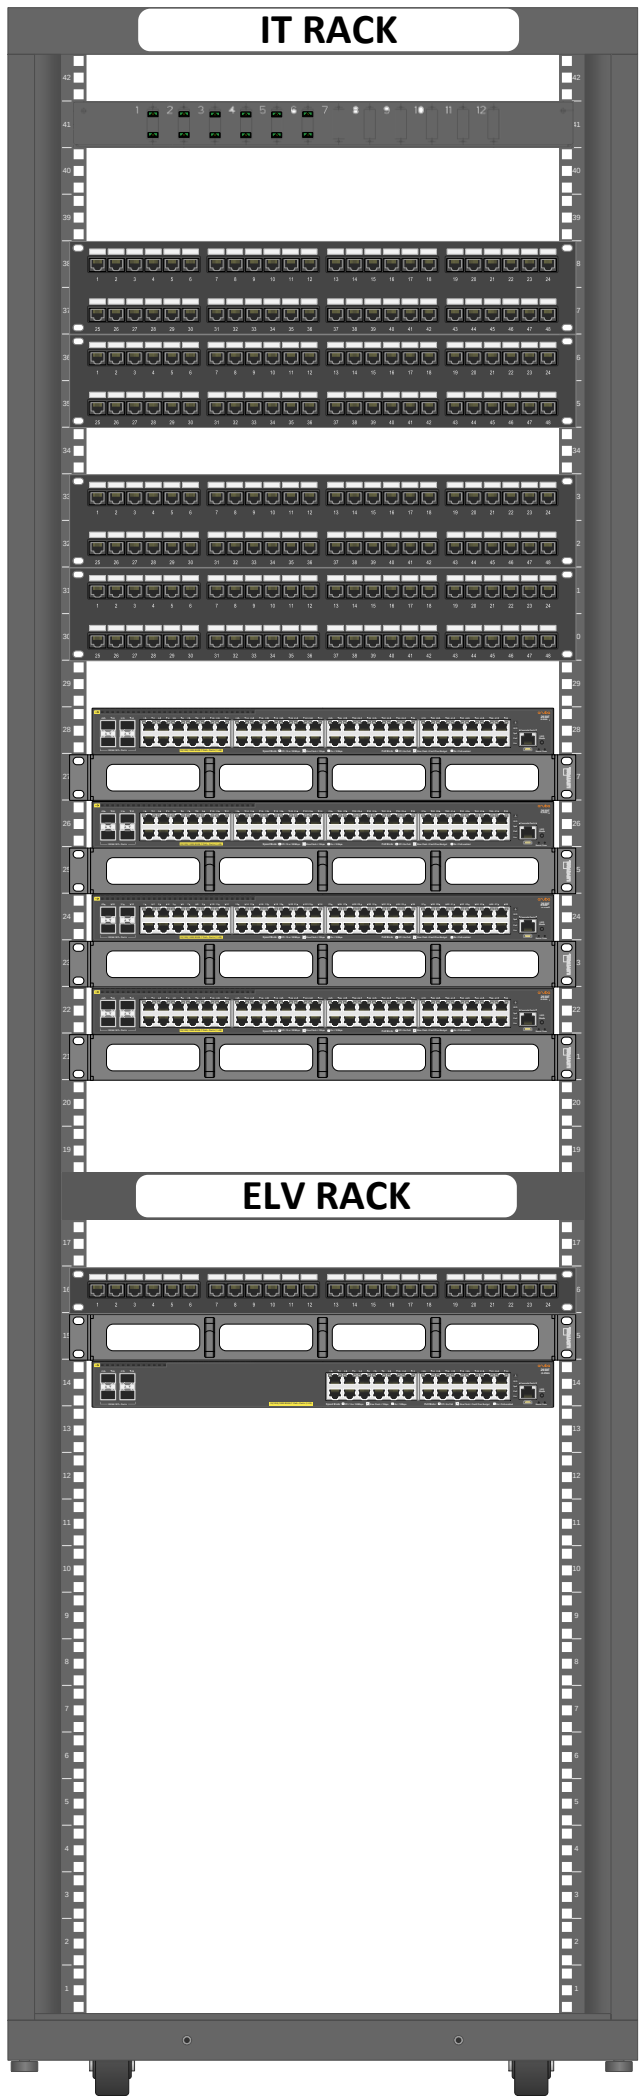


DỰ ÁN: TỔ HỢP KHÁCH SẠN, CĂN HỘ DỊCH VỤ MARRIOTT VÀ NHÀ Ở ĐỂ BÁN ĐỊA ĐIỂM XÂY DỰNG: 58 BẠCH ĐẰNG, P. HẢI CHÂU 1, Q. HẢI CHÂU, TP. ĐÀ NẴNG	
CHỦ ĐẦU TƯ: CÔNG TY CỔ PHẦN ĐỊA ỐC FOODINCO ĐỊA CHỈ: 58 BẠCH ĐẰNG, P. HẢI CHÂU 1, Q. HẢI CHÂU, TP. ĐÀ NẴNG	
BAN QUẢN LÝ DỰ ÁN:	
TƯ VẤN GIÁM SÁT: CN CÔNG TY TNHH APAVE CHÂU Á - THÁI BÌNH DƯƠNG TẠI ĐÀ NẴNG NGUYỄN ĐĂNG HÙNG	
ĐƠN VỊ NHÀ THẦU CHÍNH: CÔNG TY CỔ PHẦN ALPHANAM E&C	
NHÀ THẦU THI CÔNG:  CÔNG TY TNHH VIỄN THÔNG SÁNG TẠO THUẬN PHONG (INNOTEL) 55/31 TRẦN ĐÌNH XU, P. CẦU KHO, Q. 1, HCM Tel: (84 28) 3 862 1119 Fax: (84 28) 3 863 0366	
CHỈ HUY TRƯỞNG:	
NGUYỄN ĐỨC TIẾN	
NGƯỜI KIỂM TRA:	
NGƯỜI LẬP:	
TÊN BẢN VẼ: RACK LAYOUT IDF-M.7F	
NGÀY HT:	07/11/2022
CHÍNH SỬA:	01
MÃ BẢN VẼ:	IDF-M.7F
HỒ SƠ THAM CHIẾU:	- ELV1-1-ELV1-02 - SDNL KHOI KS - ELV1-1-ELV1-02 - SDNL KHOI MLM

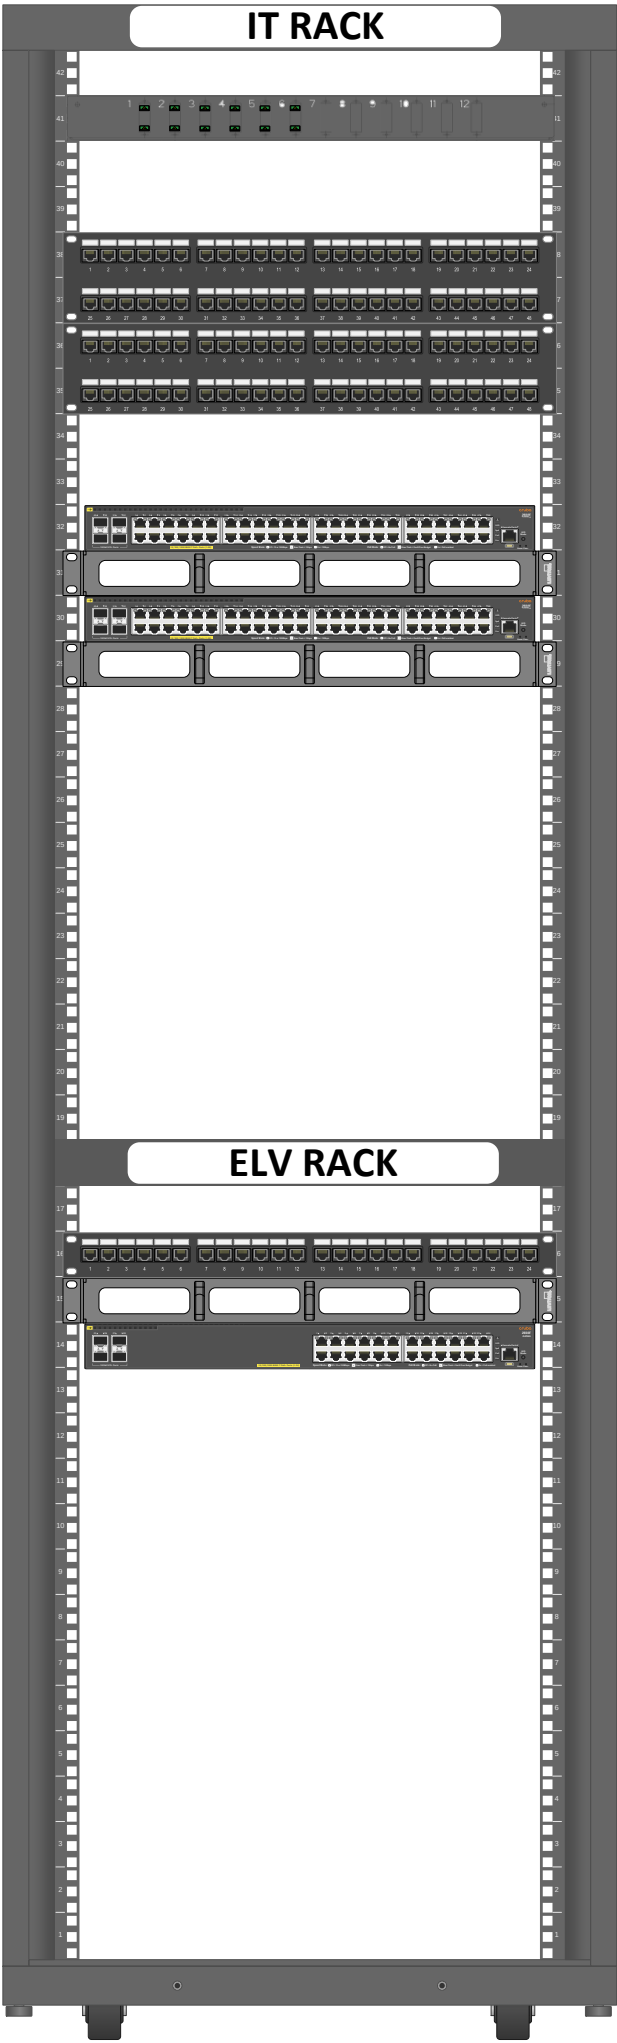


DỰ ÁN: TỔ HỢP KHÁCH SẠN, CĂN HỘ DỊCH VỤ MARRIOTT VÀ NHÀ Ở ĐỂ BÁN ĐỊA ĐIỂM XÂY DỰNG: 58 BẠCH ĐẰNG, P. HẢI CHÂU 1, Q. HẢI CHÂU, TP. ĐÀ NẴNG	
CHỦ ĐẦU TƯ: CÔNG TY CỔ PHẦN ĐỊA ỐC FOODINCO ĐỊA CHỈ: 58 BẠCH ĐẰNG, P. HẢI CHÂU 1, Q. HẢI CHÂU, TP. ĐÀ NẴNG	
BAN QUẢN LÝ DỰ ÁN:	
TƯ VẤN GIÁM SÁT: CN CÔNG TY TNHH APAVE CHÂU Á - THÁI BÌNH DƯƠNG TẠI ĐÀ NẴNG NGUYỄN ĐĂNG HÙNG	
ĐƠN VỊ NHÀ THẦU CHÍNH: CÔNG TY CỔ PHẦN ALPHANAM E&C	
NHÀ THẦU THI CÔNG:  CÔNG TY TNHH VIỄN THÔNG SÁNG TẠO THUẬN PHONG (INNOTEL) 55/31 TRẦN ĐÌNH XU, P. CẦU KHO, Q. 1, HCM Tel: (84 28) 3 862 1119 Fax: (84 28) 3 863 0366	
CHỈ HUY TRƯỞNG:	
NGƯỜI KIỂM TRA:	
NGƯỜI LẬP:	
TÊN BẢN VẼ: RACK LAYOUT IDF-M.8F	
NGÀY HT:	07/11/2022
CHỈNH SỬA:	01
MÃ BẢN VẼ:	IDF-M.8F
HỒ SƠ THAM CHIẾU:	- ELV1-1-ELV1-02 - SDNL KHOI KS - ELV1-1-ELV1-02 - SDNL KHOI MLM

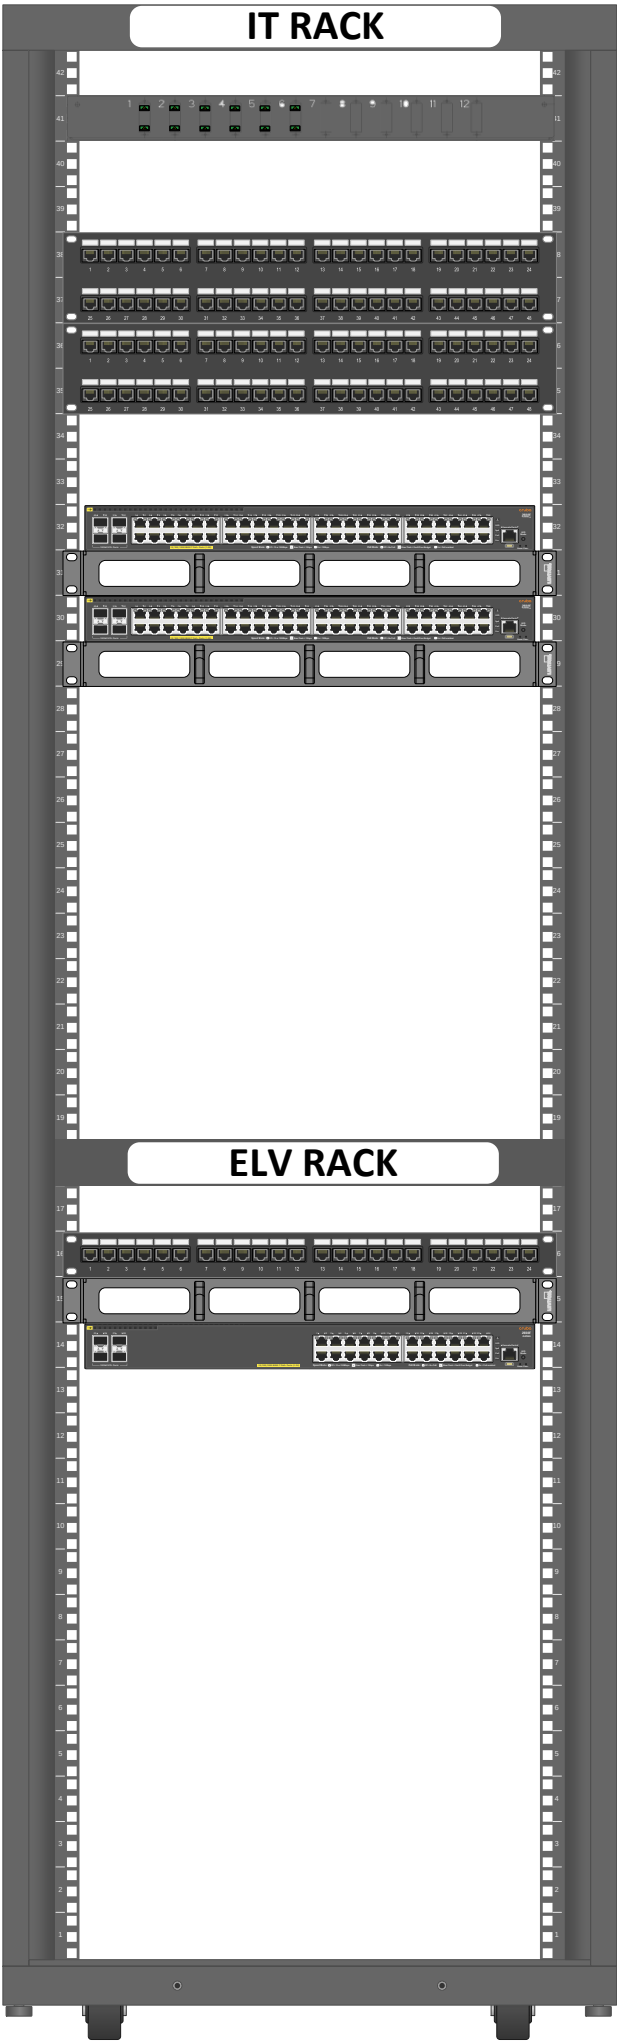


DỰ ÁN: TỔ HỢP KHÁCH SẠN, CĂN HỘ DỊCH VỤ MARRIOTT VÀ NHÀ Ở ĐỂ BÁN ĐỊA ĐIỂM XÂY DỰNG: 58 BẠCH ĐẰNG, P. HẢI CHÂU 1, Q. HẢI CHÂU, TP. ĐÀ NẴNG	
CHỦ ĐẦU TƯ: CÔNG TY CỔ PHẦN ĐỊA ỐC FOODINCO ĐỊA CHỈ: 58 BẠCH ĐẰNG, P. HẢI CHÂU 1, Q. HẢI CHÂU, TP. ĐÀ NẴNG	
BAN QUẢN LÝ DỰ ÁN:	
TƯ VẤN GIÁM SÁT: CN CÔNG TY TNHH APAVE CHÂU Á - THÁI BÌNH DƯƠNG TẠI ĐÀ NẴNG NGUYỄN ĐĂNG HÙNG	
ĐƠN VỊ NHÀ THẦU CHÍNH: CÔNG TY CỔ PHẦN ALPHANAM E&C	
NHÀ THẦU THI CÔNG:  CÔNG TY TNHH VIỄN THÔNG SÁNG TẠO THUẬN PHONG (INNOTEL) 55/31 TRẦN ĐÌNH XU, P. CẦU KHO, Q. 1, HCM Tel: (84 28) 3 862 1119 Fax: (84 28) 3 863 0366	
CHỈ HUY TRƯỞNG:	
NGUYỄN ĐỨC TIẾN	
NGƯỜI KIỂM TRA:	
NGƯỜI LẬP:	
TÊN BẢN VẼ: RACK LAYOUT IDF-M.10F	
NGÀY HT:	07/11/2022
CHỈNH SỬA:	01
MÃ BẢN VẼ:	IDF-M.10F
HỒ SƠ THAM CHIẾU:	- ELV1-1-ELV1-02 - SDNL KHOI KS - ELV1-1-ELV1-02 - SDNL KHOI MLM

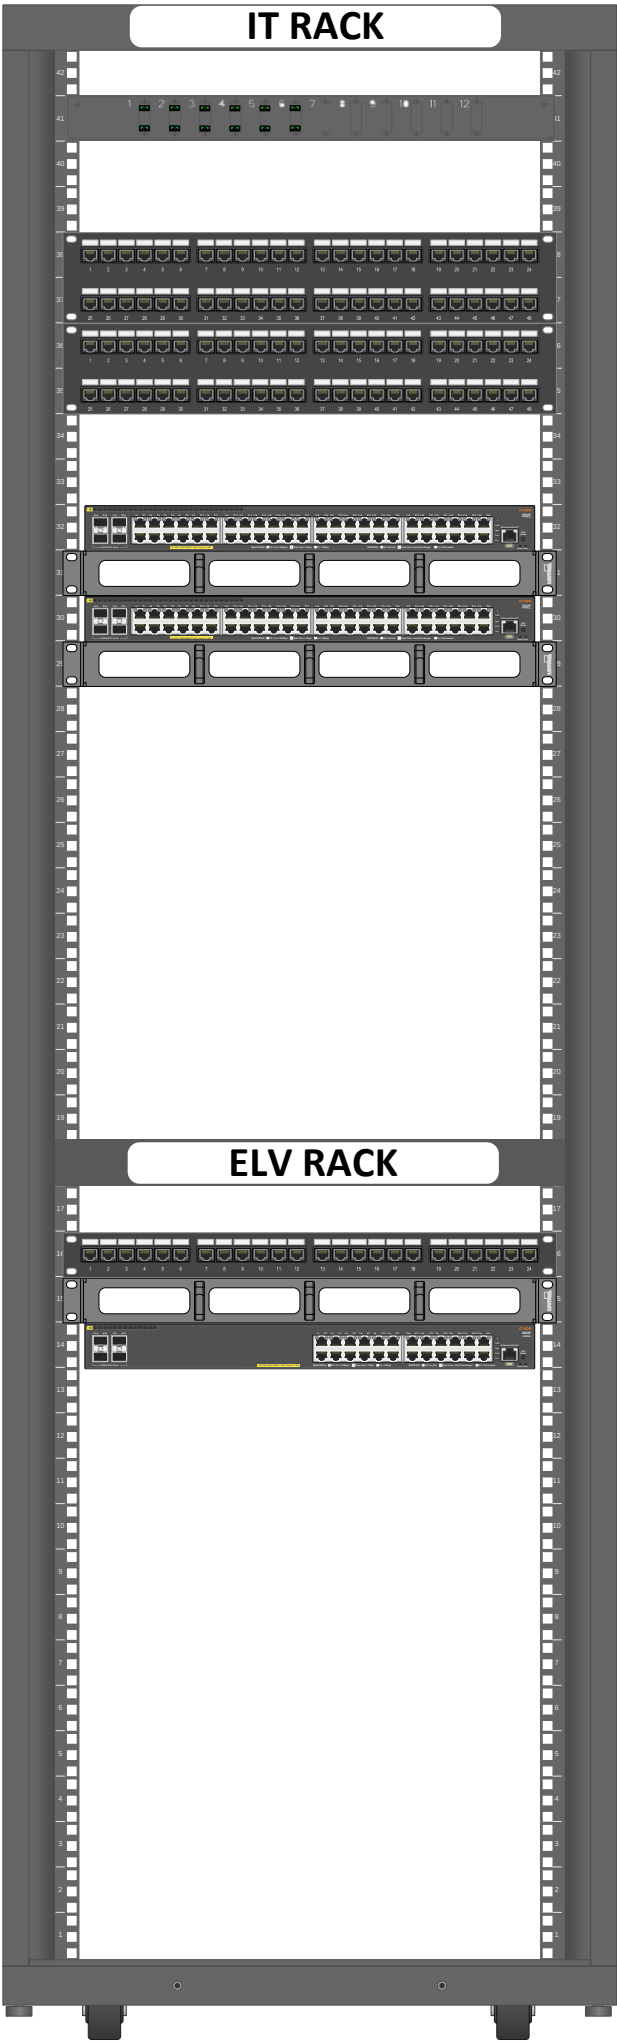


DỰ ÁN: TỔ HỢP KHÁCH SẠN, CĂN HỘ DỊCH VỤ MARRIOTT VÀ NHÀ Ở ĐỂ BÁN ĐỊA ĐIỂM XÂY DỰNG: 58 BẠCH ĐẰNG, P. HẢI CHÂU 1, Q. HẢI CHÂU, TP. ĐÀ NẴNG	
CHỦ ĐẦU TƯ: CÔNG TY CỔ PHẦN ĐỊA ỐC FOODINCO ĐỊA CHỈ: 58 BẠCH ĐẰNG, P. HẢI CHÂU 1, Q. HẢI CHÂU, TP. ĐÀ NẴNG	
BAN QUẢN LÝ DỰ ÁN:	
TƯ VẤN GIÁM SÁT: CN CÔNG TY TNHH APAVE CHÂU Á - THÁI BÌNH DƯƠNG TẠI ĐÀ NẴNG NGUYỄN ĐĂNG HÙNG	
ĐƠN VỊ NHÀ THẦU CHÍNH: CÔNG TY CỔ PHẦN ALPHANAM E&C	
NHÀ THẦU THI CÔNG:  CÔNG TY TNHH VIỄN THÔNG SÁNG TẠO THUẬN PHONG (INNOTEL) 55/31 TRẦN ĐÌNH XU, P. CẦU KHO, Q. 1, HCM Tel: (84 28) 3 862 1119 Fax: (84 28) 3 863 0366	
CHỈ HUY TRƯỞNG:	
NGƯỜI KIỂM TRA:	
NGƯỜI LẬP:	
TÊN BẢN VẼ: RACK LAYOUT IDF-M.12F	
NGÀY HT:	07/11/2022
CHỈNH SỬA:	01
MÃ BẢN VẼ:	IDF-M.12F
HỒ SƠ THAM CHIẾU:	- ELV1-1-ELV1-02 - SDNL KHOI KS - ELV1-1-ELV1-02 - SDNL KHOI MLM

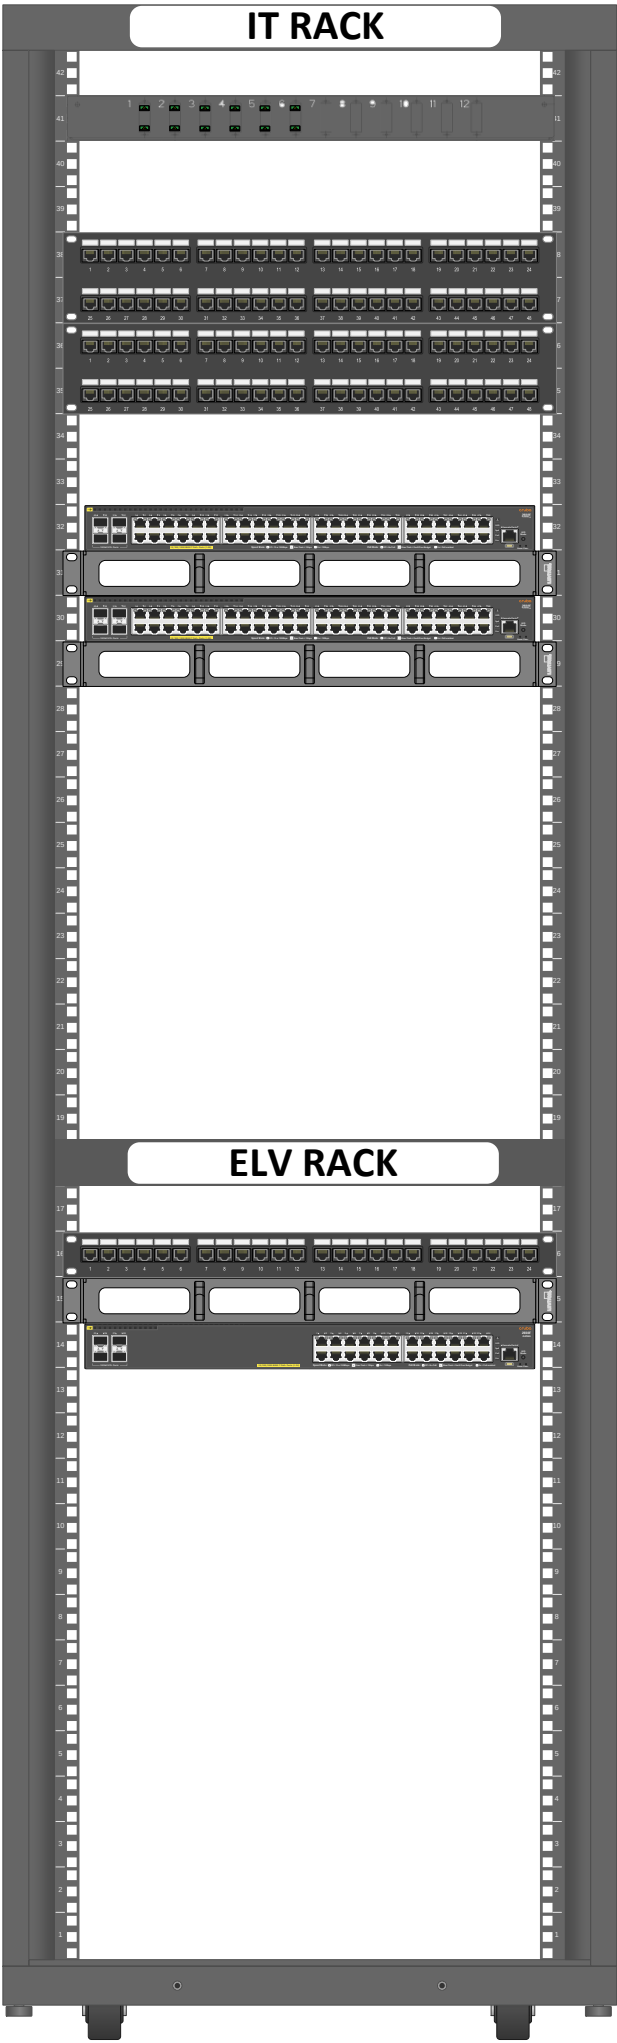


DỰ ÁN: TỔ HỢP KHÁCH SẠN, CĂN HỘ DỊCH VỤ MARRIOTT VÀ NHÀ Ở ĐỂ BÁN ĐỊA ĐIỂM XÂY DỰNG: 58 BẠCH ĐẰNG, P. HẢI CHÂU 1, Q. HẢI CHÂU, TP. ĐÀ NẴNG	
CHỦ ĐẦU TƯ: CÔNG TY CỔ PHẦN ĐỊA ỐC FOODINCO ĐỊA CHỈ: 58 BẠCH ĐẰNG, P. HẢI CHÂU 1, Q. HẢI CHÂU, TP. ĐÀ NẴNG	
BAN QUẢN LÝ DỰ ÁN:	
TƯ VẤN GIÁM SÁT: CN CÔNG TY TNHH APAVE CHÂU Á - THÁI BÌNH DƯƠNG TẠI ĐÀ NẴNG NGUYỄN ĐĂNG HÙNG	
ĐƠN VỊ NHÀ THẦU CHÍNH: CÔNG TY CỔ PHẦN ALPHANAM E&C	
NHÀ THẦU THI CÔNG:  CÔNG TY TNHH VIỄN THÔNG SÁNG TẠO THUẬN PHONG (INNOTEL) 55/31 TRẦN ĐÌNH XU, P. CẦU KHO, Q. 1, HCM Tel: (84 28) 3 862 1119 Fax: (84 28) 3 863 0366	
CHỈ HUY TRƯỞNG:	
NGƯỜI KIỂM TRA:	
NGƯỜI LẬP:	
TÊN BẢN VẼ: RACK LAYOUT IDF-M.15F	
NGÀY HT:	07/11/2022
CHỈNH SỬA:	01
MÃ BẢN VẼ:	IDF-M.15F
HỒ SƠ THAM CHIẾU:	- ELV1-1-ELV1-02 - SDNL KHOI KS - ELV1-1-ELV1-02 - SDNL KHOI MLM

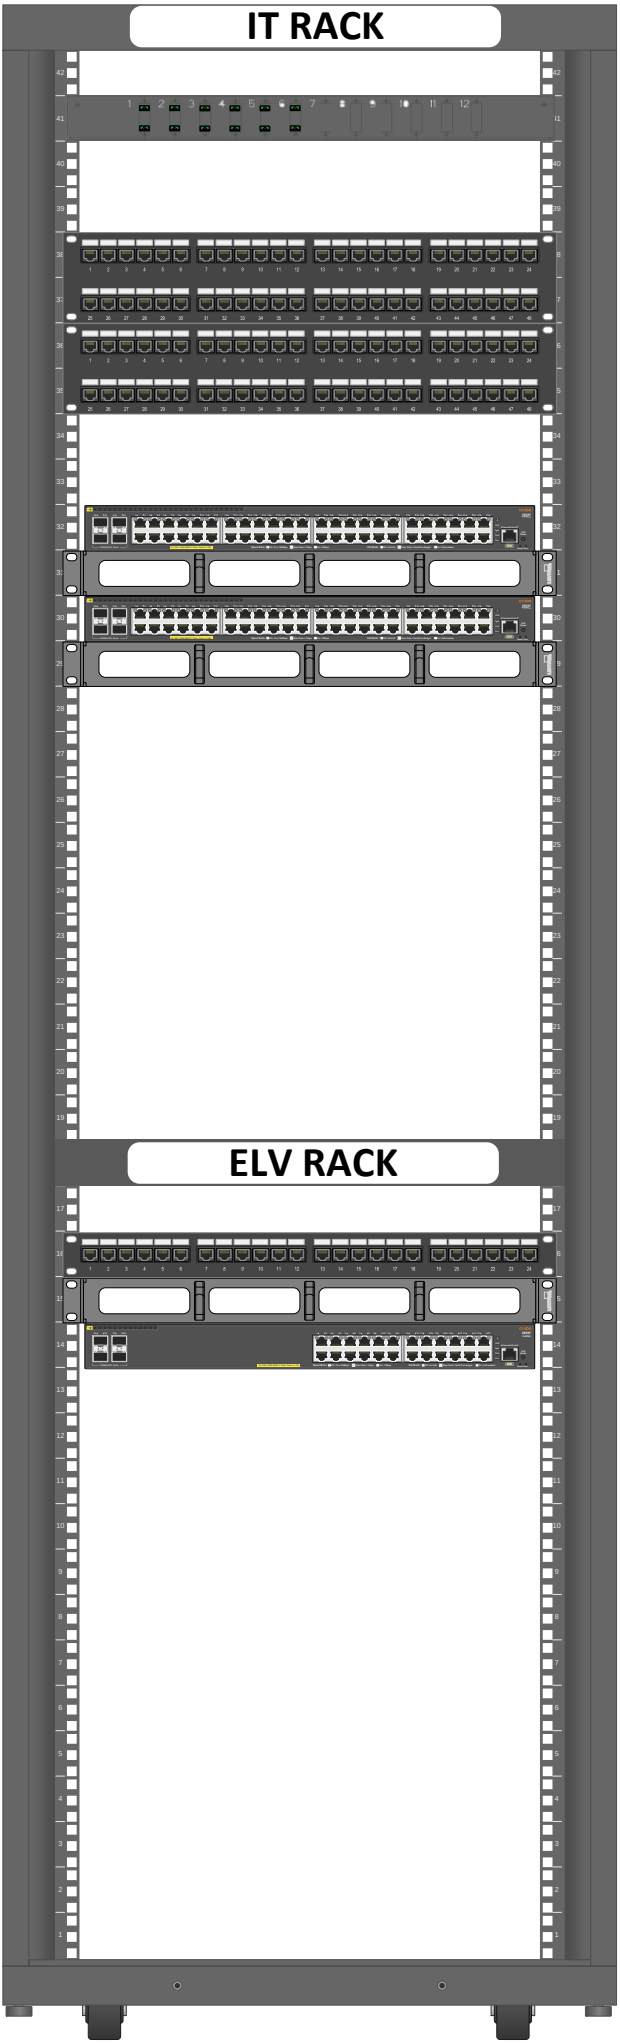


DỰ ÁN: TỔ HỢP KHÁCH SẠN, CĂN HỘ DỊCH VỤ MARRIOTT VÀ NHÀ Ở ĐỂ BÁN ĐỊA ĐIỂM XÂY DỰNG: 58 BẠCH ĐẰNG, P. HẢI CHÂU 1, Q. HẢI CHÂU, TP. ĐÀ NẴNG	
CHỦ ĐẦU TƯ: CÔNG TY CỔ PHẦN ĐỊA ỐC FOODINCO ĐỊA CHỈ: 58 BẠCH ĐẰNG, P. HẢI CHÂU 1, Q. HẢI CHÂU, TP. ĐÀ NẴNG	
BAN QUẢN LÝ DỰ ÁN:	
TƯ VẤN GIÁM SÁT: CN CÔNG TY TNHH APAVE CHÂU Á - THÁI BÌNH DƯƠNG TẠI ĐÀ NẴNG NGUYỄN ĐĂNG HÙNG	
ĐƠN VỊ NHÀ THẦU CHÍNH: CÔNG TY CỔ PHẦN ALPHANAM E&C	
NHÀ THẦU THI CÔNG:  CÔNG TY TNHH VIỄN THÔNG SÁNG TẠO THUẬN PHONG (INNOTEL) 55/31 TRẦN ĐÌNH XU, P. CẦU KHO, Q. 1, HCM Tel: (84 28) 3 862 1119 Fax: (84 28) 3 863 0366	
CHỈ HUY TRƯỞNG:	
NGUYỄN ĐỨC TIẾN	
NGƯỜI KIỂM TRA:	
NGƯỜI LẬP:	
TÊN BẢN VẼ: RACK LAYOUT IDF-M.17F	
NGÀY HT:	07/11/2022
CHỈNH SỬA:	01
MÃ BẢN VẼ:	IDF-M.17F
HỒ SƠ THAM CHIẾU:	- ELV1-1-ELV1-02 - SDNL KHOI KS - ELV1-1-ELV1-02 - SDNL KHOI MLM

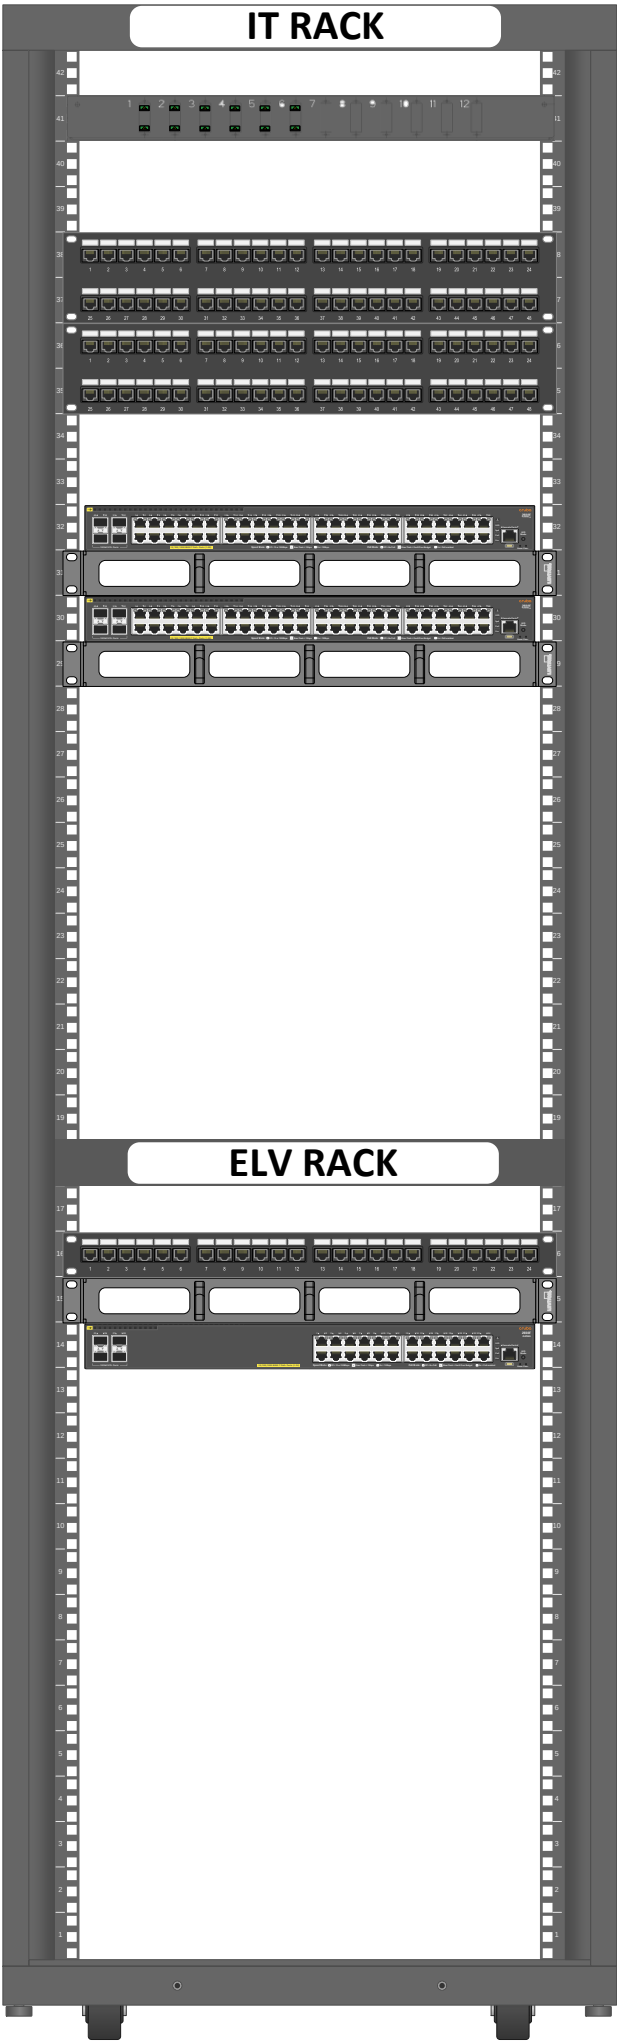


DỰ ÁN: TỔ HỢP KHÁCH SẠN, CĂN HỘ DỊCH VỤ MARRIOTT VÀ NHÀ Ở ĐỂ BÁN ĐỊA ĐIỂM XÂY DỰNG: 58 BẠCH ĐẰNG, P. HẢI CHÂU 1, Q. HẢI CHÂU, TP. ĐÀ NẴNG	
CHỦ ĐẦU TƯ: CÔNG TY CỔ PHẦN ĐỊA ỐC FOODINCO ĐỊA CHỈ: 58 BẠCH ĐẰNG, P. HẢI CHÂU 1, Q. HẢI CHÂU, TP. ĐÀ NẴNG	
BAN QUẢN LÝ DỰ ÁN:	
TƯ VẤN GIÁM SÁT: CN CÔNG TY TNHH APAVE CHÂU Á - THÁI BÌNH DƯƠNG TẠI ĐÀ NẴNG NGUYỄN ĐĂNG HÙNG	
ĐƠN VỊ NHÀ THẦU CHÍNH: CÔNG TY CỔ PHẦN ALPHANAM E&C	
NHÀ THẦU THI CÔNG:  CÔNG TY TNHH VIỄN THÔNG SÁNG TẠO THUẬN PHONG (INNOTEL) 55/31 TRẦN ĐÌNH XU, P. CẦU KHO, Q. 1, HCM Tel: (84 28) 3 862 1119 Fax: (84 28) 3 863 0366	
CHỈ HUY TRƯỞNG:	
NGƯỜI KIỂM TRA:	
NGƯỜI LẬP:	
TÊN BẢN VẼ: RACK LAYOUT IDF-M.19F	
NGÀY HT:	07/11/2022
CHỈNH SỬA:	01
MÃ BẢN VẼ:	IDF-M.19F
HỒ SƠ THAM CHIẾU:	- ELV1-1-ELV1-02 - SDNL KHOI KS - ELV1-1-ELV1-02 - SDNL KHOI MLM

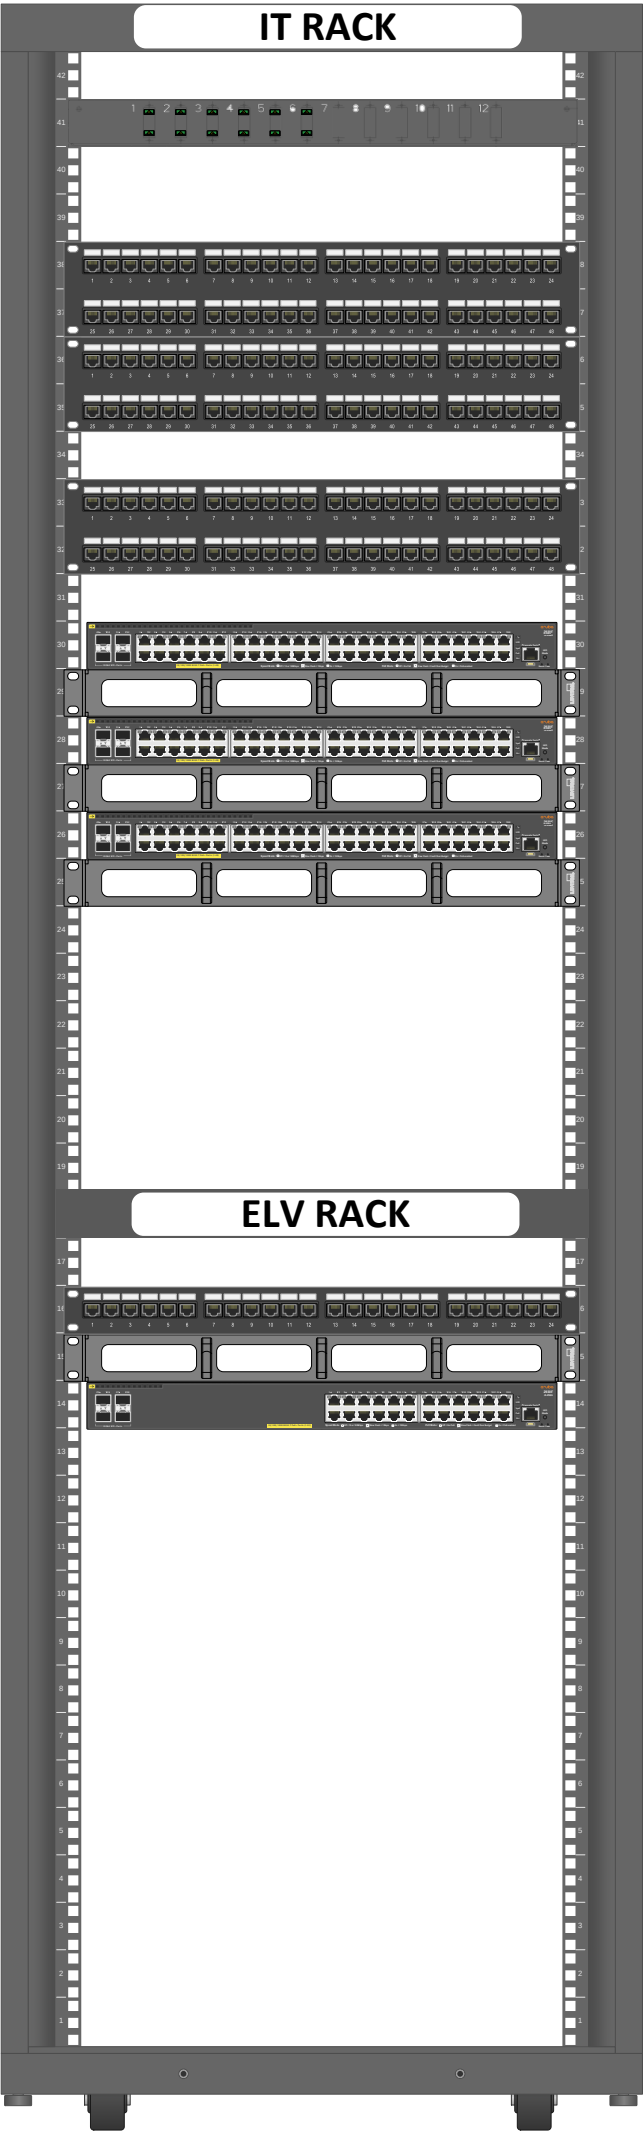


DỰ ÁN: TỔ HỢP KHÁCH SẠN, CĂN HỘ DỊCH VỤ MARRIOTT VÀ NHÀ Ở ĐỂ BÁN ĐỊA ĐIỂM XÂY DỰNG: 58 BẠCH ĐẰNG, P. HẢI CHÂU 1, Q. HẢI CHÂU, TP. ĐÀ NẴNG	
CHỦ ĐẦU TƯ: CÔNG TY CỔ PHẦN ĐỊA ỐC FOODINCO ĐỊA CHỈ: 58 BẠCH ĐẰNG, P. HẢI CHÂU 1, Q. HẢI CHÂU, TP. ĐÀ NẴNG	
BAN QUẢN LÝ DỰ ÁN:	
TƯ VẤN GIÁM SÁT: CN CÔNG TY TNHH APAVE CHÂU Á - THÁI BÌNH DƯƠNG TẠI ĐÀ NẴNG NGUYỄN ĐĂNG HÙNG	
ĐƠN VỊ NHÀ THẦU CHÍNH: CÔNG TY CỔ PHẦN ALPHANAM E&C	
NHÀ THẦU THI CÔNG:  CÔNG TY TNHH VIỄN THÔNG SÁNG TẠO THUẬN PHONG (INNOTEL) 55/31 TRẦN ĐÌNH XU, P. CẦU KHO, Q. 1, HCM Tel: (84 28) 3 862 1119 Fax: (84 28) 3 863 0366	
CHỈ HUY TRƯỞNG:	
NGƯỜI KIỂM TRA:	
NGƯỜI LẬP:	
TÊN BẢN VẼ: RACK LAYOUT IDF-M.22F	
NGÀY HT:	07/11/2022
CHỈNH SỬA:	01
MÃ BẢN VẼ:	IDF-M.22F
HỒ SƠ THAM CHIẾU:	- ELV1-1-ELV1-02 - SDNL KHOI KS - ELV1-1-ELV1-02 - SDNL KHOI MLM

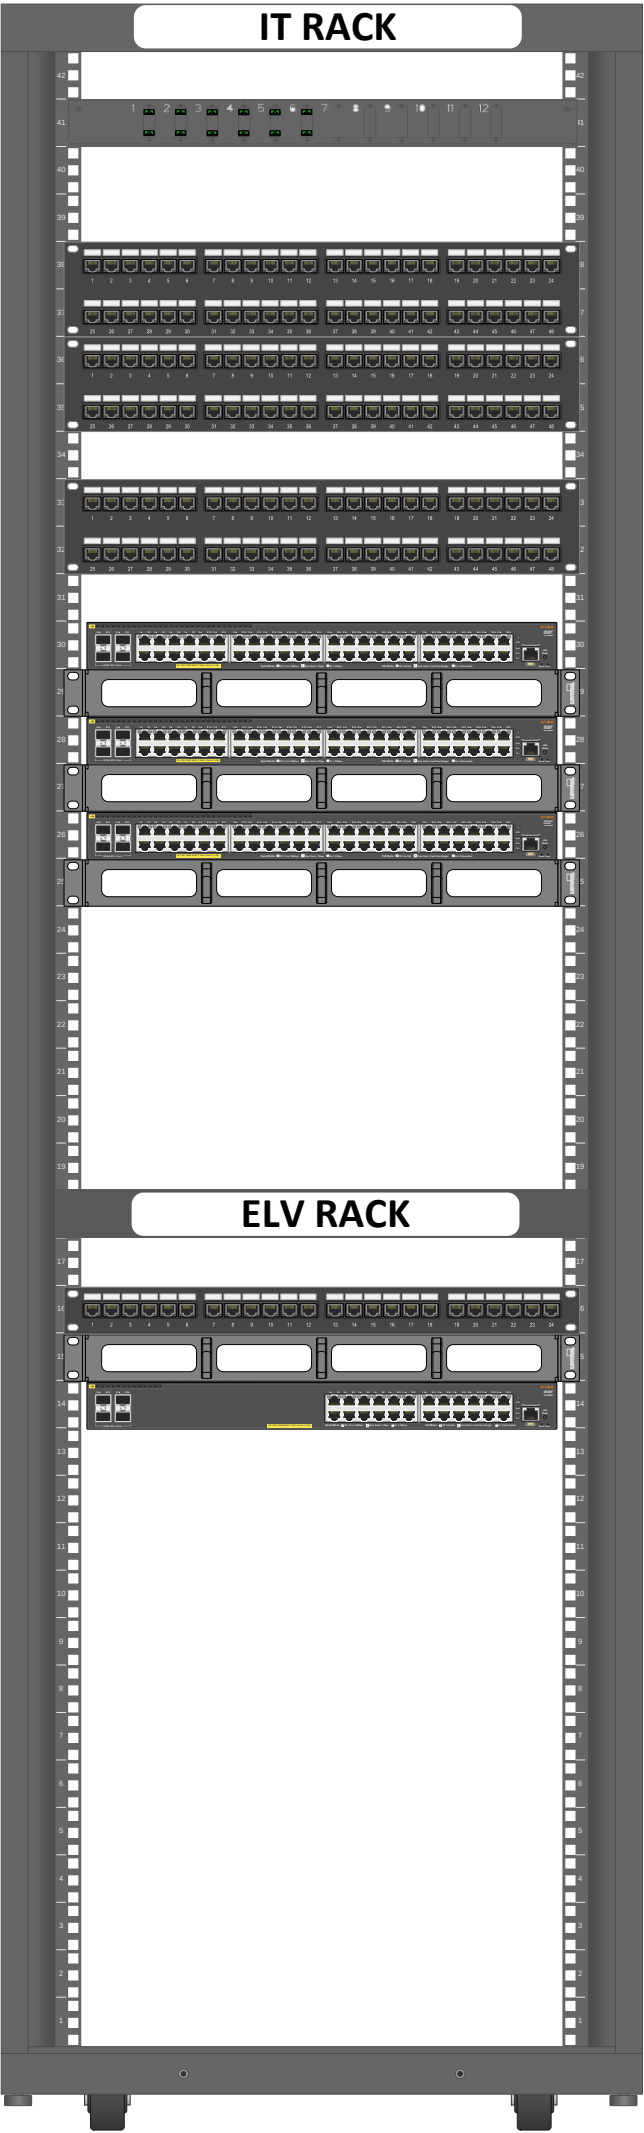

DỰ ÁN: TỔ HỢP KHÁCH SẠN, CĂN HỘ DỊCH VỤ MARRIOTT VÀ NHÀ Ở ĐỂ BÁN ĐỊA ĐIỂM XÂY DỰNG: 58 BẠCH ĐẰNG, P. HẢI CHÂU 1, Q. HẢI CHÂU, TP. ĐÀ NẴNG	
CHỦ ĐẦU TƯ: CÔNG TY CỔ PHẦN ĐỊA ỐC FOODINCO ĐỊA CHỈ: 58 BẠCH ĐẰNG, P. HẢI CHÂU 1, Q. HẢI CHÂU, TP. ĐÀ NẴNG	
BAN QUẢN LÝ DỰ ÁN:	
TƯ VẤN GIÁM SÁT: CN CÔNG TY TNHH APAVE CHÂU Á - THÁI BÌNH DƯƠNG TẠI ĐÀ NẴNG NGUYỄN ĐĂNG HÙNG	
ĐƠN VỊ NHÀ THẦU CHÍNH: CÔNG TY CỔ PHẦN ALPHANAM E&C	
NHÀ THẦU THI CÔNG:  CÔNG TY TNHH VIỄN THÔNG SÁNG TẠO THUẬN PHONG (INNOTEL) 55/31 TRẦN ĐÌNH XU, P. CẦU KHO, Q. 1, HCM Tel: (84 28) 3 862 1119 Fax: (84 28) 3 863 0366	
CHỈ HUY TRƯỞNG:	
NGƯỜI KIỂM TRA:	
NGƯỜI LẬP:	
TÊN BẢN VẼ: RACK LAYOUT IDF-M.25F	
NGÀY HT:	07/11/2022
CHỈNH SỬA:	01
MÃ BẢN VẼ:	IDF-M.25F
HỒ SƠ THAM CHIẾU:	- ELV1-1-ELV1-02 - SDNL KHOI KS - ELV1-1-ELV1-02 - SDNL KHOI MLM

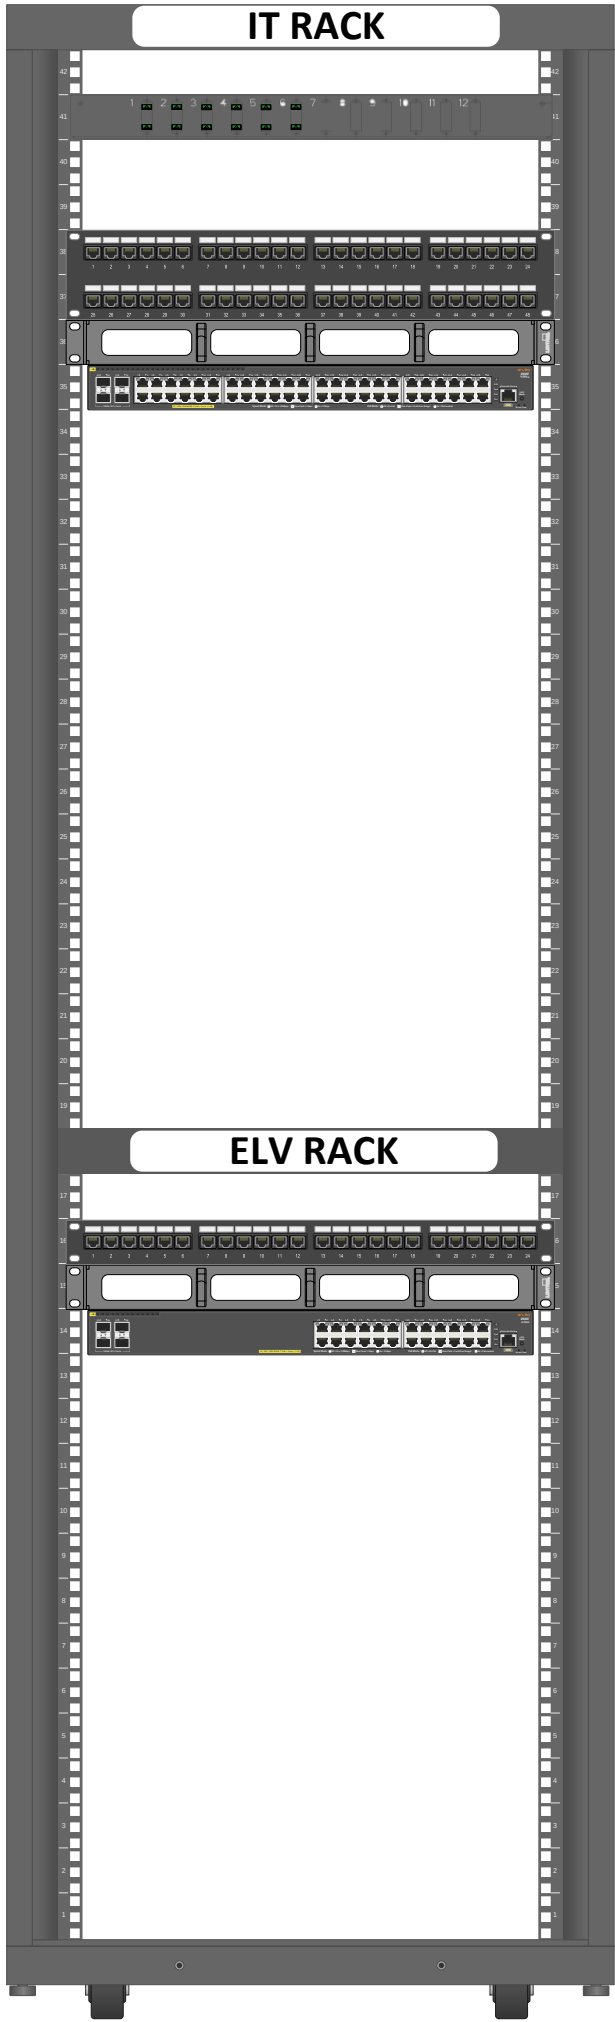

DỰ ÁN: TỔ HỢP KHÁCH SẠN, CĂN HỘ DỊCH VỤ MARRIOTT VÀ NHÀ Ở ĐỂ BÁN ĐỊA ĐIỂM XÂY DỰNG: 58 BẠCH ĐẰNG, P. HẢI CHÂU 1, Q. HẢI CHÂU, TP. ĐÀ NẴNG	
CHỦ ĐẦU TƯ: CÔNG TY CỔ PHẦN ĐỊA ỐC FOODINCO ĐỊA CHỈ: 58 BẠCH ĐẰNG, P. HẢI CHÂU 1, Q. HẢI CHÂU, TP. ĐÀ NẴNG	
BAN QUẢN LÝ DỰ ÁN:	
TƯ VẤN GIÁM SÁT: CN CÔNG TY TNHH APAVE CHÂU Á - THÁI BÌNH DƯƠNG TẠI ĐÀ NẴNG NGUYỄN ĐĂNG HÙNG	
ĐƠN VỊ NHÀ THẦU CHÍNH: CÔNG TY CỔ PHẦN ALPHANAM E&C	
NHÀ THẦU THI CÔNG:  CÔNG TY TNHH VIỄN THÔNG SÁNG TẠO THUẬN PHONG (INNOTEL) 55/31 TRẦN ĐÌNH XU, P. CẦU KHO, Q. 1, HCM Tel: (84 28) 3 862 1119 Fax: (84 28) 3 863 0366	
CHỈ HUY TRƯỞNG:	
NGUYỄN ĐỨC TIẾN	
NGƯỜI KIỂM TRA:	
NGƯỜI LẬP:	
TÊN BẢN VẼ: RACK LAYOUT IDF-M.29F	
NGÀY HT:	07/11/2022
CHỈNH SỬA:	01
MÃ BẢN VẼ:	IDF-M.29F
HỒ SƠ THAM CHIẾU:	- ELV1-1-ELV1-02 - SDNL KHOI KS - ELV1-1-ELV1-02 - SDNL KHOI MLM

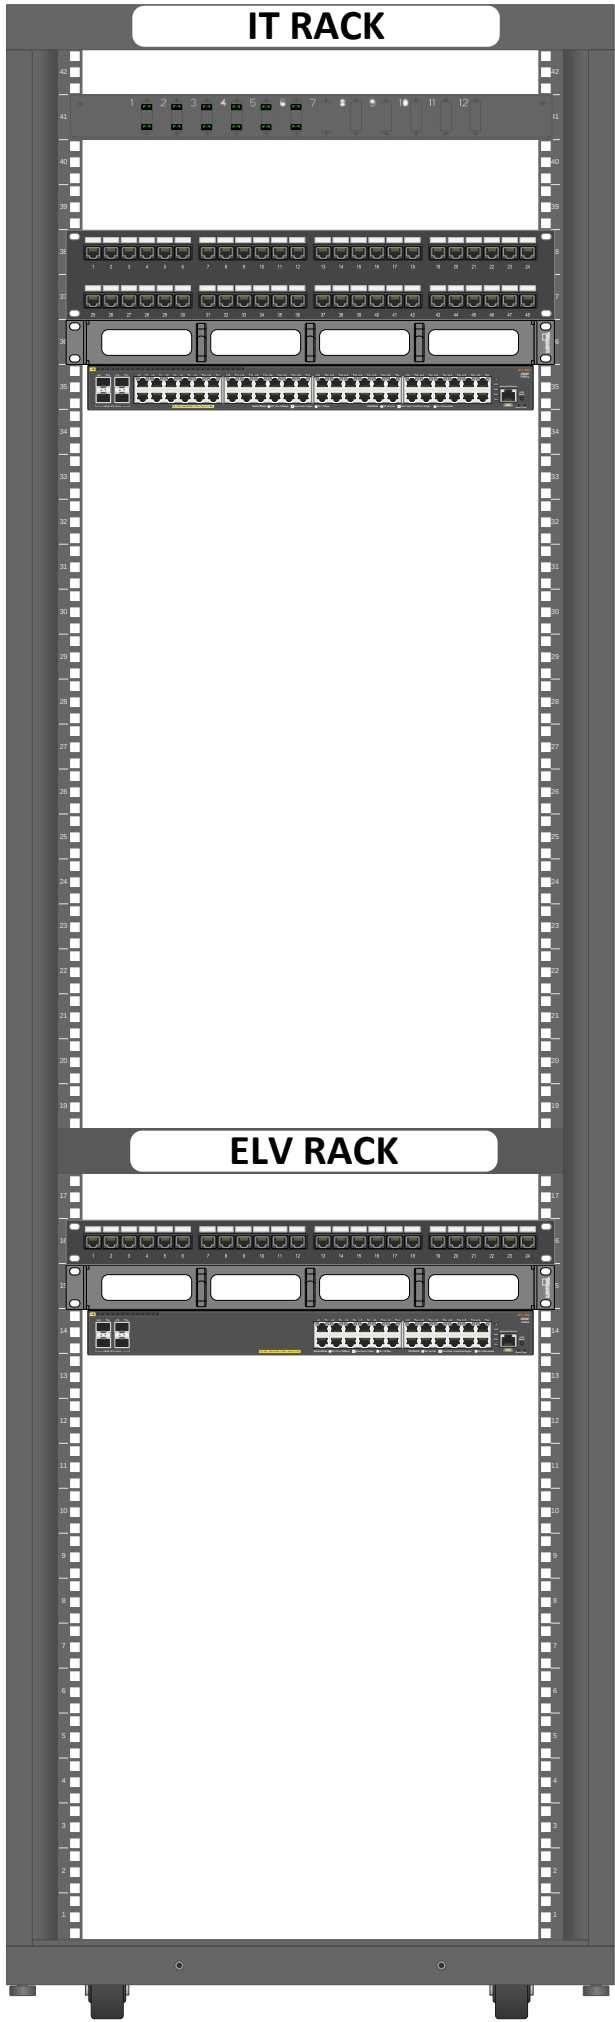

DỰ ÁN: TỔ HỢP KHÁCH SẠN, CĂN HỘ DỊCH VỤ MARRIOTT VÀ NHÀ Ở ĐỂ BÁN ĐỊA ĐIỂM XÂY DỰNG: 58 BẠCH ĐẰNG, P. HẢI CHÂU 1, Q. HẢI CHÂU, TP. ĐÀ NẴNG	
CHỦ ĐẦU TƯ: CÔNG TY CỔ PHẦN ĐỊA ỐC FOODINCO ĐỊA CHỈ: 58 BẠCH ĐẰNG, P. HẢI CHÂU 1, Q. HẢI CHÂU, TP. ĐÀ NẴNG	
BAN QUẢN LÝ DỰ ÁN:	
TƯ VẤN GIÁM SÁT: CN CÔNG TY TNHH APAVE CHÂU Á - THÁI BÌNH DƯƠNG TẠI ĐÀ NẴNG NGUYỄN ĐĂNG HÙNG	
ĐƠN VỊ NHÀ THẦU CHÍNH: CÔNG TY CỔ PHẦN ALPHANAM E&C	
NHÀ THẦU THI CÔNG:  CÔNG TY TNHH VIỄN THÔNG SÁNG TẠO THUẬN PHONG (INNOTEL) 55/31 TRẦN ĐÌNH XU, P. CẦU KHO, Q. 1, HCM Tel: (84 28) 3 862 1119 Fax: (84 28) 3 863 0366	
CHỈ HUY TRƯỞNG: NGUYỄN ĐỨC TIẾN	
NGƯỜI KIỂM TRA:	
NGƯỜI LẬP:	
TÊN BẢN VẼ: RACK LAYOUT IDF-M.45F	
NGÀY HT:	07/11/2022
CHỈNH SỬA:	01
MÃ BẢN VẼ:	IDF-M.45F
HỒ SƠ THAM CHIẾU:	- ELV1-1-ELV1-02 - SDNL KHOI KS - ELV1-1-ELV1-02 - SDNL KHOI MLM