

SHOWROOM VOLKSWAGEN CẦN THƠ

HỒ SƠ THIẾT KẾ HỆ THỐNG ĐIỆN NHÉ

**HỆ THỐNG MẠNG, ĐIỆN THOẠI,
CAMERA, ÂM THANH THÔNG BÁO**

HCMC, 01.2026

STT	TÊN BẢN VẼ	KÝ HIỆU
01	DANH MỤC BẢN VẼ	LV.01
02	GHI CHÚ CHUNG VÀ MÔ TẢ KÝ HIỆU	LV.02
03	SƠ ĐỒ NGUYÊN LÝ HỆ THỐNG MẠNG+CAMERA+ĐIỆN THOẠI+ÂM THANH	LV.03
04	MẶT BẰNG HỆ THỐNG MẠNG+CAMERA+ĐIỆN THOẠI+ÂM THANH TẦNG TRỆT	LV.04
05	CHI TIẾT LẮP ĐẶT ĐIỂN HÌNH 01	LV.05

GHI CHÚ - (Notes)

- 1/ ĐỀ NGHỊ KIỂM TRA KÍCH THƯỚC THỰC TẾ TẠI CÔNG TRÌNH TRƯỚC KHI THI CÔNG
2/ NÊN ĐỌC BẢN VẼ KẾT CẤU KÈM THEO BẢN VẼ KHAI TRIỂN CHI TIẾT KIẾN TRÚC
3/ KHI THAY ĐỔI CHI TIẾT THIẾT KẾ CẦN THAM KHẢO Ý KIẾN CỦA KIẾN TRÚC SƯ HOẶC KÝ SƯ THIẾT KẾ

BẢN VẼ PHÁT HÀNH

- ☐ THIẾT KẾ CONCEPT
☐ THIẾT KẾ CƠ SỞ
☒ THIẾT KẾ KỸ THUẬT THI CÔNG

TÊN CÔNG TRÌNH
(project name)

SHOWROOM VOLKSWAGEN
CẦN THƠ

ĐỊA ĐIỂM XÂY DỰNG
(Site)

KDC LÔ SỐ 11A, KĐT NAM CẦN THƠ
PHƯỜNG HƯNG PHÚ, TP. CẦN THƠ

CHỦ ĐẦU TƯ
(Project Owner)

CÔNG TY CP VW CẦN THƠ

TỔNG GIÁM ĐỐC

ĐƠN VỊ THIẾT KẾ

BAOLONG LAND COPORATION
Lô DVTM-08 & DVTM-11, Đường số 7
KCX Tân Thuận, P. Tân Thuận Đông, Q7, Tp.HCM



TỔNG GIÁM ĐỐC

PHAN HẢI NAM

ĐƠN VỊ THIẾT KẾ CƠ ĐIỆN

VIET TIEN CONSTRUCTION AND
DESIGN CONSULTING CO., LTD

127/23 Lê Thúc Hoạch, P. Phú Thọ Hòa, Tp.HCM

GIÁM ĐỐC

KS. NGUYỄN THỊ QUI

TÊN BẢN VẼ/Drawing Title

DANH MỤC BẢN VẼ


TỶ LỆ - Scale
1/150

NGÀY- Date
30/01/2026


BẢN VẼ SỐ
Drawing No.

LV-01
05

HỆ THỐNG CAMERA QUAN SÁT

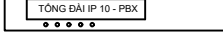KÝ HIỆU SYMBOL	MÔ TẢ DESCRIPTION
	CAMERA IP HÌNH TRỤ CỘ ĐỊNH 2MP, IP67 VÀ IK10 - Chống ngược sáng: WDR 120dB - Ghi âm: Tích hợp bên trong 1 micro - Giao diện kết nối: 1 x RJ45 10/100Mbps; 01 x Audio in; 01 x Audio out; 01 x I/O Alarm - Tuân thủ bảo mật theo mã hóa AES 256bit, Có chứng nhận an toàn công nghệ thông tin - Mã hóa các cấu hình camera; mã hóa video; mã hóa các phần sụn (firmware) - Hỗ trợ 2 chế độ đèn hồng ngoại quan sát ban đêm - Đèn quan sát ban đêm với chế độ đèn trắng khoảng cách tối thiểu 50 mét - Đèn quan sát ban đêm với đầy đủ màu sắc khoảng cách tối thiểu 30 mét
	CAMERA IP BÀN CẦU CỘ ĐỊNH 2MP, IP67 VÀ IK10 - Chống ngược sáng: WDR 120dB - Ghi âm: Tích hợp bên trong 1 micro - Giao diện kết nối: 1 x RJ45 10/100Mbps; 01 x Audio in; 01 x Audio out; 01 x I/O Alarm - Tuân thủ bảo mật theo mã hóa AES 256bit, Có chứng nhận an toàn công nghệ thông tin - Mã hóa các cấu hình camera; mã hóa video; mã hóa các phần sụn (firmware) - Hỗ trợ 2 chế độ đèn hồng ngoại quan sát ban đêm - Đèn quan sát ban đêm với chế độ đèn trắng khoảng cách tối thiểu 50 mét - Đèn quan sát ban đêm với đầy đủ màu sắc khoảng cách tối thiểu 30 mét
	BỘ QUẢN LÝ VÀ GHI HÌNH CÓ CHỨC NĂNG AI - Có bản quyền nhận diện khuôn mặt 2 kênh camera, với tốc độ nhận diện tối thiểu 12 hình ảnh/ giây - Tổng băng thông: > 1024Mbps, với 2 cổng RJ45 1Gbps - Khả năng lưu trữ hỗ trợ dung lượng lên đến 160TB, có giao thức iSCSI mở rộng dung lượng lưu trữ qua mạng - Tìm kiếm và xem lại: Xem lại hình ảnh tức thì, Tìm kiếm và xem lại hình ảnh theo sự kiện, Tìm kiếm và xem lại theo nhãn đánh dấu (Tag), Tìm kiếm và xem lại thông minh theo khuôn mặt và chuyển động - Giao diện kết nối: 02 x HDMI, I/O Alarm: 16-in/ 08-out - Onvif: Profile T, Profile S, Profile G
	Bộ phát sóng wifi (Ăng-ten gain cao (≥ 5 dBi), Wi-Fi 5 (802.11ac) hoặc Wi-Fi 6 (802.11ax),≥ 20 dBm, PoE 802.3af/802.3at)
	BỘ CHUYỂN MẠCH POE 24, 48 CÔNG RJ45, 02 CÔNG SFP POE SWITCH 24,48 PORTS RJ45, 02 PORT SFP SLOT
	CÁP TÍN HIỆU CAT6 UTP CAT6 UTP CABLE
	MÀN HÌNH QUAN SÁT 42"
	MÁY TÍNH TRẠM LÀM VIỆC - CORE I5, HDD 500GB, RAM 4GB, LCD 17"
	TỔNG ĐÀI ĐIỆN THOẠI IP 10

HỆ THỐNG PHÁT THANH

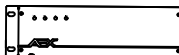KÝ HIỆU SYMBOL	MÔ TẢ DESCRIPTION
	MICRO THÔNG BÁO CHỌN VÙNG Loại để bàn, dễ dàng lắp đặt tại các khu vực thuận tiện thông báo 6 vùng loa có thể mở rộng 10 vùng loa thông báo
	BỘ ĐIỀU KHIỂN TRUNG TÂM TÍCH HỢP - Tích hợp 6 vùng loa - Tích hợp tính năng hẹn giờ - Tích hợp nguồn nhạc âm thanh: SD, FM, USB - Đầu vào giao diện bảo cháy 2 số Tiếp điểm khô: Thông báo cảnh báo , Tin nhắn sơ tán (định dạng MP3)
	BỘ KHUẾCH ĐẠI CÔNG SUẤT CÔNG NGHỆ LỚP D 600W - Output Voltage: 100V line / 8Ω - Frequency Response: 20 Hz to 20kHz - THD: <1% - Power Efficiency: >92% - Rack Mount 1U
	LOA GẮN TRẦN 6W
	LOA GẮN TƯỜNG 10W
	CÁP XOẮN CHỐNG NHIỄU 16 AWG

HỆ THỐNG ĐIỆN THOẠI & MẠNG, IPTV

KÍ HIỆU	DIỄN GIẢI
	THIẾT BỊ WIFI
	Ổ CĂM IP CHO MẠNG VÀ ĐIỆN THOẠI SỬ DỤNG CHUNG
	Ổ CĂM IP CHO MẠNG VÀ ĐIỆN THOẠI SỬ DỤNG CHUNG - ÂM SÀN
	SWITCH 16 PORT
	Ổ CĂM TIVI IPTV
	ĐIỆN THOẠI IPTV
	DÂY CÁP HDMI CHỖ, 2 SỢI (1 SỢI 5M, 1 SỢI 8M)
GHI CHÚ: - CẤU HÌNH TRUNG TÂM IP: DATA+ TEL+ IPTV SẼ DO CHỦ ĐẦU TƯ CUNG CẤP VÀ LẮP ĐẶT, TRỪ KHI CÓ CHỈ ĐẠO KHÁC.	

GHI CHÚ :

- CÁP HỆ THỐNG ĐIỆN NHẸ (THÔNG TIN) KHÔNG ĐƯỢC PHÉP LẮP ĐẶT CHUNG VỚI HỆ THỐNG KHÁC. KHAY CÁP PHẢI SƠN MÀU ĐỂ PHÂN BIỆT VÀ SỬ DỤNG TỐI ĐA 40% CỦA MẢNG.
- ỐNG ĐIỆN PHẢI ĐẠT CHẤT LƯỢNG TỐT, ĐỀU VÀ KHÔNG BỊ THÙNG, CÓ GỠ HAY SẠC CÀNH.
- NẾU ỐNG ĐIỆN LẮP NƠI NHÌN THẤY ĐƯỢC, ỐNG ĐIỆN PHẢI LẮP ĐẶT SONG SONG VÀ PHẢI THẬT VUÔNG GÓC KHI ĐỐI HƯỚNG.
- TUYẾN ỐNG ĐIỆN TRONG SÀN BÊ-TÔNG : KHÔNG ĐƯỢC CHẠY ỐNG ĐIỆN TRÊN LỚP MẶT BÊ-TÔNG. KHÔNG CHẠY TRONG NHỮNG VÙNG CĂNG CÁP KẾT CẤU, CẮT NGANG VUÔNG GÓC NHỮNG VÙNG CĂNG CÁP KẾT CẤU. CHẠY CÁC TUYẾN DÂY CÁP TRÁNH CHÉO NHAU VÀ GIẢM TỐI THIỂU SỐ LƯỢNG ỐNG ĐIỆN Ở BẤT KỶ VỊ TRÍ NÀO. TRÊN SÀN ỐNG ĐẶT SONG SONG CÁCH NHAU TỐI THIỂU LÀ 50mm Ở MỖI BÊN.
- NHÀ THẦU PHẢI KẾT HỢP VỚI CÁC CHUYÊN GIA ĐỂ XÁC NHẬN, CUNG CẤP TẤT CẢ CÁC THIẾT BỊ VÀ CÁP ĐIỆN CHO PHÙ HỢP VỚI HỆ THỐNG ĐIỆN PHỤ TRỢ. CÁP ĐIỆN PHẢI ĐƯỢC ĐỊNH KÍCH CỠ DỰA THEO CHIỀU DÀI MẠCH, TẢI, TRỞ KHÁNG VÀ ĐỘ SỤT ÁP.
- NHÀ THẦU PHẢI TÍNH ĐỘ DÀI CỦA MẠCH CỦA HỆ THỐNG THÔNG TIN SAO CHO PHÙ HỢP VỚI CHIỀU DÀI CHO PHÉP CỦA NHÀ SẢN XUẤT THIẾT BỊ, KẾ CẠ DỰ PHÒNG CHO TƯƠNG LAI.
- TRƯỚC KHI LẮP ĐẶT CÁC THIẾT BỊ HỆ THỐNG THÔNG TIN, NHÀ THẦU THÔNG TIN PHẢI PHỐI HỢP VỚI BẢN VẼ NỘI THẤT.
- HỆ THỐNG BẢO CHÁY PHẢI ĐƯỢC CÁP NGUỒN 220VAC RIÊNG VÀ DỰ PHÒNG TRONG 12 GIỜ HOẠT ĐỘNG BÌNH THƯỜNG, 2 GIỜ KHI CÓ SỰ CỐ.
- HỆ THỐNG BẢO CHÁY PHẢI ĐƯỢC KẾT NỐI VỚI HỆ THỐNG ÂM THANH, KHI CÓ SỰ CỐ CHÁY XẢY RA THÌ HỆ THỐNG BẢO CHÁY SẼ GÕI TÍN HIỆU ĐẾN VÀ HỆ THỐNG ÂM THANH SẼ CÓ NHIỆM VỤ THÔNG THÔNG BÁO VÀ HƯỚNG DẪN THOÁT HIỂM.
- ĐẦU BẢO CHÁY PHẢI CÁCH MÉP MIỆNG GIÓ CỦA HỆ THỐNG ĐIỀU HÒA HOẶC HỆ THỐNG THÔNG GIÓ TỐI THIỂU 0,5 MÉT.

GHI CHÚ - (Notes)

- ĐỀ NGHỊ KIỂM TRA KÍCH THƯỚC THỰC TẾ TẠI CÔNG TRÌNH TRƯỚC KHI THI CÔNG
- NÊN ĐỌC BẢN VẼ KẾT CẤU KÈM THEO BẢN VẼ KHAI TRIỂN CHI TIẾT KIẾN TRÚC
- KHI THAY ĐỔI CHI TIẾT THIẾT KẾ CẦN THAM KHẢO Ý KIẾN CỦA KIẾN TRÚC SƯ HOẶC KỸ SƯ THIẾT KẾ

BẢN VẼ PHÁT HÀNH

- ☐ THIẾT KẾ CONCEPT
- ☐ THIẾT KẾ CƠ SỞ
- ☒ THIẾT KẾ KỸ THUẬT THI CÔNG

TÊN CÔNG TRÌNH
(project name)

SHOWROOM VOLKSWAGEN
CẦN THƠ

ĐỊA ĐIỂM XÂY DỰNG
(Site)

KDC LÔ SỐ 11A, KĐT NAM CẦN THƠ
PHƯỜNG HƯNG PHÚ, TP. CẦN THƠ

CHỦ ĐẦU TƯ
(Project Owner)

CÔNG TY CP VW CẦN THƠ

TỔNG GIÁM ĐỐC

ĐƠN VỊ THIẾT KẾ

BAOLONG LAND COPORATION
Lô DVTM-08 & DVTM-11, Đường số 7
KCX Tân Thuận, P. Tân Thuận Đông, Q7, Tp.HCM

BAOLONGLAND

TỔNG GIÁM ĐỐC

PHAN HẢI NAM

ĐƠN VỊ THIẾT KẾ CƠ ĐIỆN

VIET TIEN CONSTRUCTION AND
DESIGN CONSULTING CO., LTD

127/23 Lê Thúc Hoạch, P. Phú Thọ Hòa, Tp.HCM

GIÁM ĐỐC

KS. NGUYỄN THỊ GUI

TÊN BẢN VẼ/Drawing Title


GHI CHÚ CHUNG VÀ MÔ TẢ KÝ HIỆU

TỶ LỆ - Scale
1/150

NGÀY- Date
30/01/2026

BẢN VẼ SỐ
Drawing No.

LV-02
05

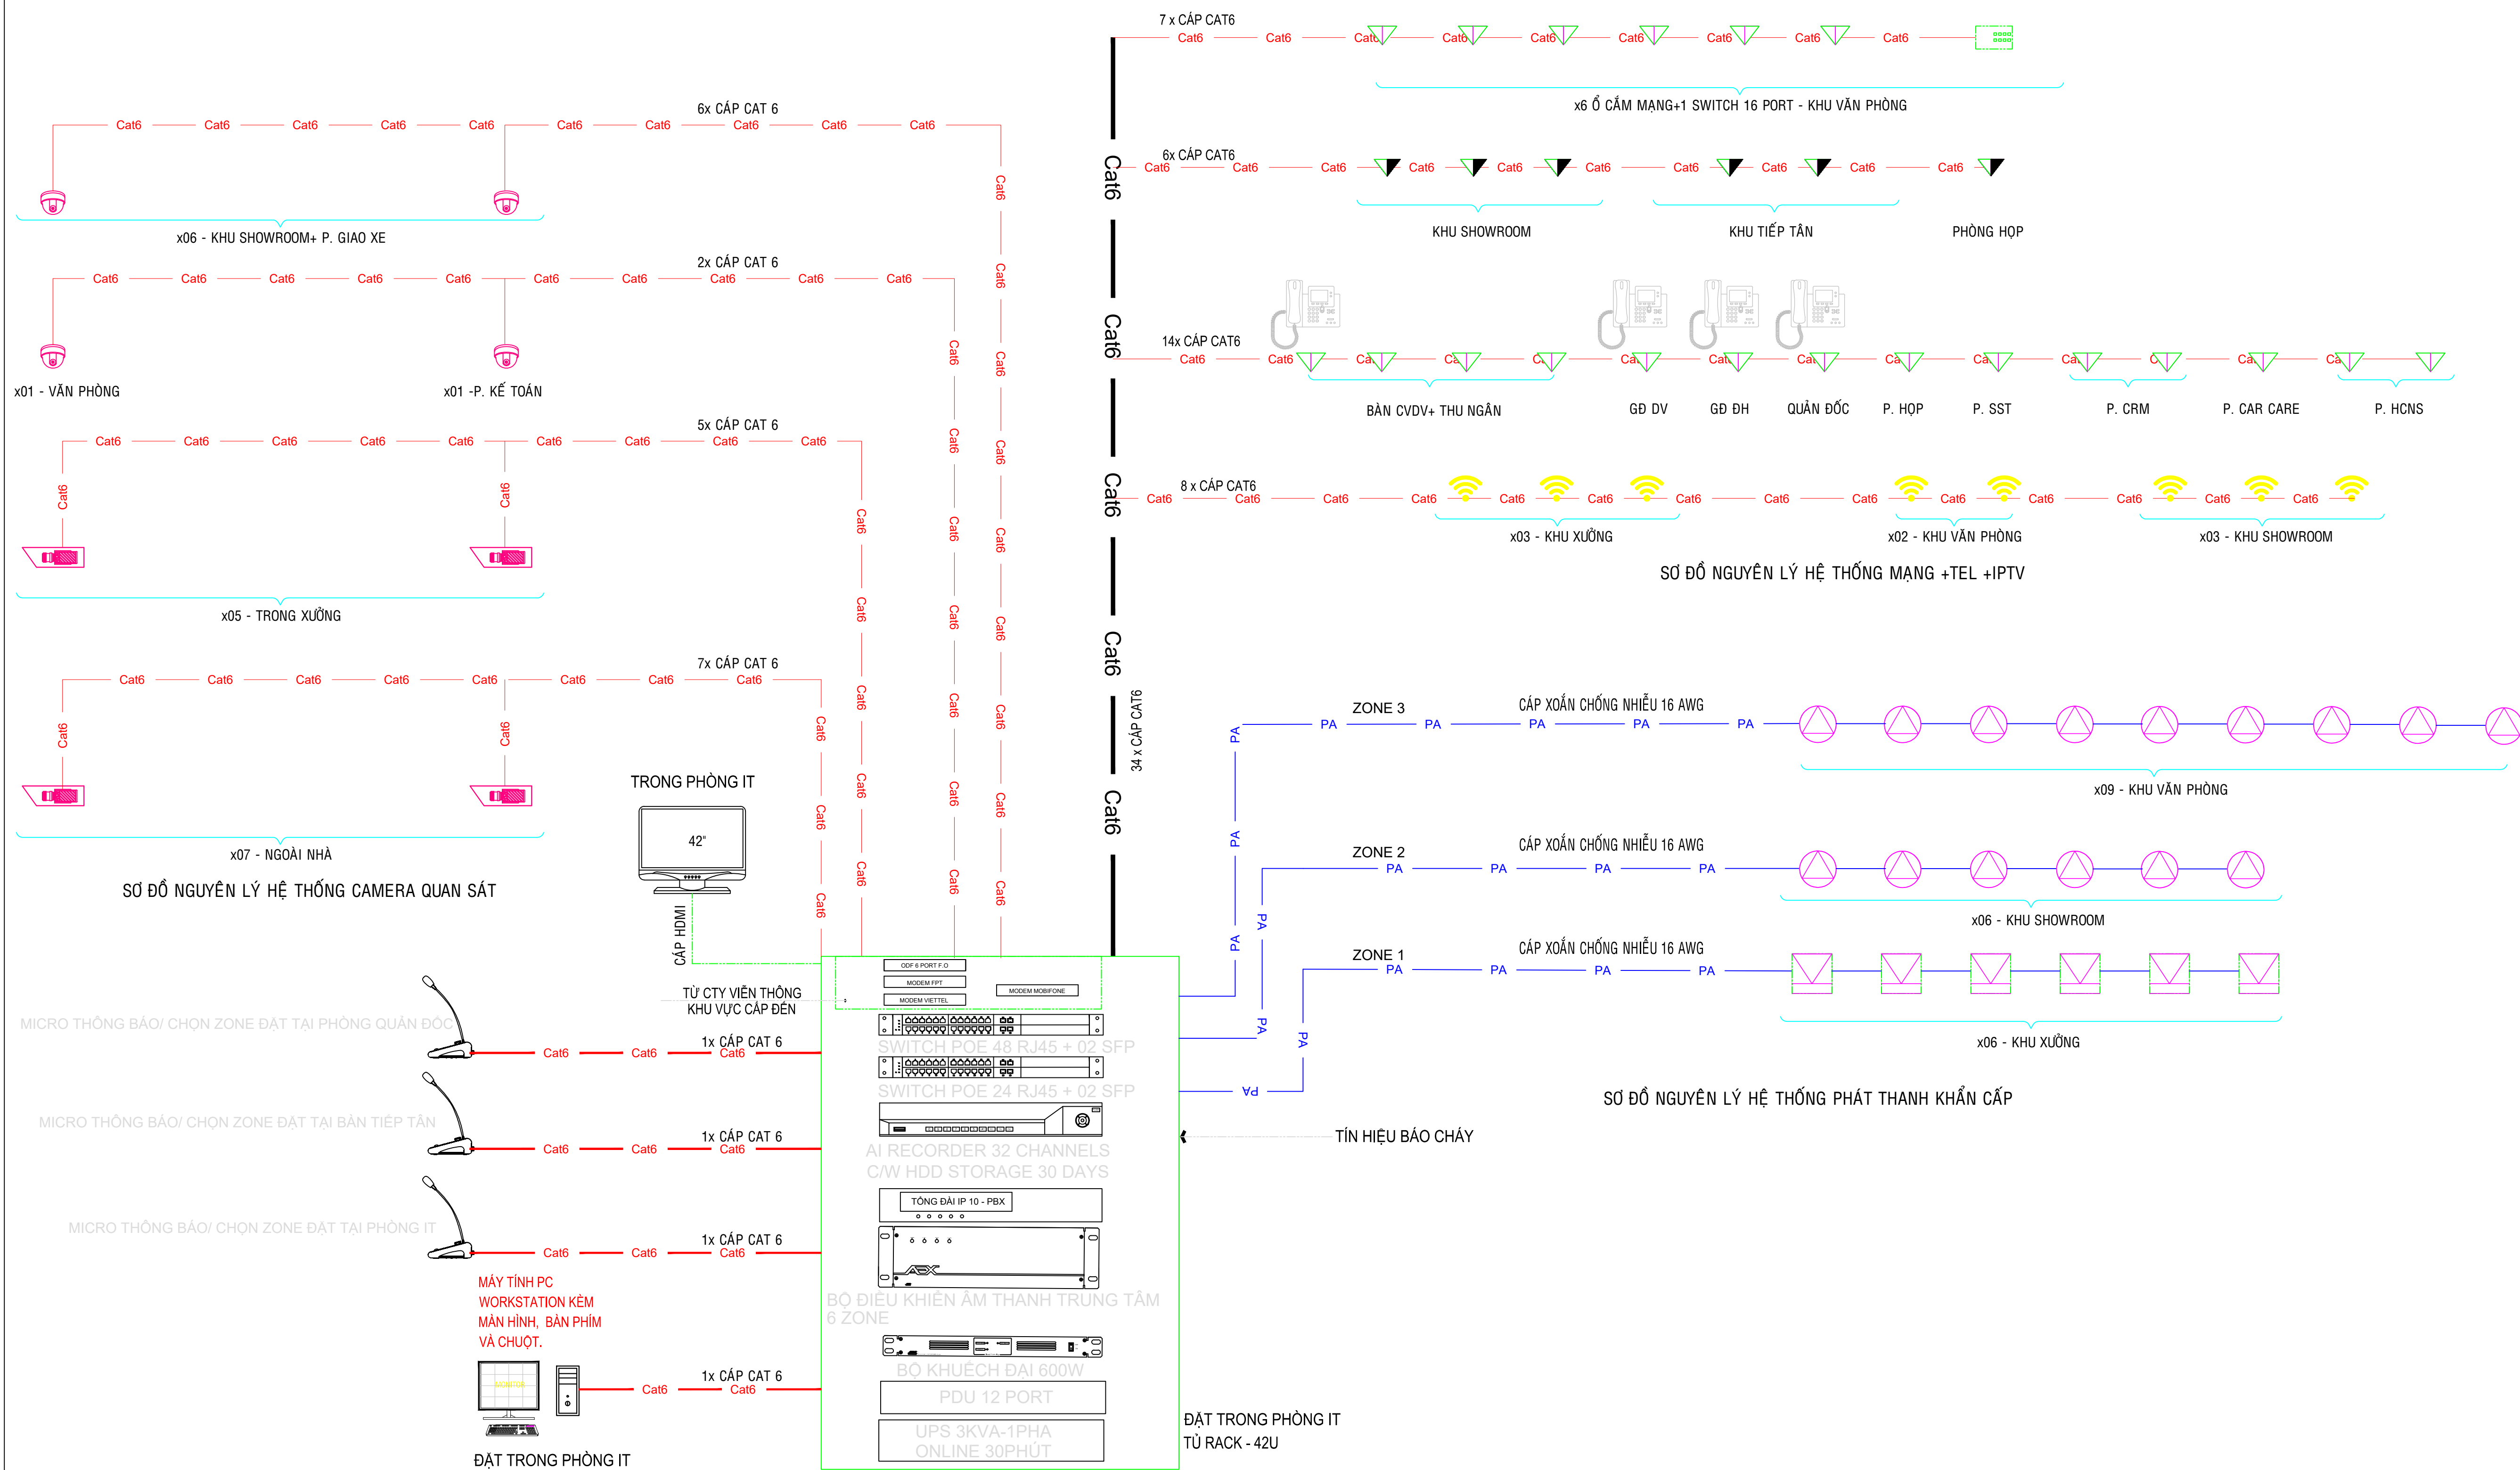

GHI CHÚ - (Notes)

- 1/ ĐỀ NGHỊ KIỂM TRA KÍCH THƯỚC THỰC TẾ TẠI CÔNG TRÌNH TRƯỚC KHI THI CÔNG
- 2/ NÊN ĐỌC BẢN VẼ KẾT CẤU KHI MÀ THEO BẢN VẼ KHAI TRIỂN CHI TIẾT KIẾN TRÚC
- 3/ KHI THAY ĐỔI KHI THIẾT KẾ CẦN THAM KHẢO Ý KIẾN CỦA KIẾN TRÚC SƯ HOẶC KỸ SƯ THIẾT KẾ

BẢN VẼ PHÁT HÀNH

- ☐ THIẾT KẾ CONCEPT
- ☐ THIẾT KẾ CƠ SỞ
- ☒ THIẾT KẾ KỸ THUẬT THI CÔNG

TÊN CÔNG TRÌNH
(project name)

SHOWROOM VOLKSWAGEN CẦN THƠ

ĐỊA ĐIỂM XÂY DỰNG
(Site)

KDC LÔ SỐ 11A, KĐT NAM CẦN THƠ
PHƯỜNG HƯNG PHÚ, TP. CẦN THƠ

CHỦ ĐẦU TƯ
Project Owner)

CÔNG TY CP VW CẦN THƠ

TỔNG GIÁM ĐỐC

ĐƠN VỊ THIẾT KẾ

BAOLONG LAND COPORATION
Lô DVTM-08 & DVTM-11, Đường số 7
CX Tân Thuận, P. Tân Thuận Đông, Q7, Tp.HCM

BAOLONGLAND

TỔNG GIÁM ĐỐC

PHAN HẢI NAM

ĐƠN VỊ THIẾT KẾ CƠ ĐIỆN

VIET TIEN CONSTRUCTION AND
DESIGN CONSULTING CO., LTD
127/23 Lê Thúc Hoạch, P. Phú Thọ Hòa, Tp.HCM

GIÁM ĐỐC

KS. NGUYỄN THỊ QUI

TÊN BẢN VẼ/Drawing Title


**SƠ ĐỒ NGUYÊN LÝ DATA + TEL +IPTV+
PA+ CAMERA QUAN SÁT**

TỶ LỆ - Scale
1/150


NGÀY- Date
30/01/2026

BẢN VẼ SỐ
Drawing No.


V.03
05

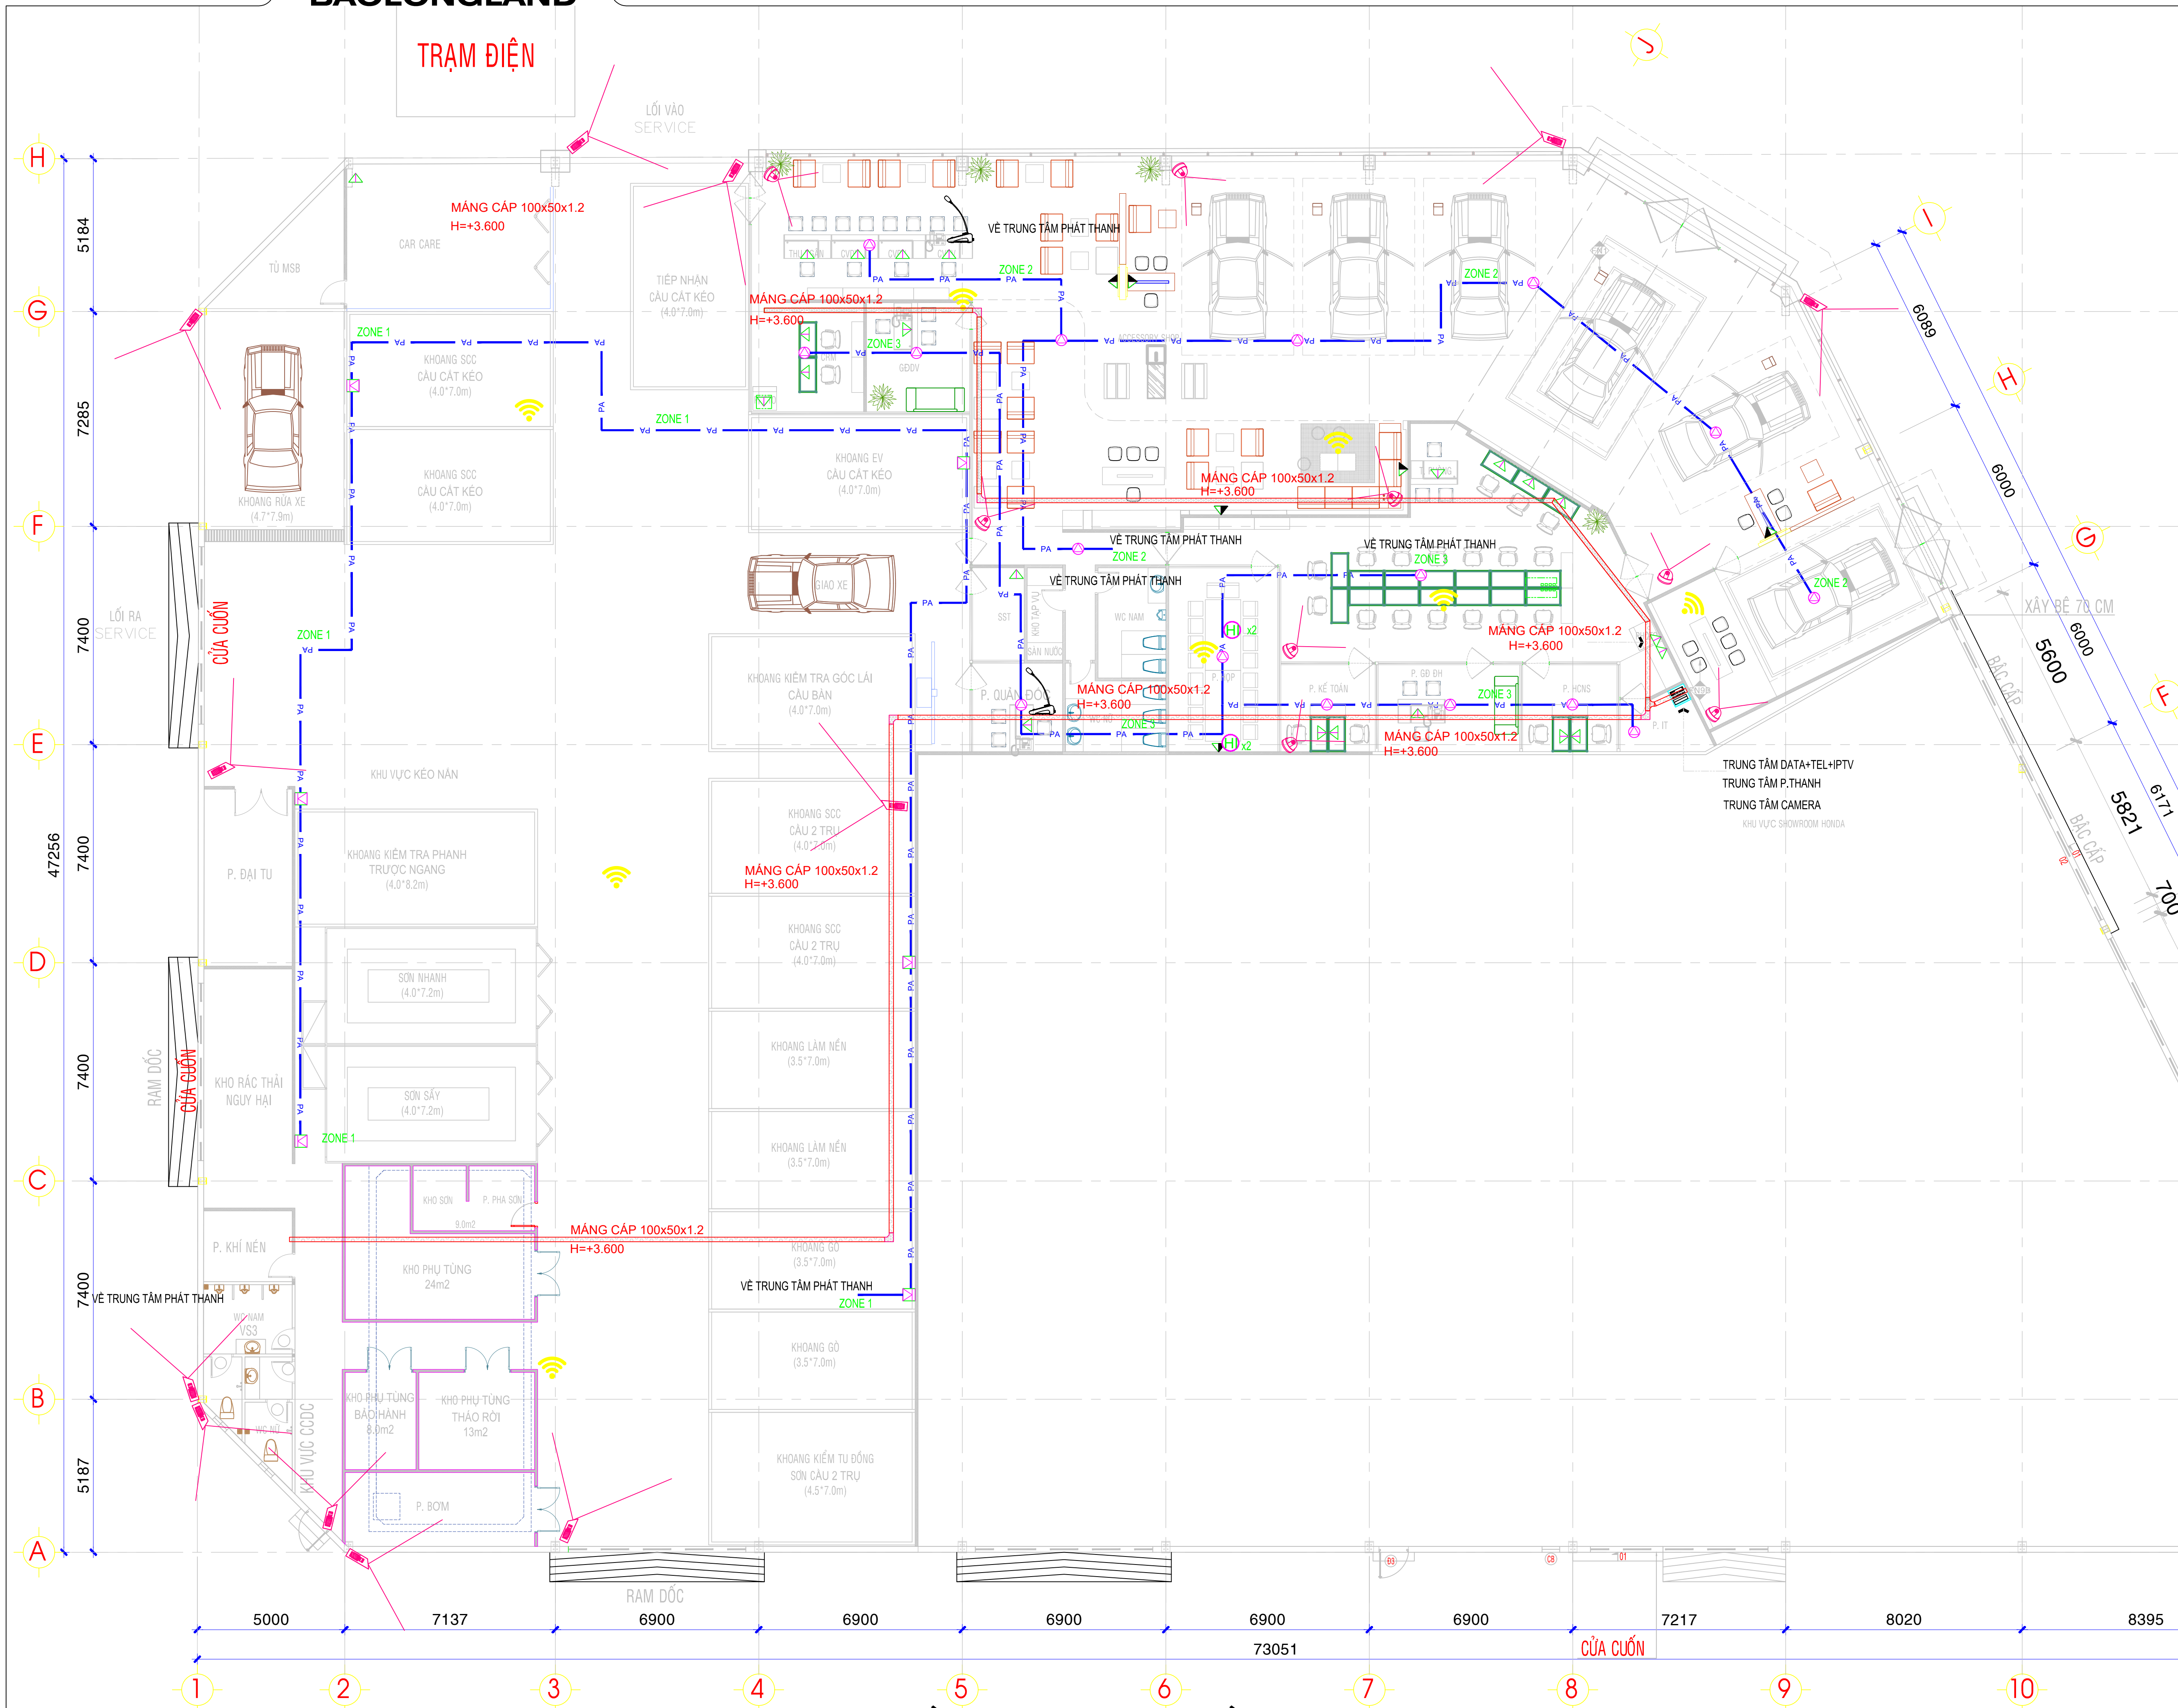


MẶT BẰNG ĐIỆN NHE TẦNG TRỆT - TL:1/150

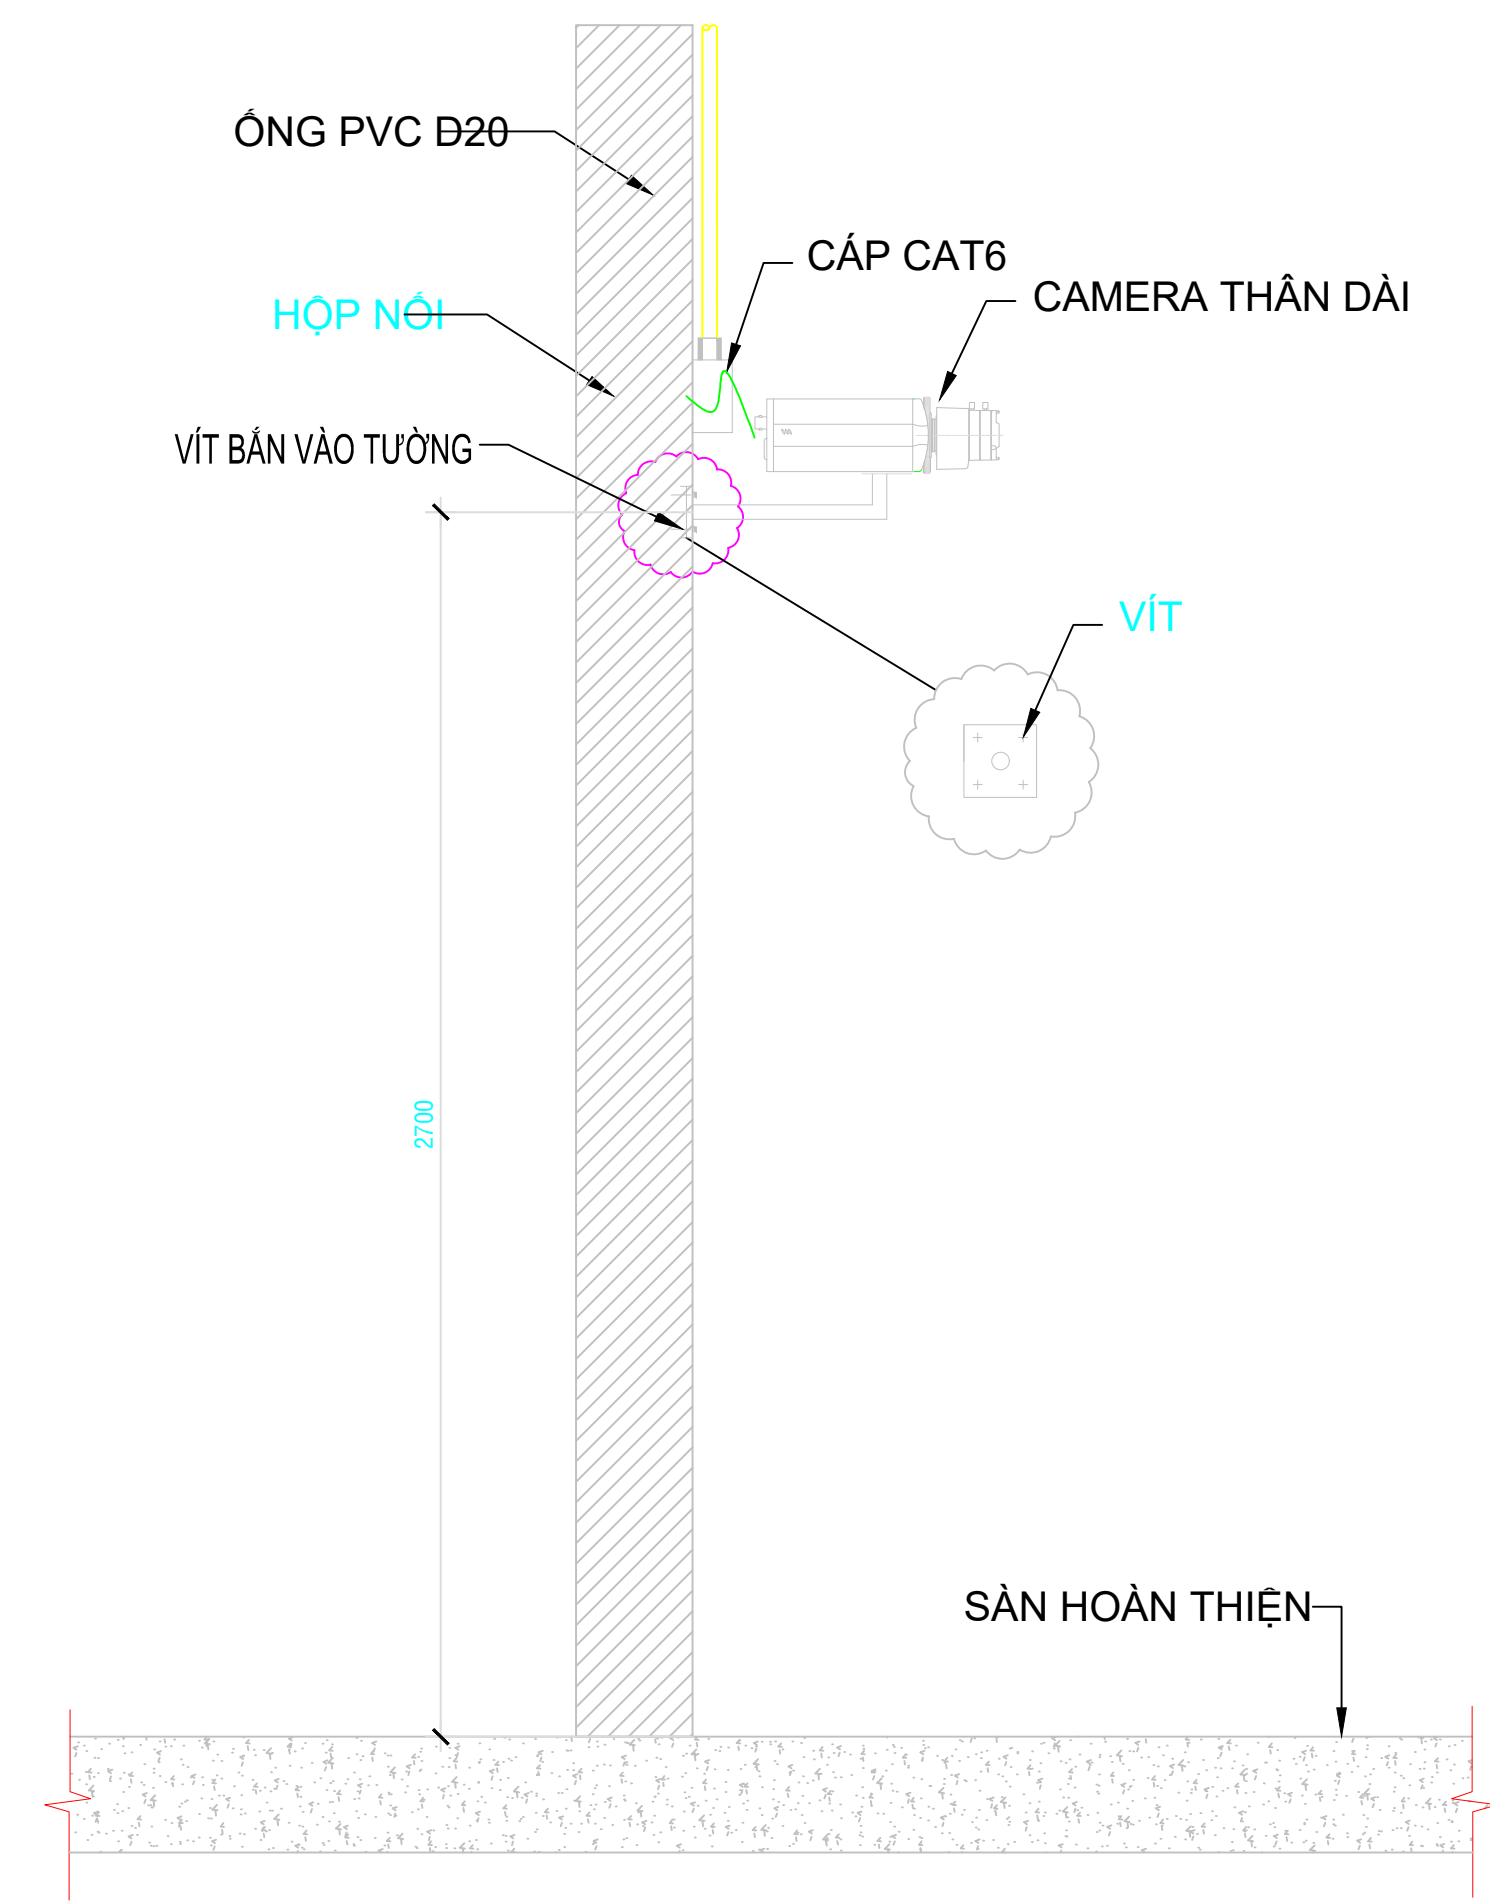

CHI TIẾT LẮP ĐẶT CAMERA THÂN DÀI GẮN TƯỜNG

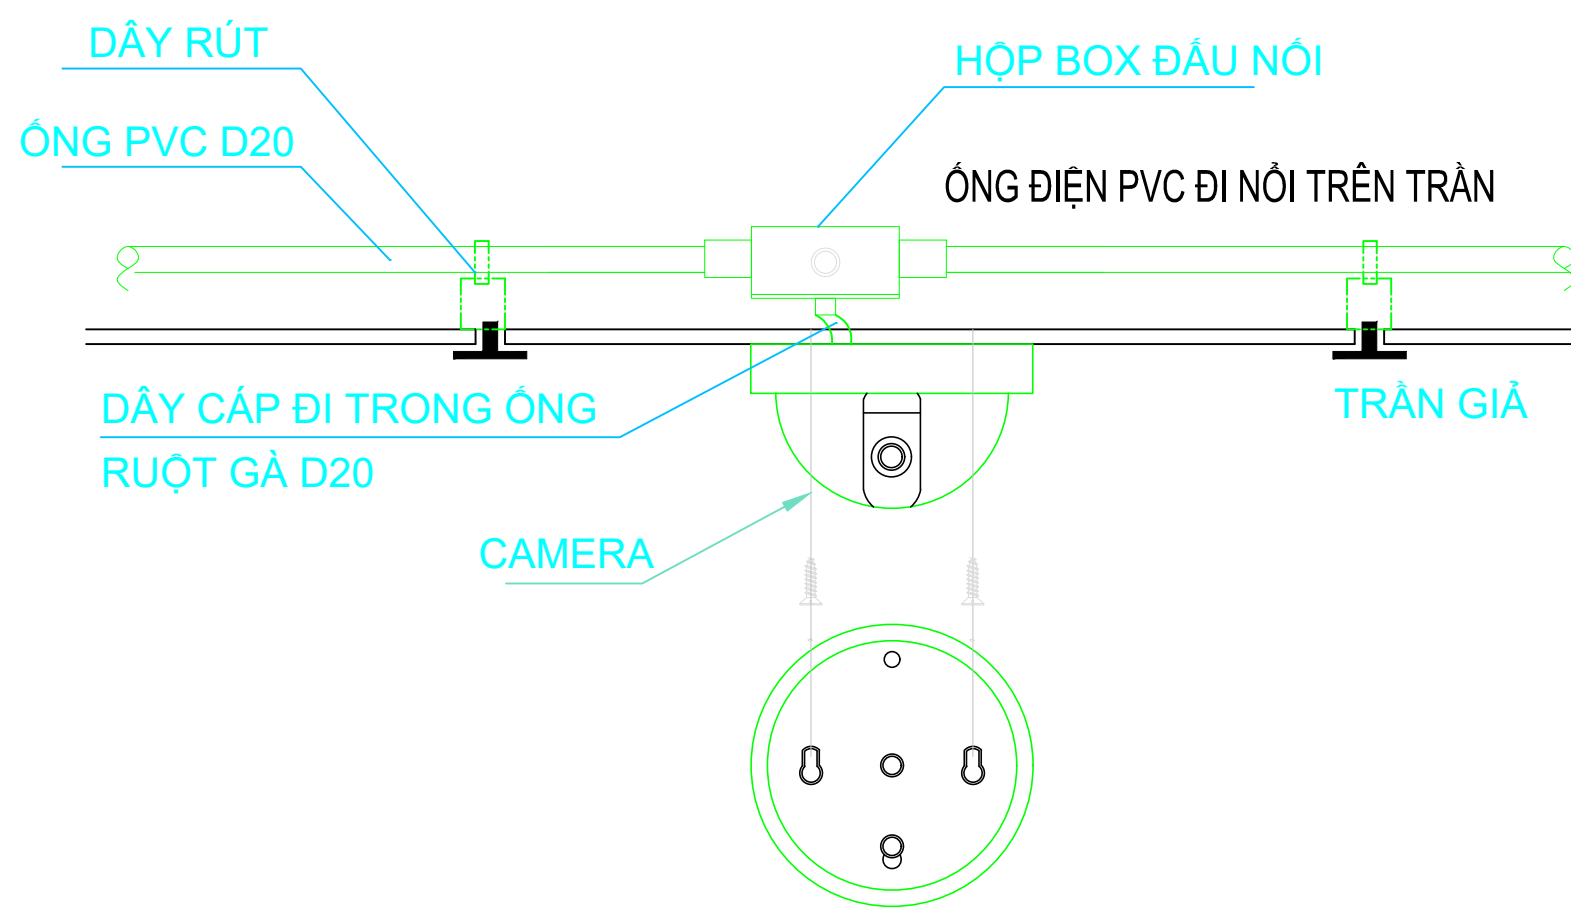

CHI TIẾT LẮP ĐẶT CAMERA DOME

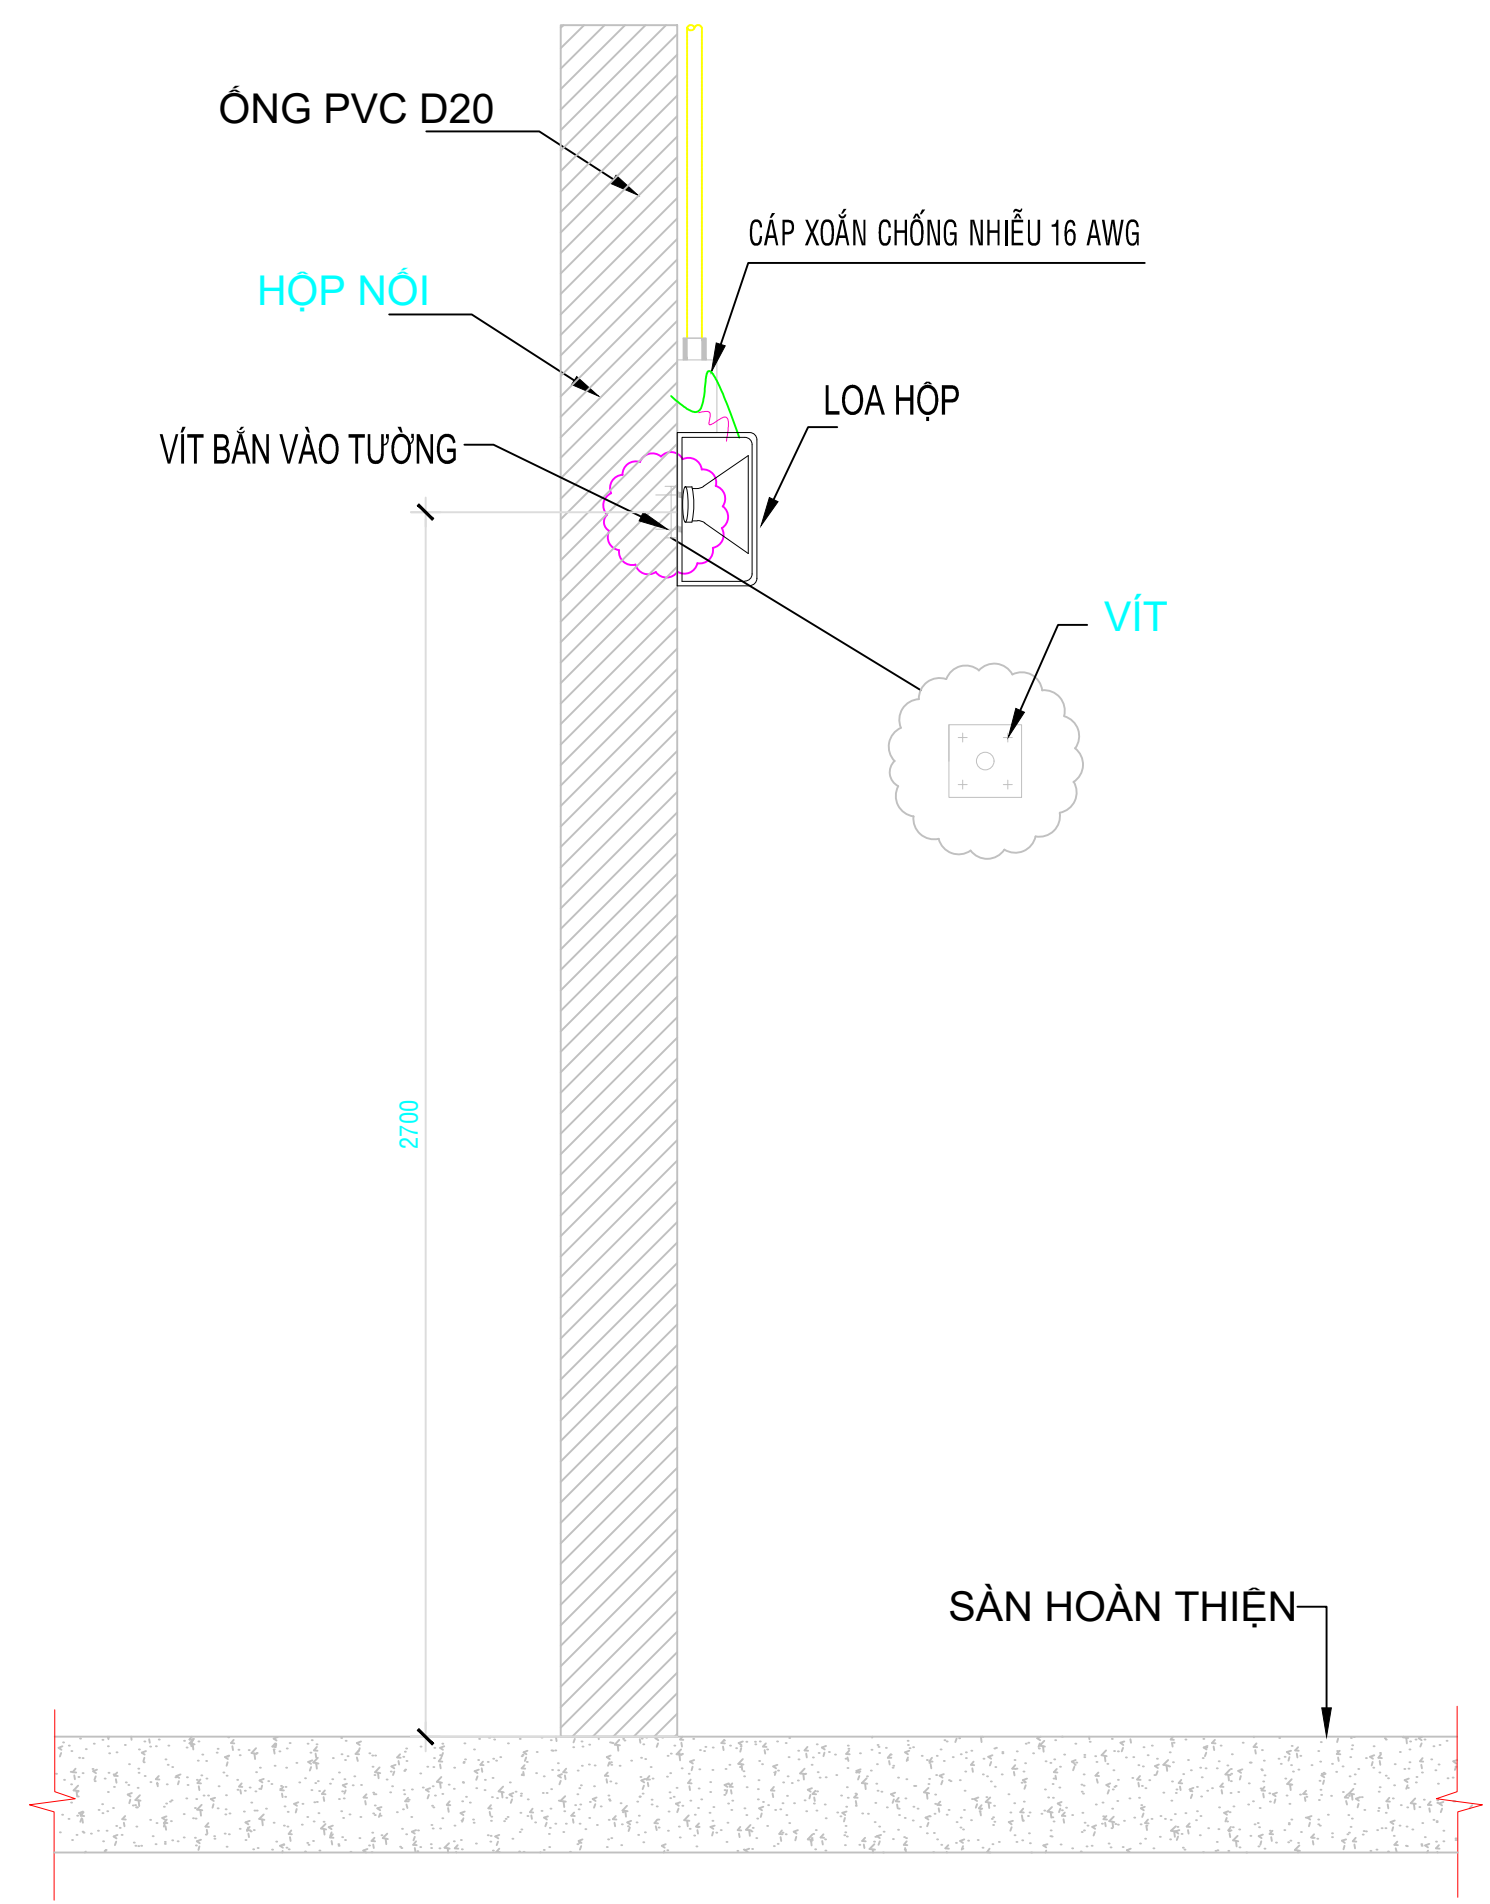

CHI TIẾT LẮP ĐẶT CAMERA THÂN DÀI GẮN TƯỜNG

GHI CHÚ - (Notes)

- 1/ ĐỀ NGHỊ KIỂM TRA KÍCH THƯỚC THỰC TẾ TẠI CÔNG TRÌNH TRƯỚC KHI THI CÔNG
- 2/ NÊN ĐỌC BẢN VẼ KẾT CẤU KÈM THEO BẢN VẼ KHAI TRIỂN CHI TIẾT KIẾN TRÚC
- 3/ KHI THAY ĐỔI CHI TIẾT THIẾT KẾ CẦN THAM KHẢO Ý KIẾN CỦA KIẾN TRÚC SƯ HOẶC KỸ SƯ THIẾT KẾ

BẢN VẼ PHÁT HÀNH

- ☐ THIẾT KẾ CONCEPT
- ☐ THIẾT KẾ CƠ SỞ
- ☒ THIẾT KẾ KỸ THUẬT THI CÔNG

TÊN CÔNG TRÌNH
(project name)SHOWROOM VOLKSWAGEN
CẦN THƠĐỊA ĐIỂM XÂY DỰNG
(Site)KDC LÔ SỐ 11A, KẾT NAM CẦN THƠ
PHƯỜNG HƯNG PHÚ, TP. CẦN THƠCHỦ ĐẦU TƯ
(Project Owner)

CÔNG TY CP VW CẦN THƠ

TỔNG GIÁM ĐỐC

ĐƠN VỊ THIẾT KẾ

BAOLONG LAND COPORATION
Lô DVTM-08 & DVTM-11, Đường số 7
KCN Tân Thuận, P. Tân Thuận Đông, Q7, Tp.HCM

BAOLONGLAND

TỔNG GIÁM ĐỐC

PHAN HẢI NAM

ĐƠN VỊ THIẾT KẾ CƠ ĐIỆN

VIET TIEN CONSTRUCTION AND
DESIGN CONSULTING CO., LTD
127/23 Lê Thúc Hoạch, P. Phú Thọ Hòa, Tp.HCM

GIÁM ĐỐC

KS. NGUYỄN THỊ QUI

TÊN BẢN VẼ/Drawing Title

CHI TIẾT LẮP ĐẶT ĐIỆN HÌNH 01

TỶ LỆ - Scale
1/100NGÀY- Date
30/01/2026BẢN VẼ SỐ
Drawing No.

LV.07

05